


PROPOSED RESIDENCE FOR Mr. MIJULAL . P

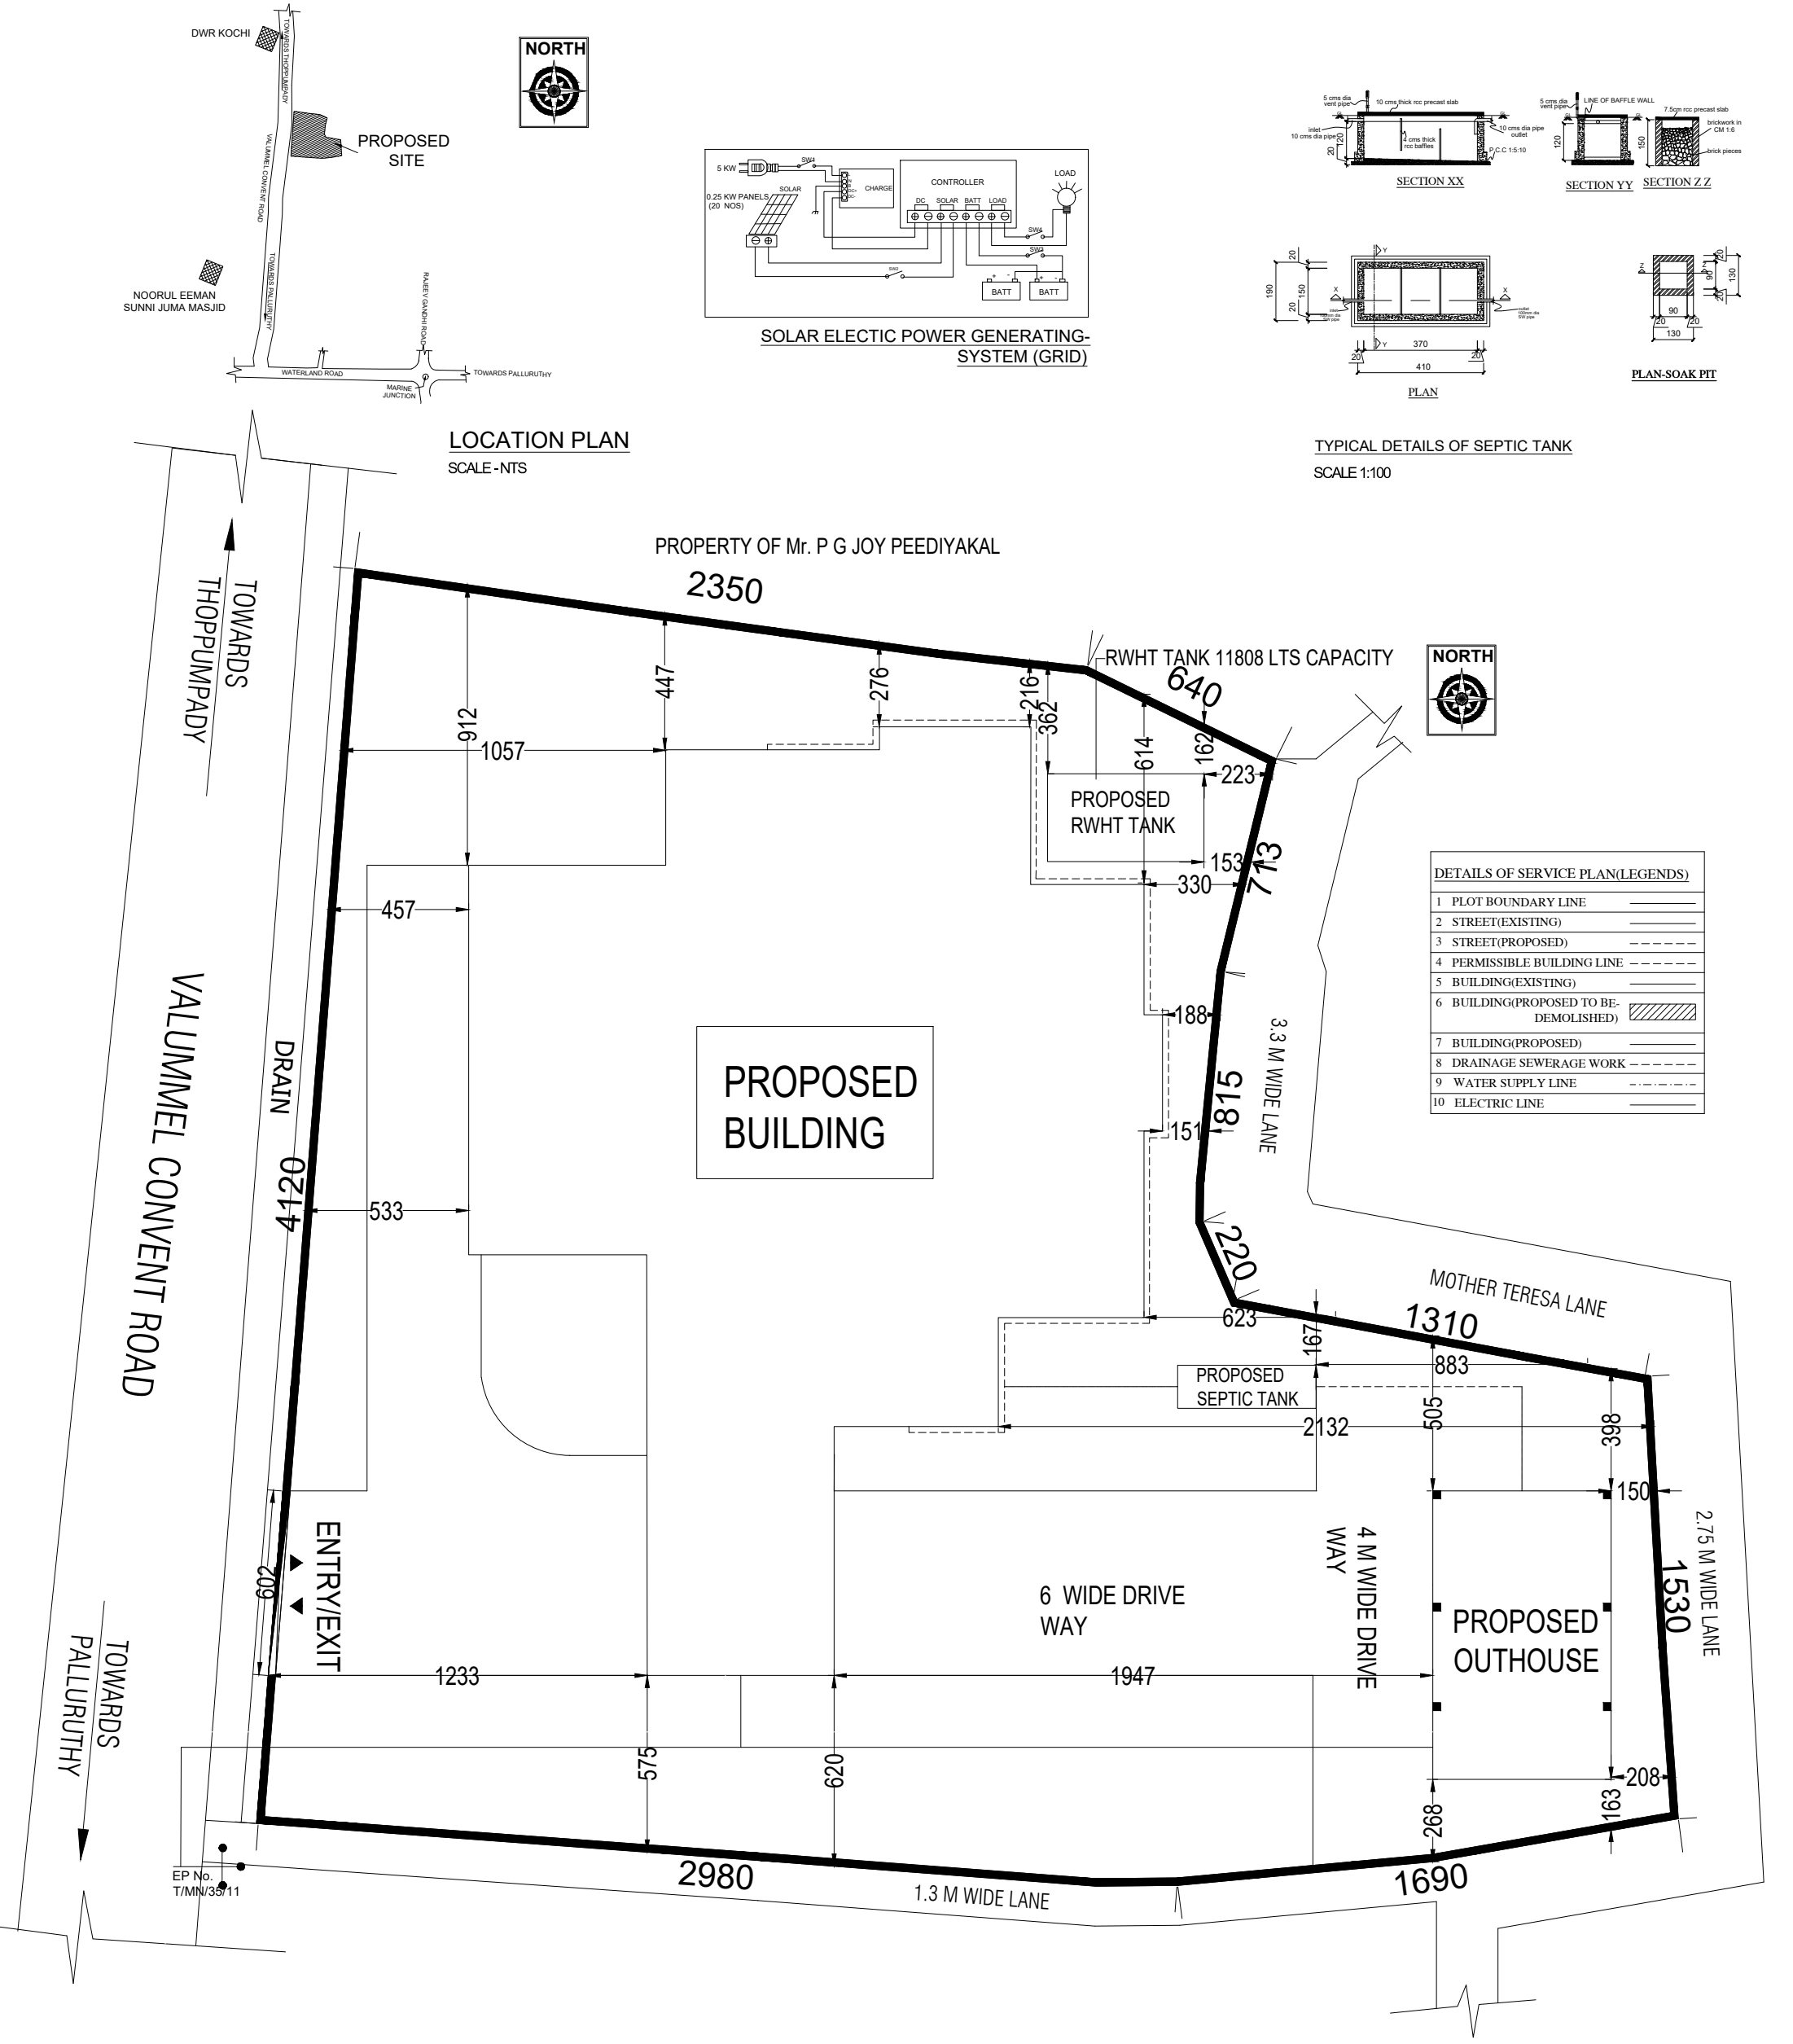

CERTIFICATE :

1. CERTIFIED THAT THE SITE PLAN IS PREPARED AFTER VERIFICATION OF OWNERSHIP DOCUMENT & SITE AND THE MEASUREMENTS SHOWN ARE FOUND TO BE CORRECT.

2. CERTIFIED THAT THE BUILDING PLAN IS PREPARED IN ACCORDANCE WITH THE KMBR 2019, KERALA MUNICIPALITY ACT 1994 & THE PROVISIONS CONTAINED IN THE SANCTIONED TOWN PLANNING SCHEME.

3. CERTIFIED THAT THERE IS NO WELL WITHIN 7.50m RADIUS FROM PROPOSED SEPTIC TANK.

SPECIFICATIONS	SCHEDULE OF OPENING	LAND DETAILS	AREA STATEMENT	OWNER ADDRESS&SIGNATURE	SIGNATURE OF THE ARCHITECT	PROJECT :	DRG :
1. Foundation bed :- PCC 15CM thick 2. Foundation :- Pile foundation 3. Superstructure :- RCC columns and beams with first class brick masonry and throughout lintel above 4. Flooring :- Tile&Granite finish 5. Joinary works :- Glazed Aluminium&Wood 6. Plastering :- 12mm thick CM 1:4 7. Roofing :- RCC Slab 15cm Thick 8. Stair case :- 12cm thick RCC slab and MS with Rise :-15.75cm Tread :-30cm Stair width:-150cm 9. Hand rail :- SS,MS&Wood hand rail 90cm height 10. Parapet wall :- 15cm thick masonry 120cm height 11. Ventilation :- Mechanical(forced) / Natural 12. Water Supply :- Bore well & Public water supply 13. Drainage :- To Public drain& Diverted to soak pit 14. Access :- Road 15. Sewage :- Disposed to STP& Septic tank	DD DOUBLE LEAF DOOR 120 X 240 D1 DOOR 100 X 240 D2 DOOR 90 X 240 D3 DOOR 80 X 240 FG FIXED GLASS WINDOW L X 240 FW2 WINDOW 120 X 240 FW3 WINDOW 180 X 240 FW4 WINDOW 240 X 240 FW5 WINDOW 300 X 240 KW3 KITCHEN WINDOW 180 X 120 KW4 KITCHEN WINDOW 240 X 120 V VENTILATOR 60 X 60 GR GRILL OPENING L X 120 NOTE: LINTEL HEIGHT = 245 CM	DISTRICT : ERNAKULAM TALUK : KOCHI VILLAGE : RAMESHWARAM SURVEY NO : 772/3 part , 1662 part EXTENT : 1427 SQM (14.27 ARES)	FLOOR A MAIN RESIDENCE 1 GROUND FLOOR 417.94 2 FIRST FLOOR 176.74 TOTAL 594.68 B OUT HOUSE 1 GROUND FLOOR 54.41 2 FIRST FLOOR 46.37 3 STAIR HEAD ROOM 16.46 TOTAL 117.24 GRAND TOTAL (A+B) 711.92 DETAILS FOR KMBR FSI = GRAND TOTAL AREA = 711.92 = 0.49 PLOT AREA 1427 COVERAGE AREA = 417.94 + 54.41 = 472.35 Sqm or 472.35 / 1427 = 33.10 % RWHT CAPACITY - 25Lts PER COVERAGE AREA - 25 x 472.35 = 11808 Lts	Mr. MIJULAL . P S/o LALAN PRADEEPS HOUSE THOPUMPADY PALLURUTHY, VADAKKU MURI 682005	ARCHITECTS  33/1622 A , Navam , Haritha By Lane Vennala p.o.Kochi 682028 T:0484 2808673,2808517 F:0484 2809246 ahanas@ahanas.com	PROPOSED RESIDENTIAL BUILDING AT THOPUMPADY	DRG : SANCTION DRAWING Drawing Title : SITE AND SERVICE PLAN LOCATION PLAN, SEPTIC TANK DETAILS. ALL DIMENSIONS IN CMS Date : 08/03/2021 Scale: : 1:100,1:200 Dwg.No : SD/RD - 09 SHEET NO: 3/3 Drawn : Aneena Checked : AP