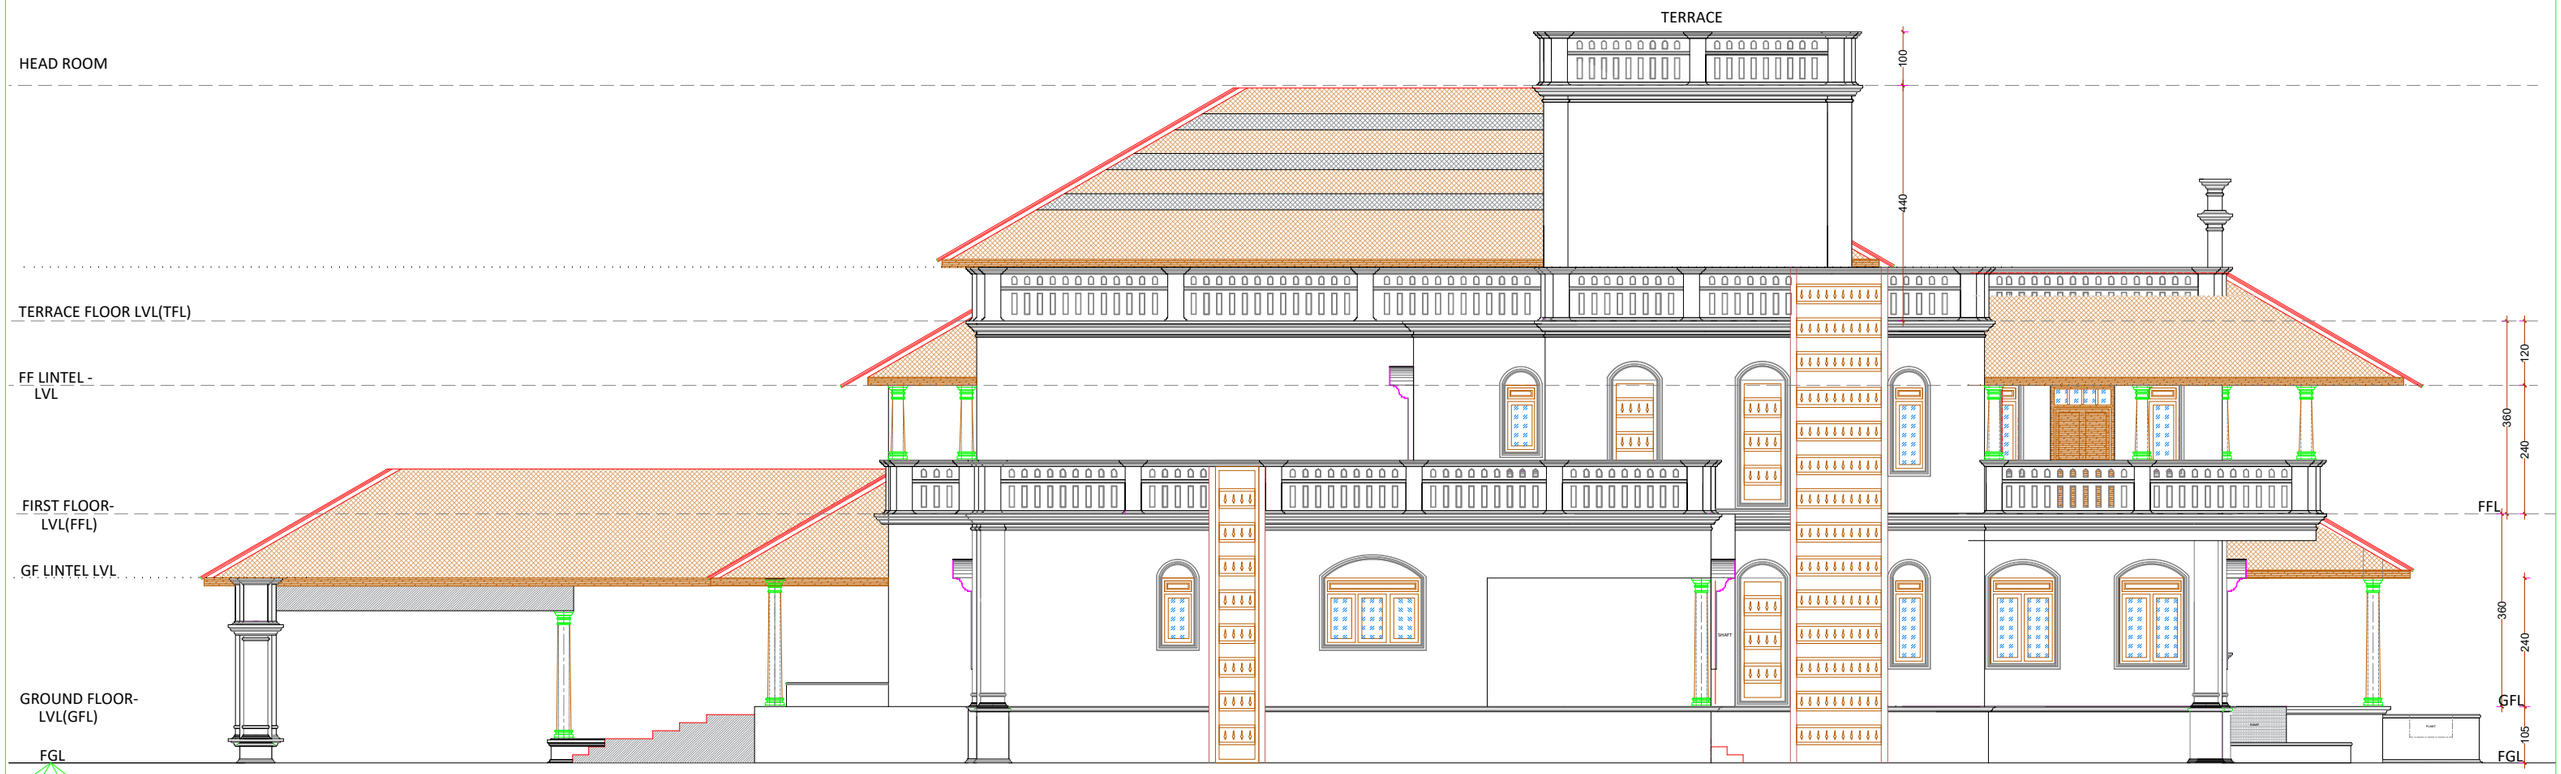

RIGHT SIDE ELEVATION

DATE: 29.03.2023		PROJECT: RESIDENTIAL PROJECT AT TIRUNELVELI	REVISION:		NOTES:
SCALE : NA			1	13-05-24- WALL EXTENSION OF TOILET FOR PROVIDING TV	○ ALL DIMENSIONS ARE IN CMS, UNLESS OTHERWISE SPECIFIED
DRAWN: PINKY		CLIENT: SHABREESH		CHANGES IN SHAFT LOCATION/ SIZE AS PER HVAC CONSULTANT REQUIREMENT	○ DIMENSIONS SHALL NOT BE MEASURED DIRECTLY FROM THIS DRAWINGS. FOLLOW ONLY WRITTEN DIMENSIONS
CHECKED: JAMESLEE		DRAWING TITLE: RIGHT SIDE ELEVATION			○ IN THE EVENT OF ANY DISCREPANCY OR DIFFERENCE BETWEEN ANY DRAWINGS OR SITE CONDITIONS OR OTHERWISE IMMEDIATE REFERENCE IS TO BE MADE TO THE DESIGNER FOR CLARIFICATION PRIOR TO EXECUTION OF WORK AT SITE
PROJECT NO:563	DRAWING NO: ADFS/AR/ 563/FH-09				○ ALL THE CIVIL WORKS SHOULD BE IN LINE LEVEL AND PLUMB.
					○ PLASTERING TO BE CUT AT SKIRTING LEVEL.

ATHANAS