

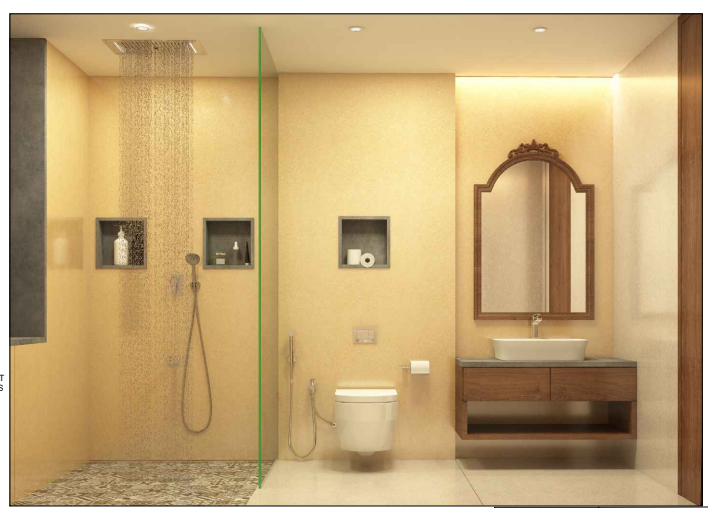
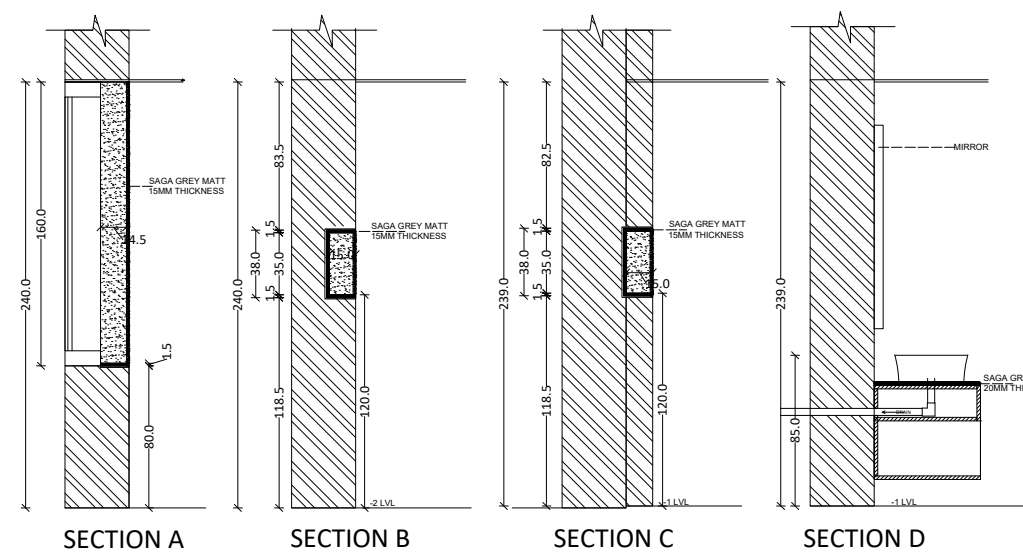
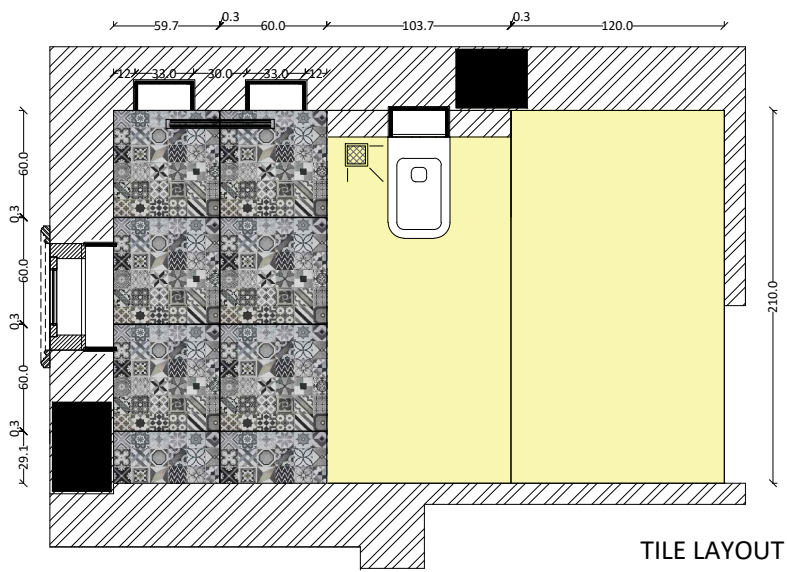
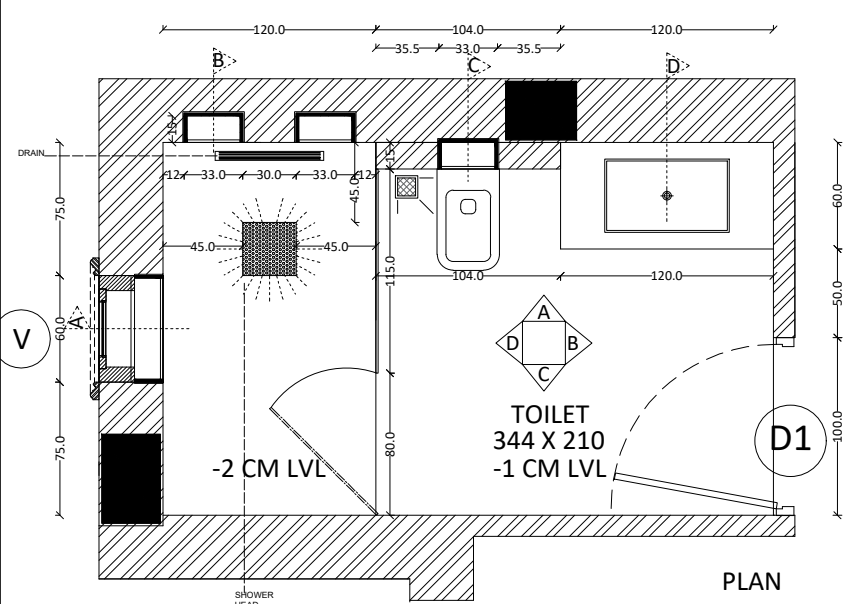


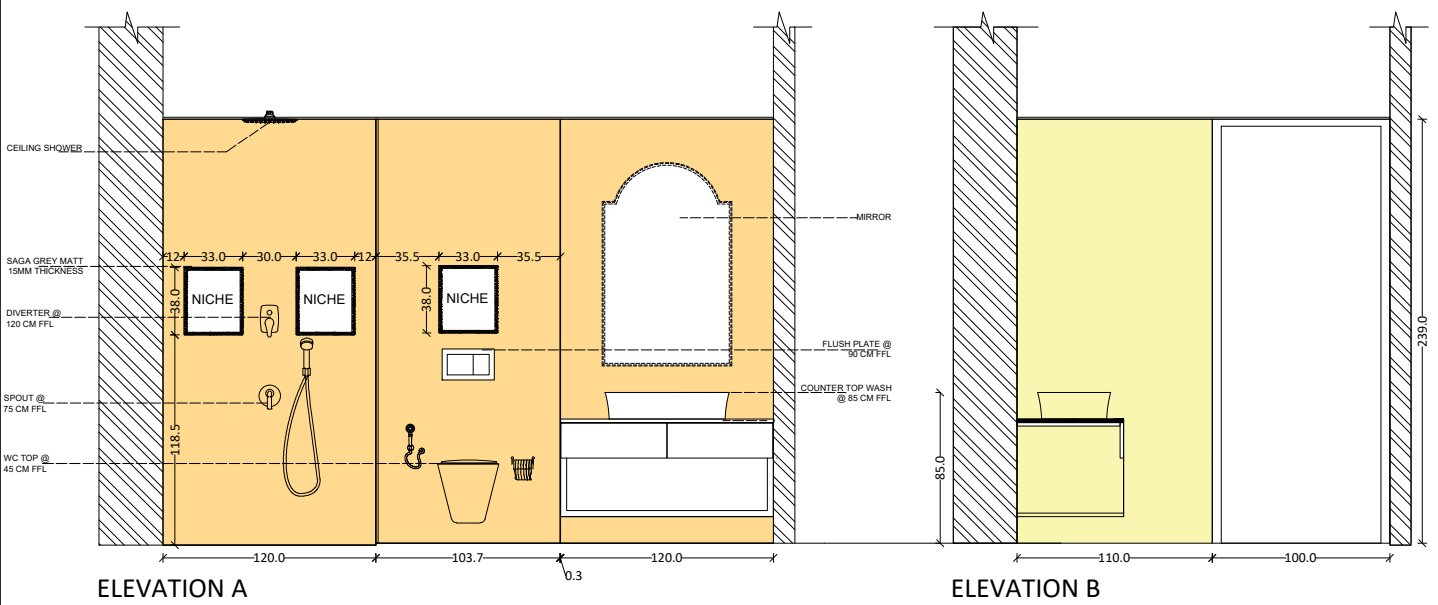

	DRY AREA WALL (WC & WASH) ALL WALLS OF WET AREA - SIMPOLO SPECTRA MUSTARD 240 x 120 CM WITH 2MM SPACER
	NICHE & TOP OF LEDGE WALL - SERA GREY POLISH 300x80 CM 15MM & 20MM THICKNESS
	WET AREA FLOOR - FND ACHIRA - 16270 60 x60 CM
	DRY AREA FLOOR AND BALANCE WALLS - SIMPOLO SPECTRA CHEESE 240 x 120 CM WITH 3MM SPACER

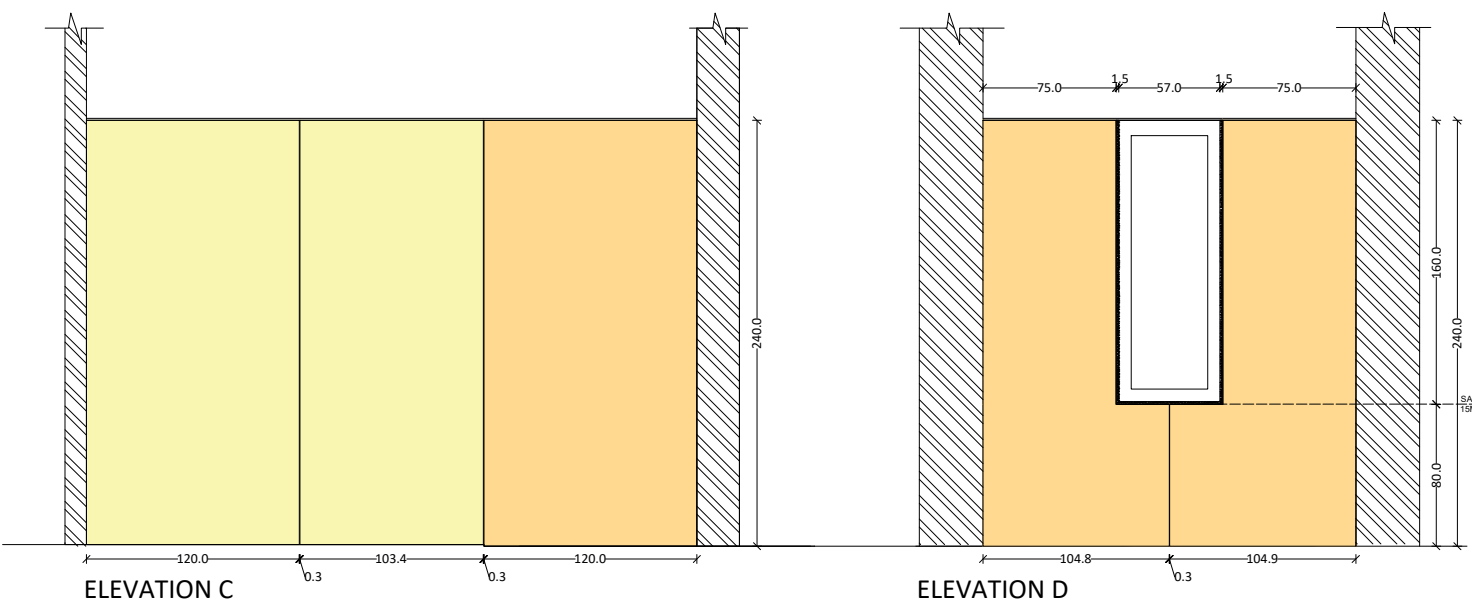

	PROJECT: FARM HOUSE @ TIRUNELVELI	DWG TITLE: BEDROOM 3 TOILET DETAILS (NEAR STAIRCASE)	DATE: 23.05.2024	REVISED DATE: 28.06.2024	ALL DIMENSIONS ARE IN CMS No dimensions to be scaled off from the drawings only written dimensions to be. In the event of any discrepancy or difference between any interior drawings or site conditions or other wise immediate reference is to be made to the designer for clarification prior to execution of work at site
		DRAWN: AA	CHECKED:	REVISION NO:	
	REVISION:			SCALE: NTS	