



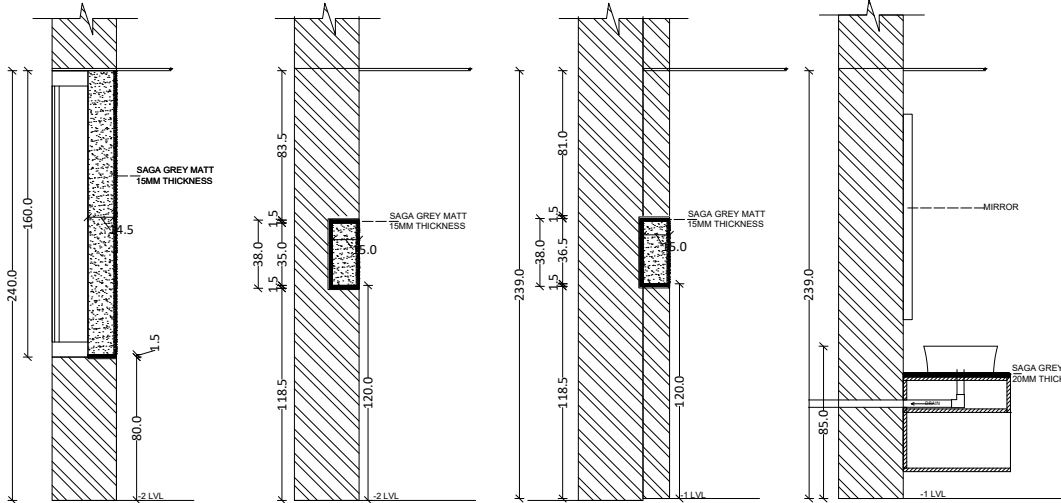


SECTION A


SECTION B

SECTION C

SECTION D

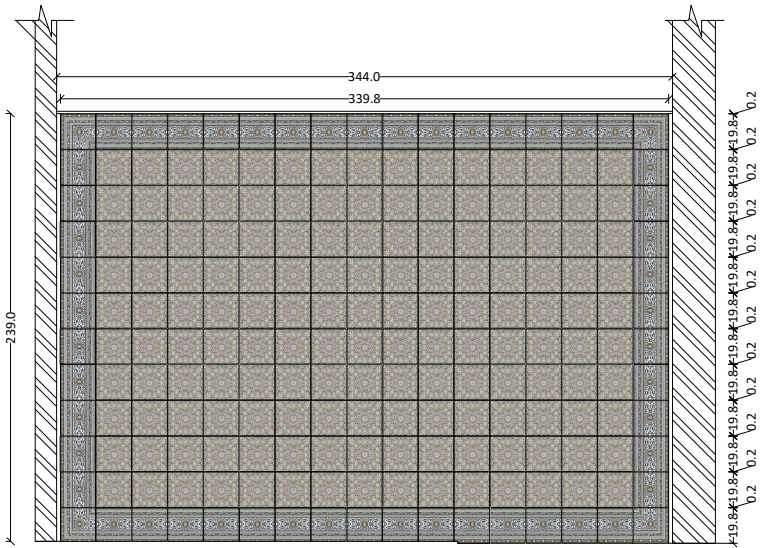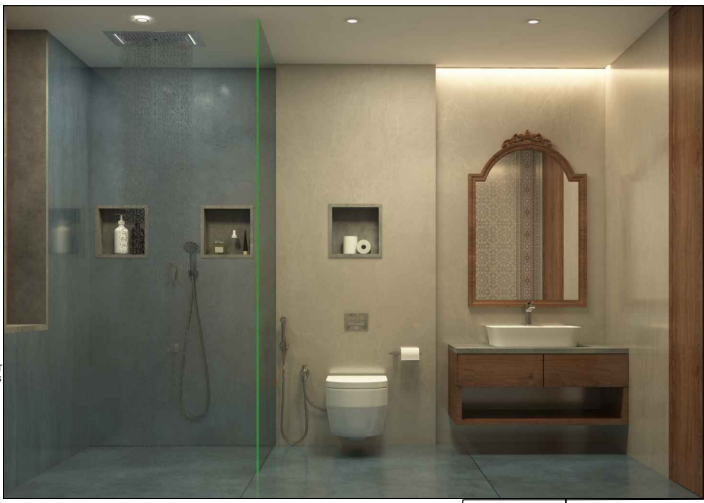


ELEVATION C

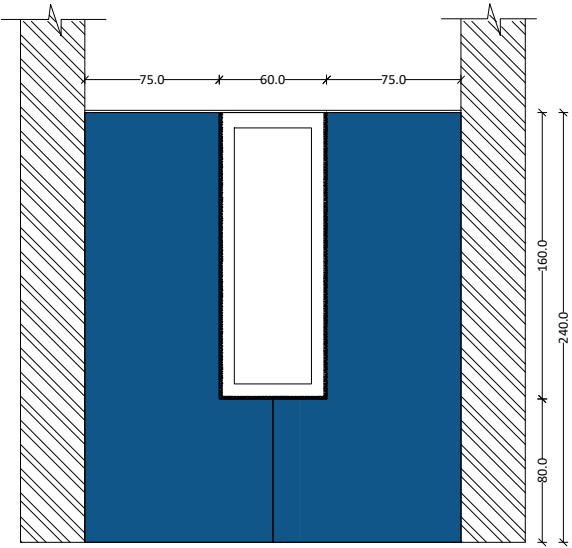


ELEVATION D


	DRY AREA WALLS NEXION RUNA GRIGIO CHIRIO GREY 240 x 120 CM
	WET AREA ALL WALLS & FLOOR DRY AREA FLOOR NEXION TERRAELINO GINEPRO (BLUE) NATURALE 240 x 120 CM
	NICHE & TOP OF LEDGE WALL SERA GREY POLISH 300x80 CM 15MM THICKNESS
	HIGHLIGHT WALL WET AREA FOLK ORIGIN CORNER 19.8CMx19.8CM
	HIGHLIGHT WALL WET AREA FOLK ORIGIN BORDER 19.8CMx19.8CM
	HIGHLIGHT WALL WET AREA FOLK ORIGIN BASE 19.8CMx19.8CM

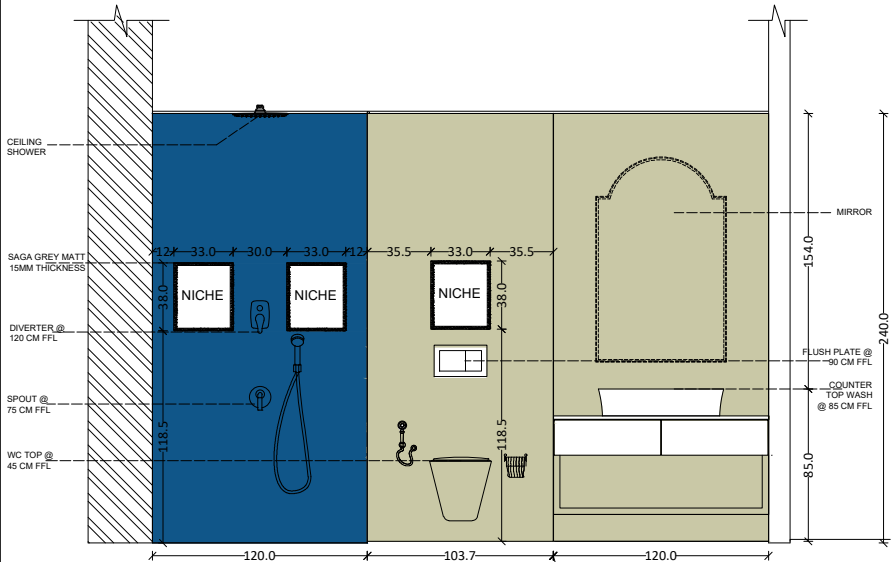


ELEVATION A

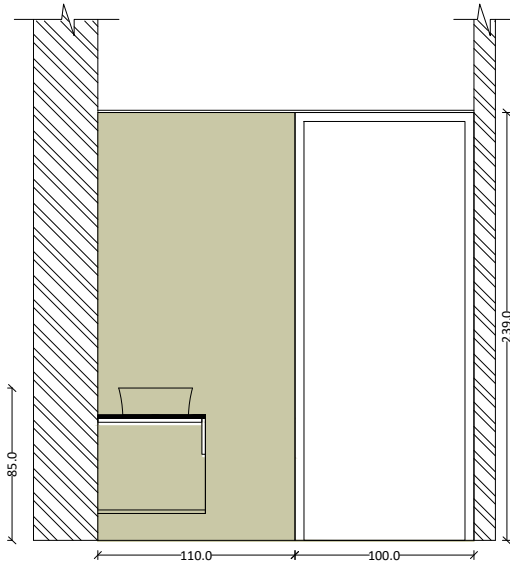


ELEVATION B

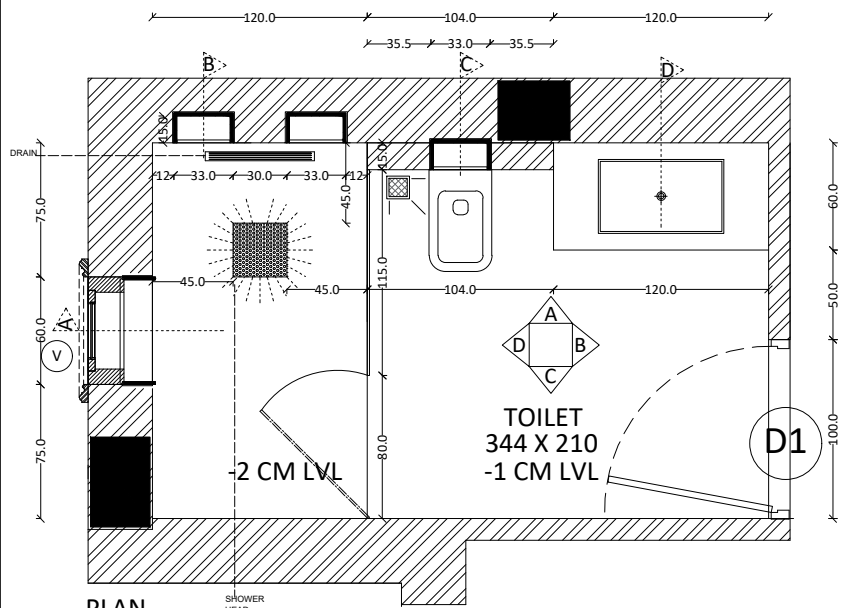

PLAN

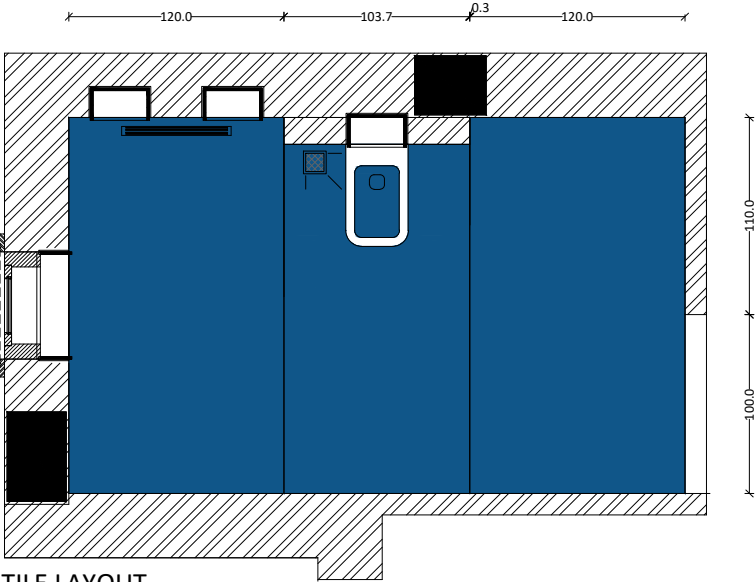

TILE LAYOUT

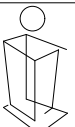

AHANAS

PROJECT:
FARM HOUSE @ TIRUNELVELI

REVISION:

DWG TITLE:BEDROOM 4 TOILET
DETAILS (SABARI BEDROOM)

DRAWN: AA

DATE: 23.05.2024

CHECKED:

REVISED DATE: 28.06.2024

REVISION NO:

SCALE: NTS

ALL DIMENSIONS ARE IN CMS
No dimensions to be scaled off from the drawings only written dimensions to be.
In the event of any discrepancy or difference between any interior drawings or site conditions or other wise immediate reference is to be made to the designer for clarification prior to execution of work at site