

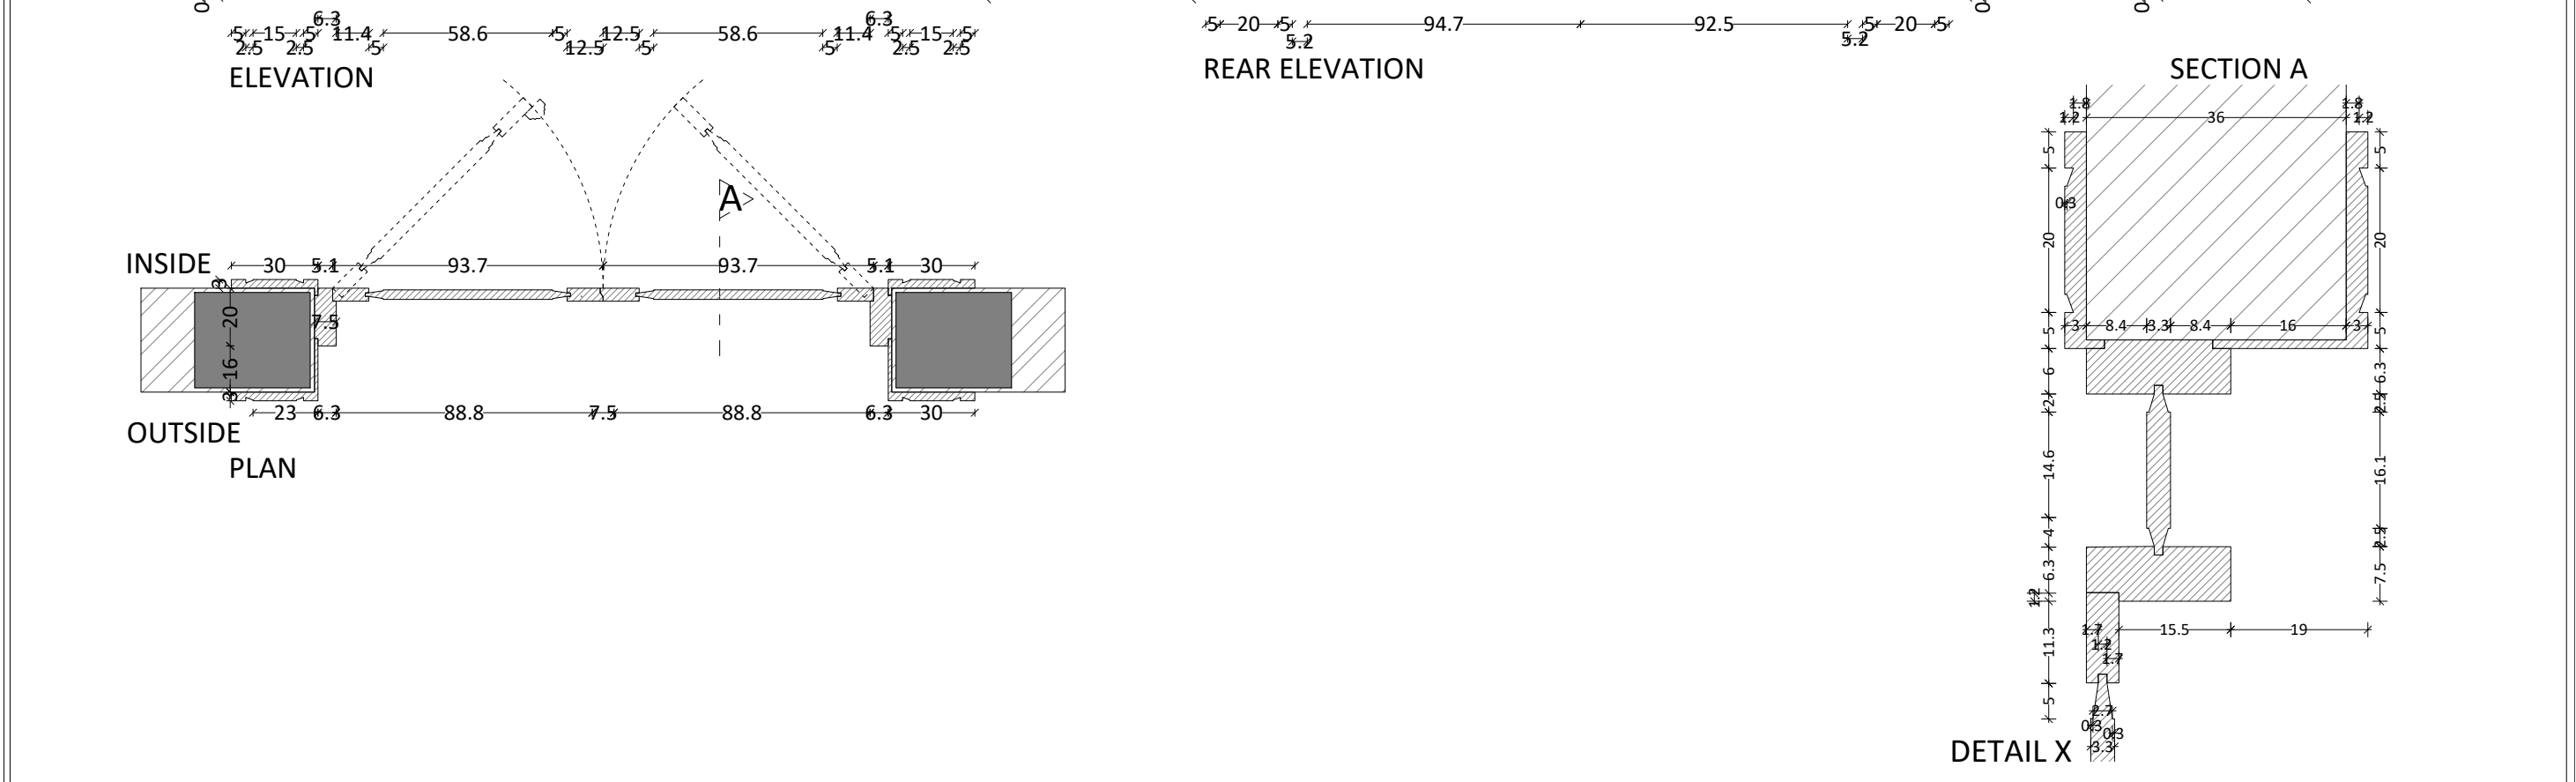
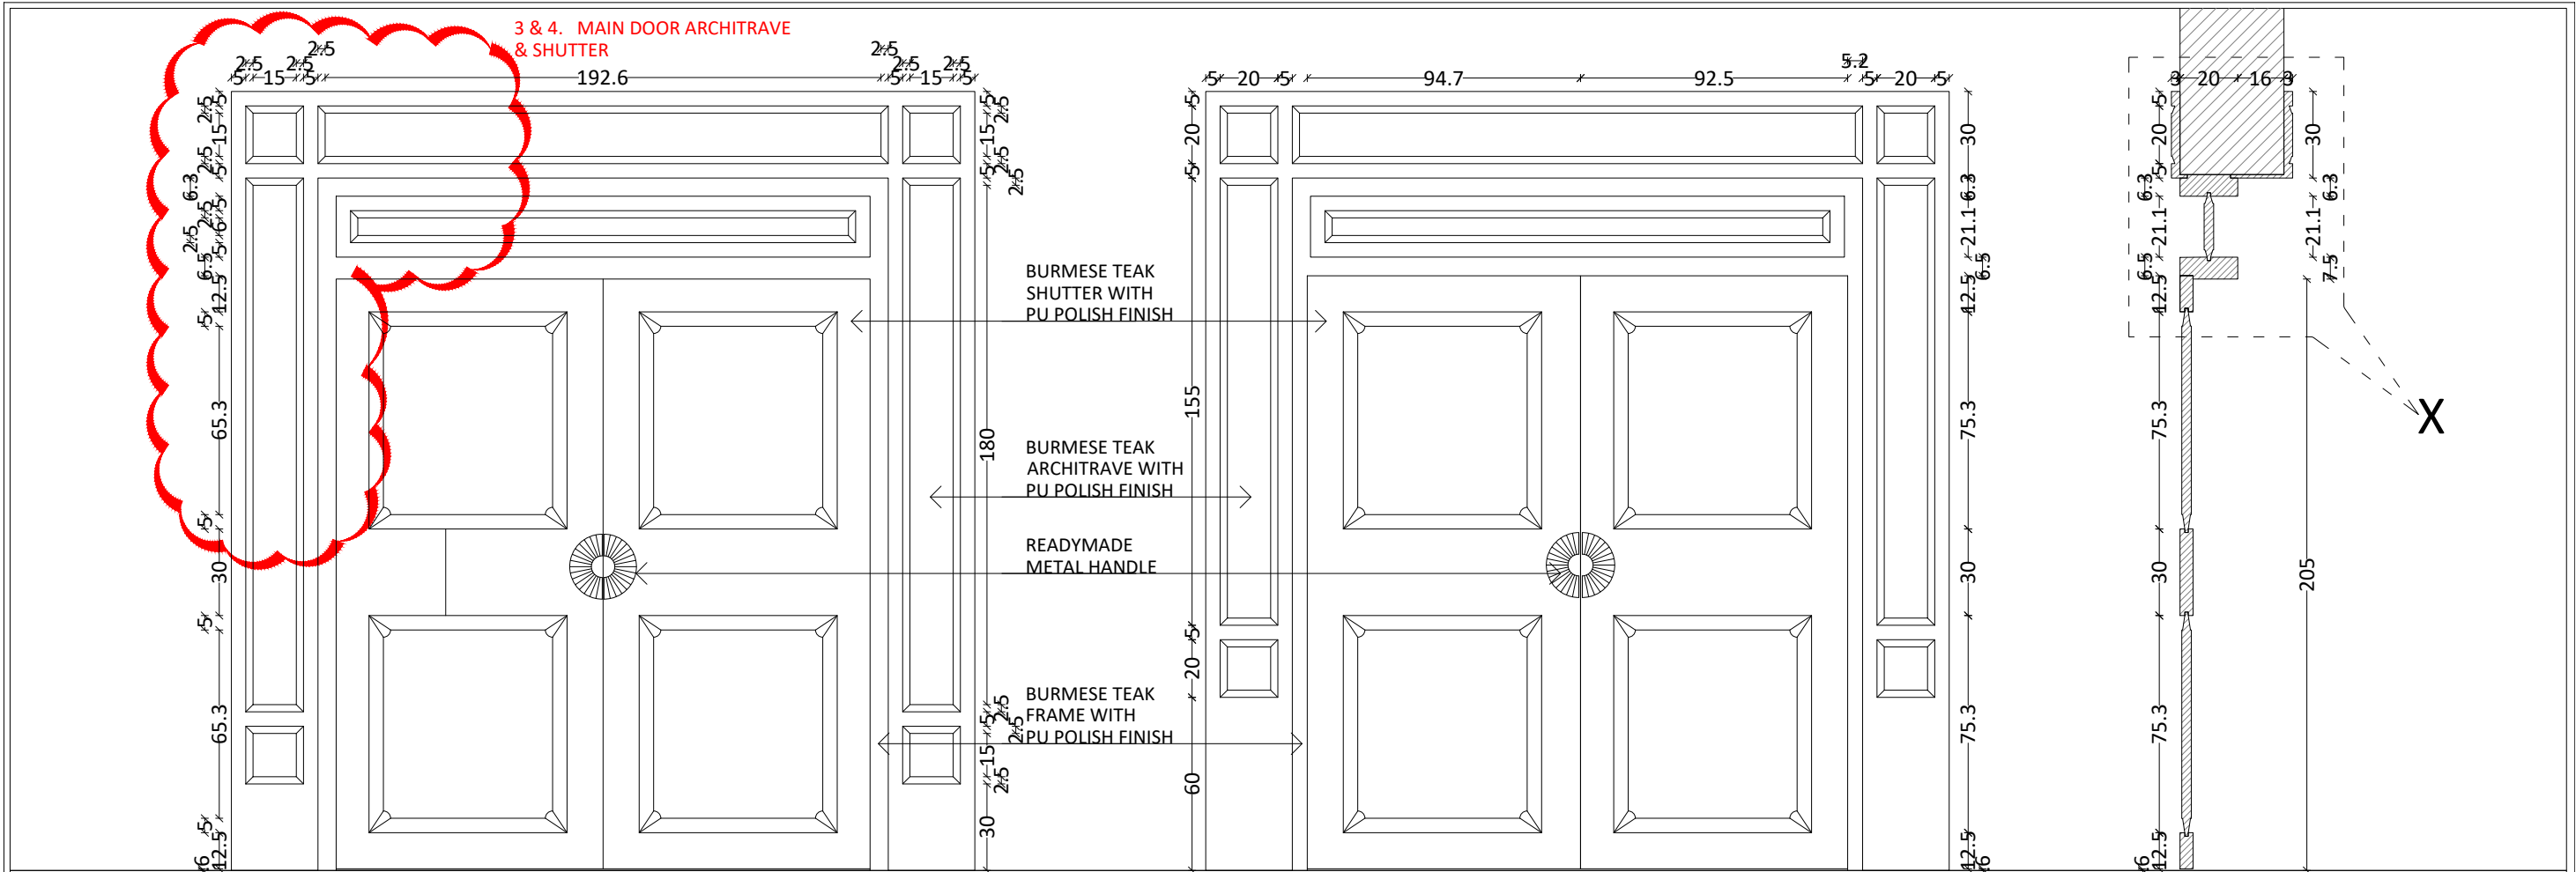
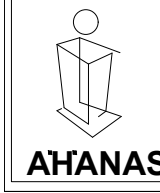
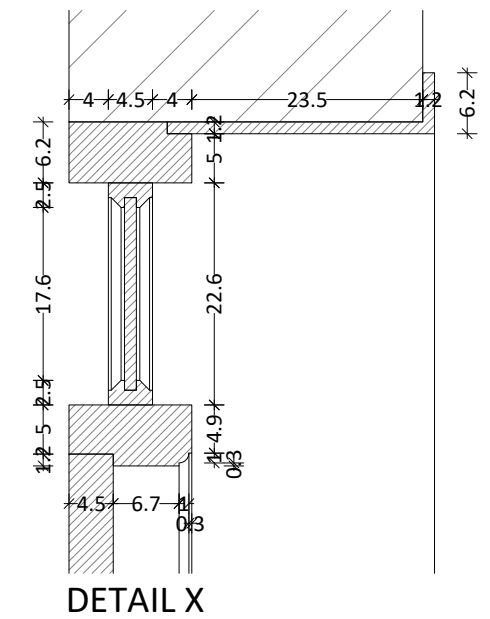



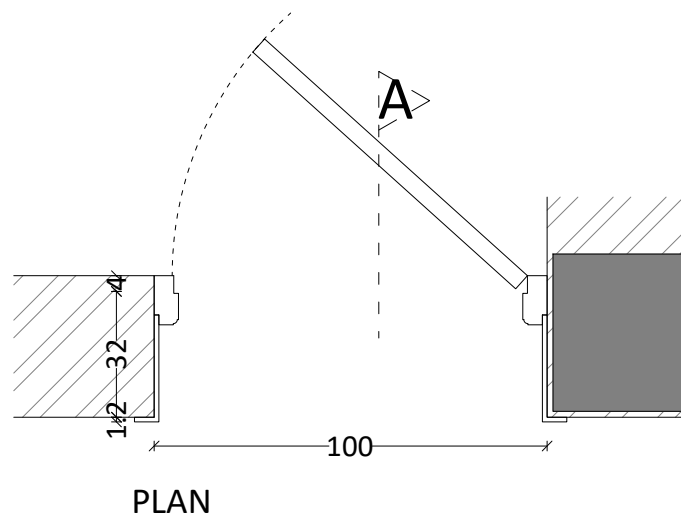


	PROJECT: FARM HOUSE @ TIRUNELVELI	DWG TITLE: MAIN DOOR	DRAWN:	REVISED DATE: 29-08-2024	ALL DIMENSIONS ARE IN CMS No dimensions to be scaled off from the drawings only written dimensions to be followed. In the event of any discrepancy or difference between any interior drawings or site conditions or other wise immediate reference is to be made to the designer for clarification prior to execution of work at site
	ITEM:	DATE: 28/05/2024	CHECKED:	REVISION NO : R01	
				SCALE: 1:25	



5. ROOM DOOR TOP PORTION
WOOD WORK SAMPLE

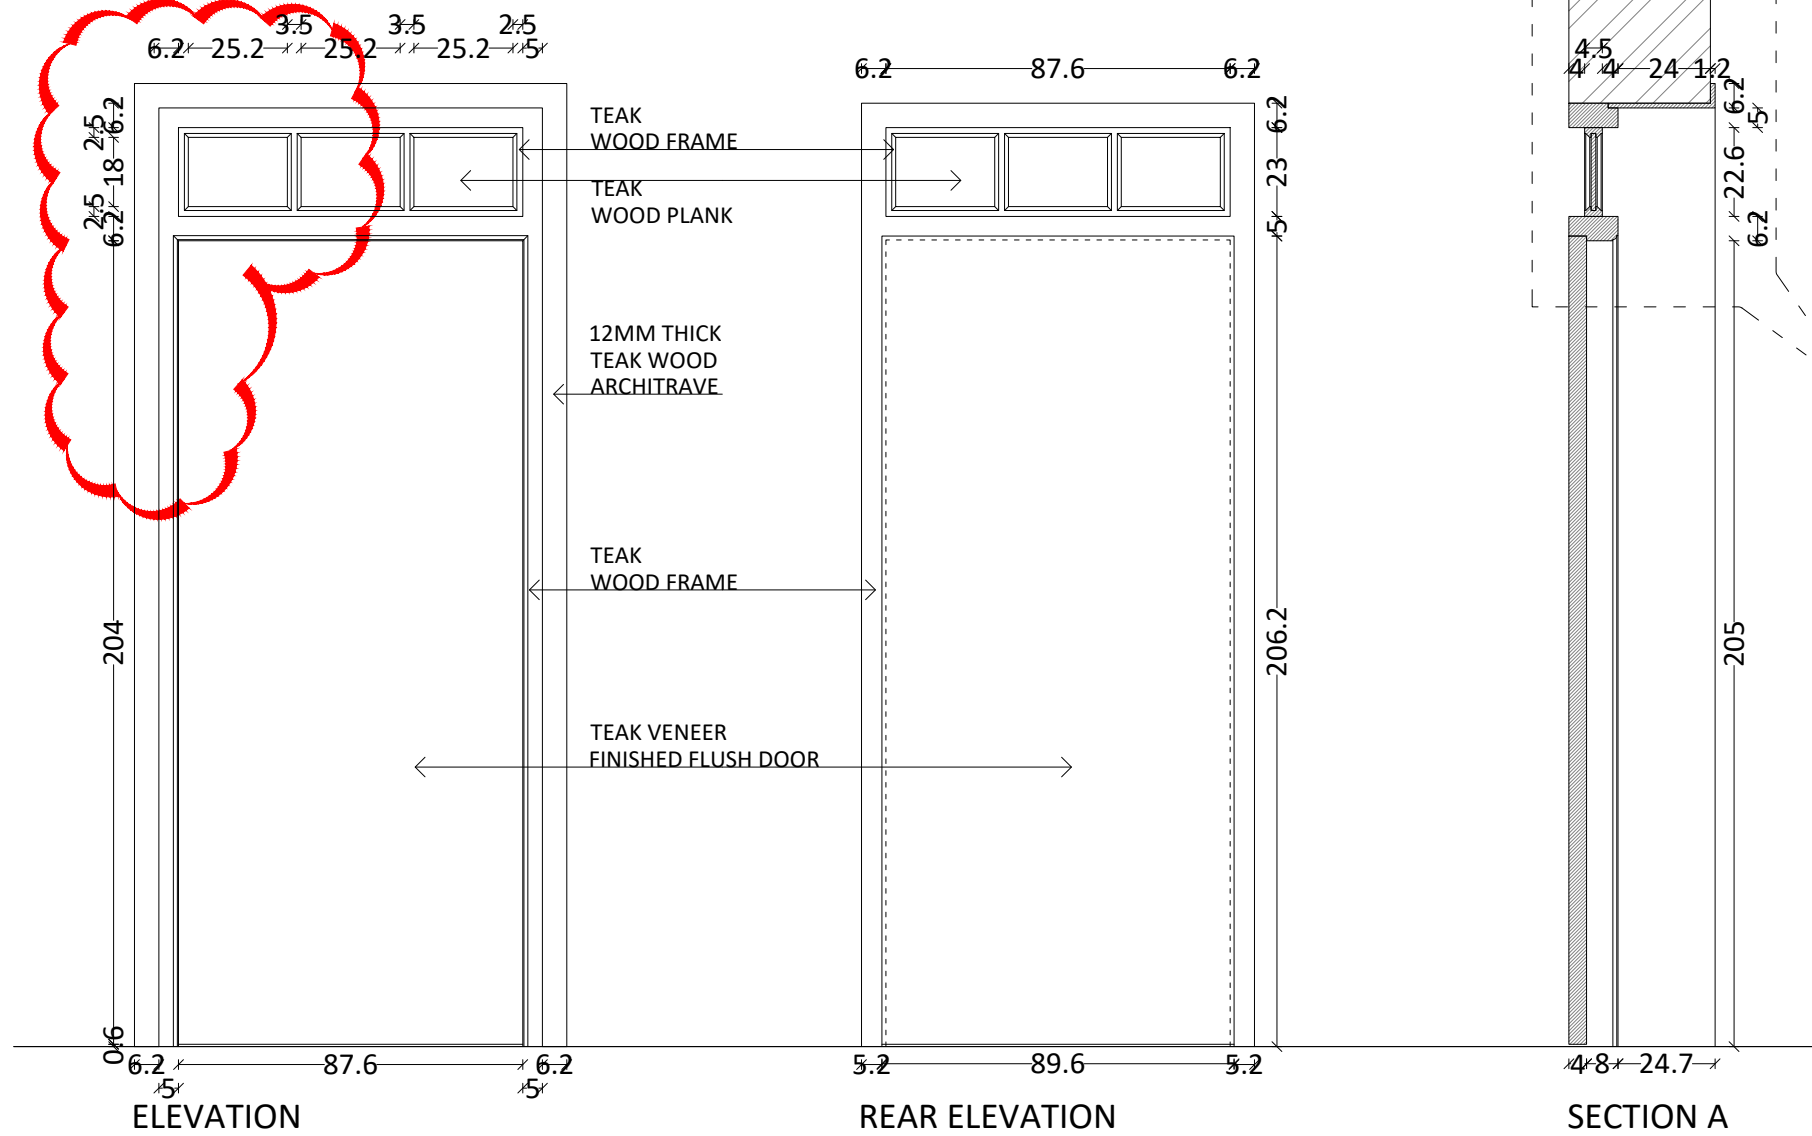

	PROJECT: FARM HOUSE @ TIRUNELVELI	DWG TITLE: TYPICAL DOORS	DRAWN:	REVISED DATE:	ALL DIMENSIONS ARE IN CMS No dimensions to be scaled off from the drawings only written dimensions to be followed. In the event of any discrepancy or difference between any interior drawings or site conditions or other wise immediate reference is to be made to the designer for clarification prior to execution of work at site
	ITEM:	DATE: 16/02/2024	CHECKED:	REVISION NO:	
				SCALE: 1:25	

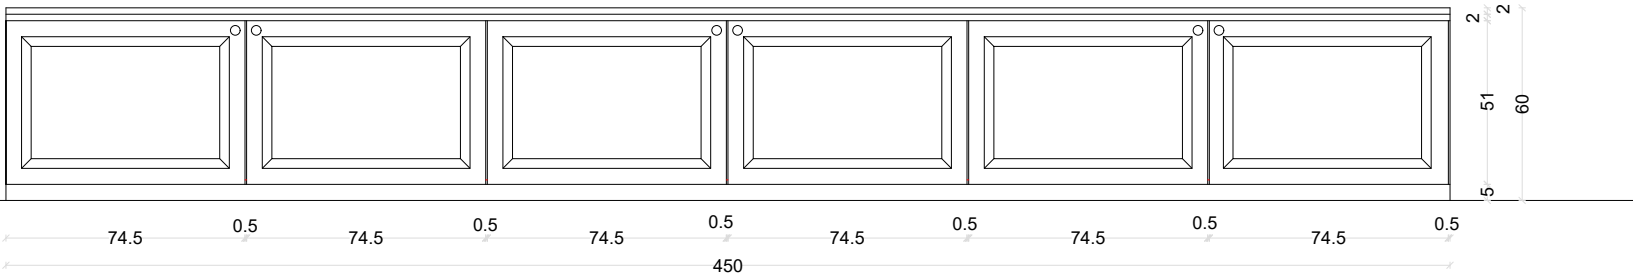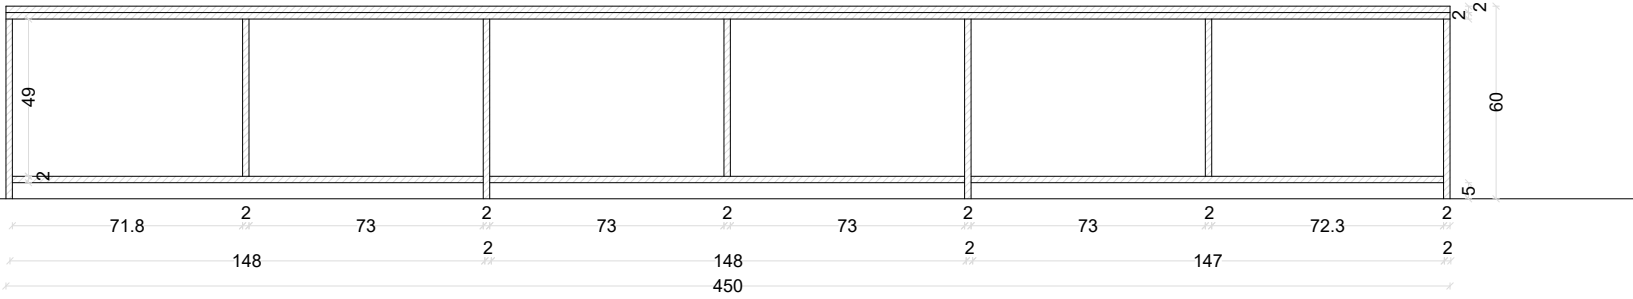


FRONT ELEVATION

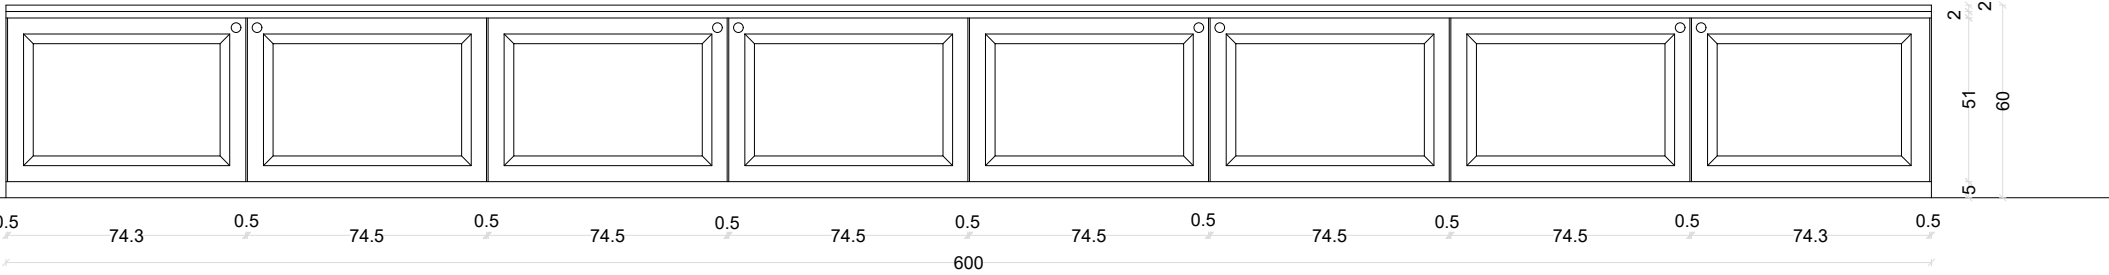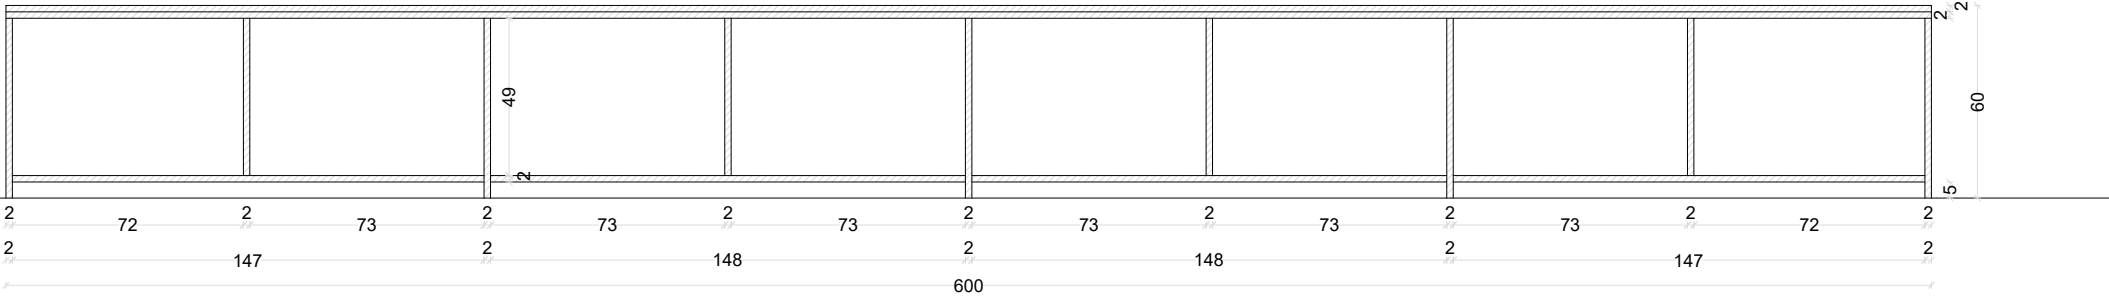


FRONT ELEVATION

DOOR DETAIL

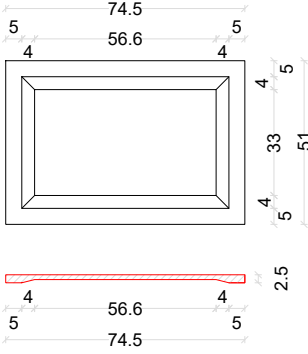

DOOR DETAIL

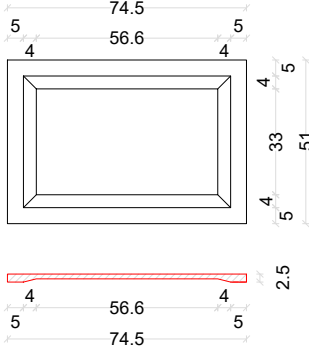

CARDINAL DIRECTION:



KEY PLAN:


KEY PLAN TO BE SHOWN

GENERAL NOTES:

- ALL DIMENSIONS ARE IN CMS, UNLESS OTHERWISE SPECIFIED.
- DIMENSIONS SHALL NOT BE MEASURED DIRECTLY FROM THIS DRAWINGS. FOLLOW ONLY WRITTEN DIMENSIONS.
- IN THE EVENT OF ANY DISCREPANCY OR DIFFERENCE BETWEEN ANY DRAWINGS OR SITE CONDITIONS / OTHERWISE IMMEDIATE REFERENCE IS TO BE MADE TO THE DESIGNER.
- FOR CLARIFICATION PRIOR TO EXECUTION OF WORK AT SITE.
- ALL THE CIVIL/INTERIOR WORKS SHOULD BE IN LINE LEVEL & PLUMB.
- PLASTERING TO BE CUT AT SKIRTING LEVEL (AS PER SPECIFICATION).

REVISION NOTES:

ARCHITECTURAL/INTERIOR DESIGN CONSULTANT:

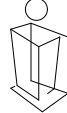

AHANAS
DESIGN SPACE

33/1622A, 'NAVAM'
Haritha By-Lane
Vennala P.O, Kochi 682 028
Email: ahanas@ahanas.com

STRUCTURAL CONSULTANT: /MEP CONSULTANT:

CLIENT:

MR. SHABAREESH

PROJECT:

FARMHOUSE @ TIRUNELVELI

STATUS/ISSUED FOR:

REFERENCE

DRAWING TITLE:

DORMITORY SIDEBORD

DRAWN:

VM

CHECKED:

-

REVISION:

-

PROJECT NO:

563

DRAWING NO:

-

SCALE:



NTS

SHEET SIZE:


A3


DATE:

24/03/2025

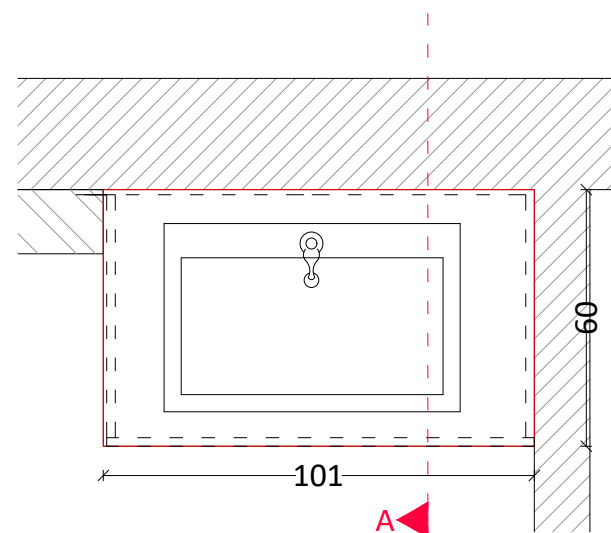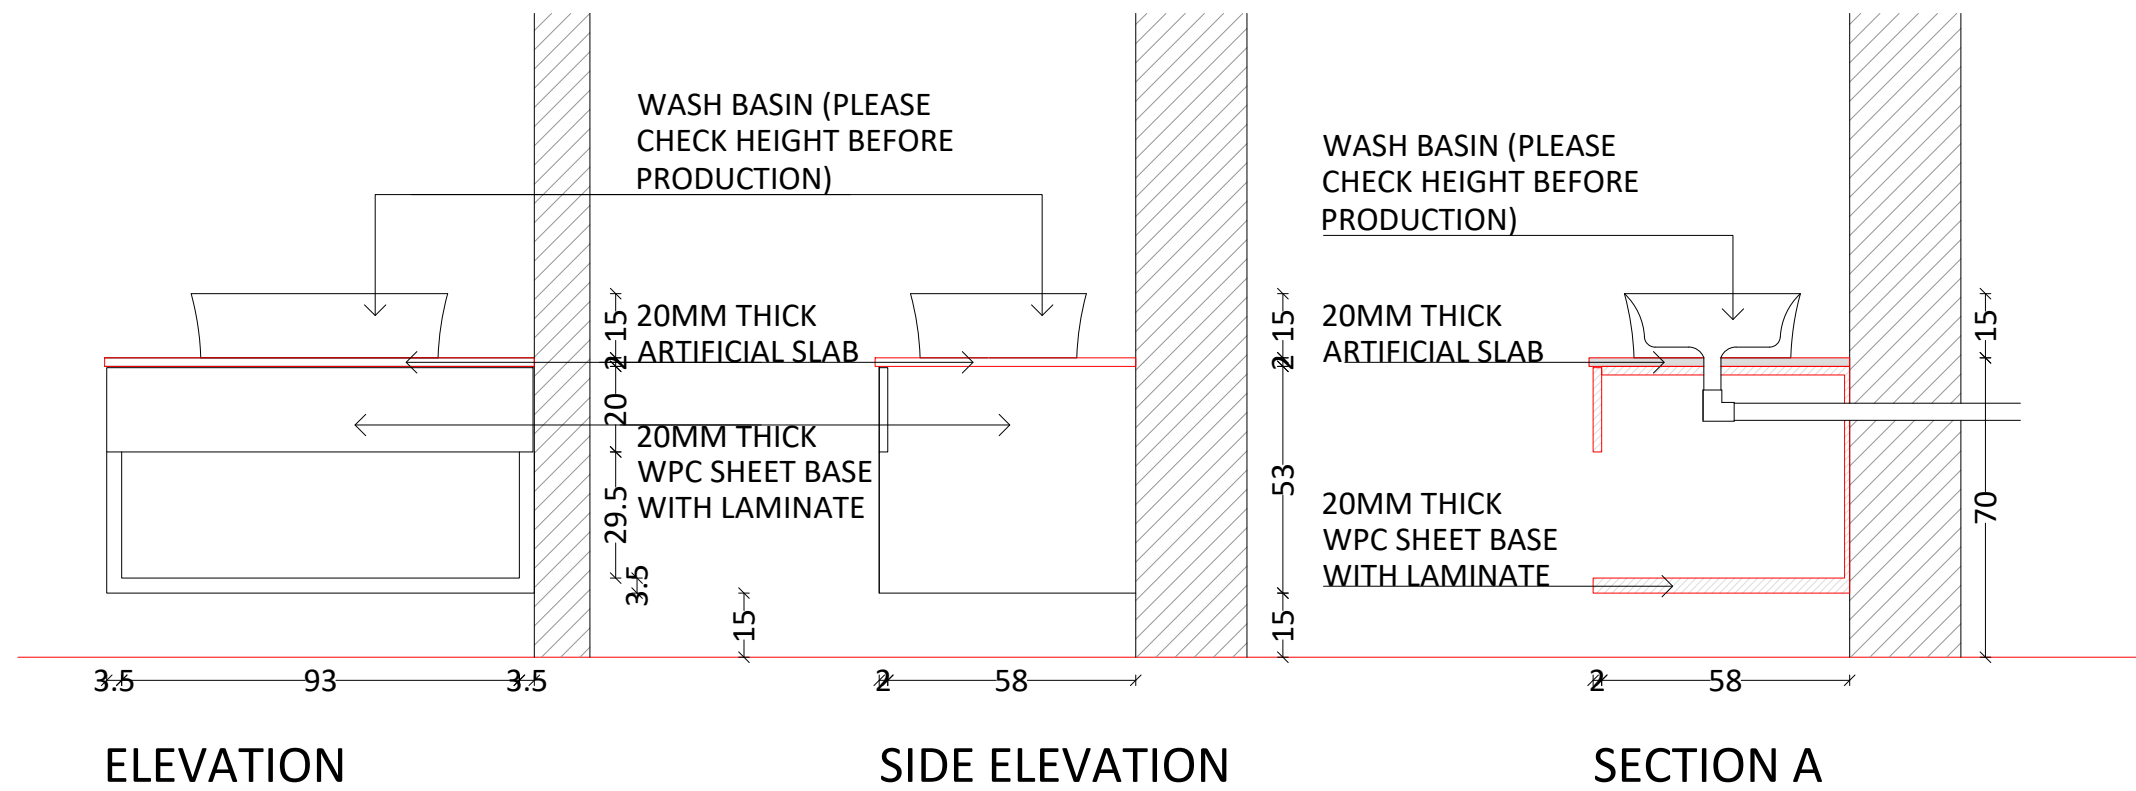


PROJECT: FARM HOUSE @ TIRUNELVELI	DWG TITLE: BED 1 TOILET WASH COUNTER DETAILS	DRAWN: NA	REVISED DATE:	ALL DIMENSIONS ARE IN CMS No dimensions to be scaled off from the drawings only written dimensions to be. In the event of any discrepancy or difference between any interior drawings or site conditions or other wise immediate reference is to be made to the designer for clarification prior to execution of work at site
DWG NO:	DATE: 18/07/2024	CHECKED:	REVISION NO:	
REVISION:			SCALE: 1:25	

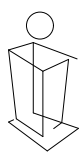

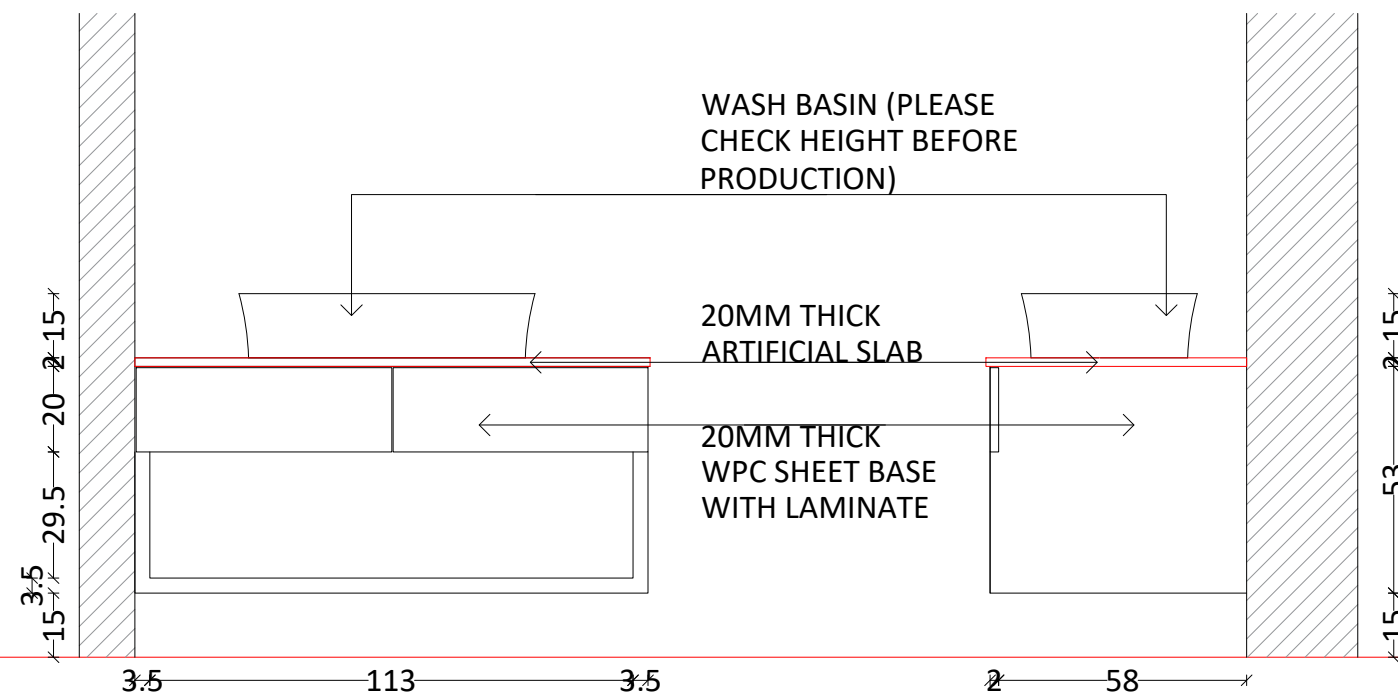


ELEVATION

SIDE ELEVATION

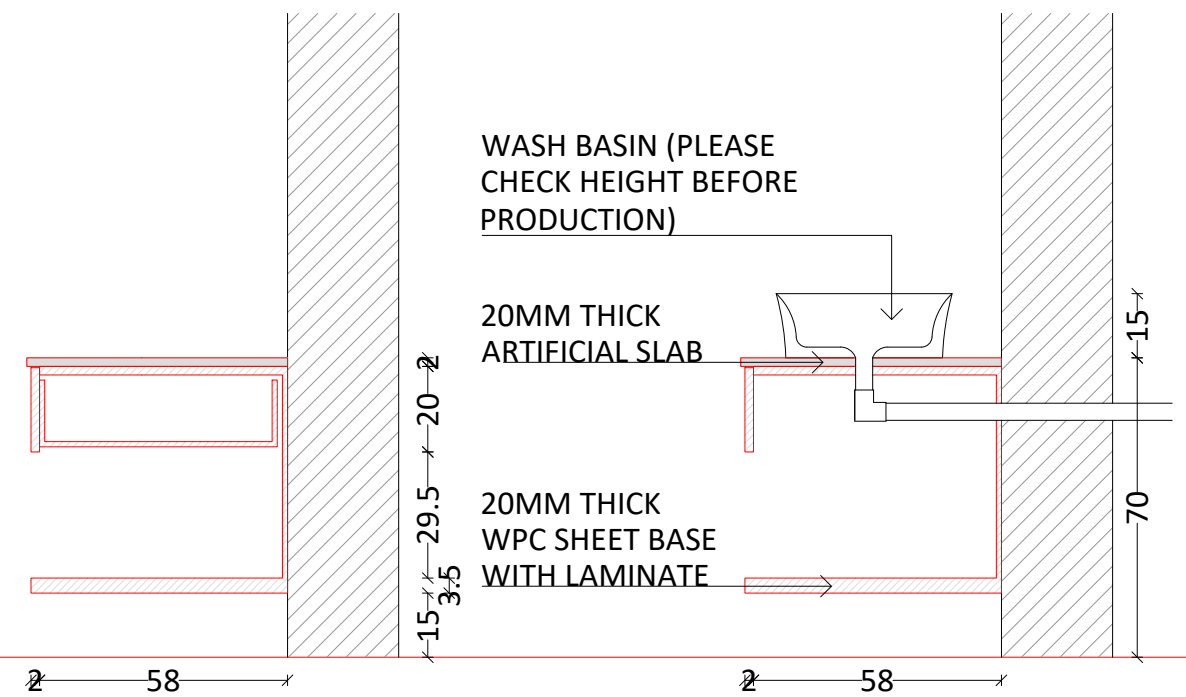


SECTION A

SECTION B




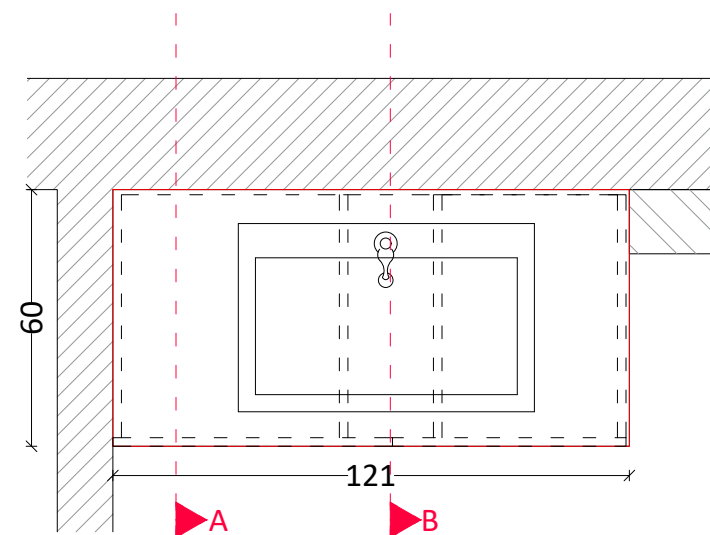


PLAN






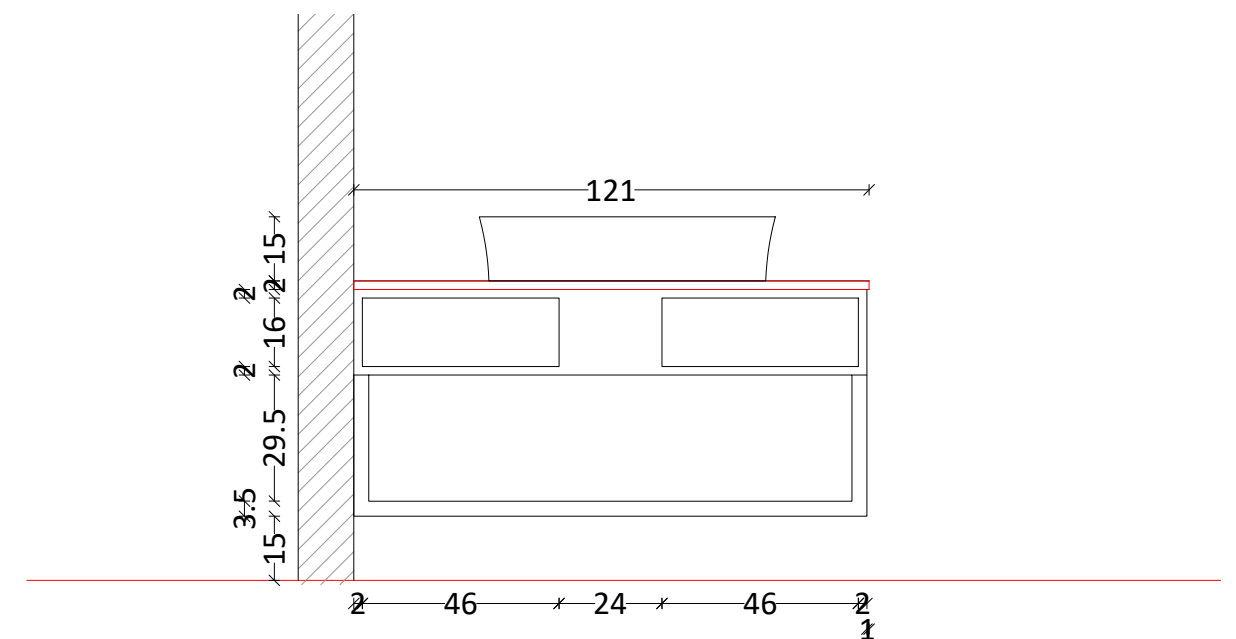


INSIDE PARTITION ELEVATION


PROJECT: FARM HOUSE @ TIRUNELVELI	DWG TITLE: BED 2,3 & 4 TOILET WASH COUNTER DETAILS	DRAWN: NA	REVISED DATE:	ALL DIMENSIONS ARE IN CMS No dimensions to be scaled off from the drawings only written dimensions to be. In the event of any discrepancy or difference between any interior drawings or site conditions or other wise immediate reference is to be made to the designer for clarification prior to execution of work at site
DWG NO:	DATE: 18/07/2024	CHECKED:	REVISION NO:	
REVISION:			SCALE: 1:25	

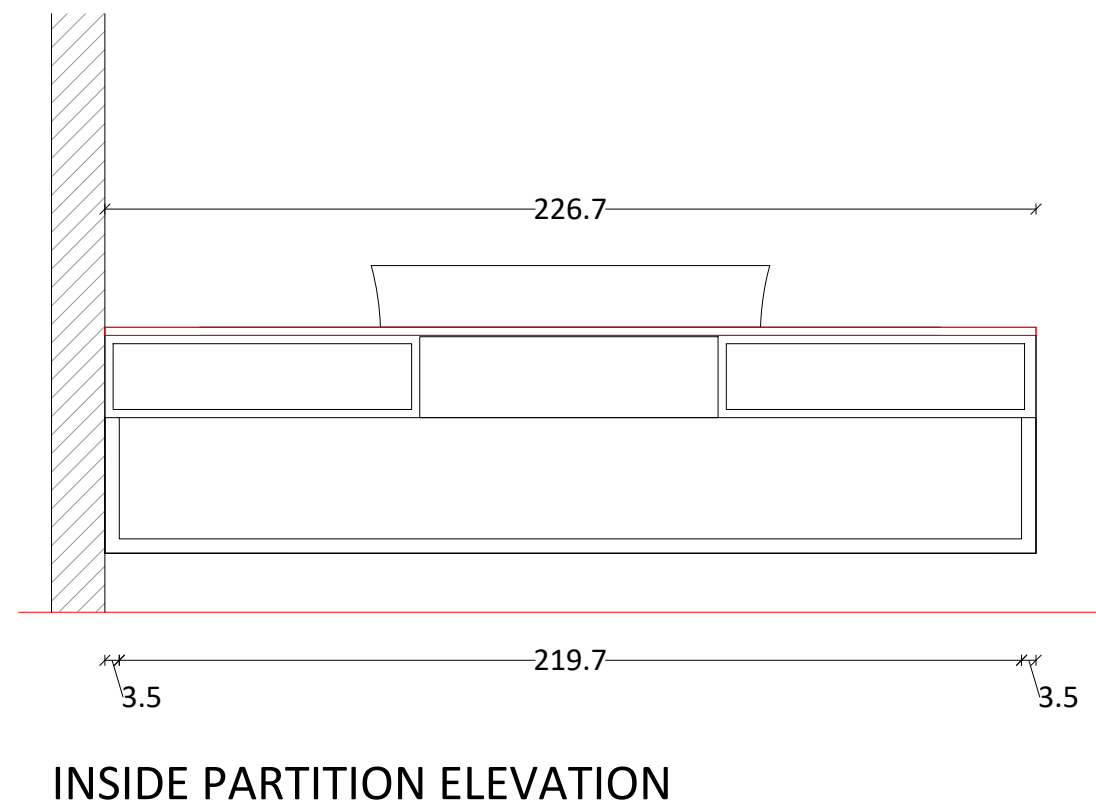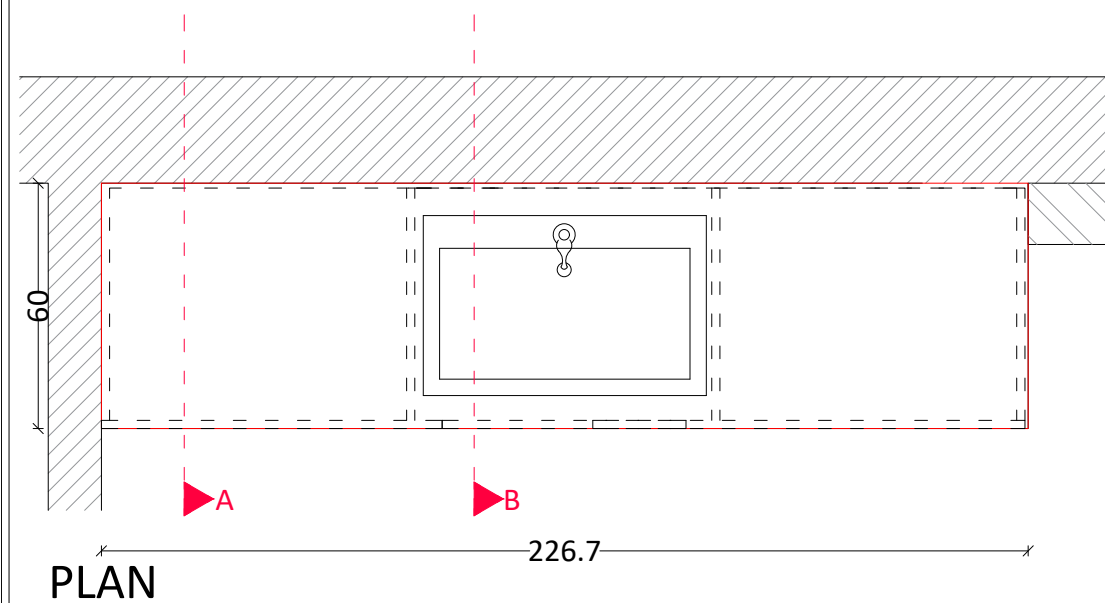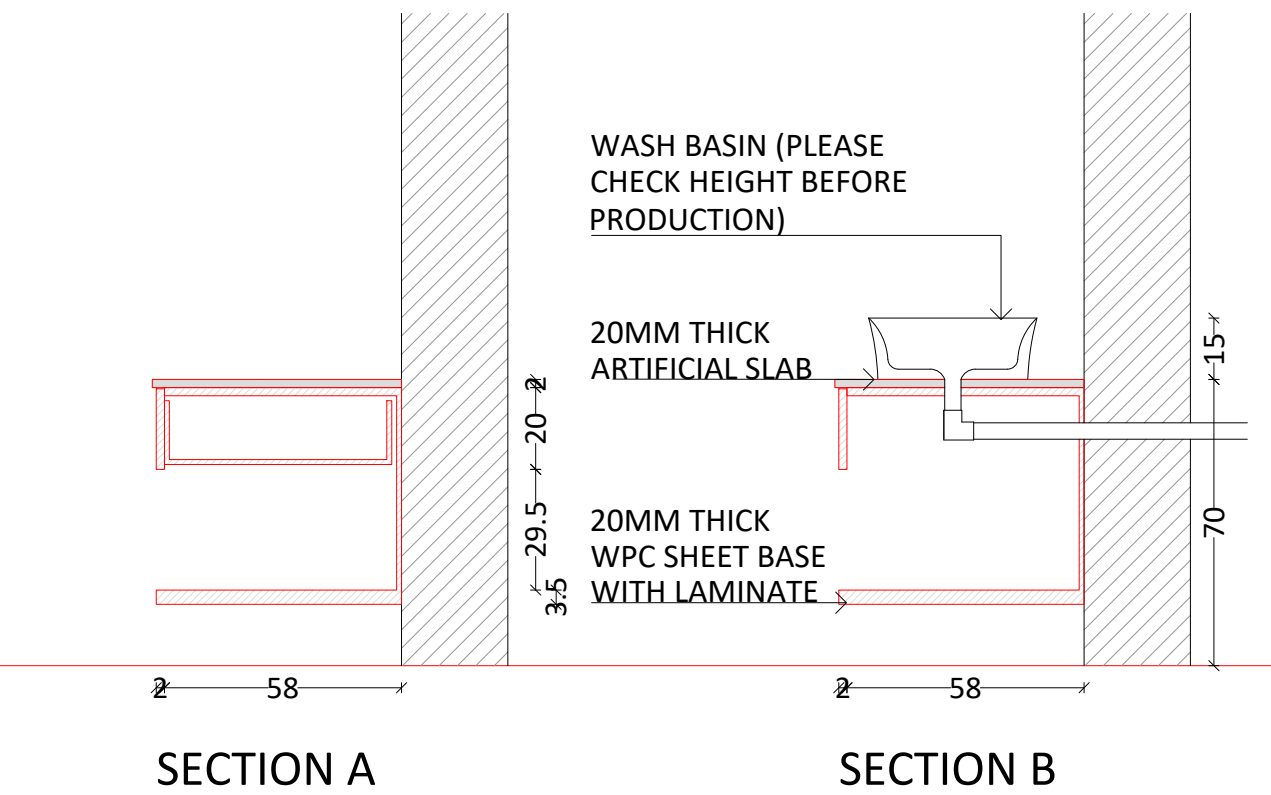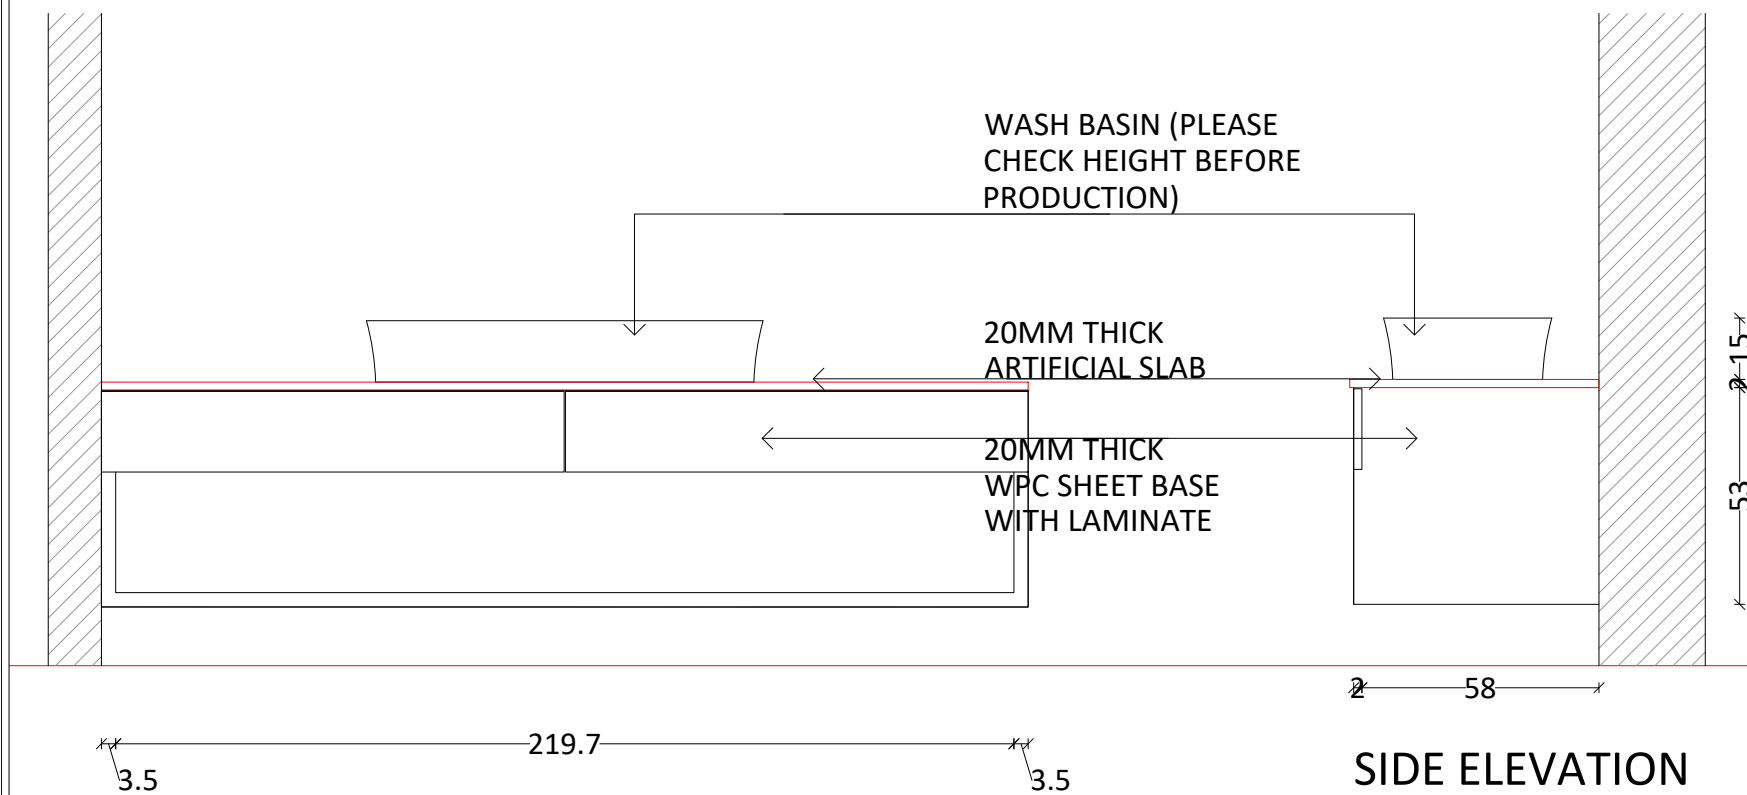


PROJECT: FARM HOUSE @ TIRUNELVELI	DWG TITLE: GF & FF DORMITORY TOILET WASH COUNTER DETAILS	DRAWN: NA	REVISED DATE:	ALL DIMENSIONS ARE IN CMS No dimensions to be scaled off from the drawings only written dimensions to be. In the event of any discrepancy or difference between any interior drawings or site conditions or other wise immediate reference is to be made to the designer for clarification prior to execution of work at site
DWG NO:	DATE: 18/07/2024	CHECKED:	REVISION NO:	
REVISION:			SCALE: 1:25	

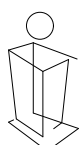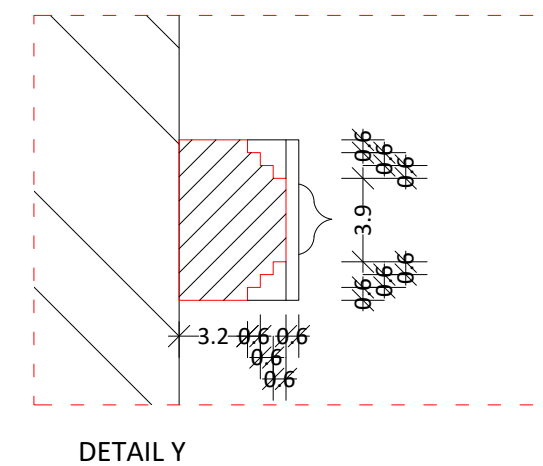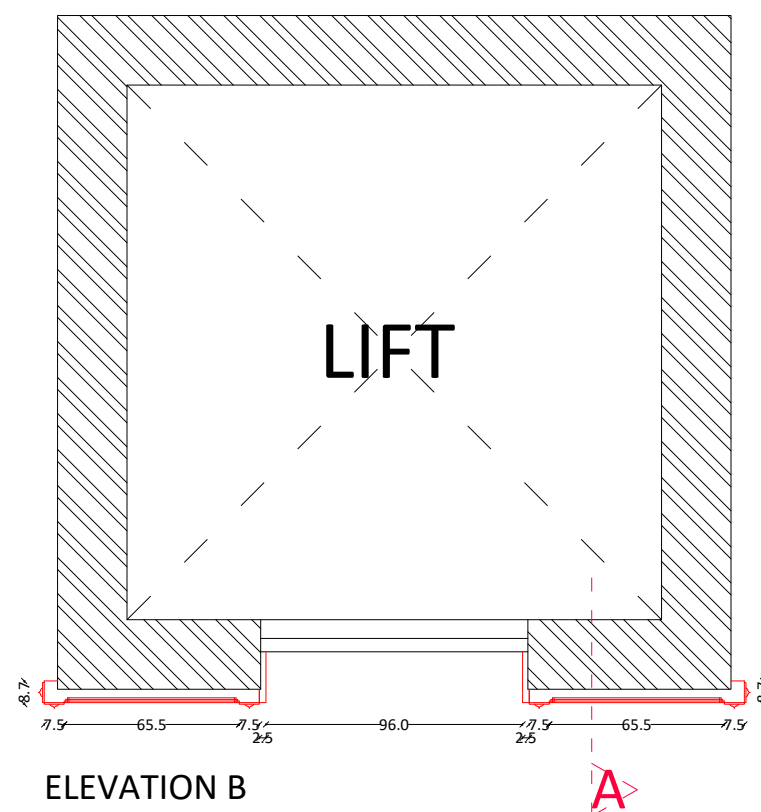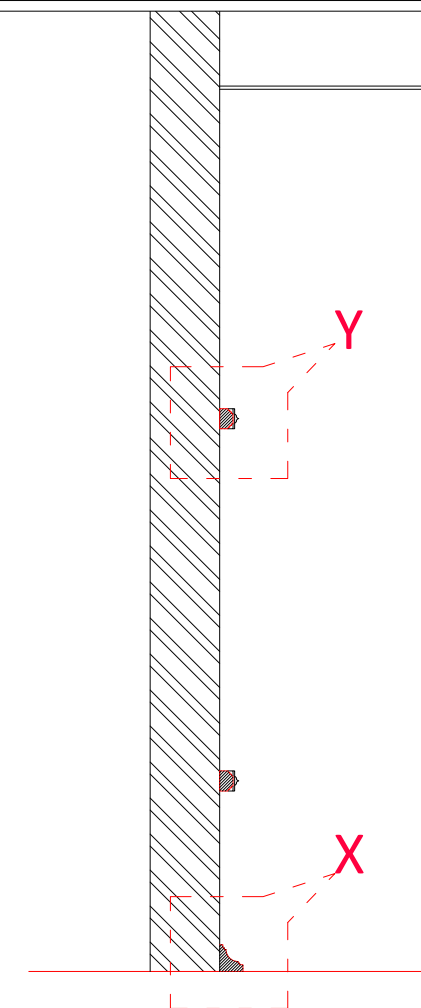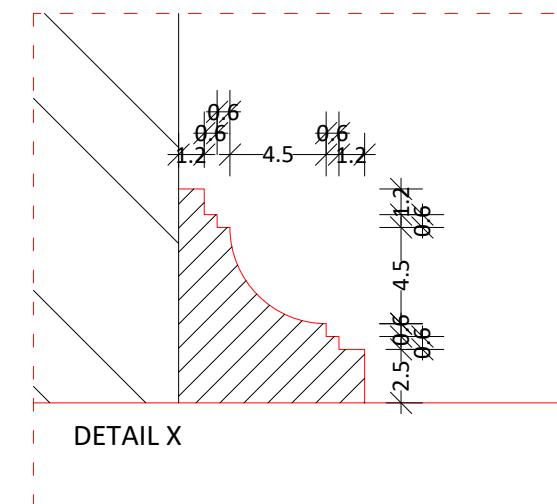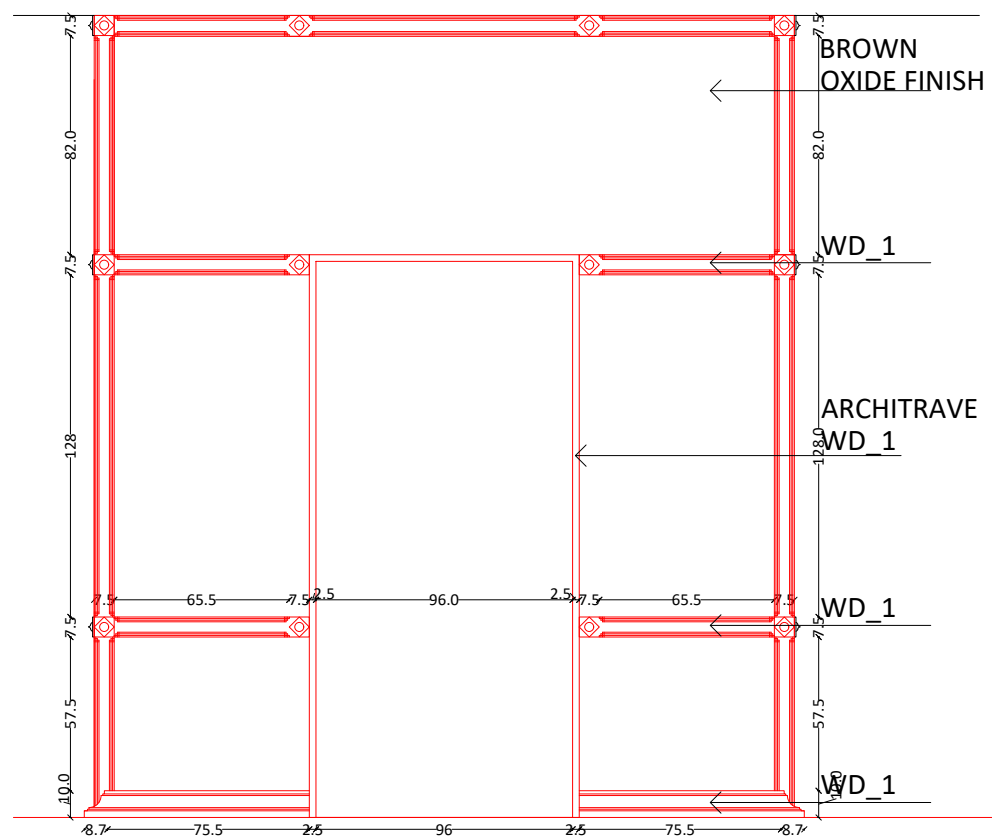


PROJECT: FARM HOUSE @ TIRUNELVELI	DWG TITLE: LIFT WALL CLADDING DETAILS	DRAWN: NA	REVISED DATE:	ALL DIMENSIONS ARE IN CMS No dimensions to be scaled off from the drawings only written dimensions to be. In the event of any discrepancy or difference between any interior drawings or site conditions or other wise immediate reference is to be made to the designer for clarification prior to execution of work at site
DWG NO:	DATE: 18/07/2024	CHECKED:	REVISION NO:	
REVISION:			SCALE: 1:25	

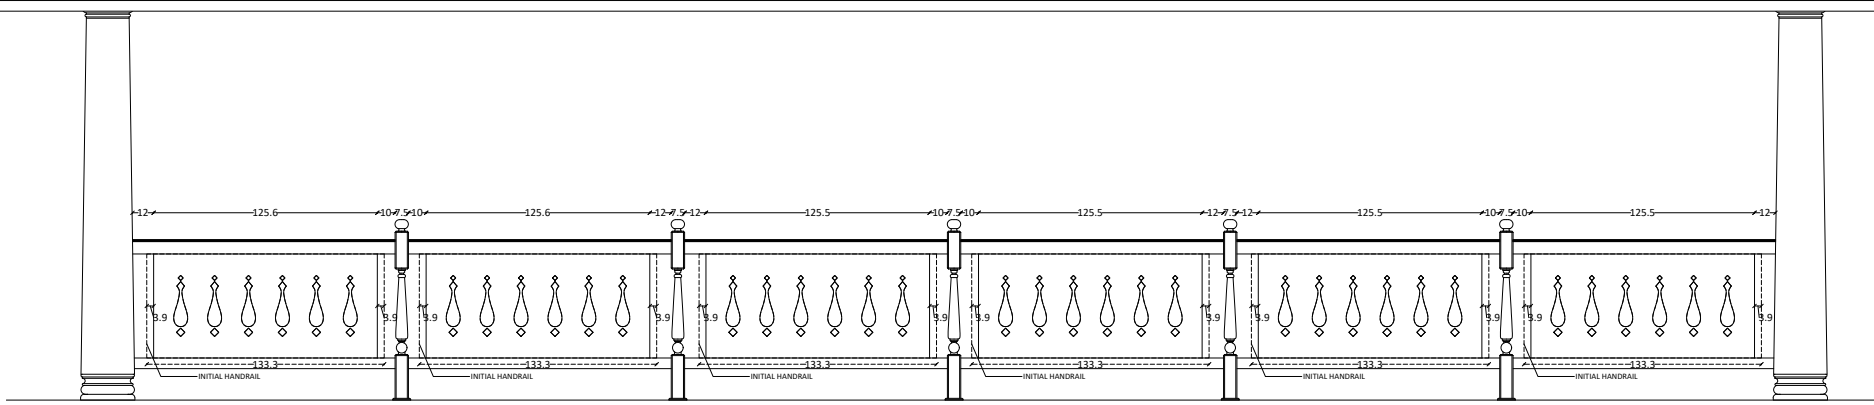


ELEVATION A

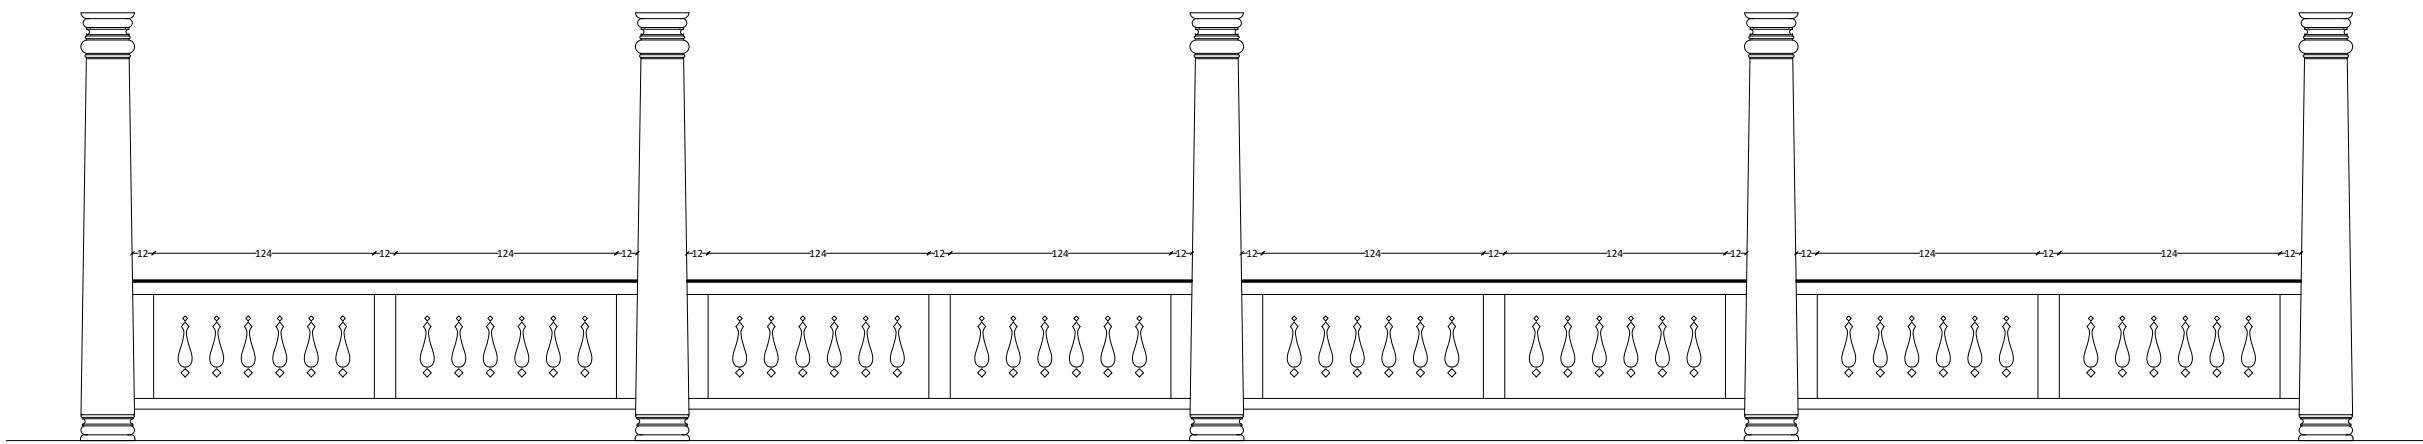

ELEVATION B

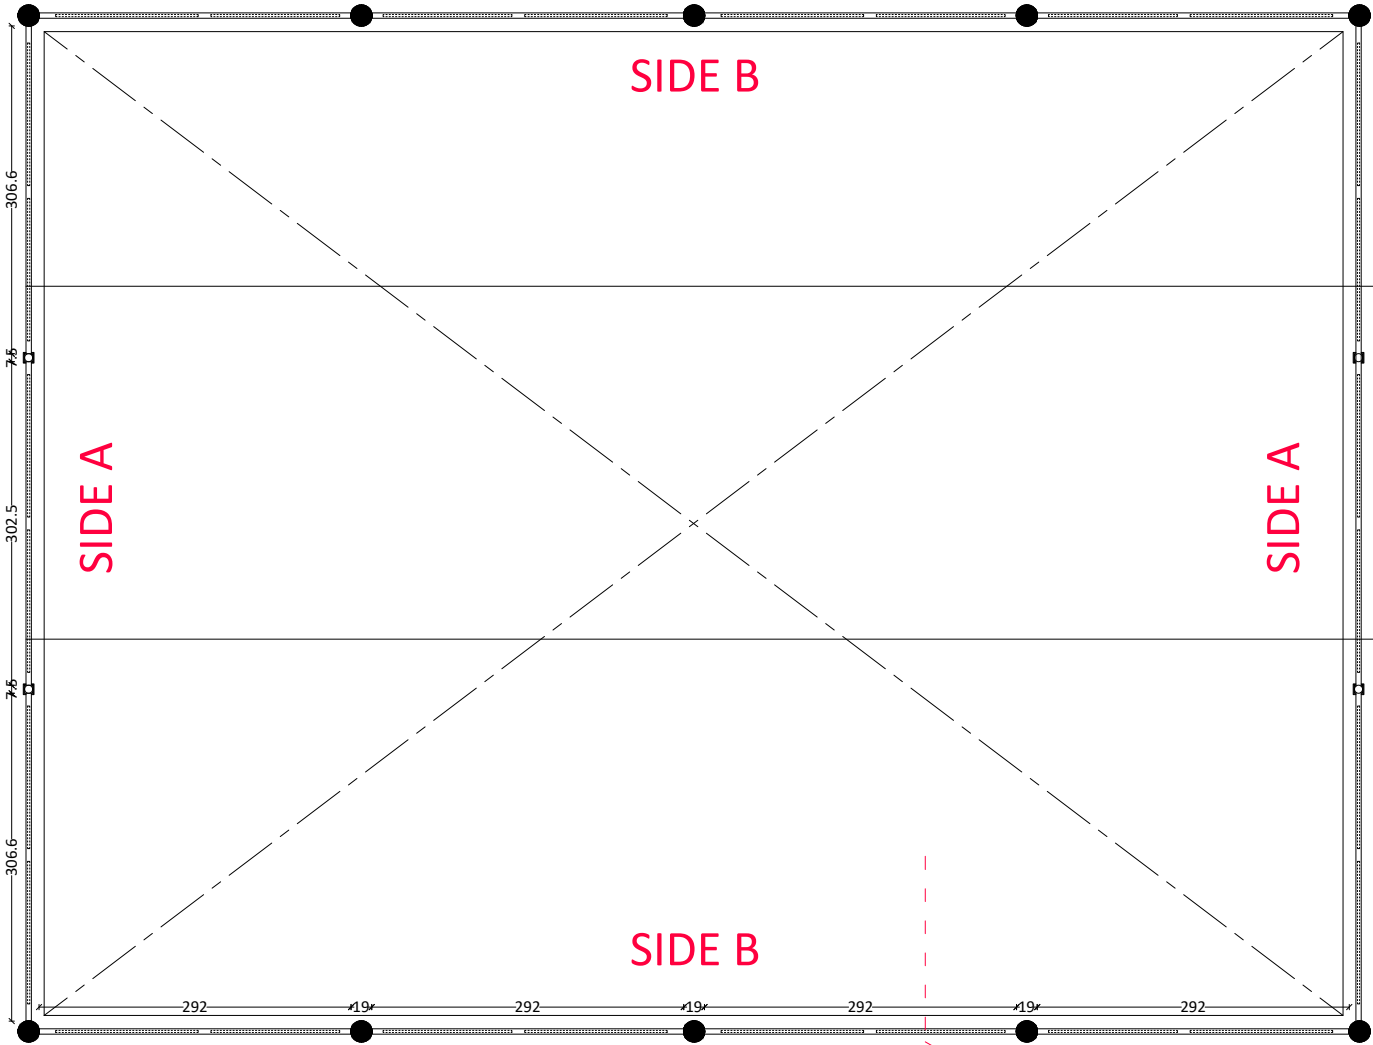


PLAN

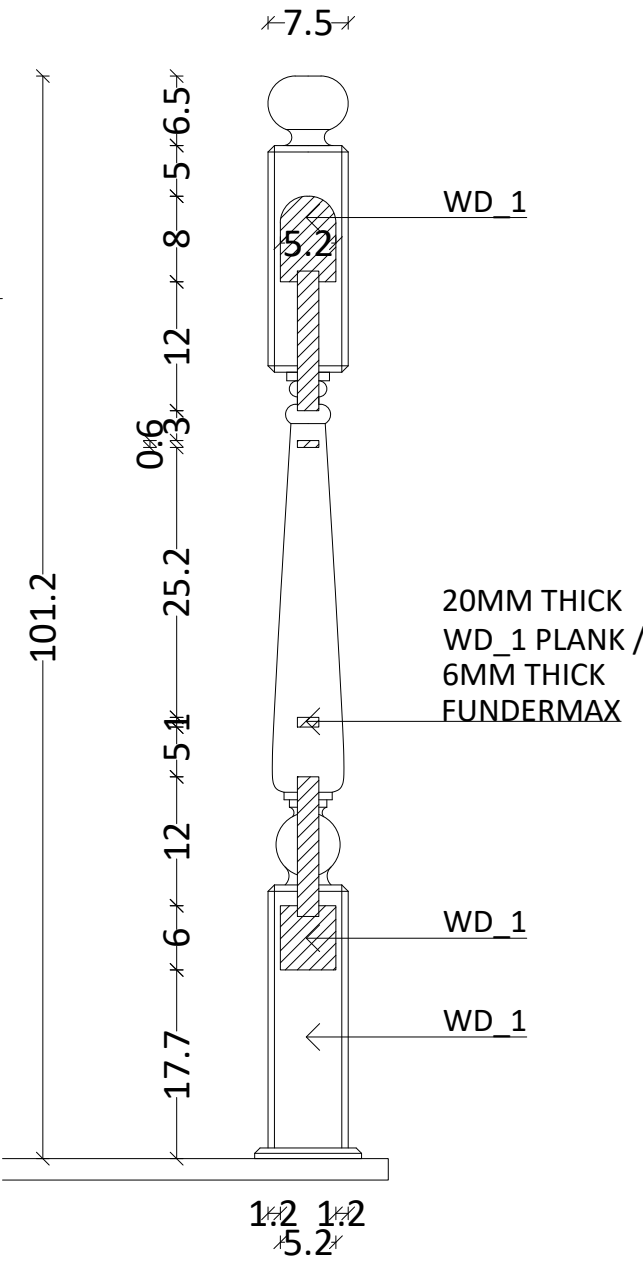





SECTION A



PROJECT:	FARM HOUSE @ TIRUNELVELI	DWG TITLE:	CUT-OUT AREA HANDRAIL DETAILS	DRAWN:	NA	REVISED DATE:		ALL DIMENSIONS ARE IN CMS No dimensions to be scaled off from the drawings only written dimensions to be. In the event of any discrepancy or difference between any interior drawings or site conditions or other wise immediate reference is to be made to the designer for clarification prior to execution of work at site
DWG NO:		DATE:	18/07/2024	CHECKED:		REVISION NO:		
REVISION:						SCALE:	1:50	

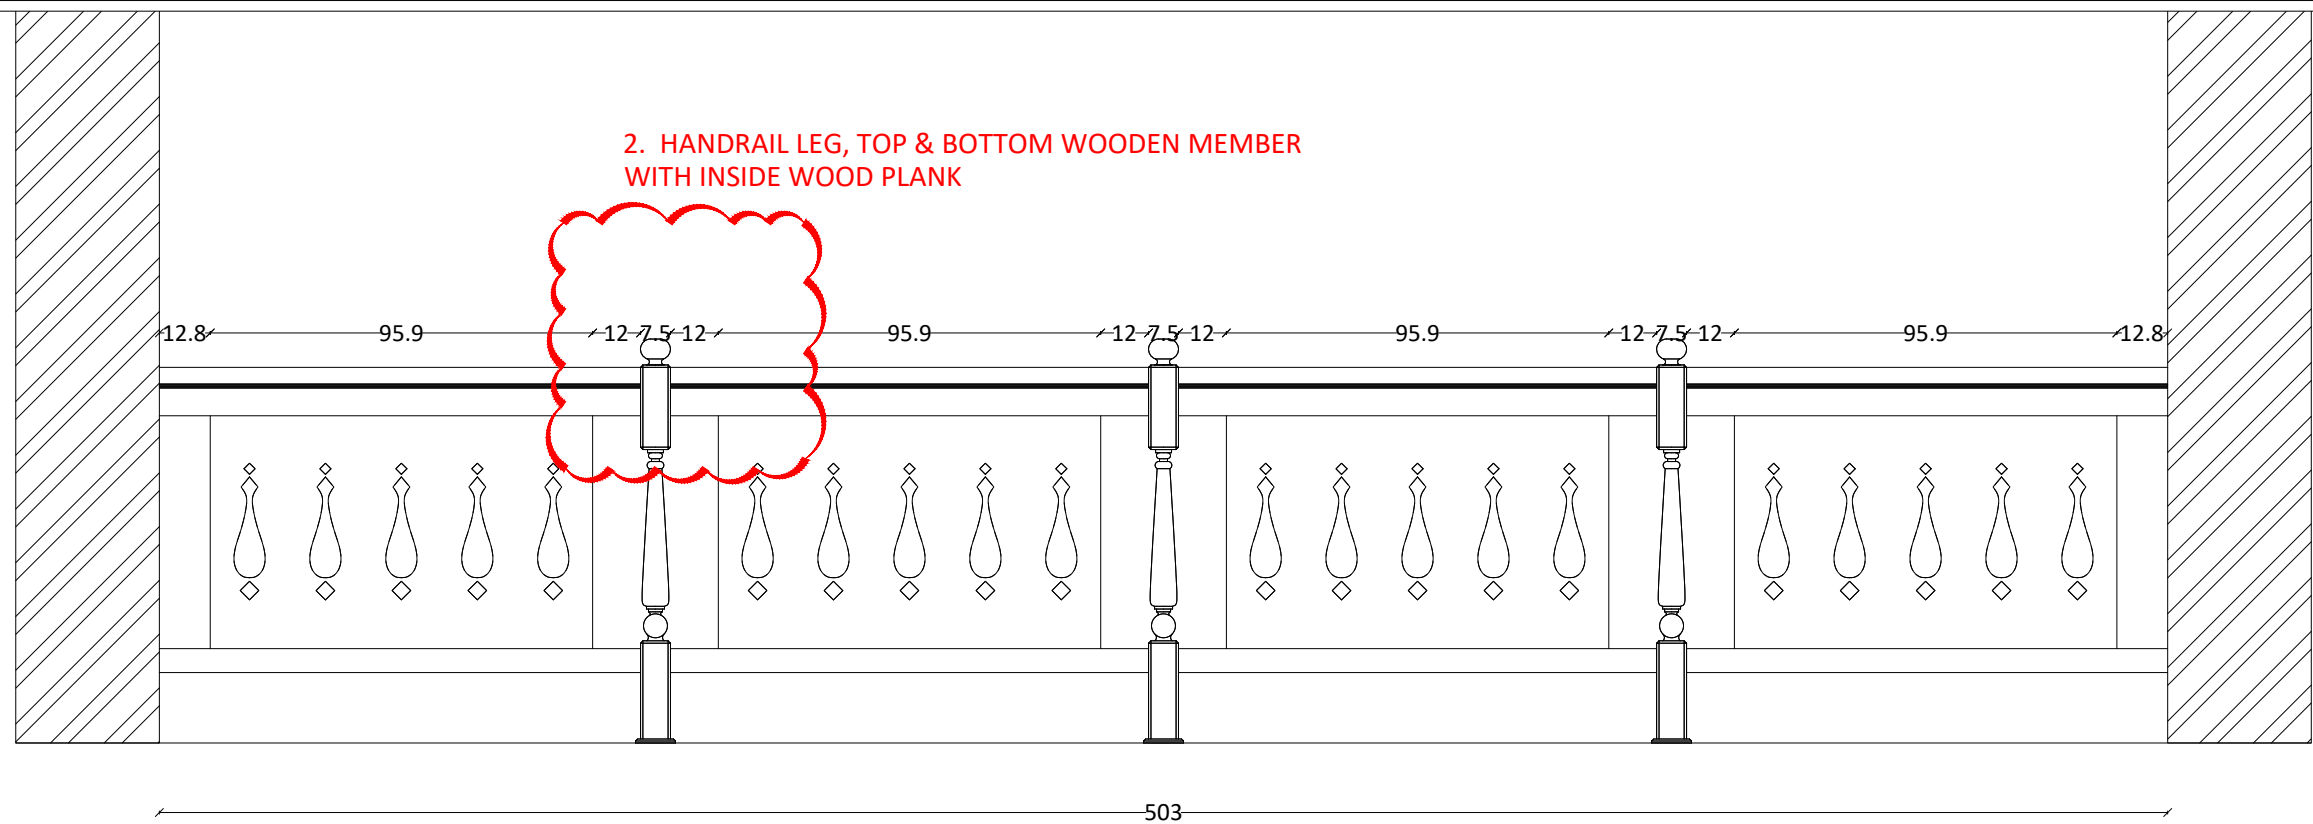


ELEVATION A

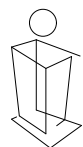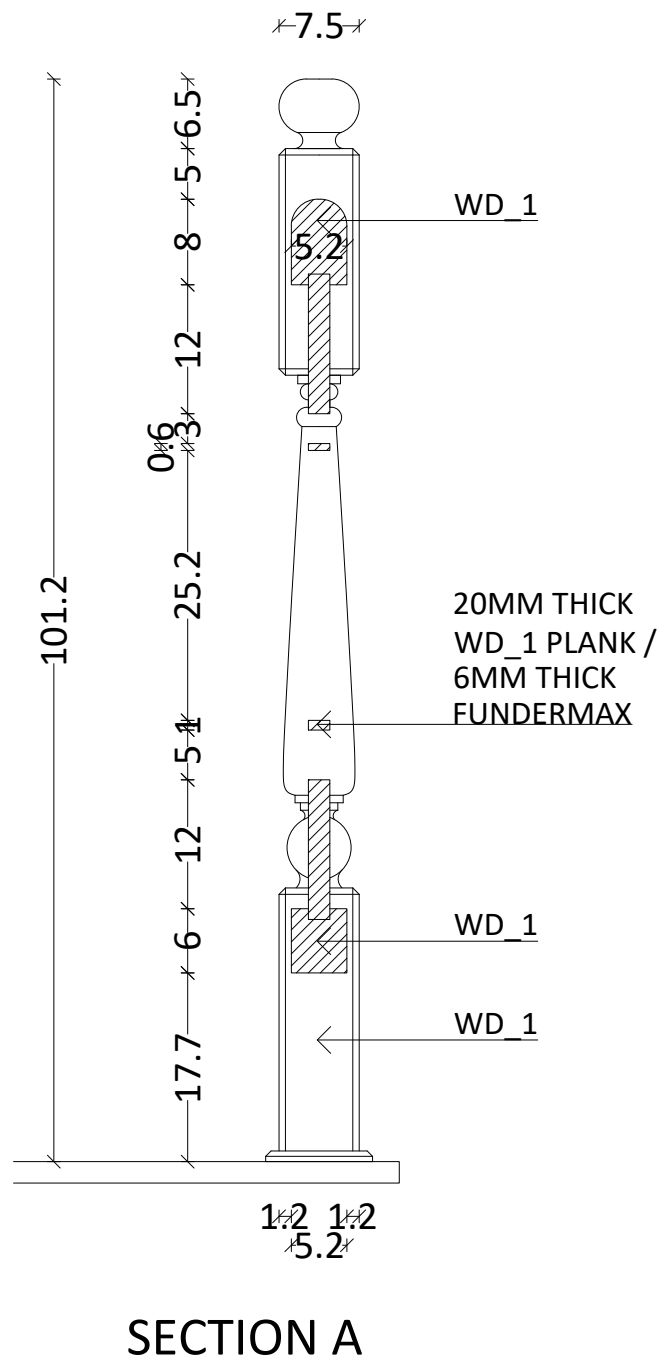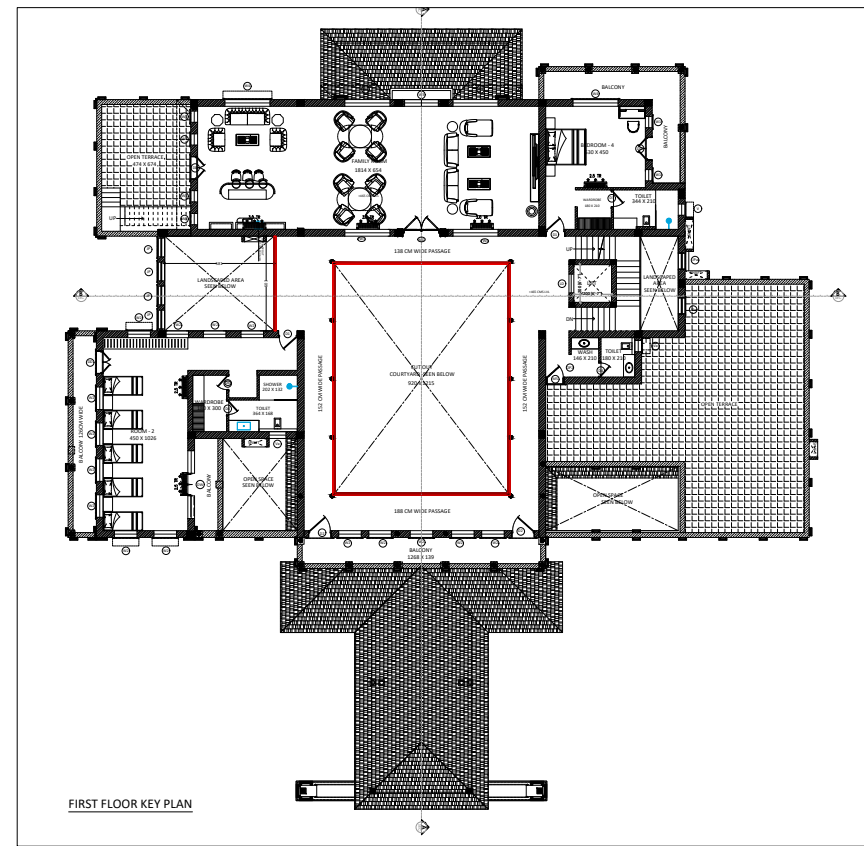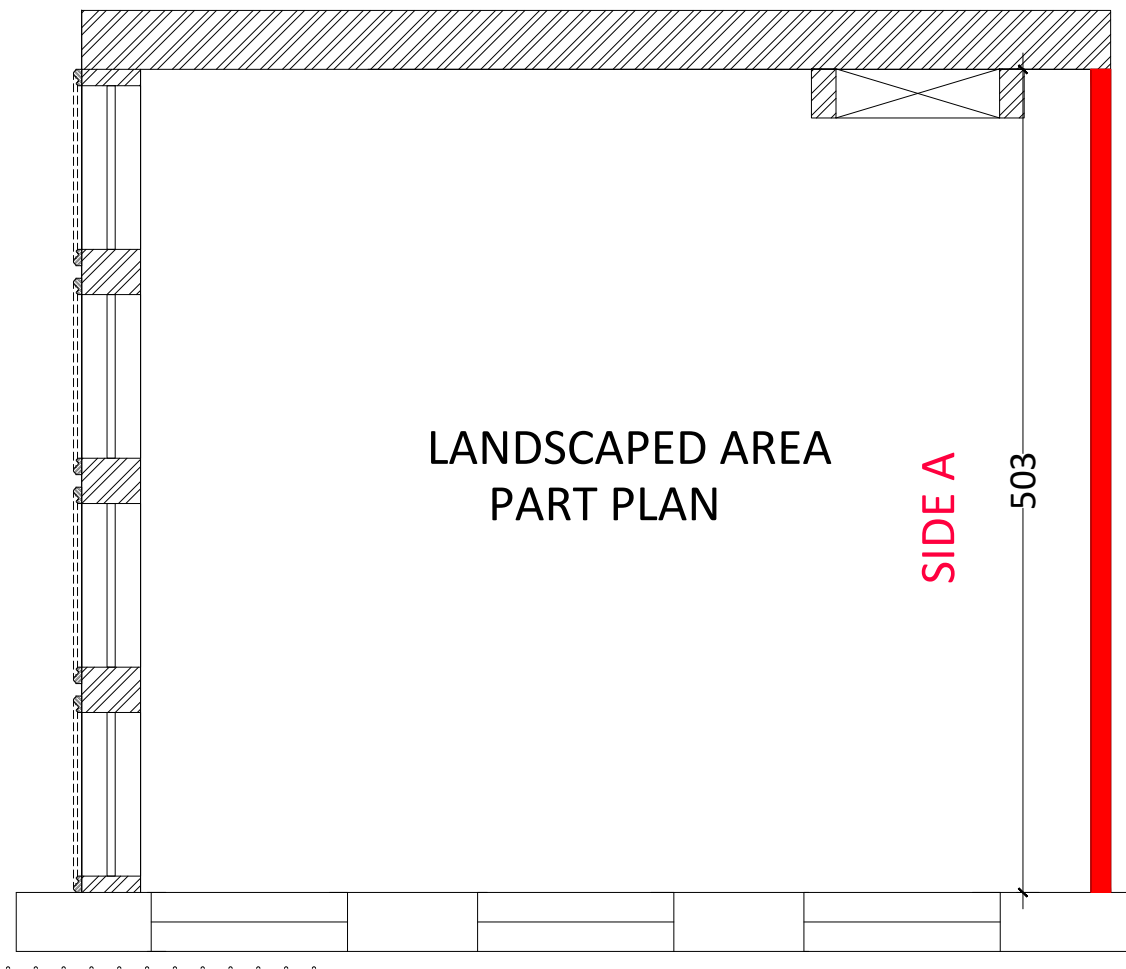


AHANAS


PROJECT: FARM HOUSE @ TIRUNELVELI	DWG TITLE: HANDRAIL DETAILS	DRAWN: NA	REVISED DATE:	ALL DIMENSIONS ARE IN CMS No dimensions to be scaled off from the drawings only written dimensions to be. In the event of any discrepancy or difference between any interior drawings or site conditions or other wise immediate reference is to be made to the designer for clarification prior to execution of work at site
DWG NO:	DATE: 18/07/2024	CHECKED:	REVISION NO:	
REVISION:			SCALE: 1:50	

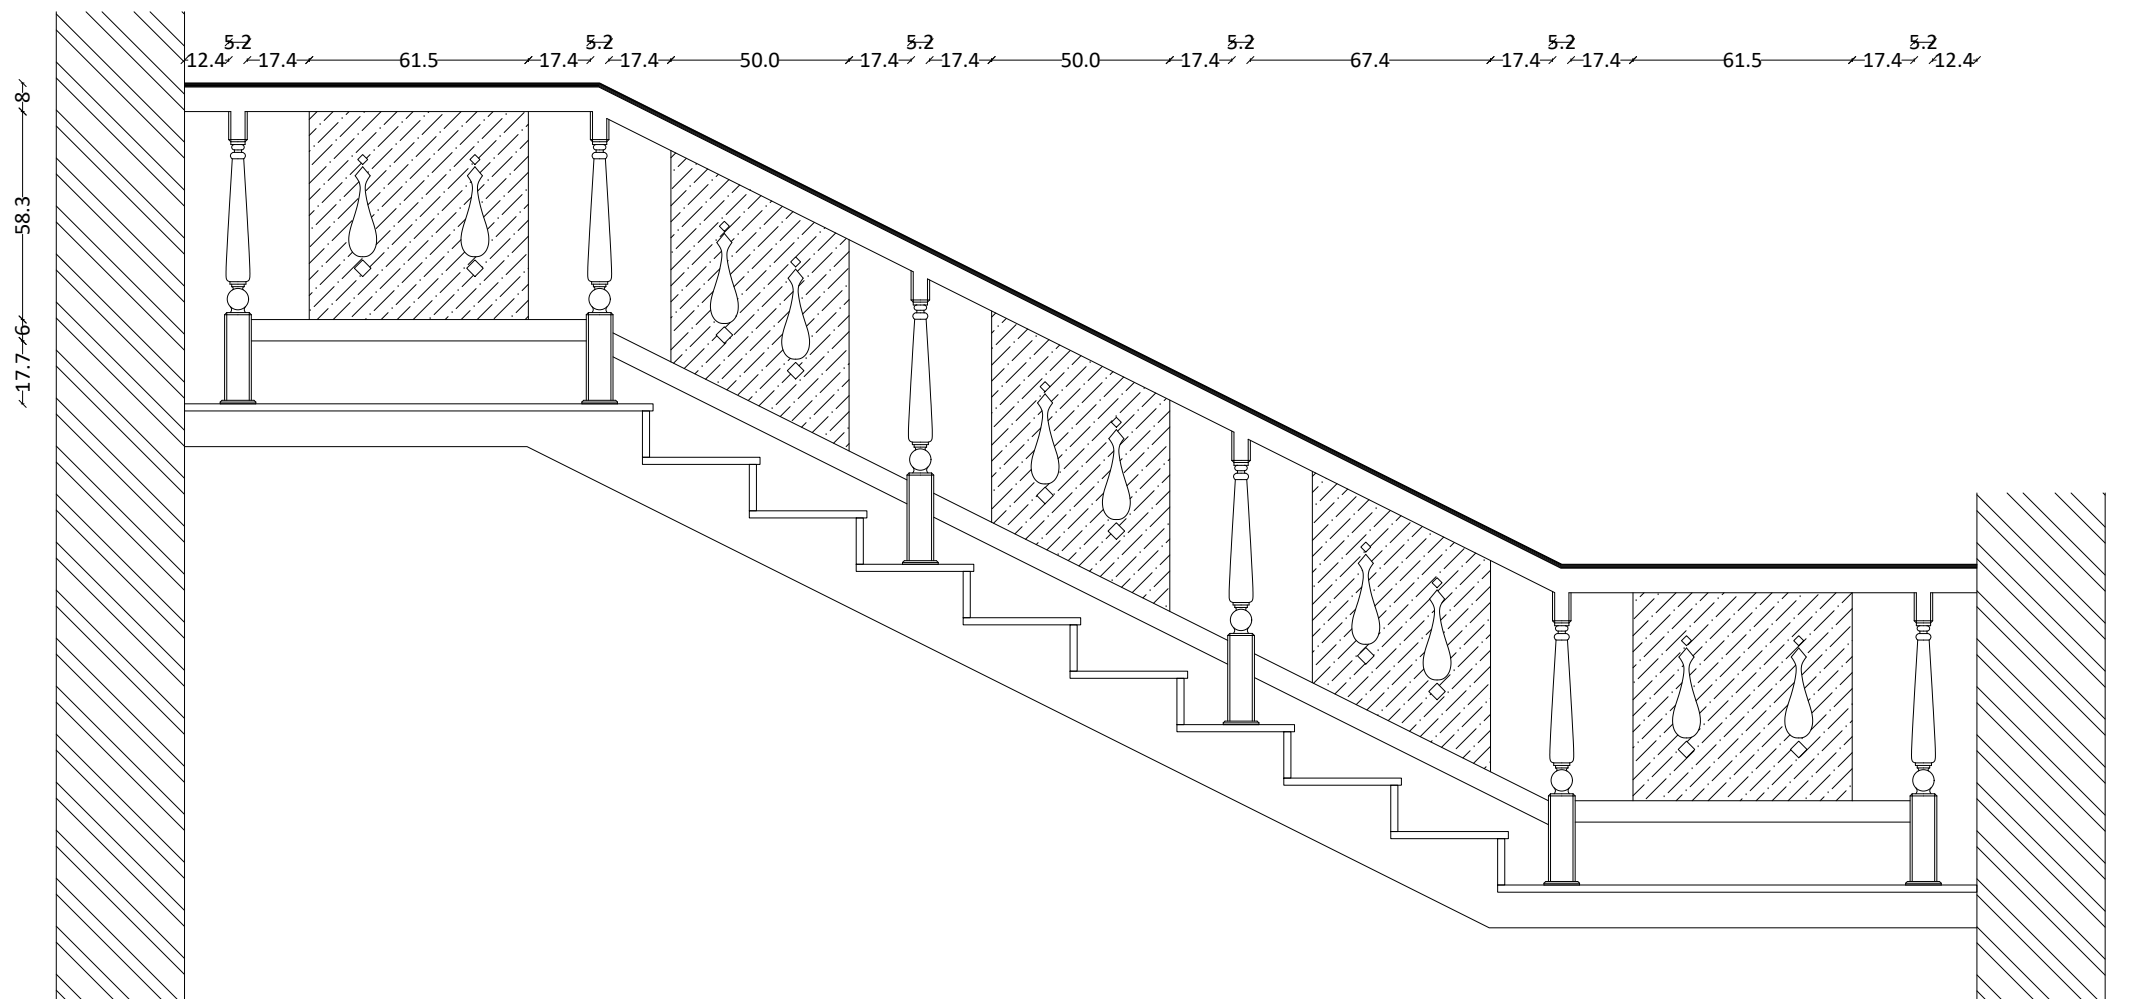

ELEVATION

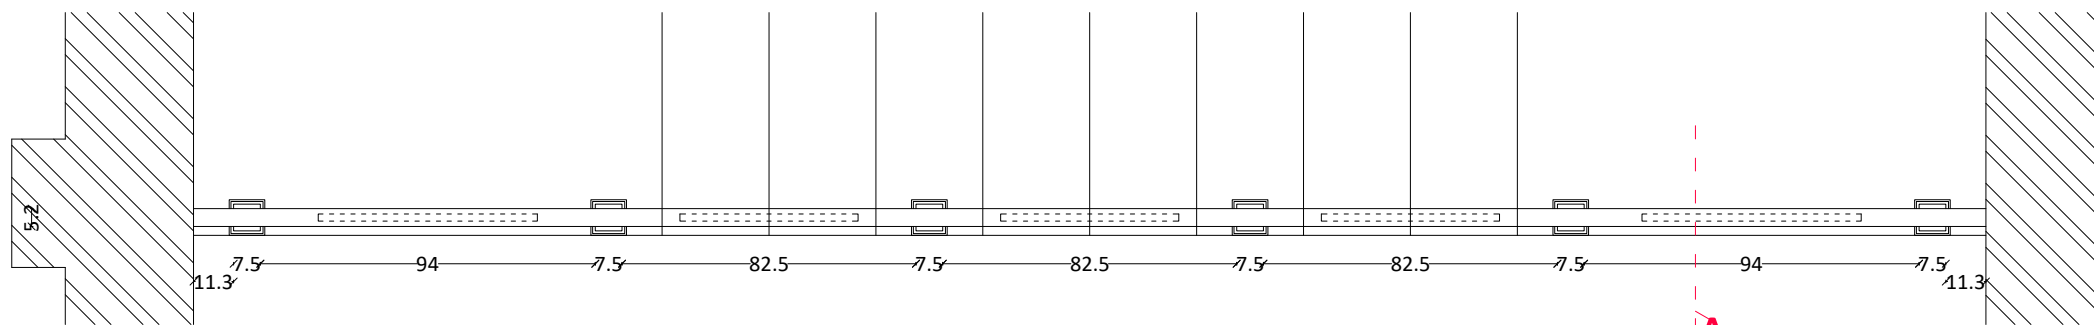

PLAN

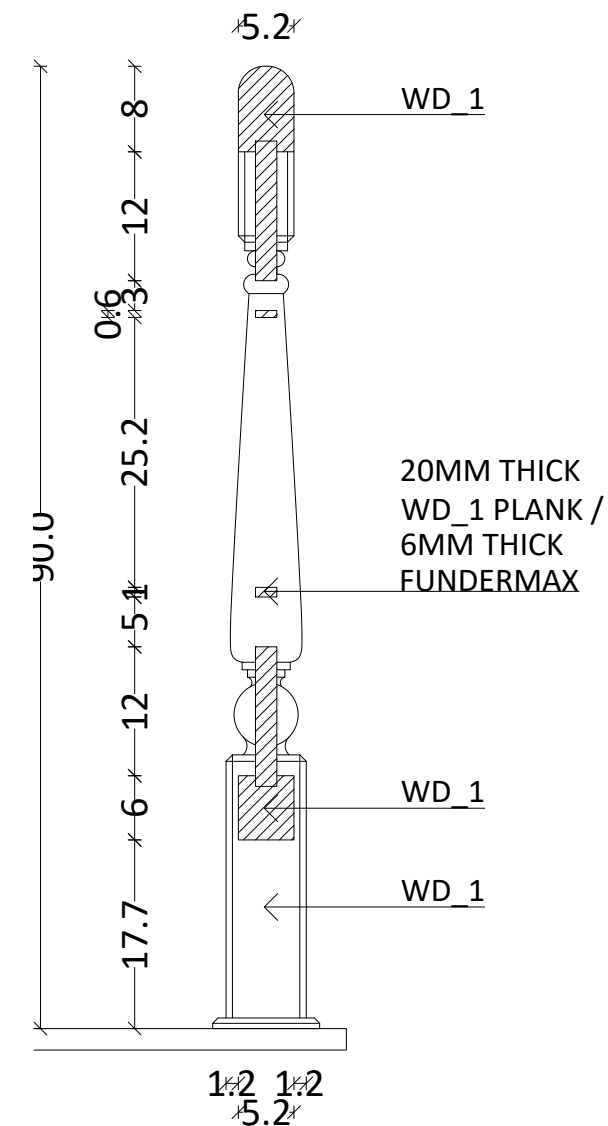


SECTION A



PROJECT: FARM HOUSE @ TIRUNELVELI	DWG TITLE: STAIR HANDRAIL DETAILS	DRAWN:	REVISED DATE:	ALL DIMENSIONS ARE IN CMS No dimensions to be scaled off from the drawings only written dimensions to be. In the event of any discrepancy or difference between any interior drawings or site conditions or other wise immediate reference is to be made to the designer for clarification prior to execution of work at site
DWG NO:	DATE: 18/07/2024	CHECKED:	REVISION NO:	
REVISION:			SCALE: 1:25	

LIST OF ACCESSORIES :	LIST OF APPLIANCES:	NOTE:
1. CUTLERY BASKET - 90 CM 2.WASTE BIN 3. DETERGENT HOLDER	a. HOB b. HOOD c. SINGLE BOWL SINK WITH DRAIN BOARD d. REFRIGERATOR e. DISHWASHER f. UNDER COUNTER WATER PURIFIER	1. DIMENSIONS OF THE APPLIANCES MAY VARY ACCORDING TO THE ITEMS FINALIZED BY THE CLIENT. LIST OF MATERIALS

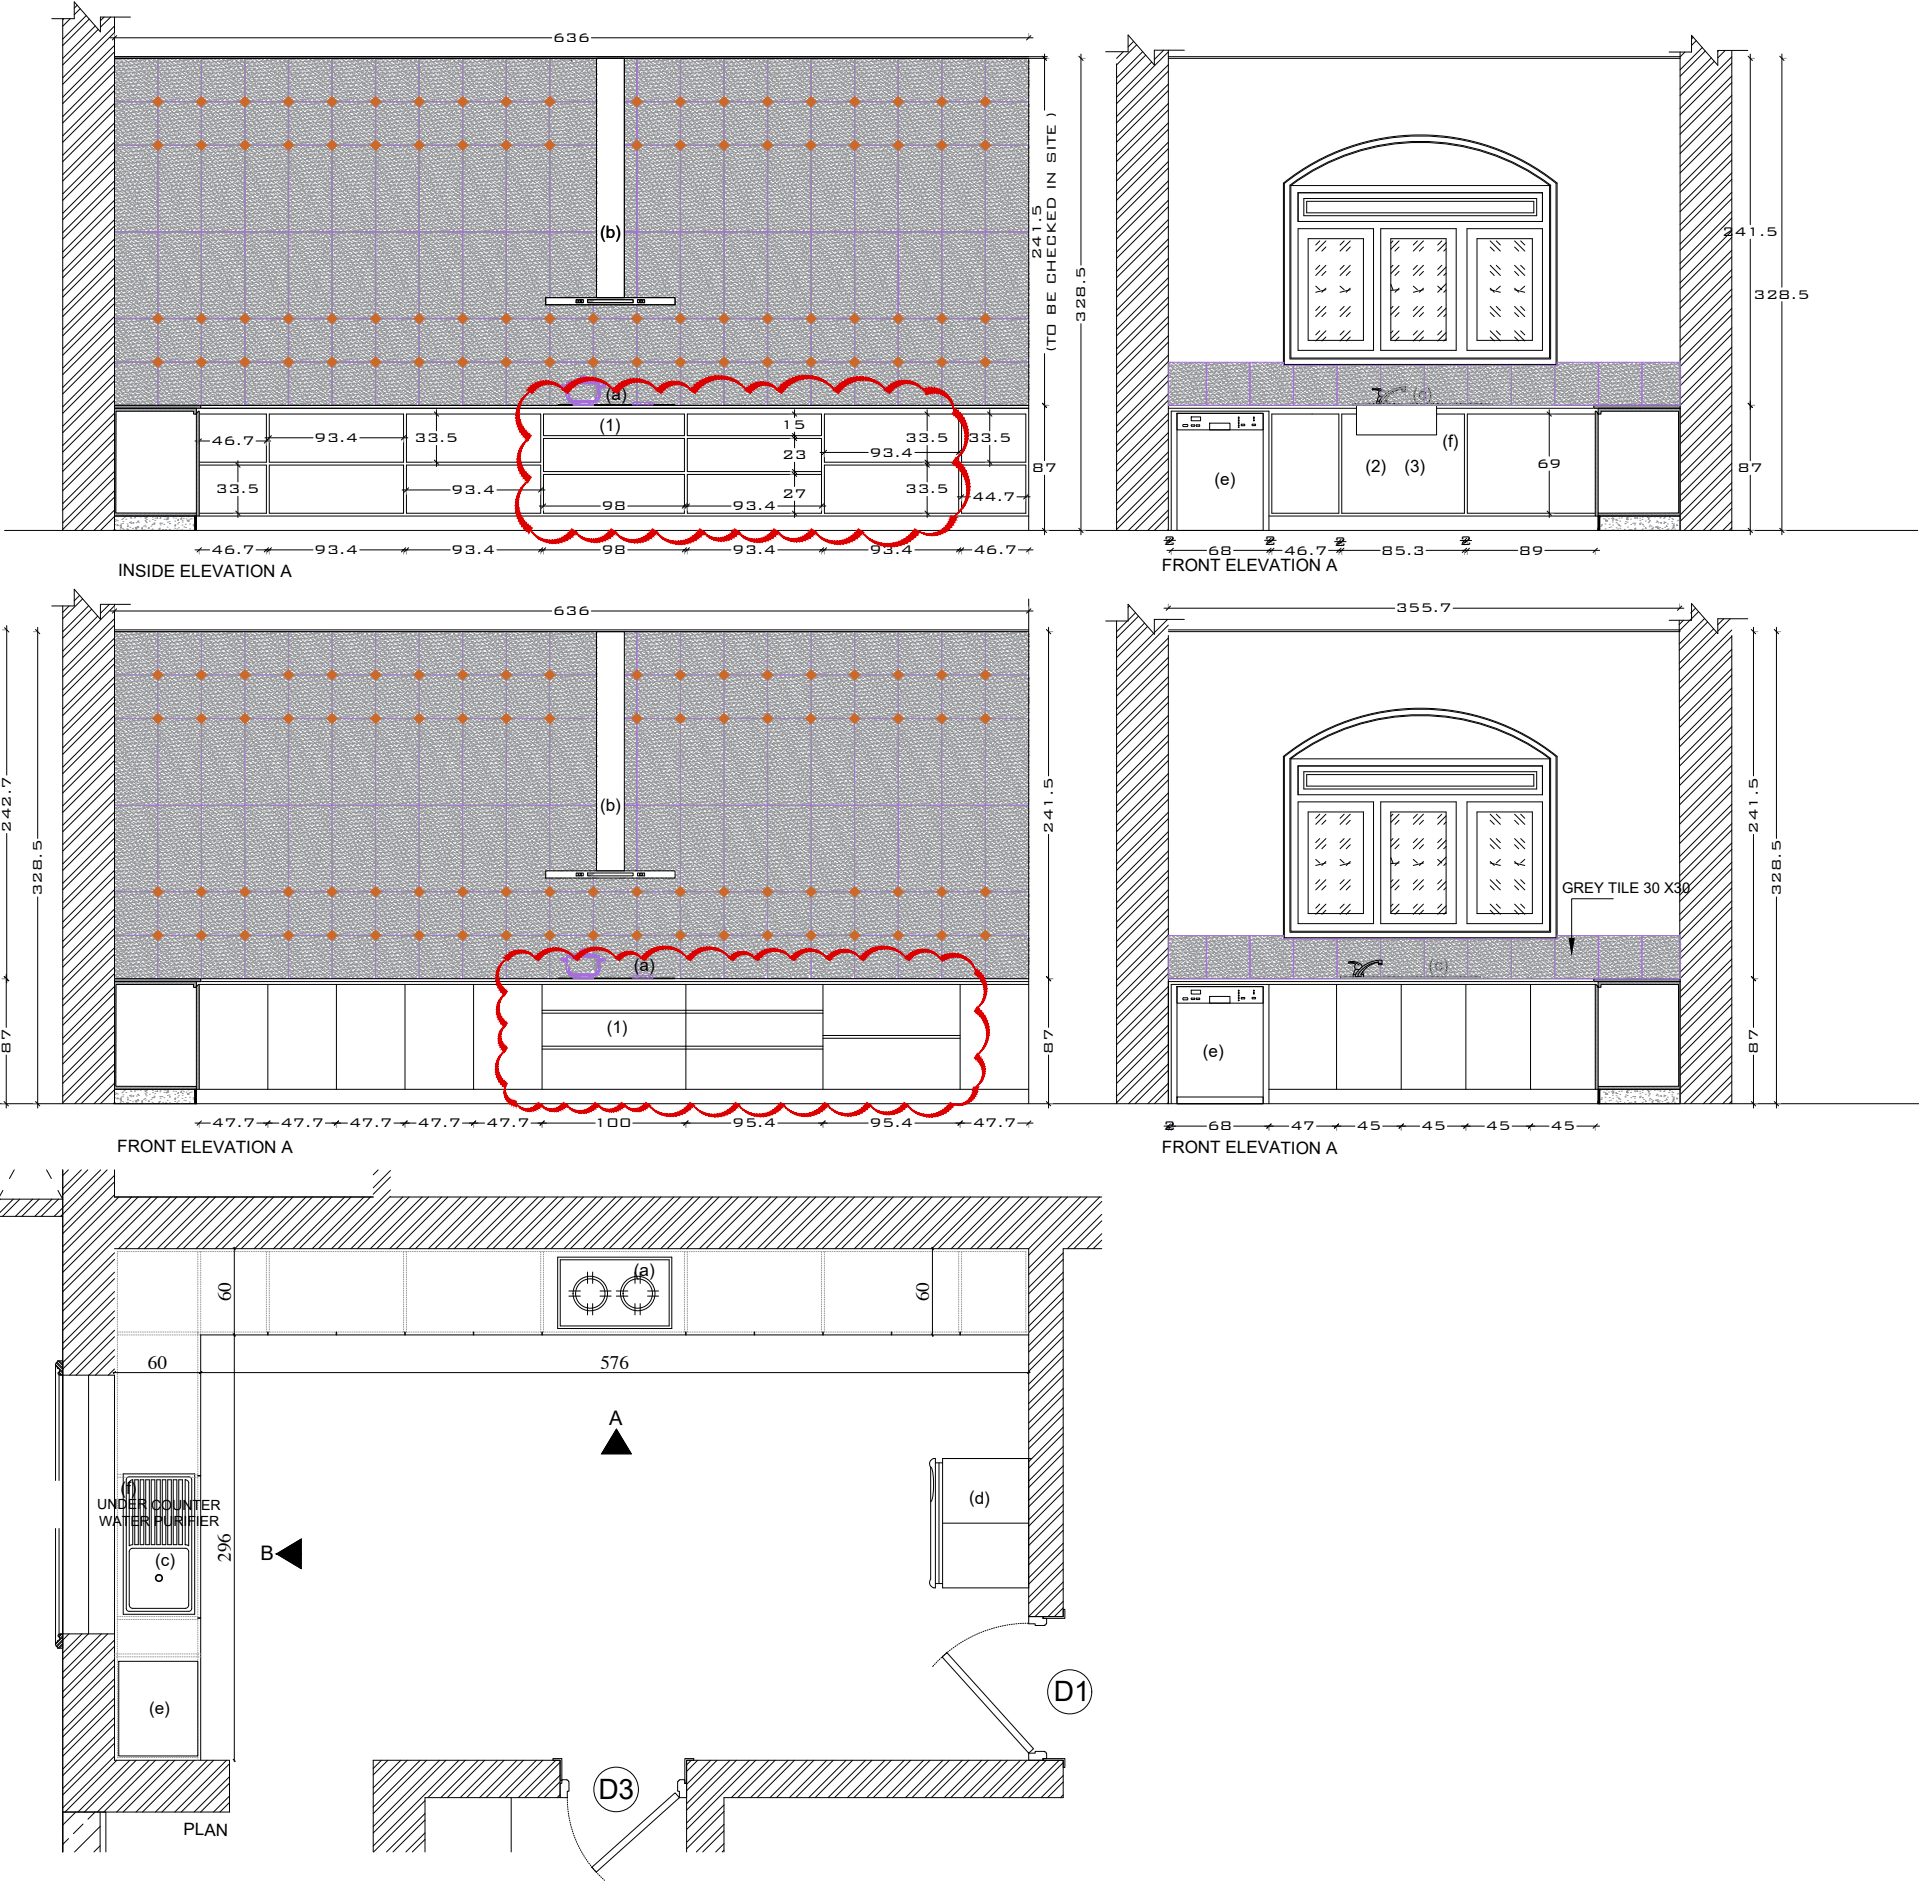

GENERAL NOTES: ○ ALL DIMENSIONS ARE IN MM,UNLESS OTHERWISE SPECIFIED. ○ DIMENSIONS SHALL NOT BE MEASURED DIRECTLY FROM- THIS DRAWINGS. FOLLOW ONLY WRITTEN DIMENSIONS. ○ IN THE EVENT OF ANY DISCREPANCY OR DIFFERENCE- BETWEEN ANY DRAWINGS OR SITE CONDITIONS /OTHERWISE IMMEDIATE REFERENCE IS TO BE MADE TO THE DESIGNER- FOR CLARIFICATION PRIOR TO EXECUTION OF WORK AT SITE. ○ ALL THE CIVIL/INTERIOR WORKS SHOULD BE IN LINE LEVEL AND PLUMB. ○ PLASTERING TO BE CUT AT SKIRTING LEVEL(AS PER SPECIFICATION).		ARCHITECTURAL/INTERIOR DESIGN CONSULTANT:  33/1622A, 'NAVAM' Haritha By-Lane Vennala P.O, Kochi 682 028 Email: ahanas@ahanas.com AHANAS DESIGN 4 SPaCE		KEY PLAN:		CARDINAL DIRECTION: 					
REVISION NOTES: 22/02/2025 BOTTOM CABINET REVISION		STRUCTURAL CONSULTANT: /MEP CONSULTANT:		PROJECT: FARMHOUSE AT TIRUNELVELI		DRAWN: AA		CHECKED: AP		REVISION: R1	
		CLIENT: MR. SHABAREESH		STATUS/ISSUED FOR: REFERENCE		PROJECT NO: 563		DRAWING NO: -			
				DRAWING TITLE: KITCHEN LAYOUT		SCALE: NTS		SHEET SIZE: A3		DATE: 22/02/2025	