

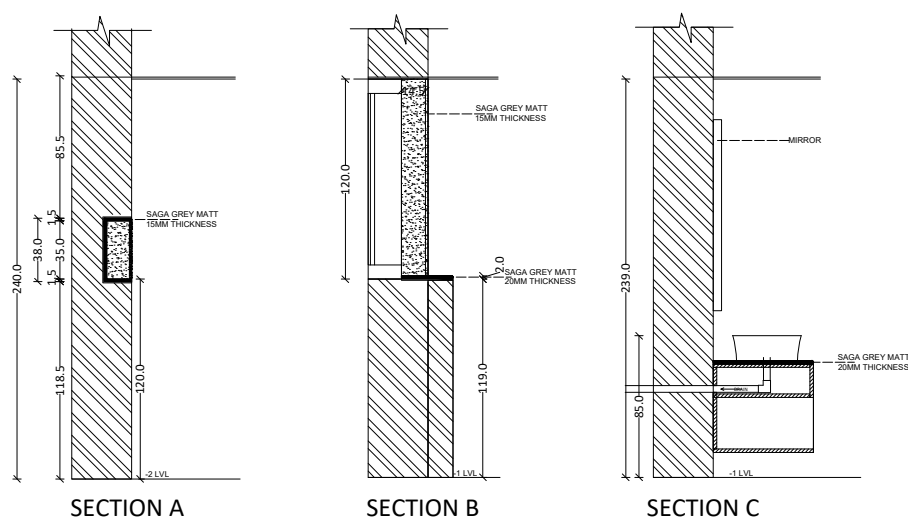
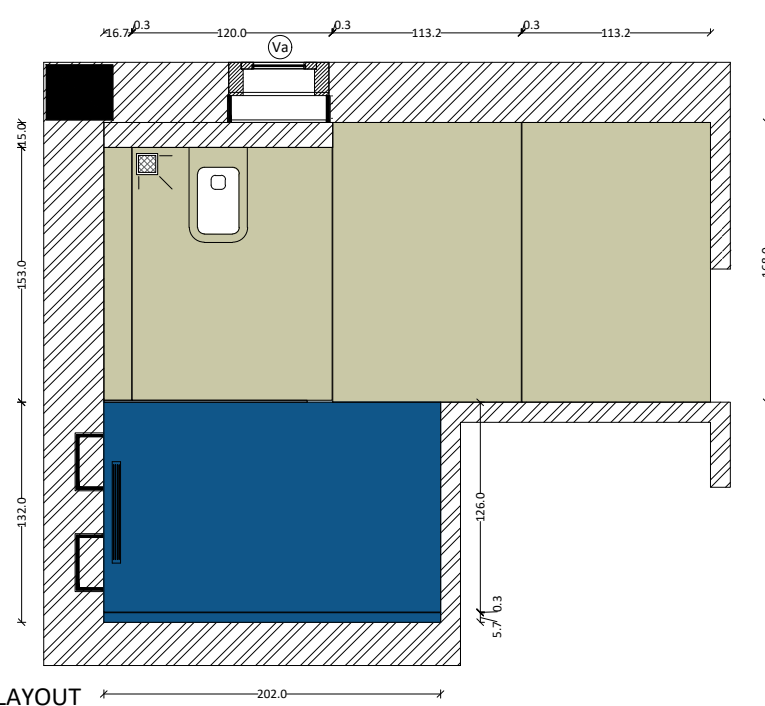
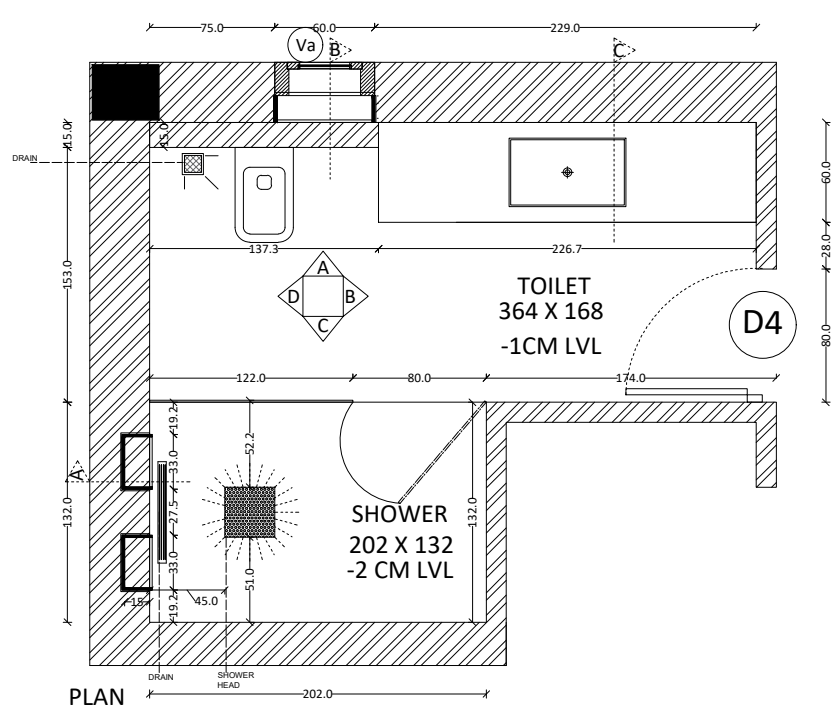
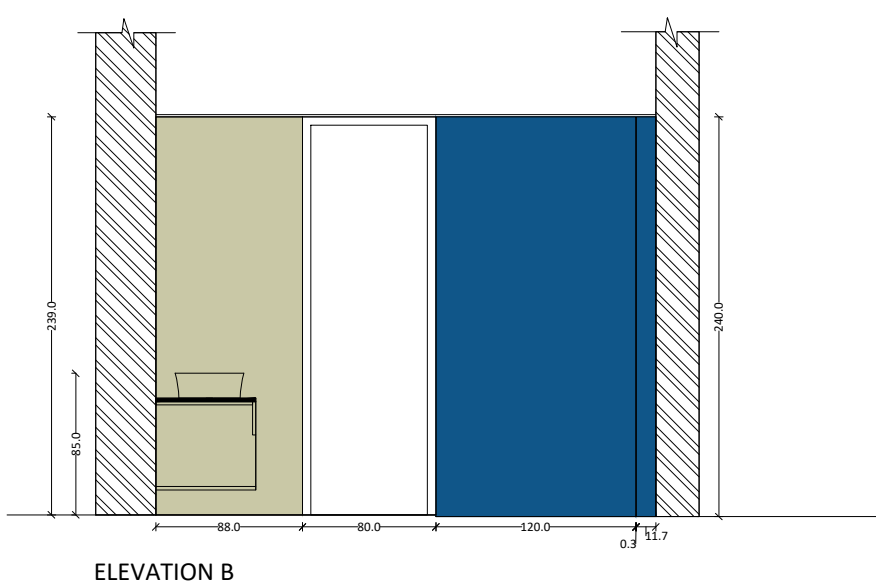
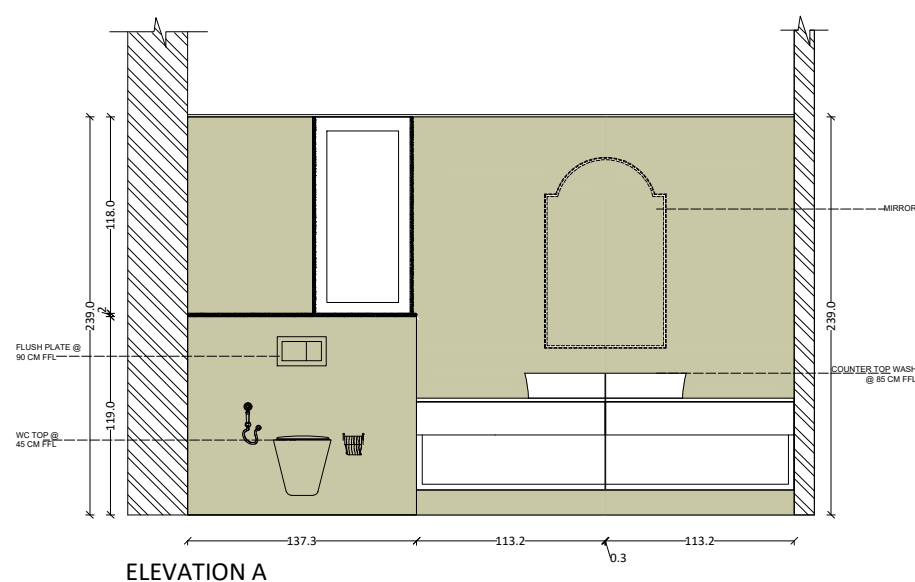


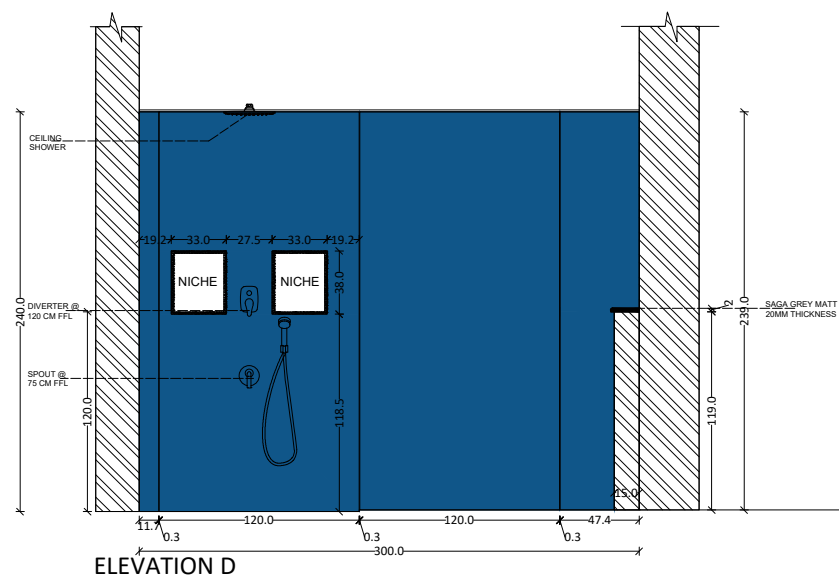

	WET AREA HIGHLIGHT - FND-16931 60CM x 60CM WITH 3MM SPACER
	DRY AREA WALLS - NEXION RUNA GRIGIO CHIRIO GREY 240 x 120 CM WITH 3MM SPACER
	WET AREA ALL WALLS & FLOOR DRY AREA FLOOR NEXION TERRAELINO GINEPRO (BLUE) NATURALE 240 x 120 CM WITH 3MM SPACER
	NICHE & TOP OF LEDGE WALL - SAGA GREY POLISH 300x80 CM 15MM THICKNESS

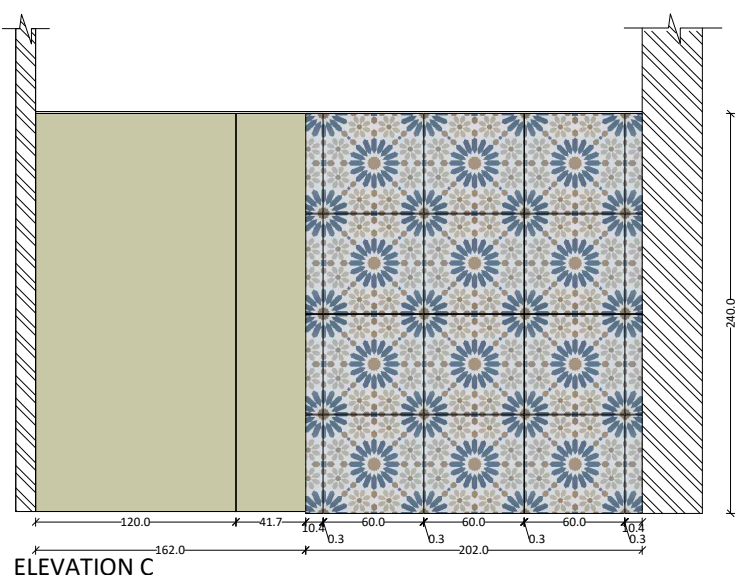

PROJECT: FARM HOUSE @ TIRUNELVELI	DWG TITLE: GROUND FLOOR DORM TOILET DETAILS	DATE: 23.05.2024	REVISED DATE: 28.06.2024	ALL DIMENSIONS ARE IN CMS No dimensions to be scaled off from the drawings only written dimensions to be. In the event of any discrepancy or difference between any interior drawings or site conditions or other wise immediate reference is to be made to the designer for clarification prior to execution of work at site
	DRAWN: AA	CHECKED:	REVISION NO:	
REVISION:			SCALE: NTS	