

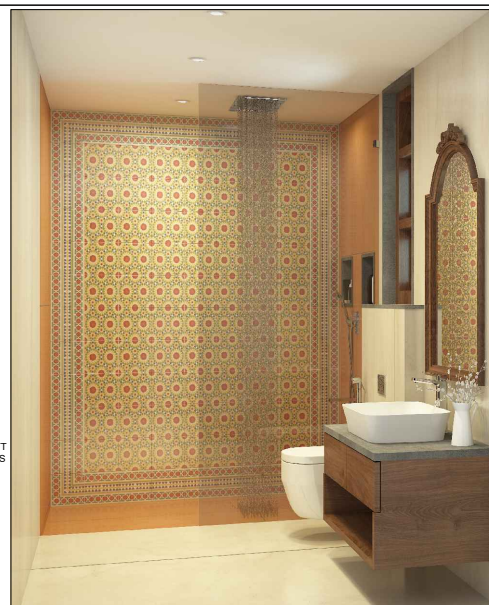
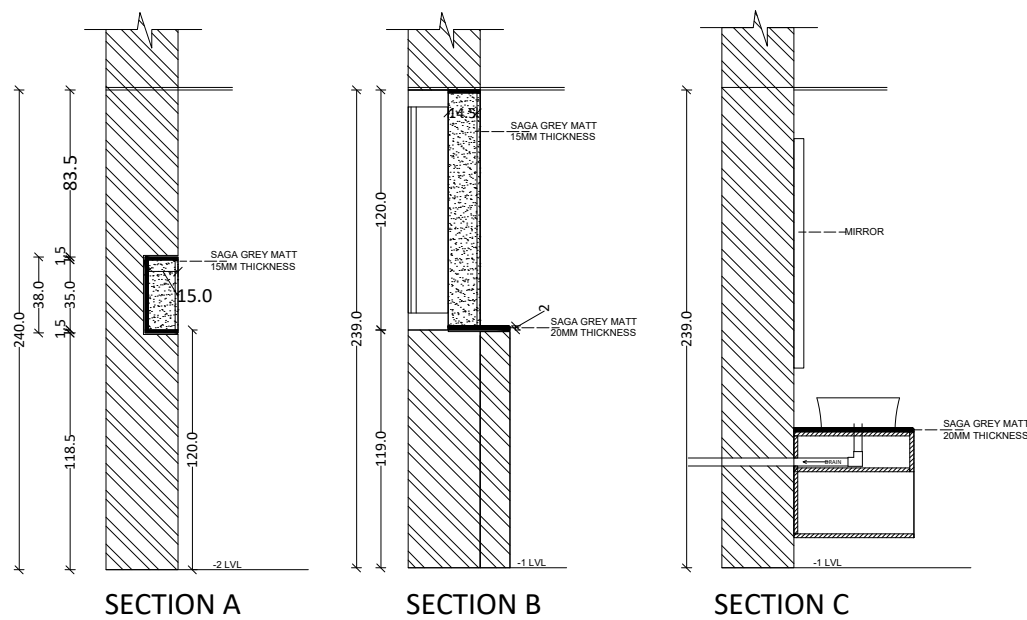
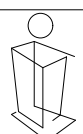
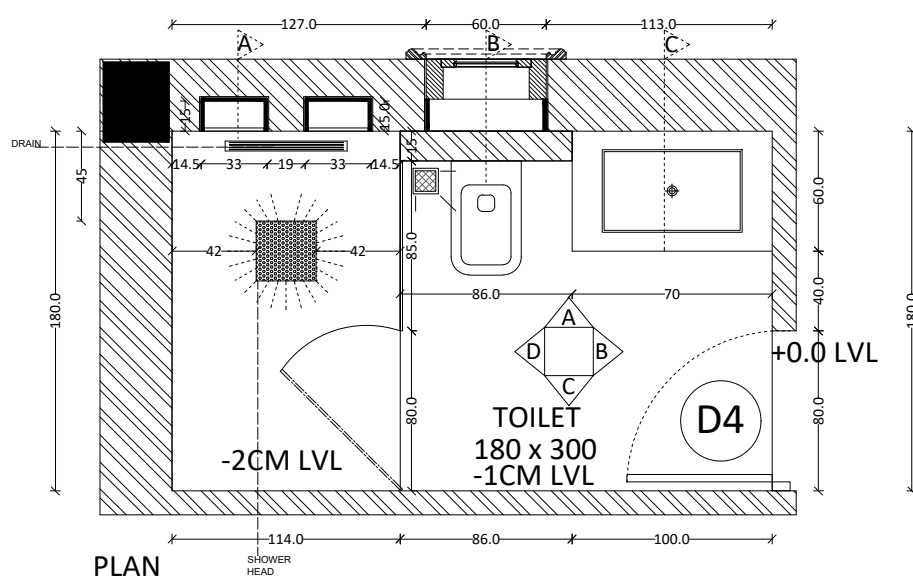
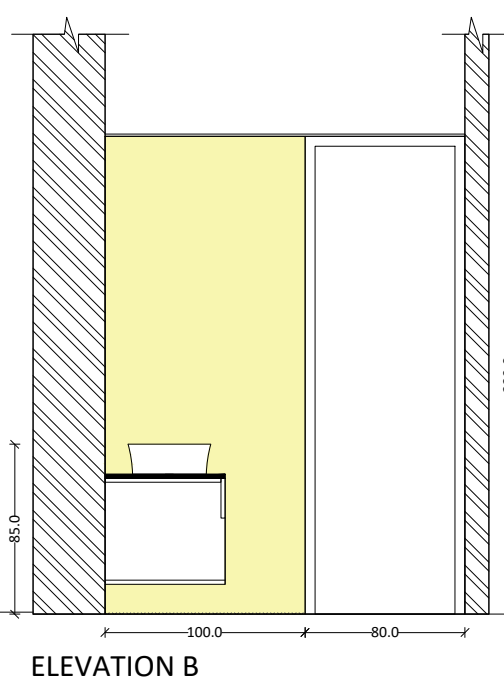
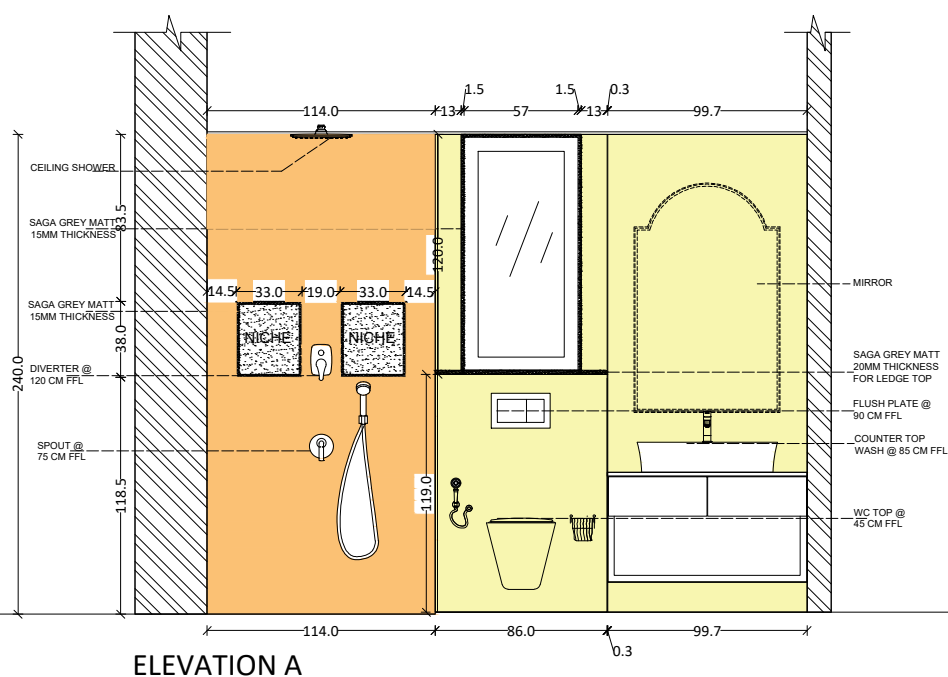


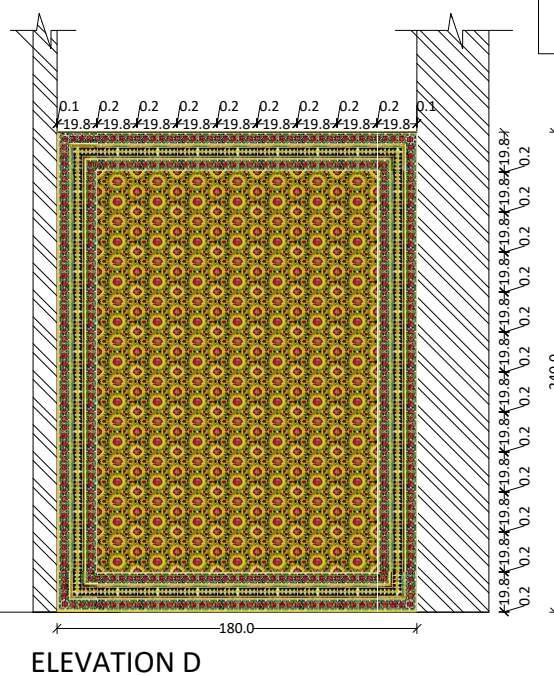

	WET AREA FLOOR & WALL - SIMPOLO SPECTRA CHILLI 240x120 CM WITH 3MM SPACER
	DRY AREA FLOOR & WALL (WC & WASH)- NEXION CREMA EUROPA 240 x 120 CM WITH 3MM SPACER
	NICHE & TOP OF LEDGE WALL - SAGA GREY POLISH 300x80 CM 15MM & 20MM THICKNESS
	HIGHLIGHT WALL WET AREA - FOLKSTAR CORNER 19.8CM x 19.8CM WITH 2MM SPACER
	HIGHLIGHT WALL WET AREA - FOLKSTAR BORDER 19.8CMx19.8CM WITH 2MM SPACER
	HIGHLIGHT WALL WET AREA - FOLKSTAR BASE 19.8CM x 19.8CM WITH 2MM SPACER

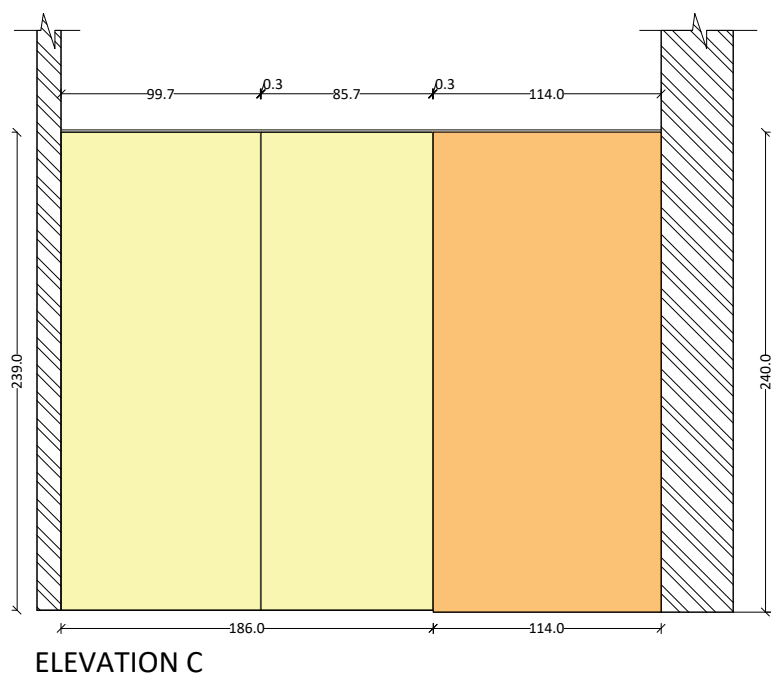

A'HANAS

PROJECT: FARM HOUSE @ TIRUNELVELI

REVISION:

DWG TITLE:BED1 TOILET DETAILS
(NEAR KITCHEN)

DRAWN: AA

DATE: 23.05.2024


CHECKED:

REVISÉD DATE: 28 06 2024

REVISION NO:

SCALE: NTS


ALL DIMENSIONS ARE IN CMS
No dimensions to be scaled off from the drawings only
written dimensions to be.
In the event of any discrepancy or difference between any
interior drawings or site conditions or other wise
immediate reference is to be made to the designer for
clarification prior to execution of work at site

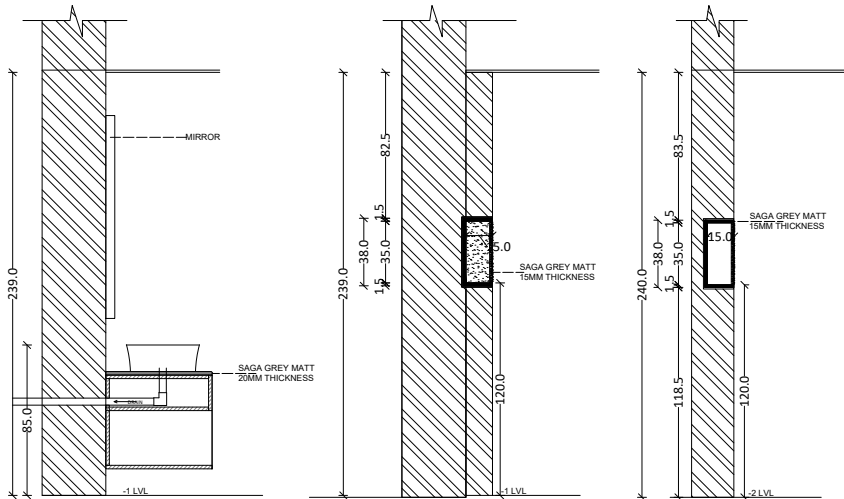


SECTION A

SECTION B

SECTION C

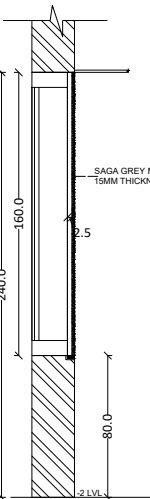


SECTION D

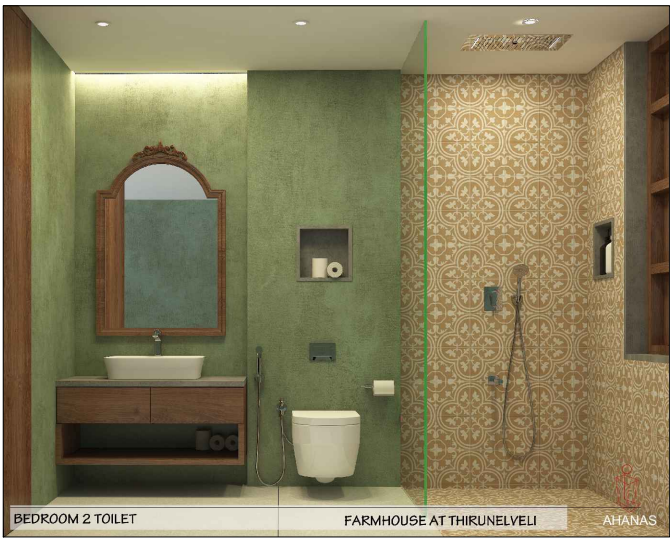


BEDROOM 2 TOILET

FARMHOUSE AT THIRUNELVELI

AHANAS

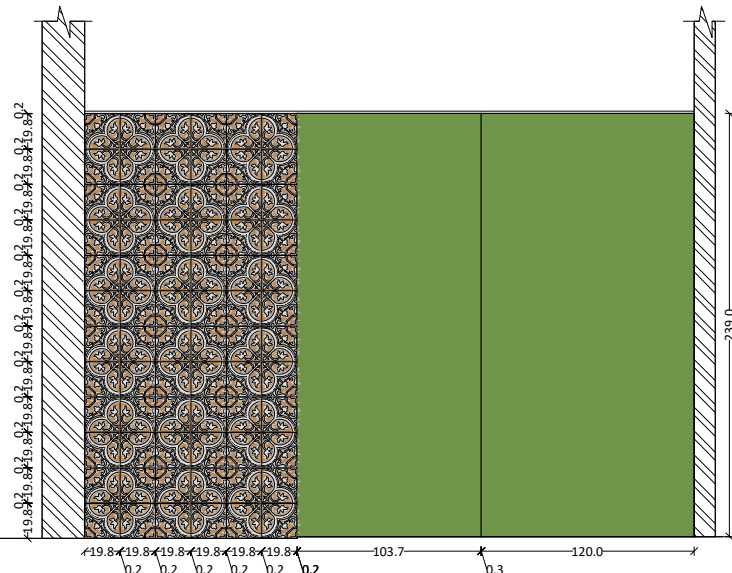


ELEVATION C

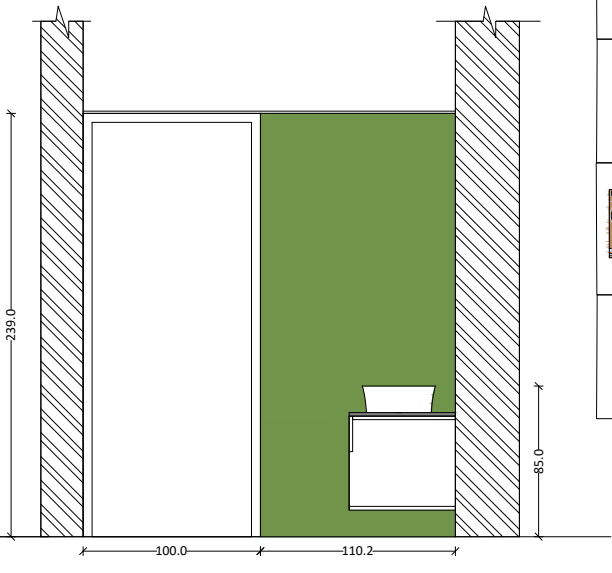


ELEVATION D


	DRY AREA WALL (WC & WASH) - NEXION MENTA TERRALINO 240 x 120 CM WITH 2MM SPACER
	NICHE & TOP OF LEDGE WALL - SERA GREY POLISH 300x80 CM 15MM THICKNESS
	WET AREA / FLOOR & WALL - NEO BEIGE DECOR -2 19.8 x 19.8 CM WITH 2MM SPACER
	DRY AREA FLOOR - SIMPOLO SPECTRA CHEESE 240 x 120 CM WITH 3MM SPACER

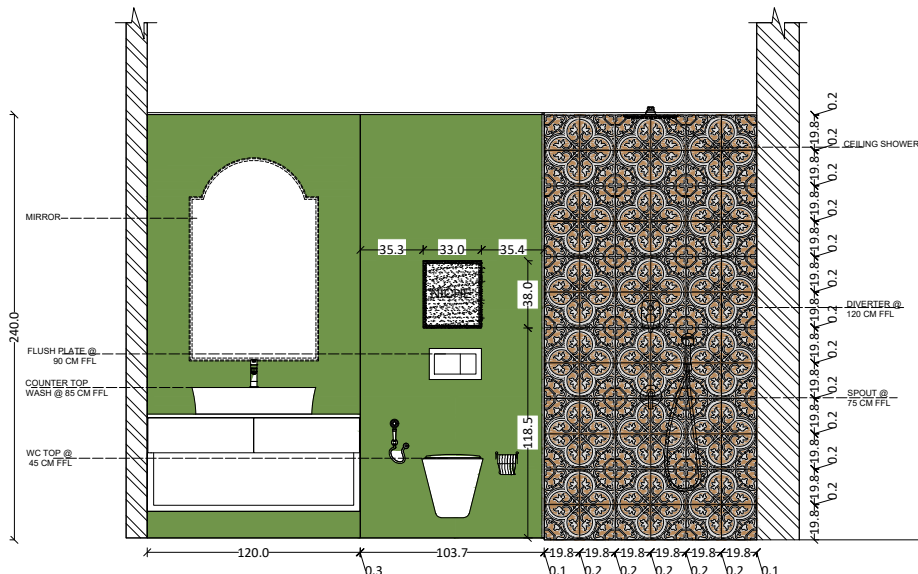


ELEVATION A

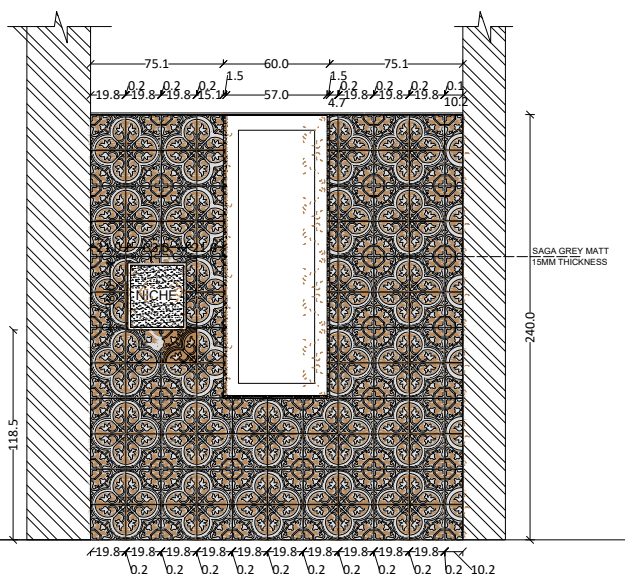

ELEVATION B

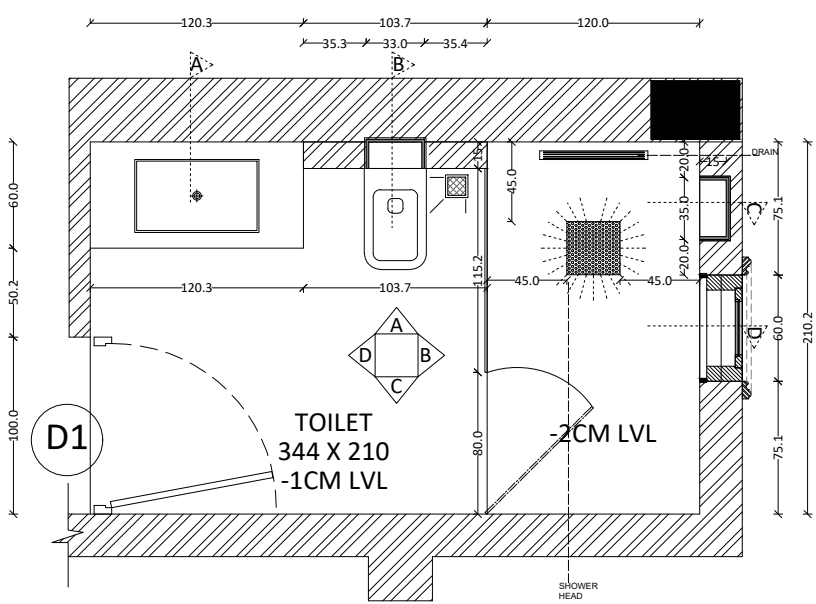

PLAN

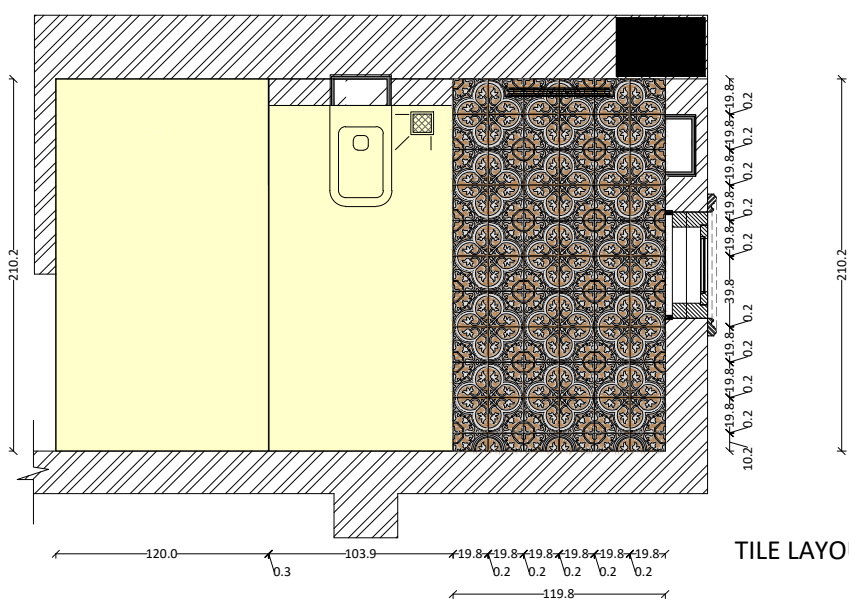

TILE LAYOUT



PROJECT:
FARM HOUSE @ TIRUNELVELI

REVISION:

DWG TITLE:BEDROOM 2 TOILET
DETAILS (NEAR POOJA)

DRAWN: AA

DATE: 23.05.2024


CHECKED:

REVISED DATE: 28.06.2024




REVISION NO:

SCALE: NTS

ALL DIMENSIONS ARE IN CMS
No dimensions to be scaled off from the drawings only
written dimensions to be.
In the event of any discrepancy or difference between any
interior drawings or site conditions or other wise
immediate reference is to be made to the designer for
clarification prior to execution of work at site

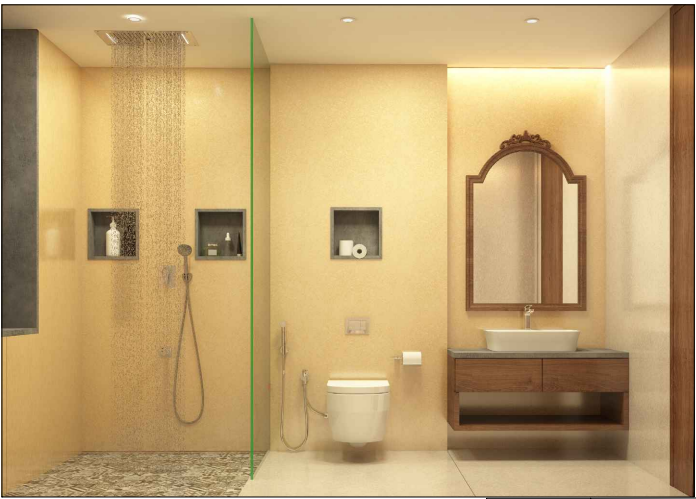


	DRY AREA WALL (WC & WASH) ALL WALLS OF WET AREA - SIMPOLO SPECTRA MUSTARD 240 x 120 CM WITH 2MM SPACER
	NICHE & TOP OF LEDGE WALL - SERA GREY POLISH 300x80 CM 15MM & 20MM THICKNESS
	WET AREA FLOOR - FND ACHIRA - 16270 60 x 60 CM
	DRY AREA FLOOR AND BALANCE WALLS - SIMPOLO SPECTRA CHEESE 240 x 120 CM WITH 3MM SPACER

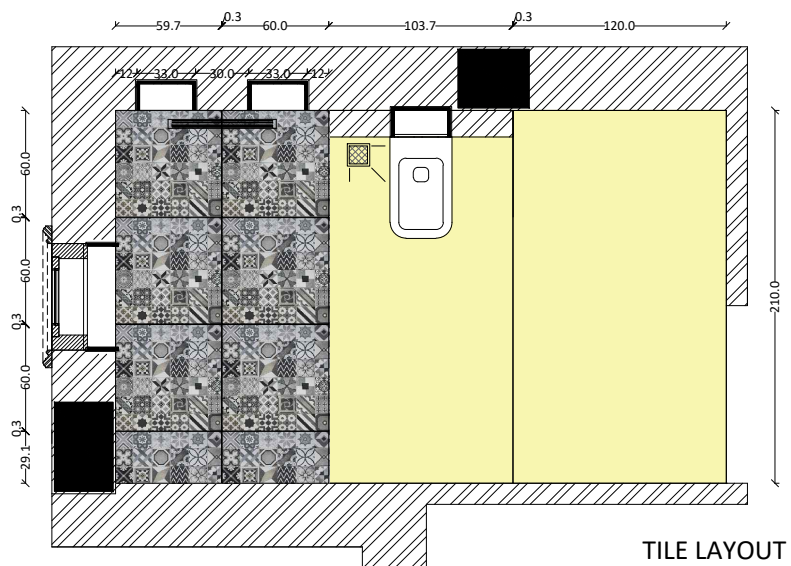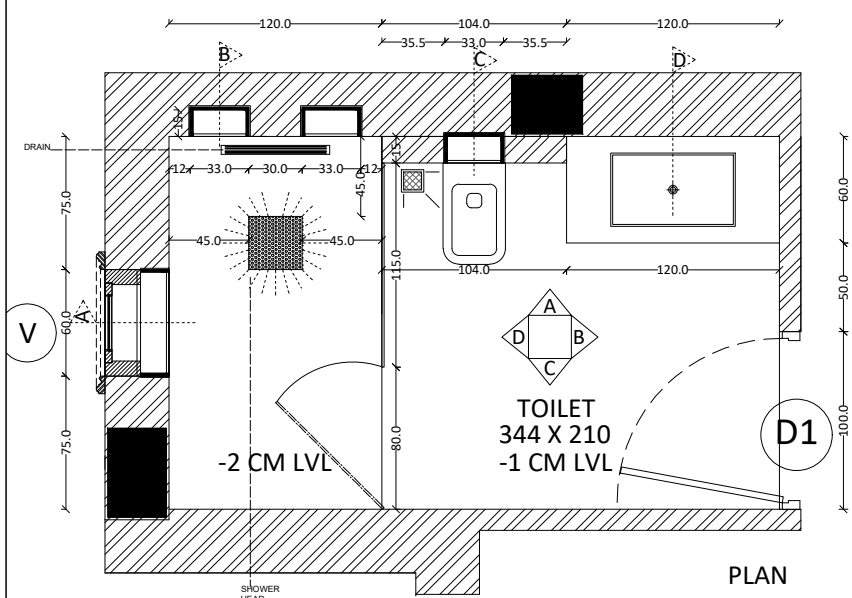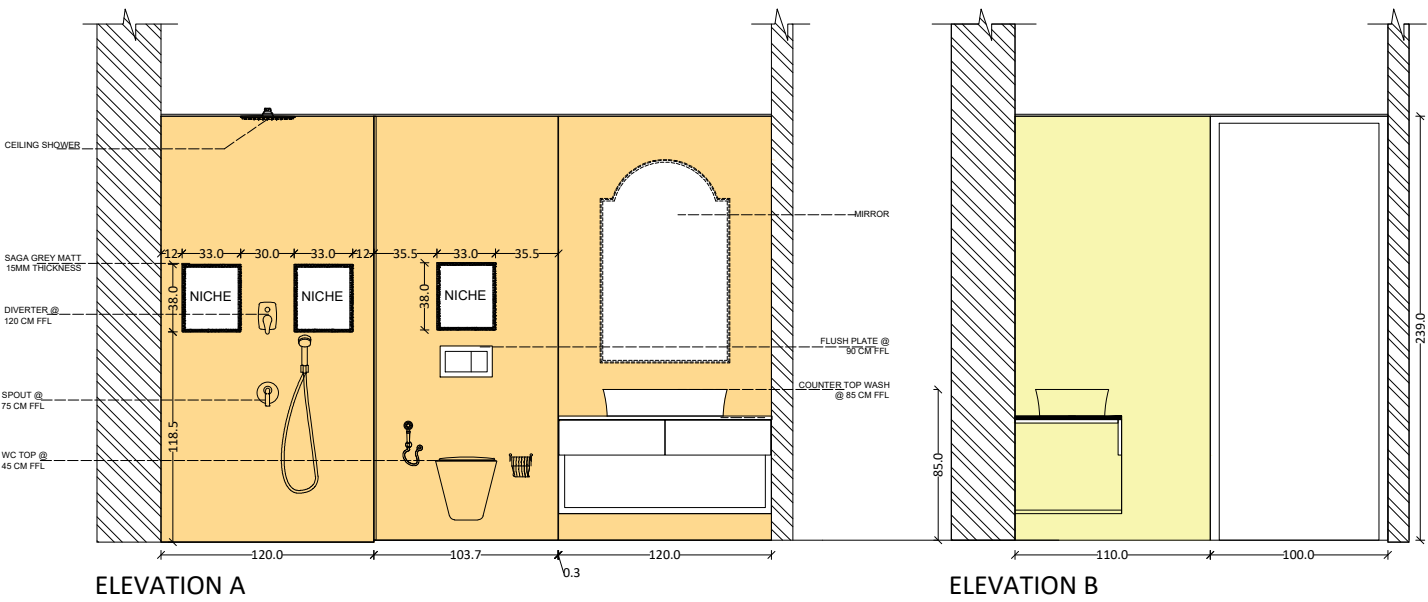

ALL DIMENSIONS ARE IN CMS
No dimensions to be scaled off from the drawings only
written dimensions to be.
In the event of any discrepancy or difference between any
interior drawings or site conditions or other wise
immediate reference is to be made to the designer for
clarification prior to execution of work at site

SCALE: NTS


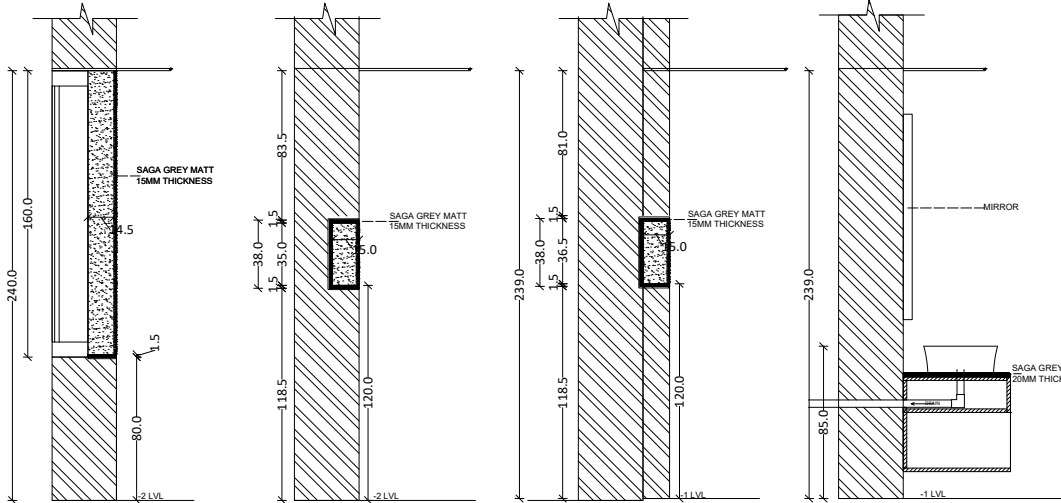


SECTION A


SECTION B

SECTION C

SECTION D

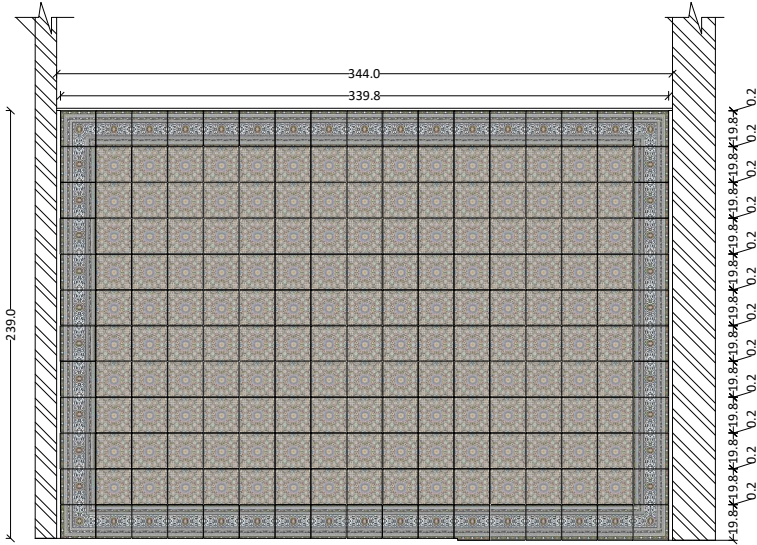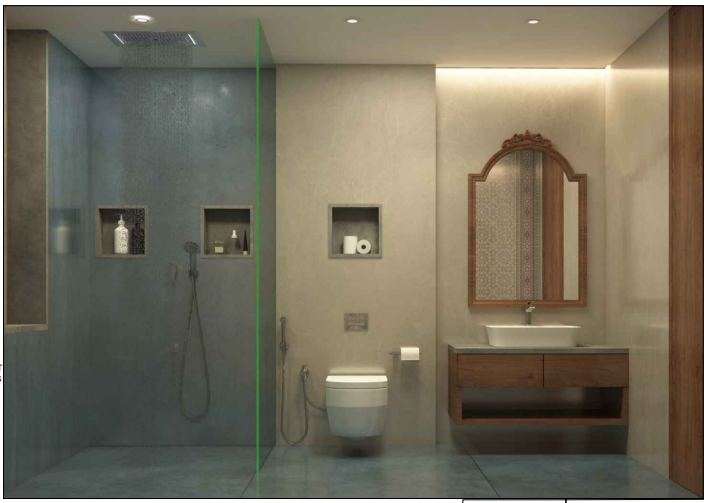


ELEVATION C

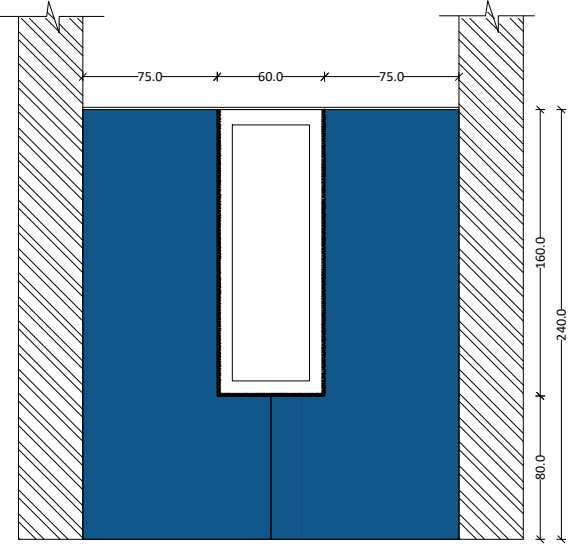


ELEVATION D


	DRY AREA WALLS NEXION RUNA GRIGIO CHIRIO GREY 240 x 120 CM
	WET AREA ALL WALLS & FLOOR DRY AREA FLOOR NEXION TERRAELINO GINEPRO (BLUE) NATURALE 240 x 120 CM
	NICHE & TOP OF LEDGE WALL SERA GREY POLISH 300x80 CM 15MM THICKNESS
	HIGHLIGHT WALL WET AREA FOLK ORIGIN CORNER 19.8CMx19.8CM
	HIGHLIGHT WALL WET AREA FOLK ORIGIN BORDER 19.8CMx19.8CM
	HIGHLIGHT WALL WET AREA FOLK ORIGIN BASE 19.8CMx19.8CM

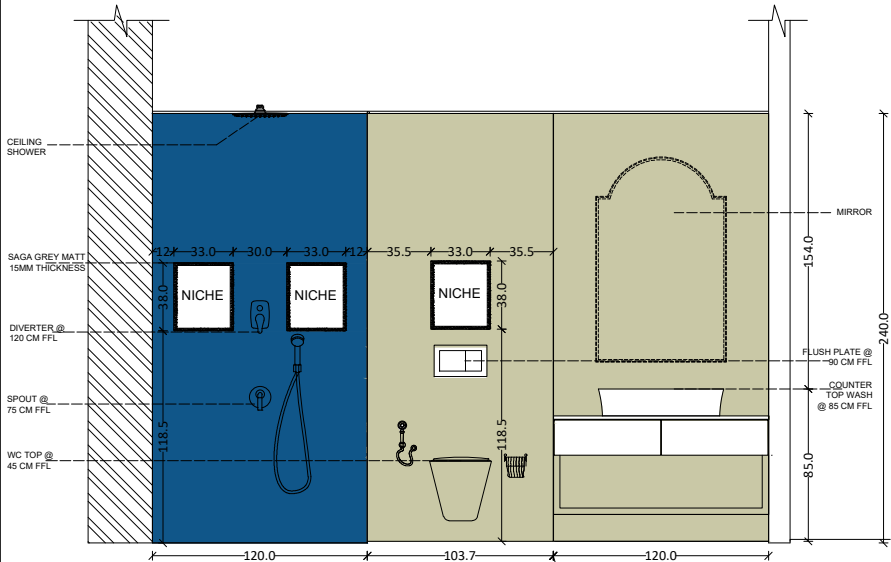


ELEVATION A

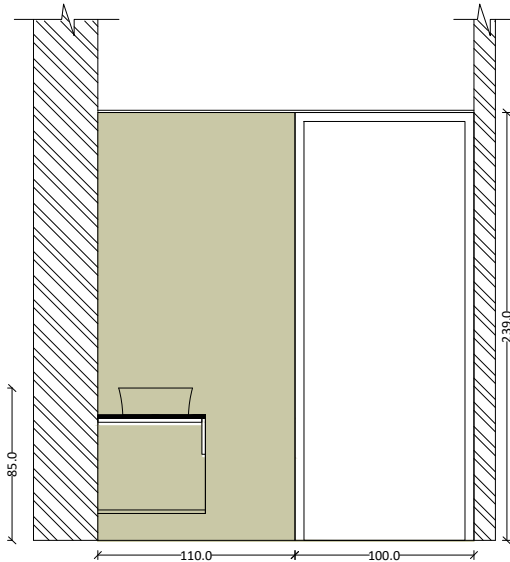


ELEVATION B

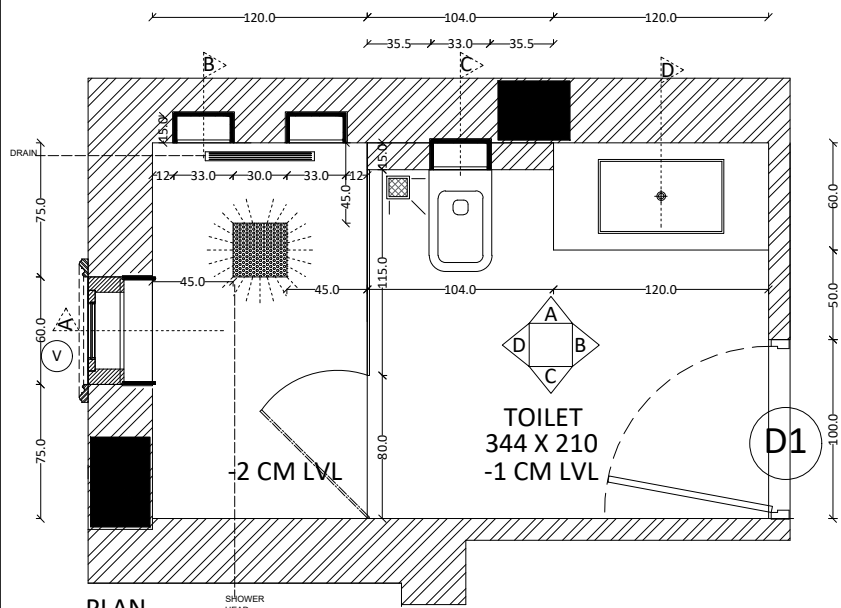

PLAN

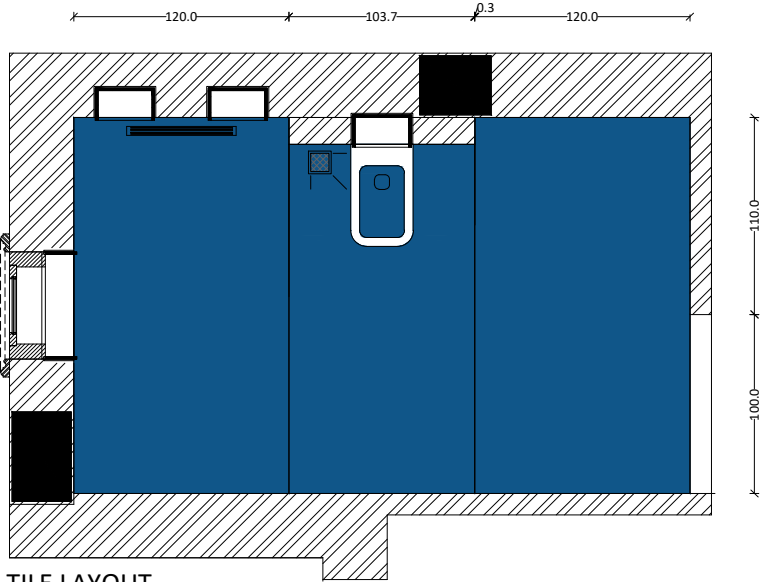

TILE LAYOUT

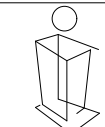

AHANAS

PROJECT:
FARM HOUSE @ TIRUNELVELI

REVISION:

DWG TITLE:BEDROOM 4 TOILET
DETAILS (SABARI BEDROOM)

DRAWN: AA

DATE: 23.05.2024


CHECKED:

REVISED DATE: 28.06.2024







REVISION NO:

SCALE: NTS

ALL DIMENSIONS ARE IN CMS
No dimensions to be scaled off from the drawings only written dimensions to be.
In the event of any discrepancy or difference between any interior drawings or site conditions or other wise immediate reference is to be made to the designer for clarification prior to execution of work at site

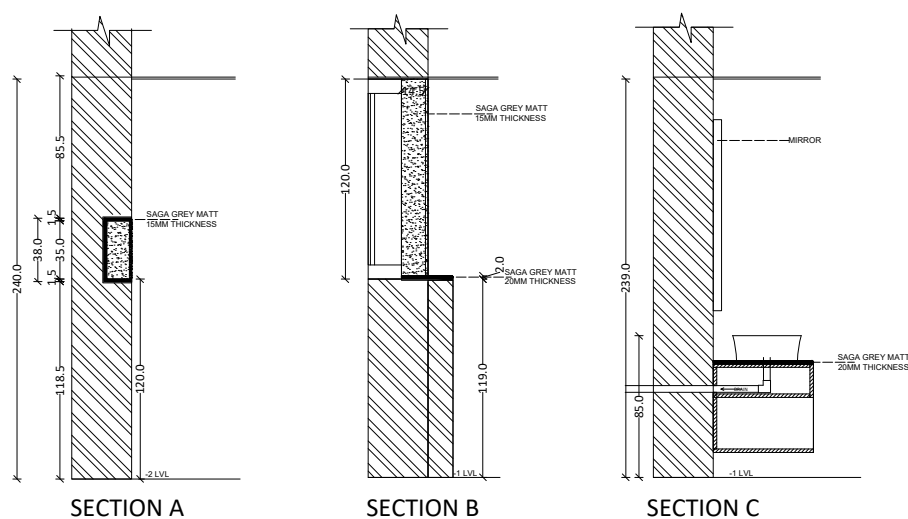

	WET AREA HIGHLIGHT - FND-16931 60CM x 60CM WITH 3MM SPACER
	DRY AREA WALLS - NEXION RUNA GRIGIO CHIRIO GREY 240 x 120 CM WITH 3MM SPACER
	WET AREA ALL WALLS & FLOOR DRY AREA FLOOR NEXION TERRAELINO GINEPRO (BLUE) NATURALE 240 x 120 CM WITH 3MM SPACER
	NICHE & TOP OF LEDGE WALL - SAGA GREY POLISH 300x80 CM 15MM THICKNESS

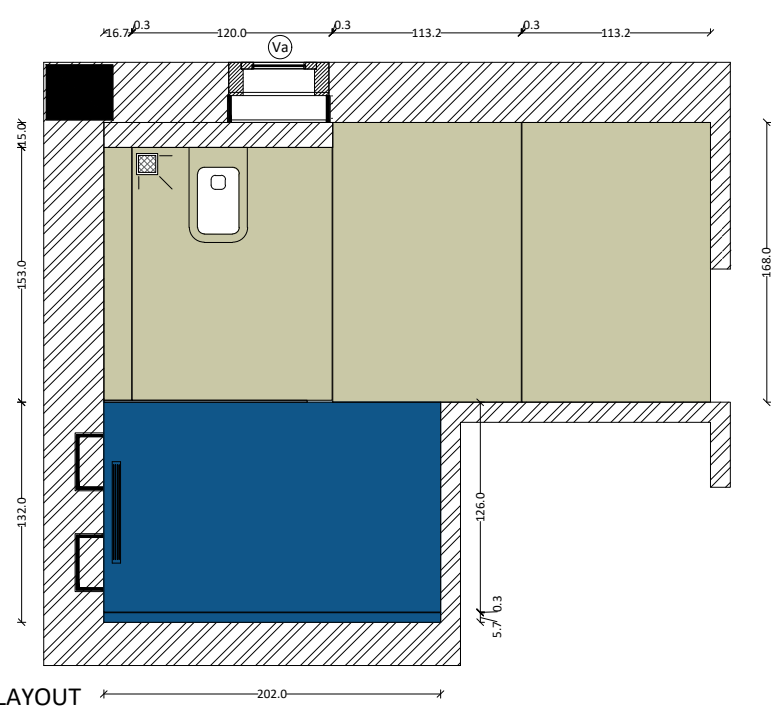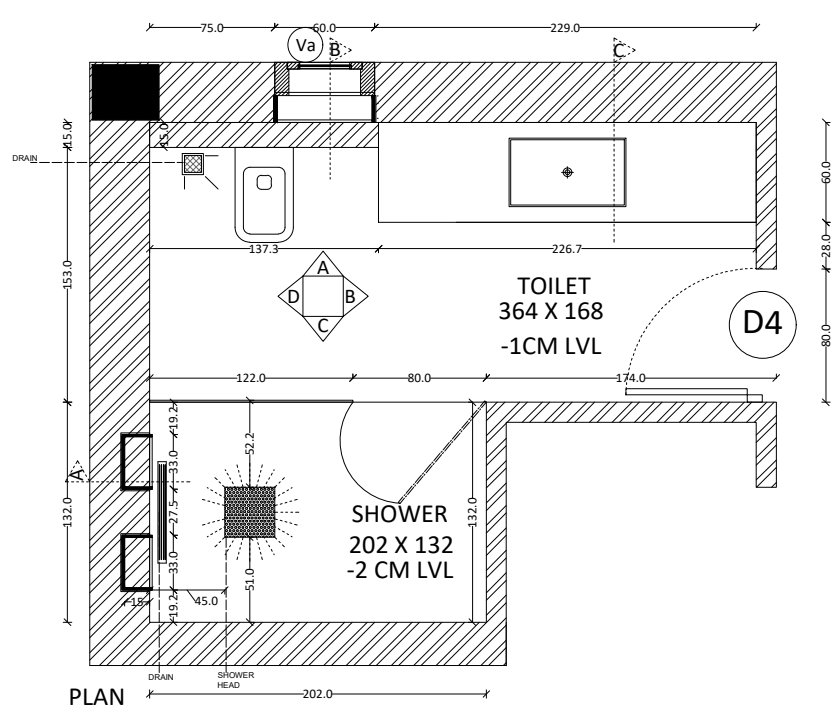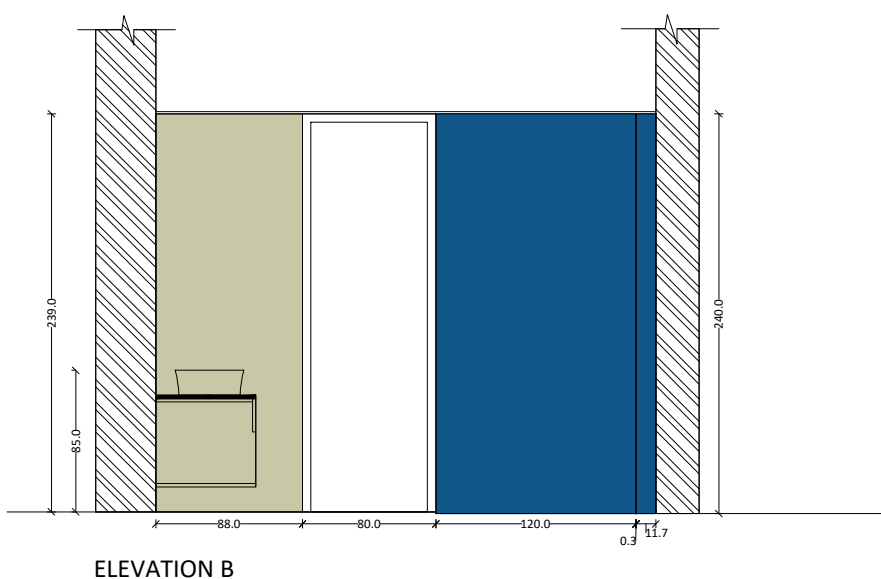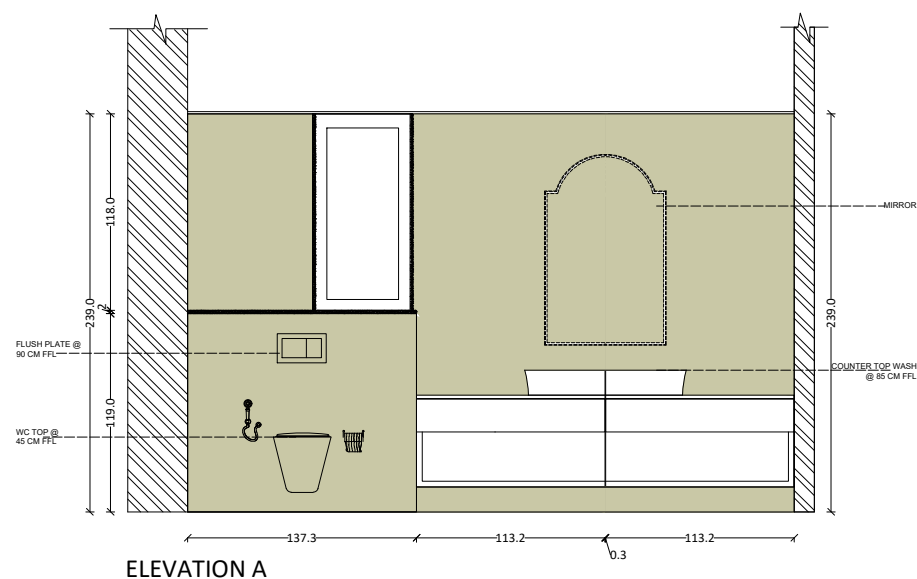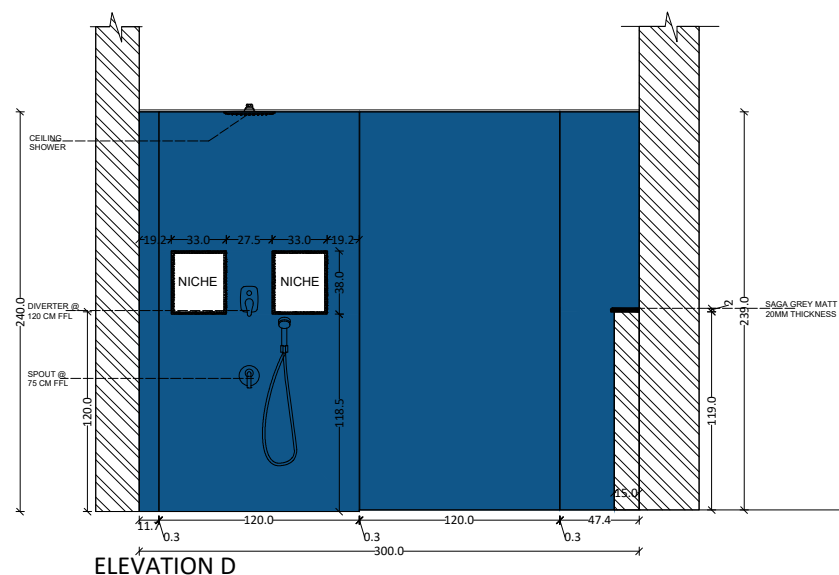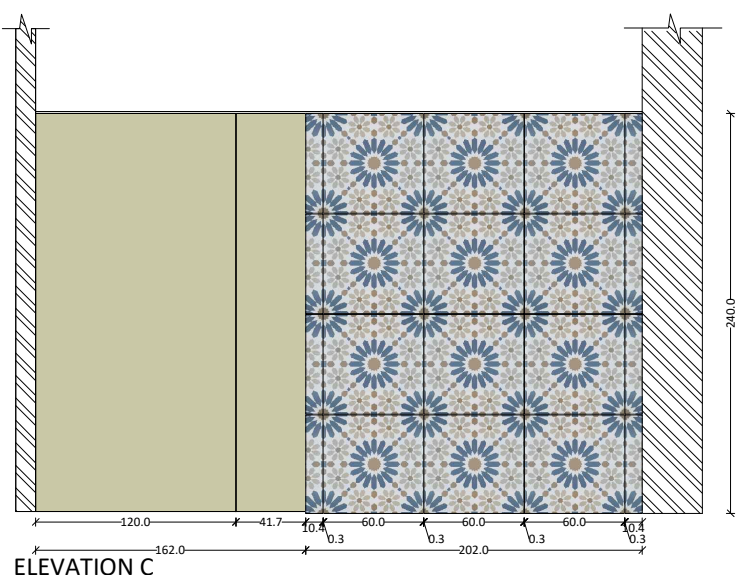

PROJECT: FARM HOUSE @ TIRUNELVELI

REVISION:

DWG TITLE: GROUND FLOOR
DORM TOILET DETAILS

DRAWN: AA

DATE: 23.05.2024


CHECKED:

REVISÉ DATE: 28 06 2024




REVISION NO:

SCALE: NTS

ALL DIMENSIONS ARE IN CMS
No dimensions to be scaled off from the drawings only written dimensions to be.
In the event of any discrepancy or difference between any interior drawings or site conditions or other wise immediate reference is to be made to the designer for clarification prior to execution of work at site

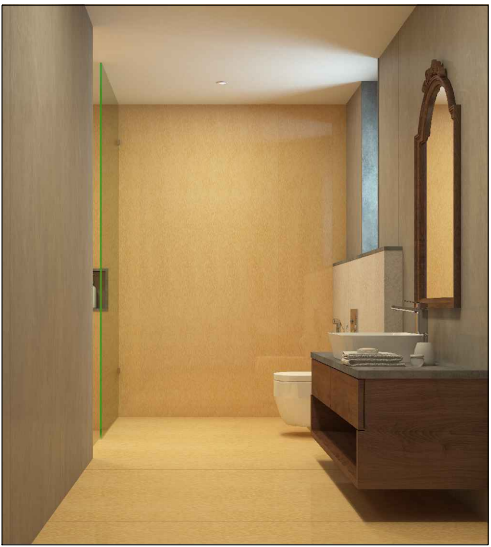

	DRY AREA ALL WALLS - SIMPOLO TINY TILES SPECTRA CHEESE 240 x 120 CM
	DRY & WET AREA FLOOR WALLS - SIMPOLO SPECTRA MUSTARD NATURALE 240 x 120 CM
	NICHE & TOP OF LEDGE WALL - SERA GREY POLISH 300x80 CM 15MM & 20MM THICKNESS
	HIGHLIGHT WALL WET AREA - SOIL HERITAGE CORNER 19.8CMx19.8CM
	HIGHLIGHT WALL WET AREA - SOIL HERITAGE BORDER 19.8CMx19.8CM
	HIGHLIGHT WALL WET AREA - SOIL HERITAGE BASE 19.8CMx19.8CM

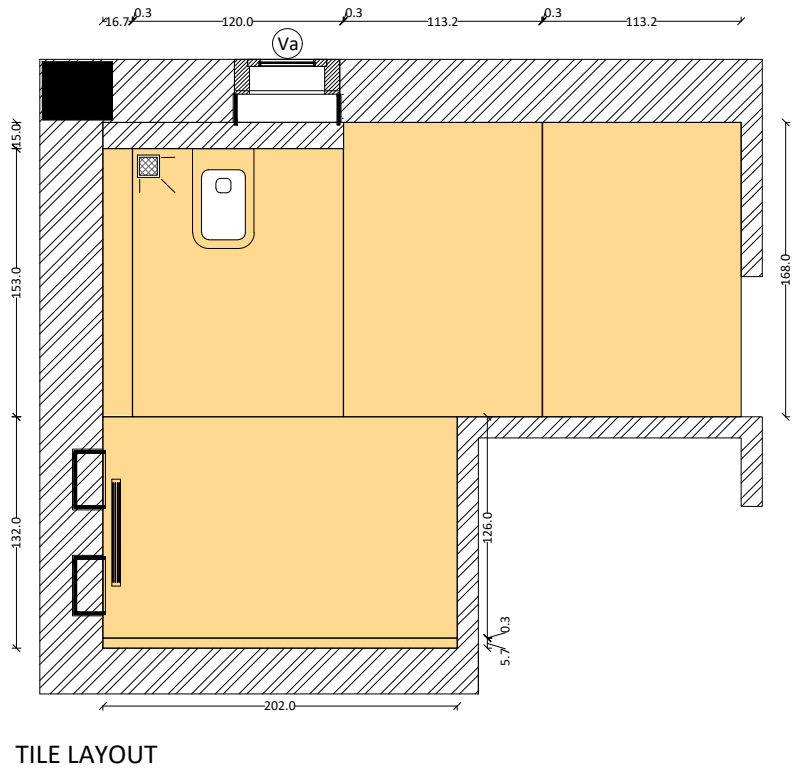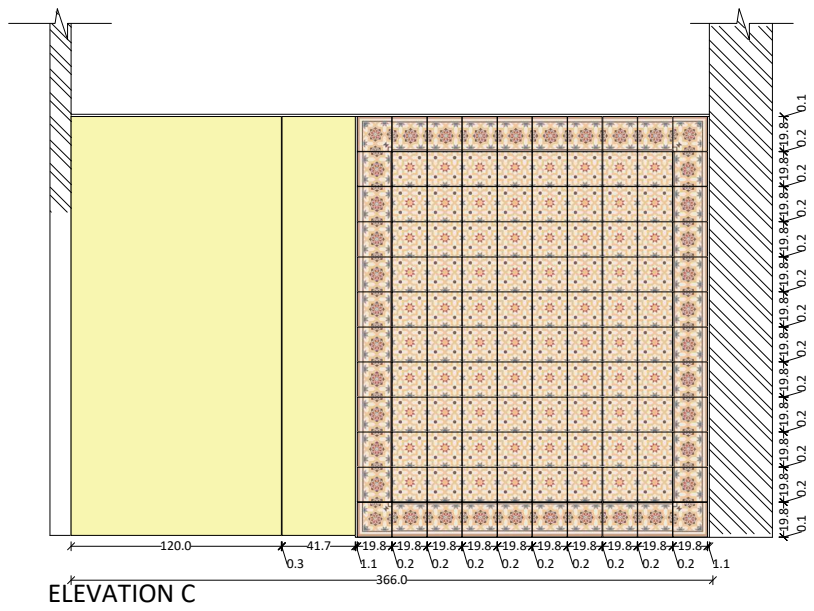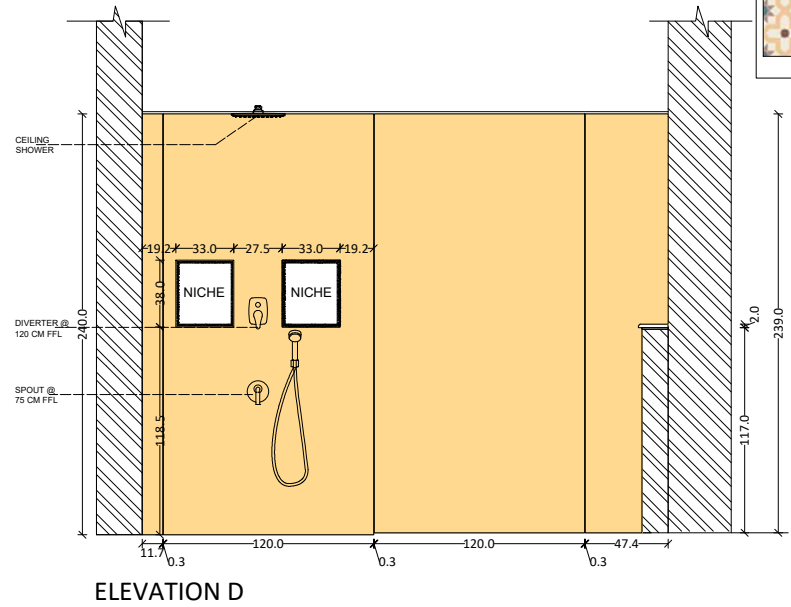

PROJECT:
FARM HOUSE @ TIRUNELVELI

REVISION:

DWG TITLE: FIRST FLOOR
DORM TOILET DETAILS

DRAWN: AA

DATE: 23.05.2024


REVISÉ DATE: 28.06.2024

CHECKED:


REVISION NO:

SCALE: NTS


ALL DIMENSIONS ARE IN CMS
No dimensions to be scaled off from the drawings only
written dimensions to be.
In the event of any discrepancy or difference between any
interior drawings or site conditions or other wise
immediate reference is to be made to the designer for
clarification prior to execution of work at site

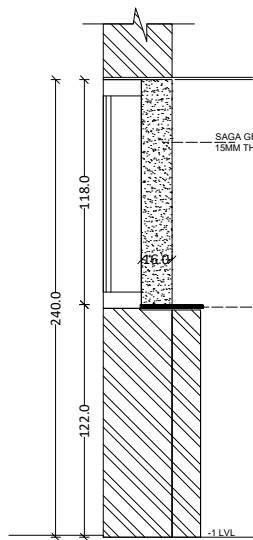


SECTION A

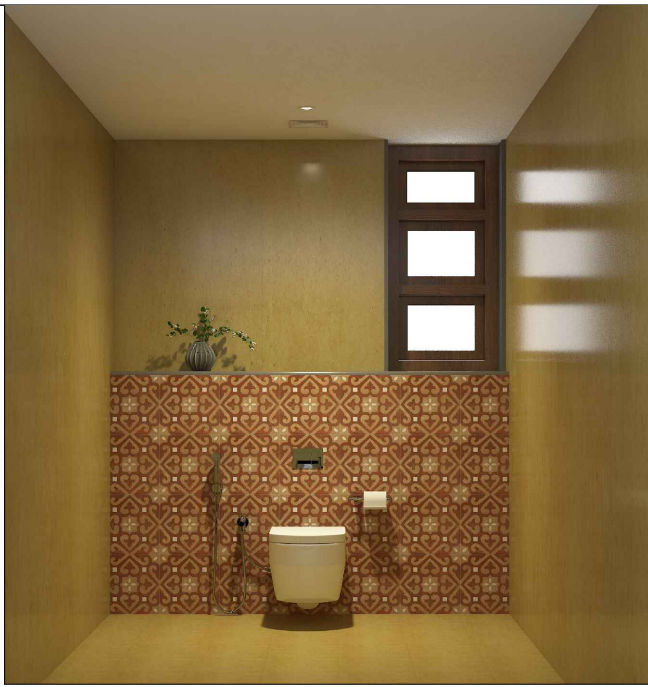


	FLOOR & WALLS (EXCEPT LEDGE WALL) - SIMPOLO SPECTRA MUSTARD TINY TILES 240x120 CM
	SRBL 1266 30x30 CM
	NICHE & TOP OF LEDGE WALL-SAGA GREY POLISH 300x80CM

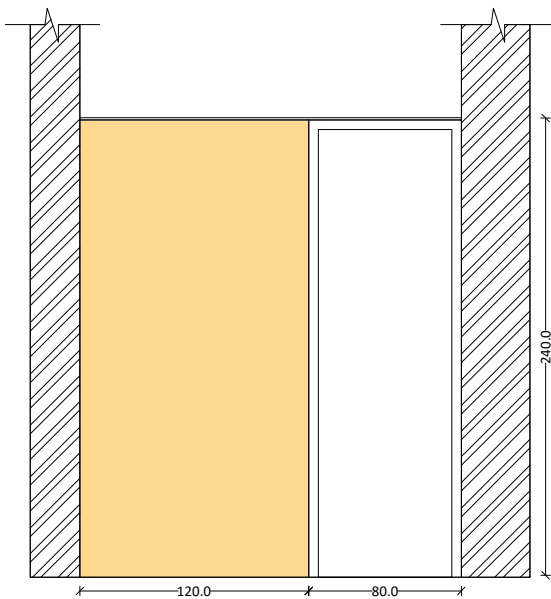


ELEVATION C

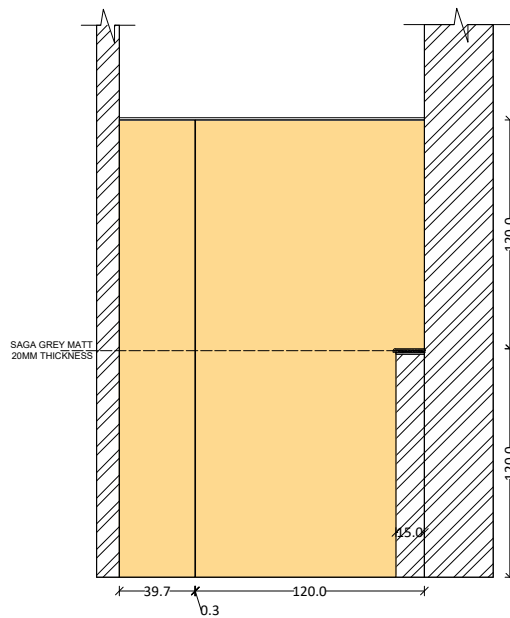


ELEVATION D

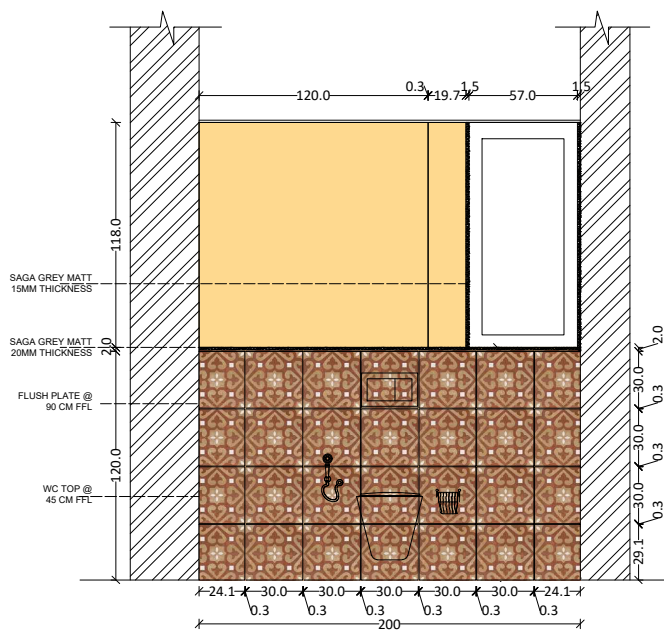


ELEVATION A

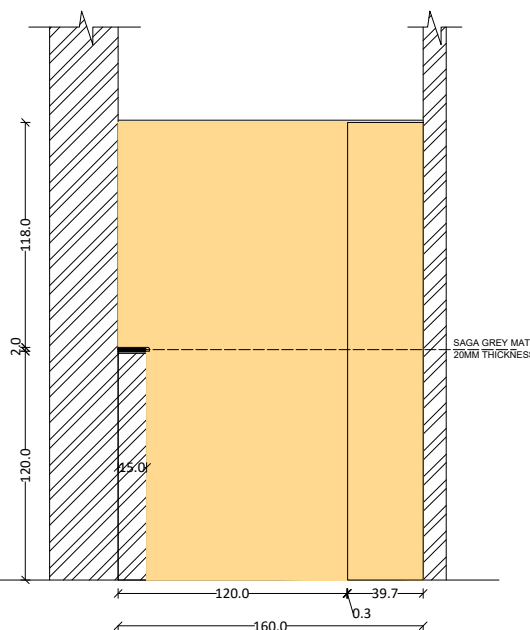

ELEVATION B

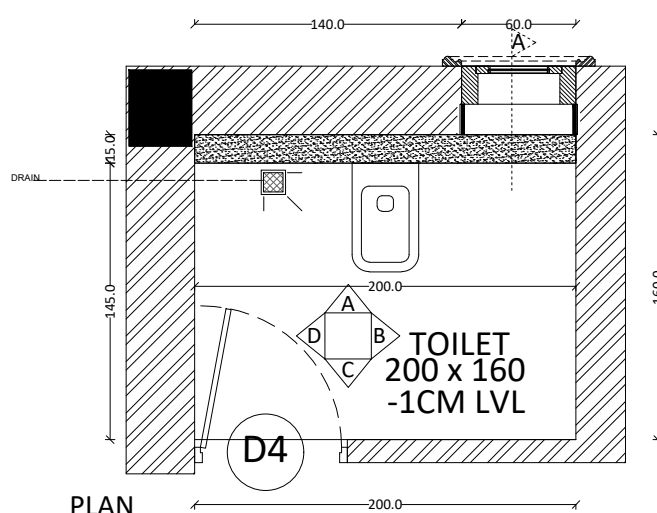

PLAN

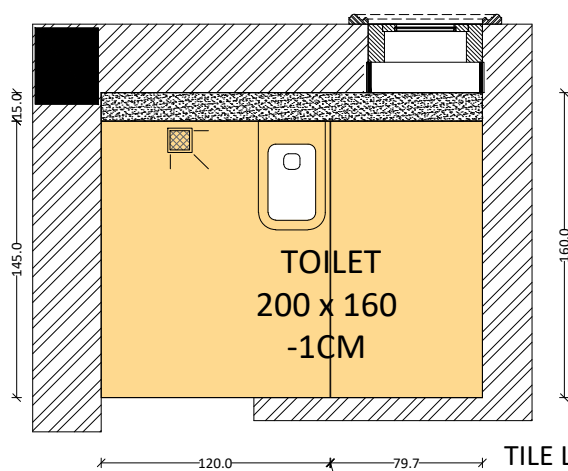

TILE LAYOUT



PROJECT:
FARM HOUSE @ TIRUNELVELI

REVISION:

DWG TITLE: GROUND FLOOR
POWDER ROOM DETAILS

DRAWN: AA

DATE: 23.05.2024


CHECKED:

REVISED DATE: 28.06.2024

REVISION NO:

SCALE: NTS

ALL DIMENSIONS ARE IN CMS
No dimensions to be scaled off from the drawings only written dimensions to be.
In the event of any discrepancy or difference between any interior drawings or site conditions or other wise immediate reference is to be made to the designer for clarification prior to execution of work at site

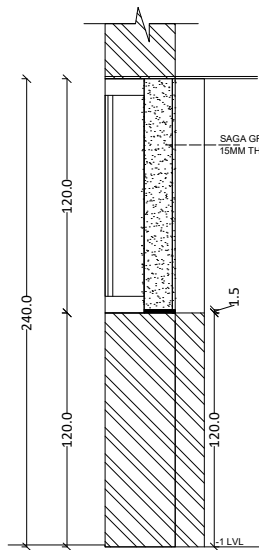

SECTION A



WC LEDGE WALL - NEXION
ANTIQUE BLACK LAP MATT
240x120 CM 3MM SPACER



ALL WALLS EXCEPT FIXTURE
WALL - NEXION KAIR
CALACATTA LAP MATT
240x120 CM 3MM SPACER




WINDOW BORDER
SAGA GREY MATT 15MM
THICKNESS 300x80 CM




ET CHORAS CUBO BLACK L-S
60x60 CM




WALL - WASH HIGHLIGHT -
HERRING BONE DARK
VRHB1201

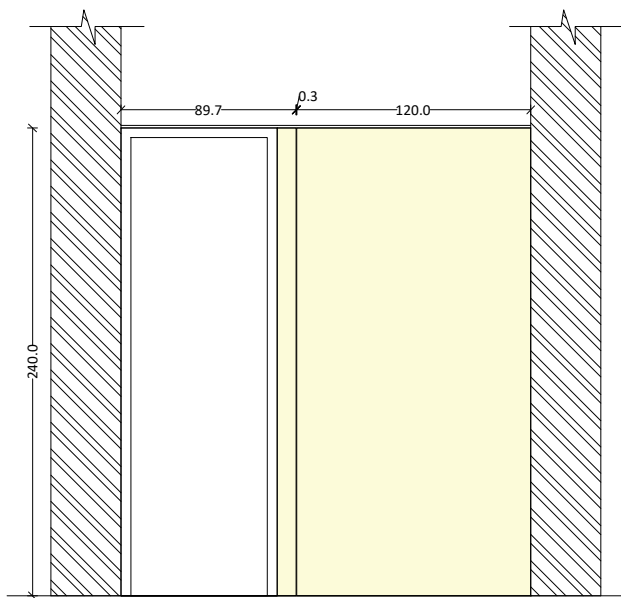


ELEVATION C

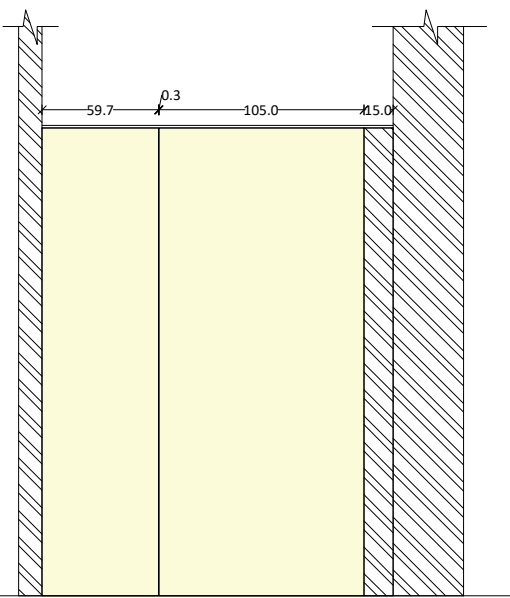


ELEVATION D

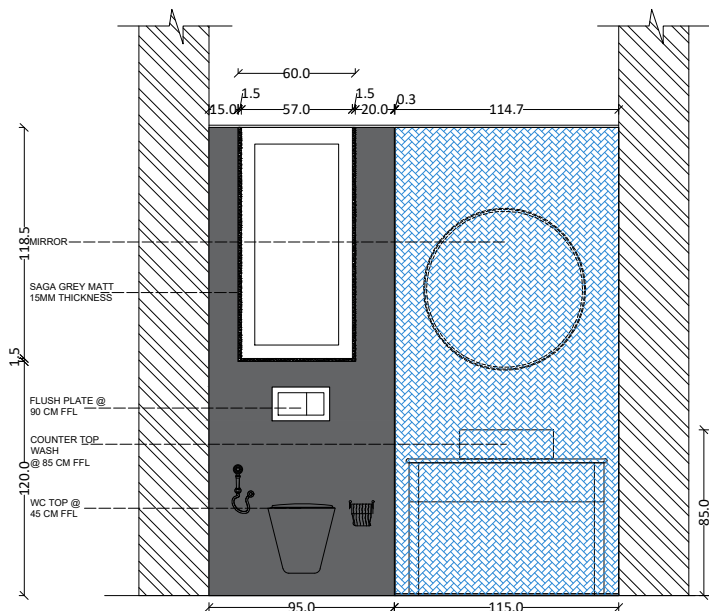


ELEVATION A

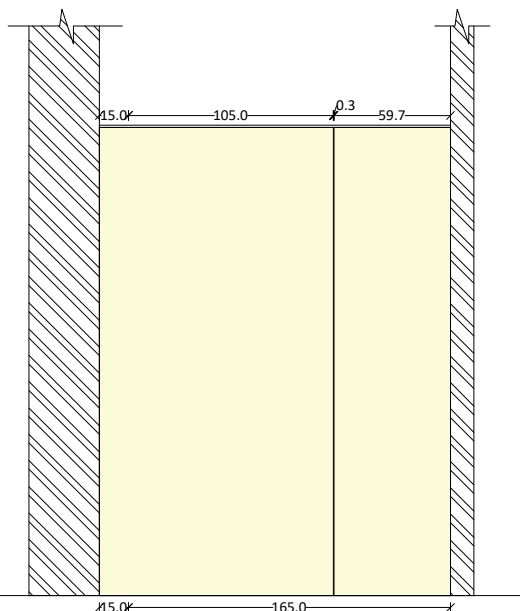

ELEVATION B

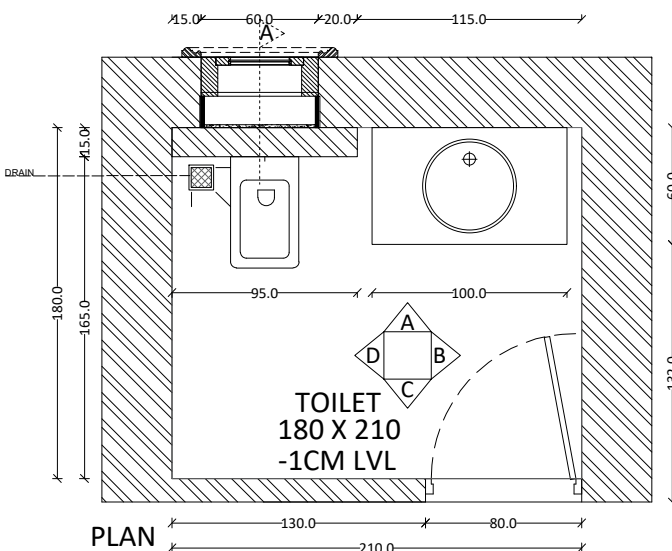

PLAN

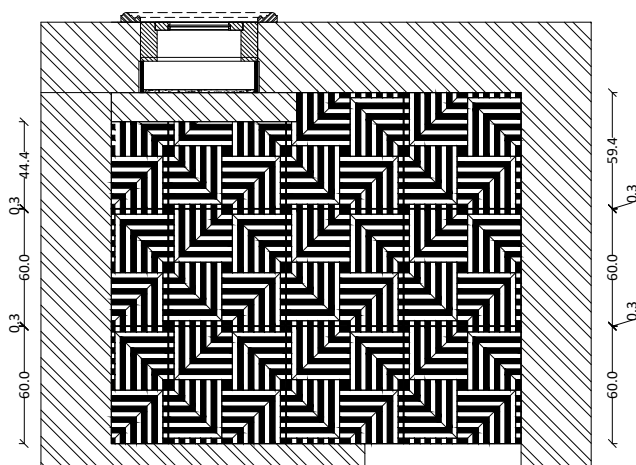

TILE LAYOUT



PROJECT:
FARM HOUSE @ TIRUNELVELI

DWG TITLE: FIRST FLOOR
POWDER ROOM DETAILS

DRAWN: AA

DATE: 23.05.2024

CHECKED:

REVISED DATE: 28.06.2024

REVISION NO:

REVISION:

SCALE: NTS

ALL DIMENSIONS ARE IN CMS
No dimensions to be scaled off from the drawings only
written dimensions to be.
In the event of any discrepancy or difference between any
interior drawings or site conditions or other wise
immediate reference is to be made to the designer for
clarification prior to execution of work at site