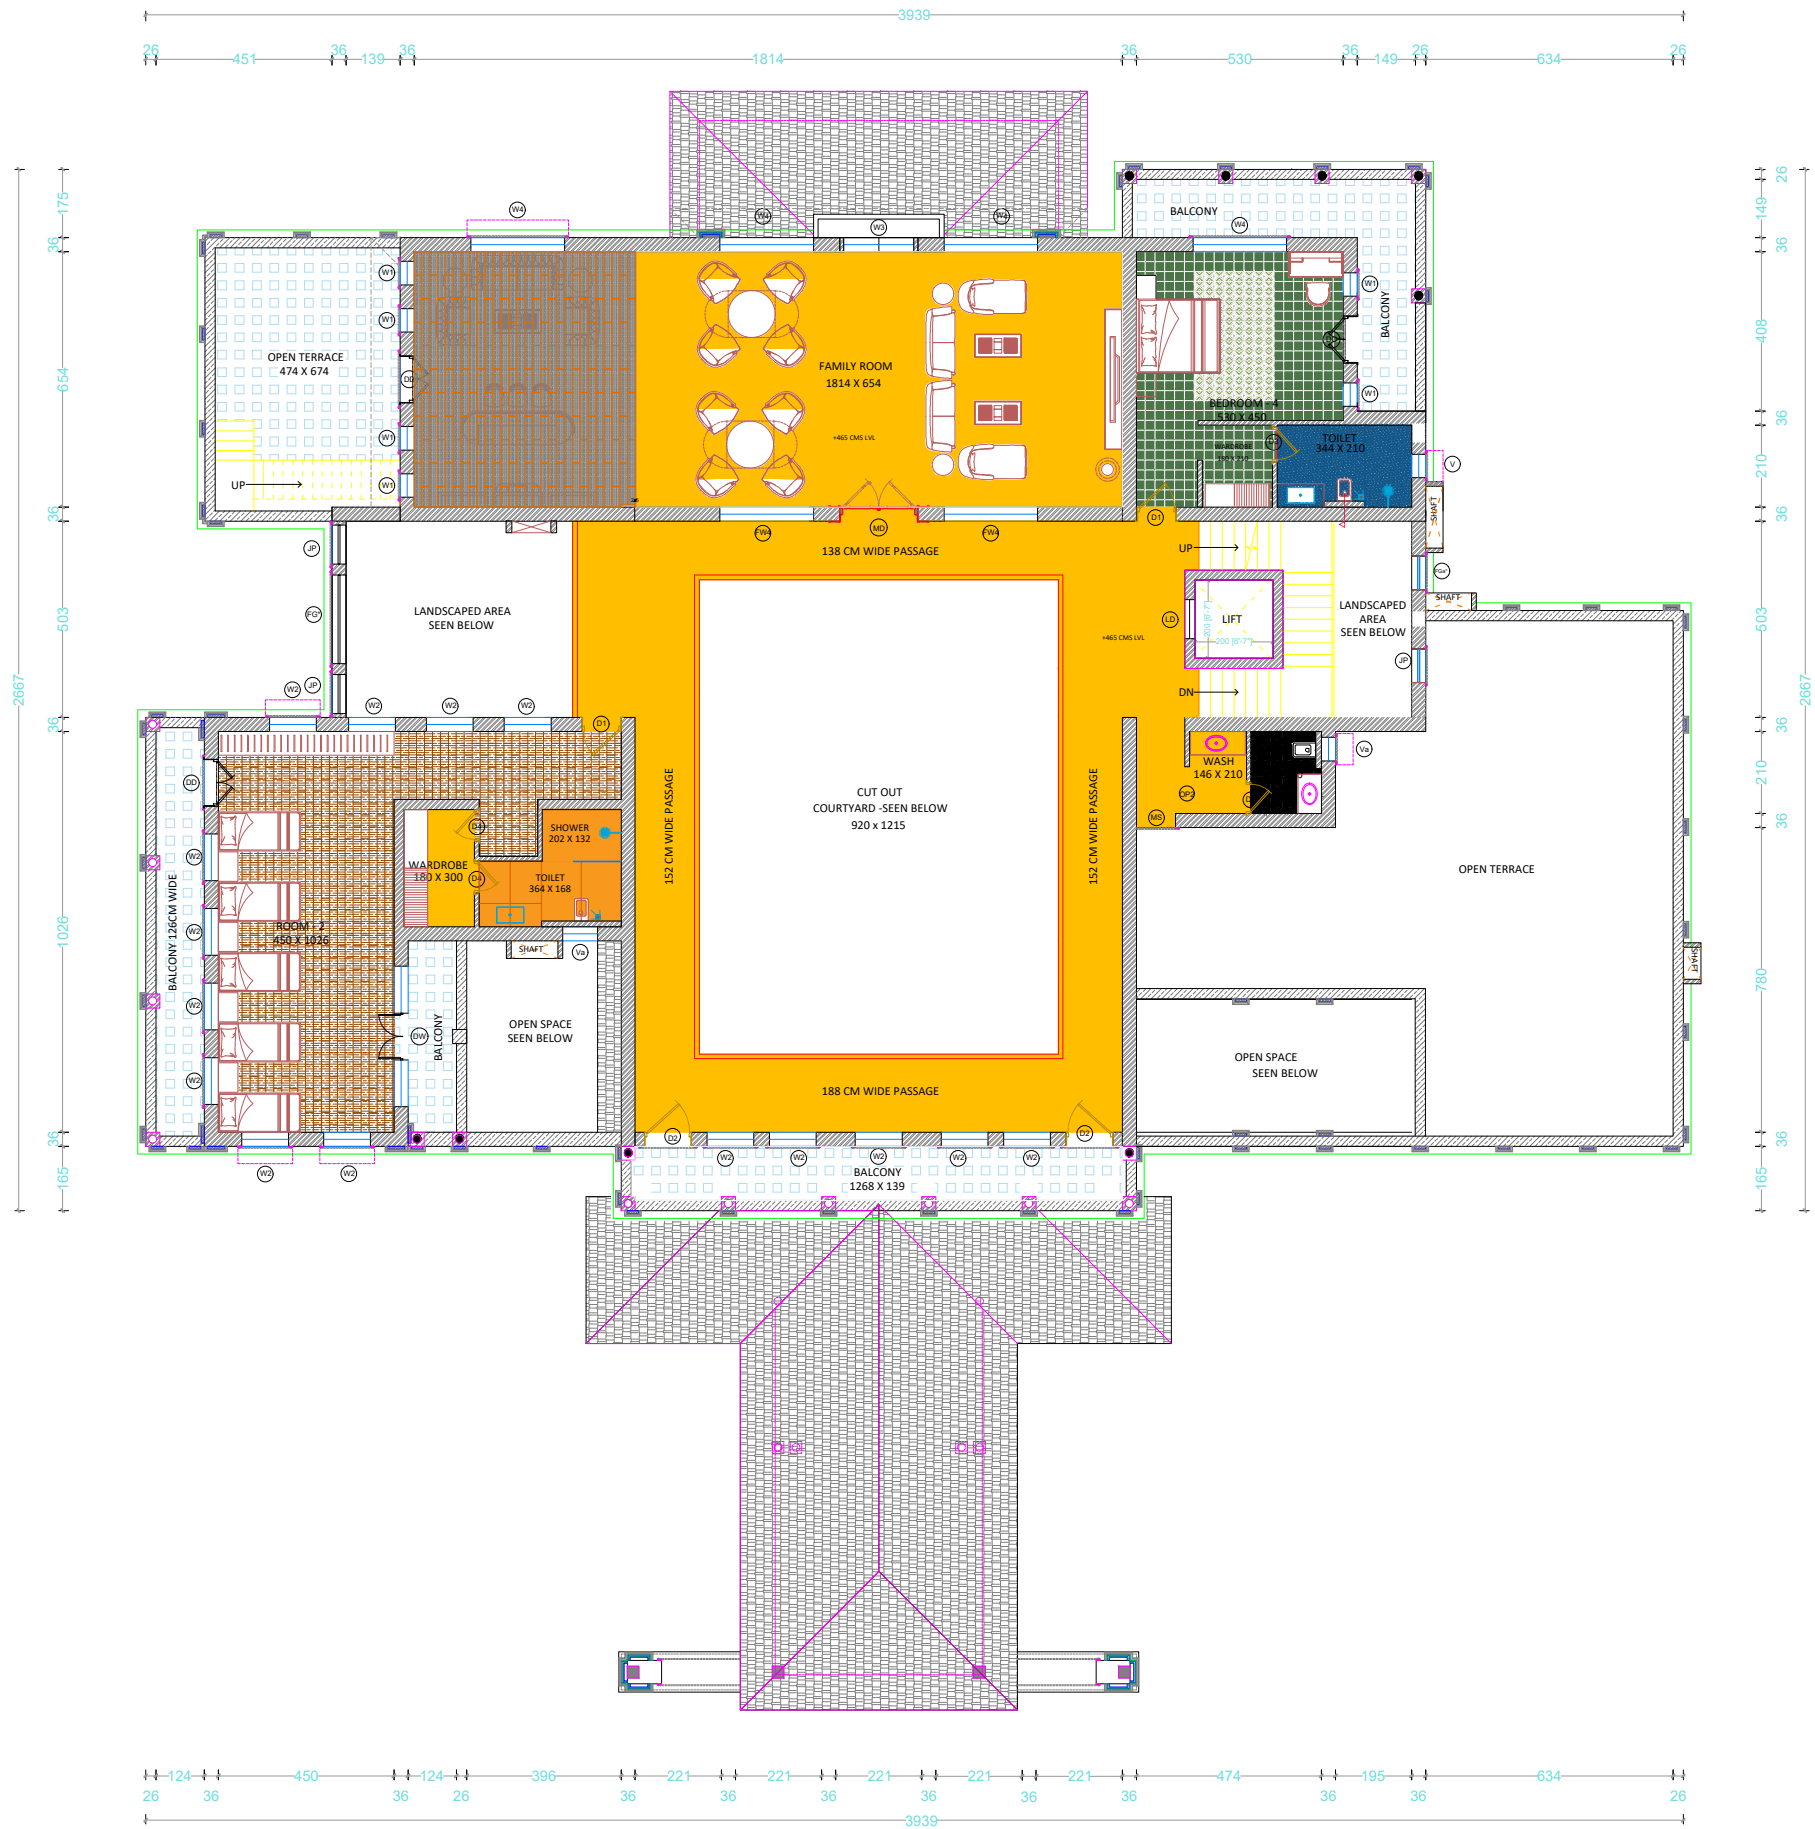


DATE: 20.06.2024

SCALE : NTS

DRAWN: JAB

CHECKED:

PROJECT NO:563

DRAWING NO:
ADFS/AR/ 563/

PROJECT: RESIDENTIAL PROJECT AT
TIRUNELVELI

CLIENT: SHABREESH

DRAWING TITLE:

FIRST FLOOR TILE LAYOUT

REVISION:



NOTES:

- ALL DIMENSIONS ARE IN CMS, UNLESS OTHERWISE SPECIFIED
- DIMENSIONS SHALL NOT BE MEASURED DIRECTLY FROM THIS DRAWINGS.
FOLLOW ONLY WRITTEN DIMENSIONS
- IN THE EVENT OF ANY DISCREPANCY OR DIFFERENCE BETWEEN ANY
DRAWINGS OR SITE CONDITIONS OR OTHERWISE IMMEDIATE REFERENCE
IS TO BE MADE TO THE DESIGNER FOR CLARIFICATION PRIOR TO EXECUTION
- OF WORK AT SITE
- ALL THE CIVIL WORKS SHOULD BE IN LINE LEVEL AND PLUMB.
- PLASTERING TO BE CUT AT SKIRTING LEVEL.