

SECTION A



WC LEDGE WALL - NEXION
ANTIQUE BLACK LAP MATT
240x120 CM 3MM SPACER



ALL WALLS EXCEPT FIXTURE
WALL - NEXION KAIR
CALACATTA LAP MATT
240x120 CM 3MM SPACER




WINDOW BORDER
SAGA GREY MATT 15MM
THICKNESS 300x80 CM




ET CHORAS CUBO BLACK L-S
60x60 CM




WALL - WASH HIGHLIGHT -
HERRING BONE DARK
VRHB1201

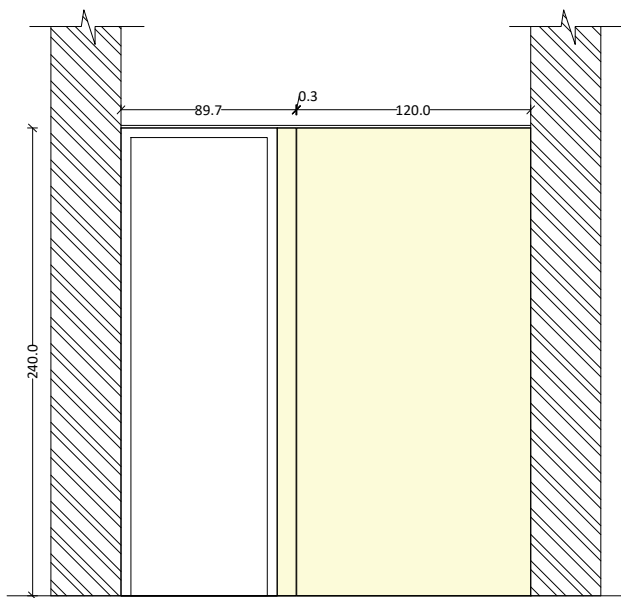


ELEVATION C

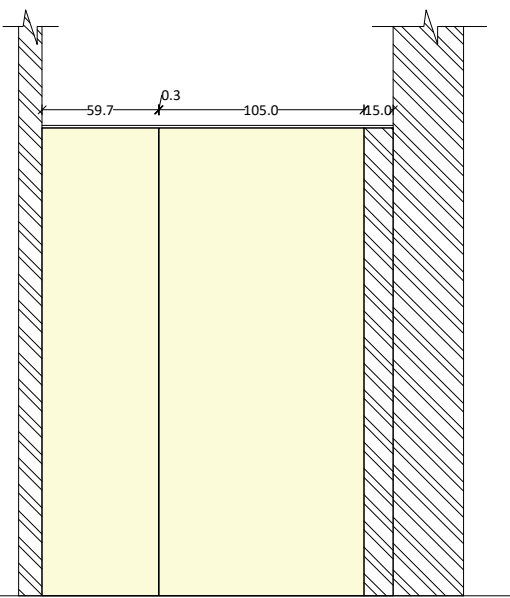


ELEVATION D

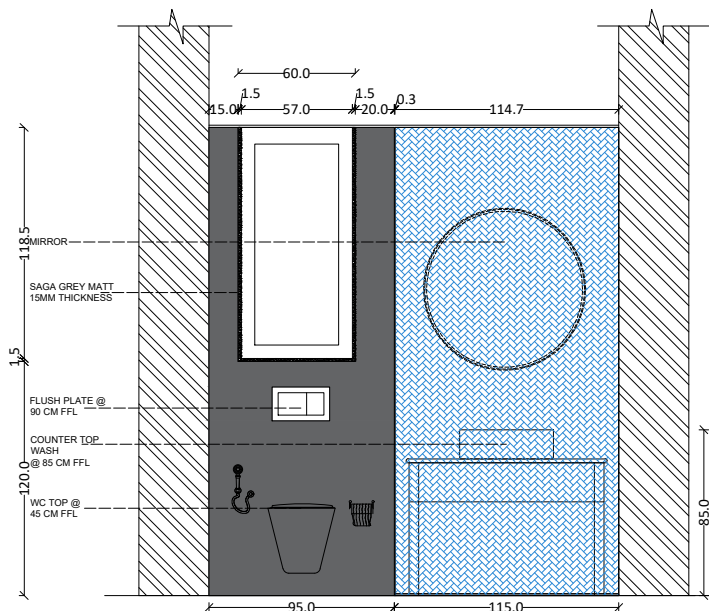


ELEVATION A

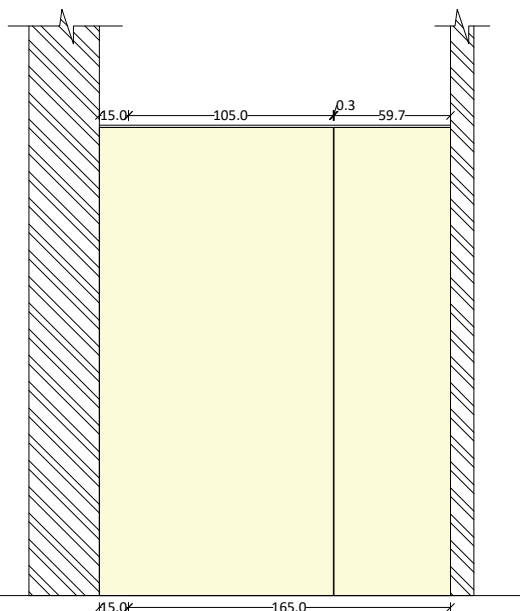


ELEVATION B

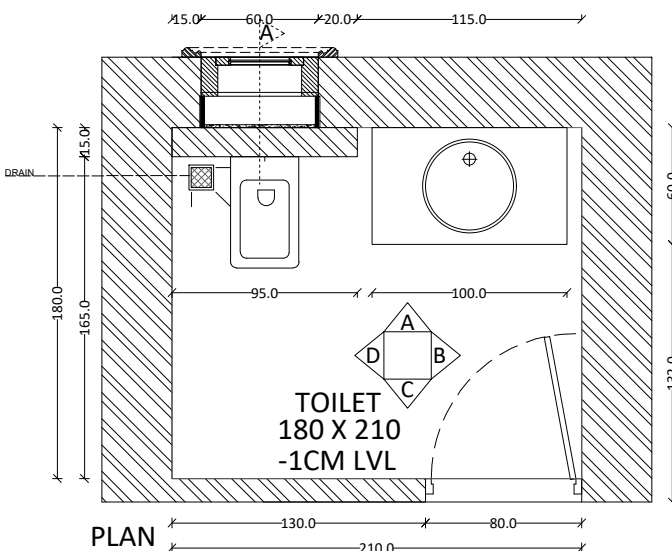

PLAN

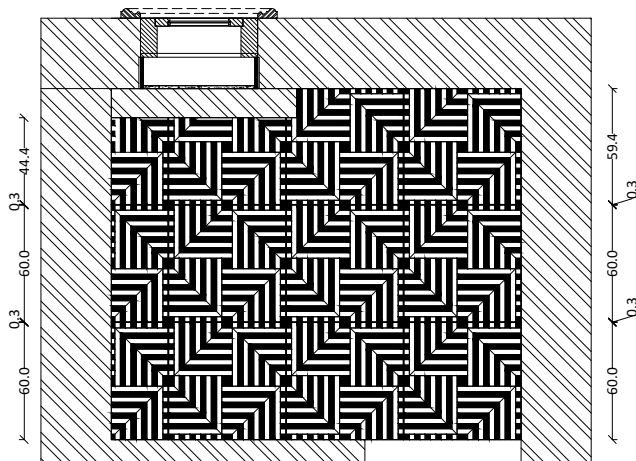

TILE LAYOUT

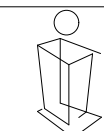

AHANAS

PROJECT:
FARM HOUSE @ TIRUNELVELI

DWG TITLE: FIRST FLOOR
POWDER ROOM DETAILS

DRAWN: AA

DATE: 23.05.2024

CHECKED:

REVISED DATE: 28.06.2024

REVISION NO:

REVISION:

SCALE: NTS

ALL DIMENSIONS ARE IN CMS
No dimensions to be scaled off from the drawings only
written dimensions to be.
In the event of any discrepancy or difference between any
interior drawings or site conditions or other wise
immediate reference is to be made to the designer for
clarification prior to execution of work at site