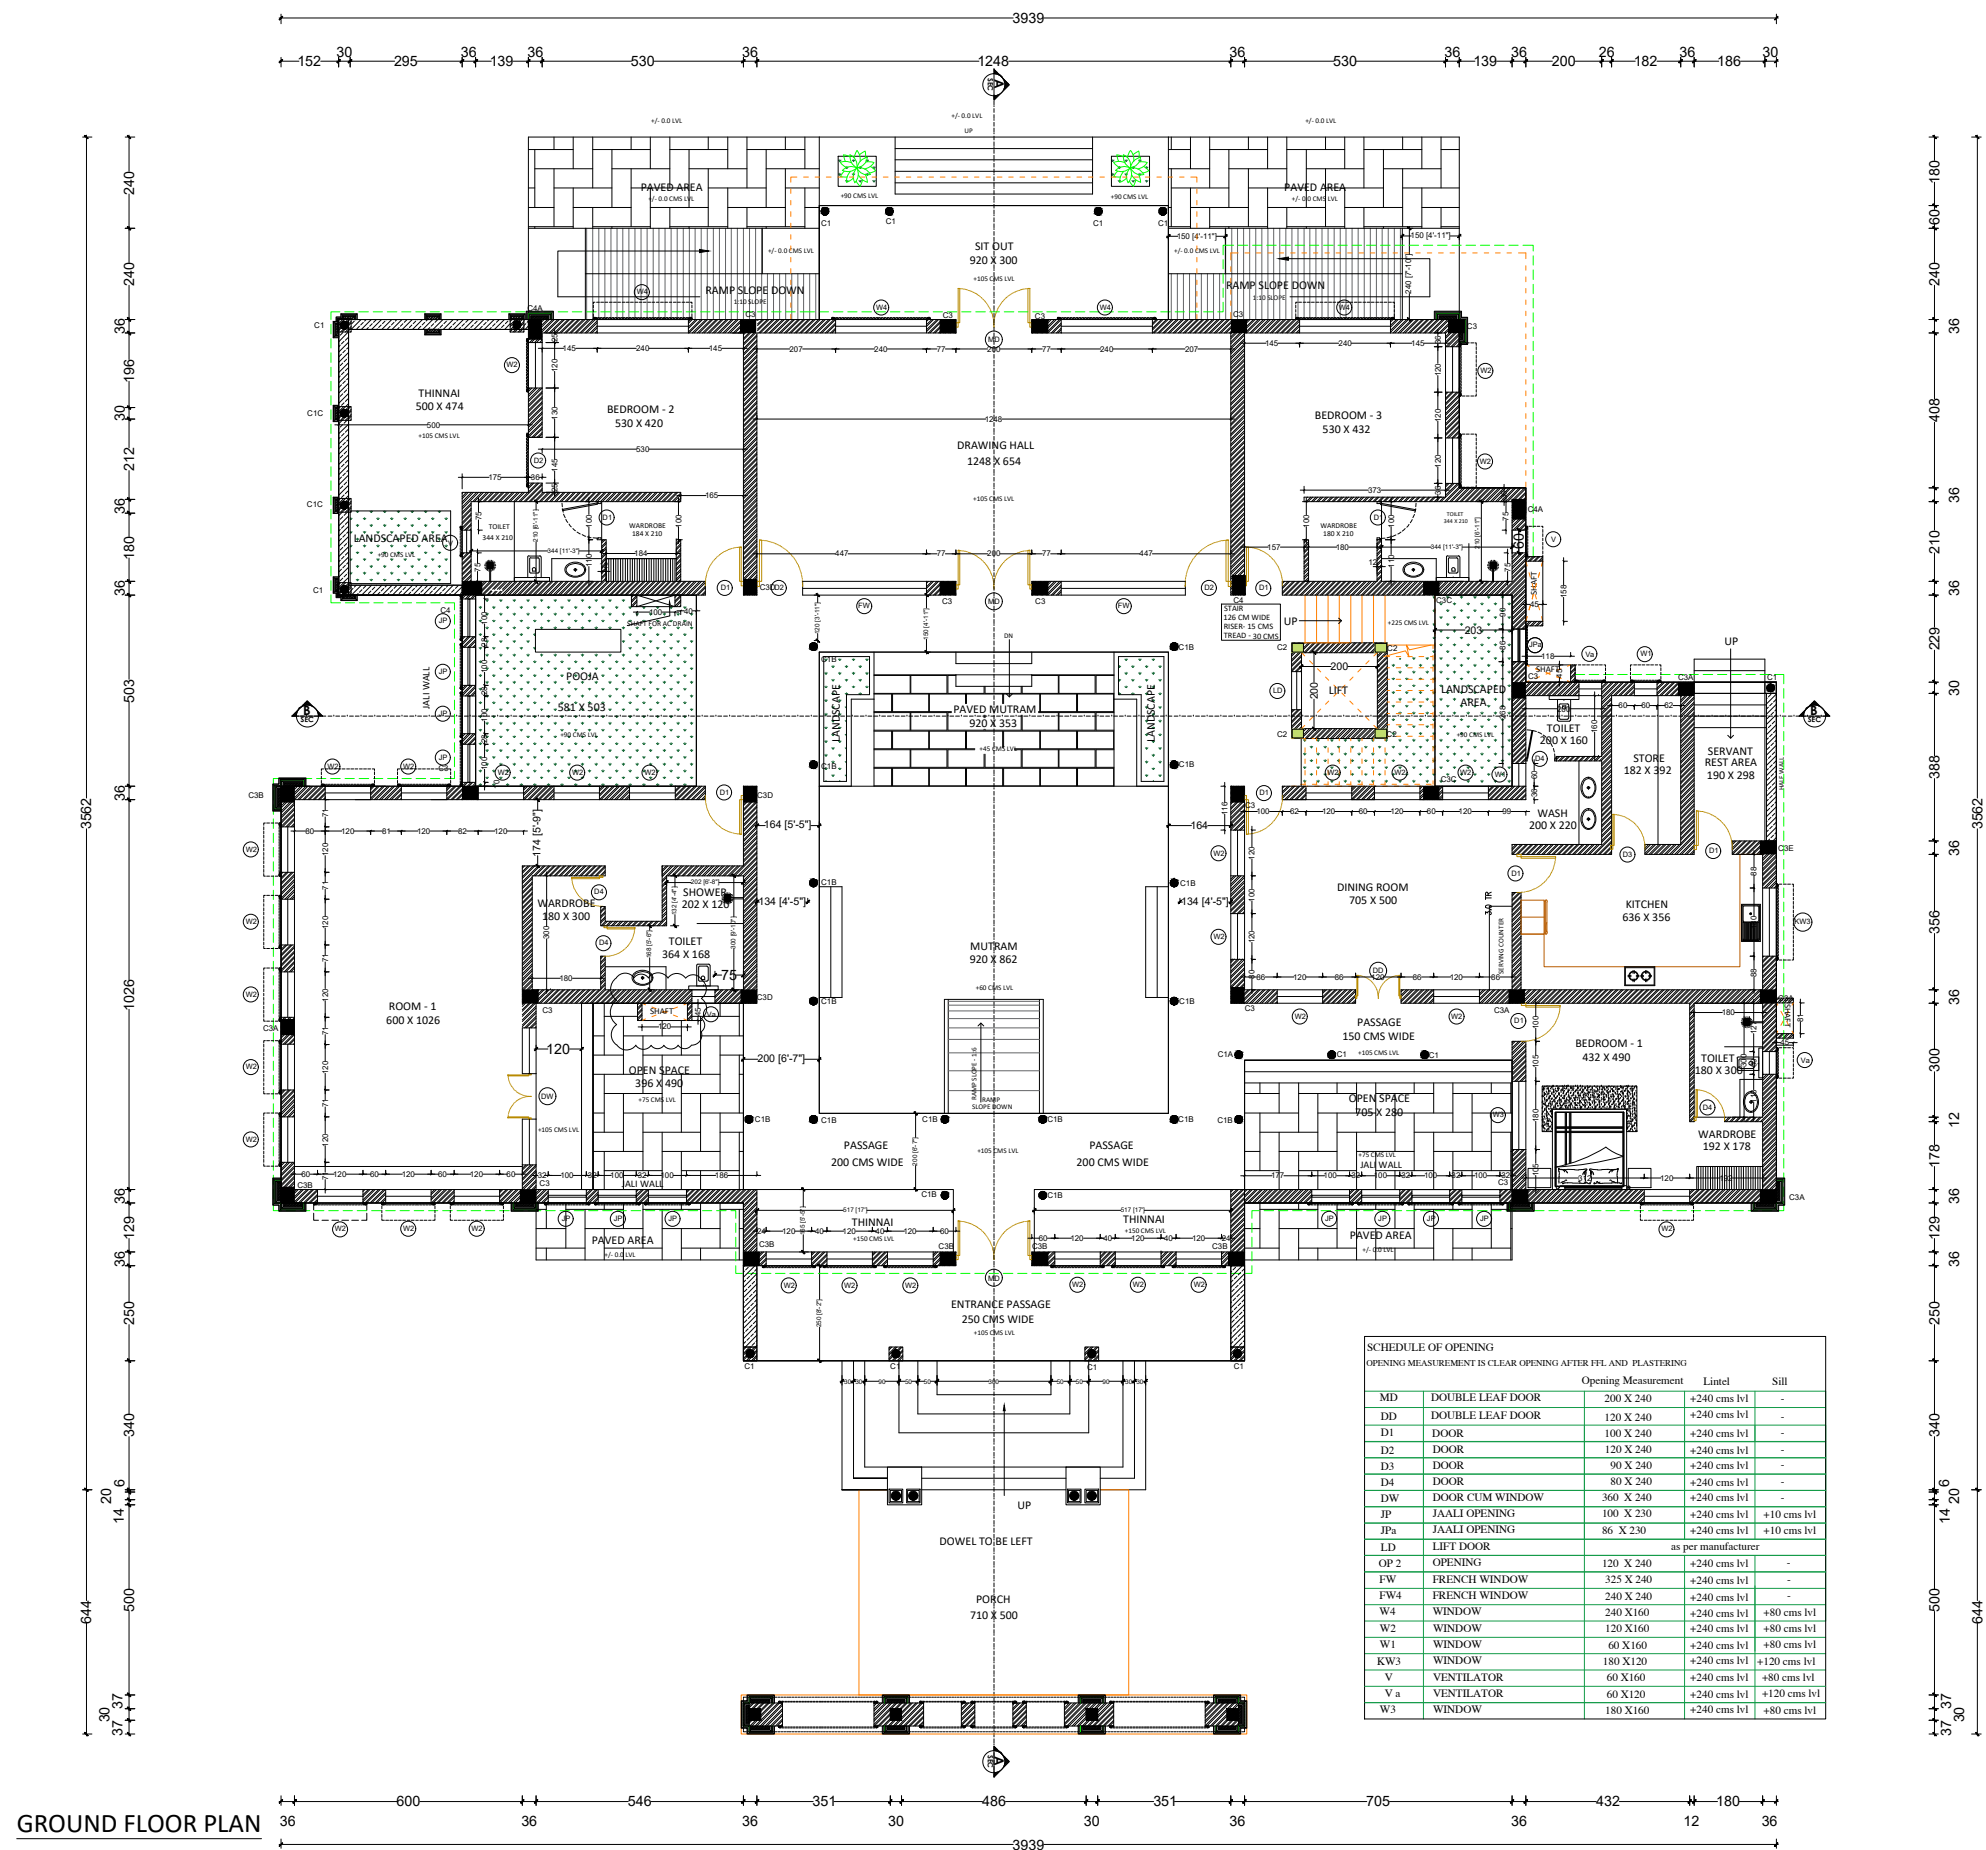


DATE: 19.08.2023

SCALE : NA

DRAWN: AP

CHECKED: ANEENA

PROJECT NO:563

DRAWING NO:
ADFS/AR/ 563/FH-03

PROJECT: RESIDENTIAL PROJECT AT
TIRUNELVELI

CLIENT: SHABREESH


DRAWING TITLE:
GROUND FLOOR PLAN

REVISION:

1,	22-08-23-CHANGE IN TOILET DIMENSION AS PER CLIENT REQUEST
----	---

2,	13-05-24- WALL EXTENSION OF TOILET FOR PROVIDING TV
	CHANGES IN SHAFT LOCATION/ SIZE AS PER HVAC
	CONSULTANT REQUIREMENT

3,	27-05-24- BEDROOM TOILET WALL CHANGE AS PER INTERIORS
----	---

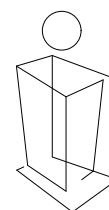

A'HANAS

NOTES:

○ ALL DIMENSIONS ARE IN CMS, UNLESS OTHERWISE SPECIFIED

○ DIMENSIONS SHALL NOT BE MEASURED DIRECTLY FROM THIS DRAWINGS.

FOLLOW ONLY WRITTEN DIMENSIONS

○ IN THE EVENT OF ANY DISCREPANCY OR DIFFERENCE BETWEEN ANY DRAWINGS OR SITE CONDITIONS OR OTHERWISE IMMEDIATE REFERENCE

IS TO BE MADE TO THE DESIGNER FOR CLARIFICATION PRIOR TO EXECUTION

OF WORK AT SITE

○ ALL THE CIVIL WORKS SHOULD BE IN LINE LEVEL AND PLUMB.

○ PLASTERING TO BE CUT AT SKIRTING LEVEL.