


LIST OF ACCESSORIES :	LIST OF APPLIANCES:	NOTE:
1. CUTLERY BASKET - 90 CM 2.WASTE BIN 3. DETERGENT HOLDER	a. HOB b. HOOD c. SINGLE BOWL SINK WITH DRAIN BOARD d. REFRIGERATOR e. DISHWASHER f. UNDER COUNTER WATER PURIFIER	1. DIMENSIONS OF THE APPLIANCES MAY VARY ACCORDING TO THE ITEMS FINALIZED BY THE CLIENT. LIST OF MATERIALS

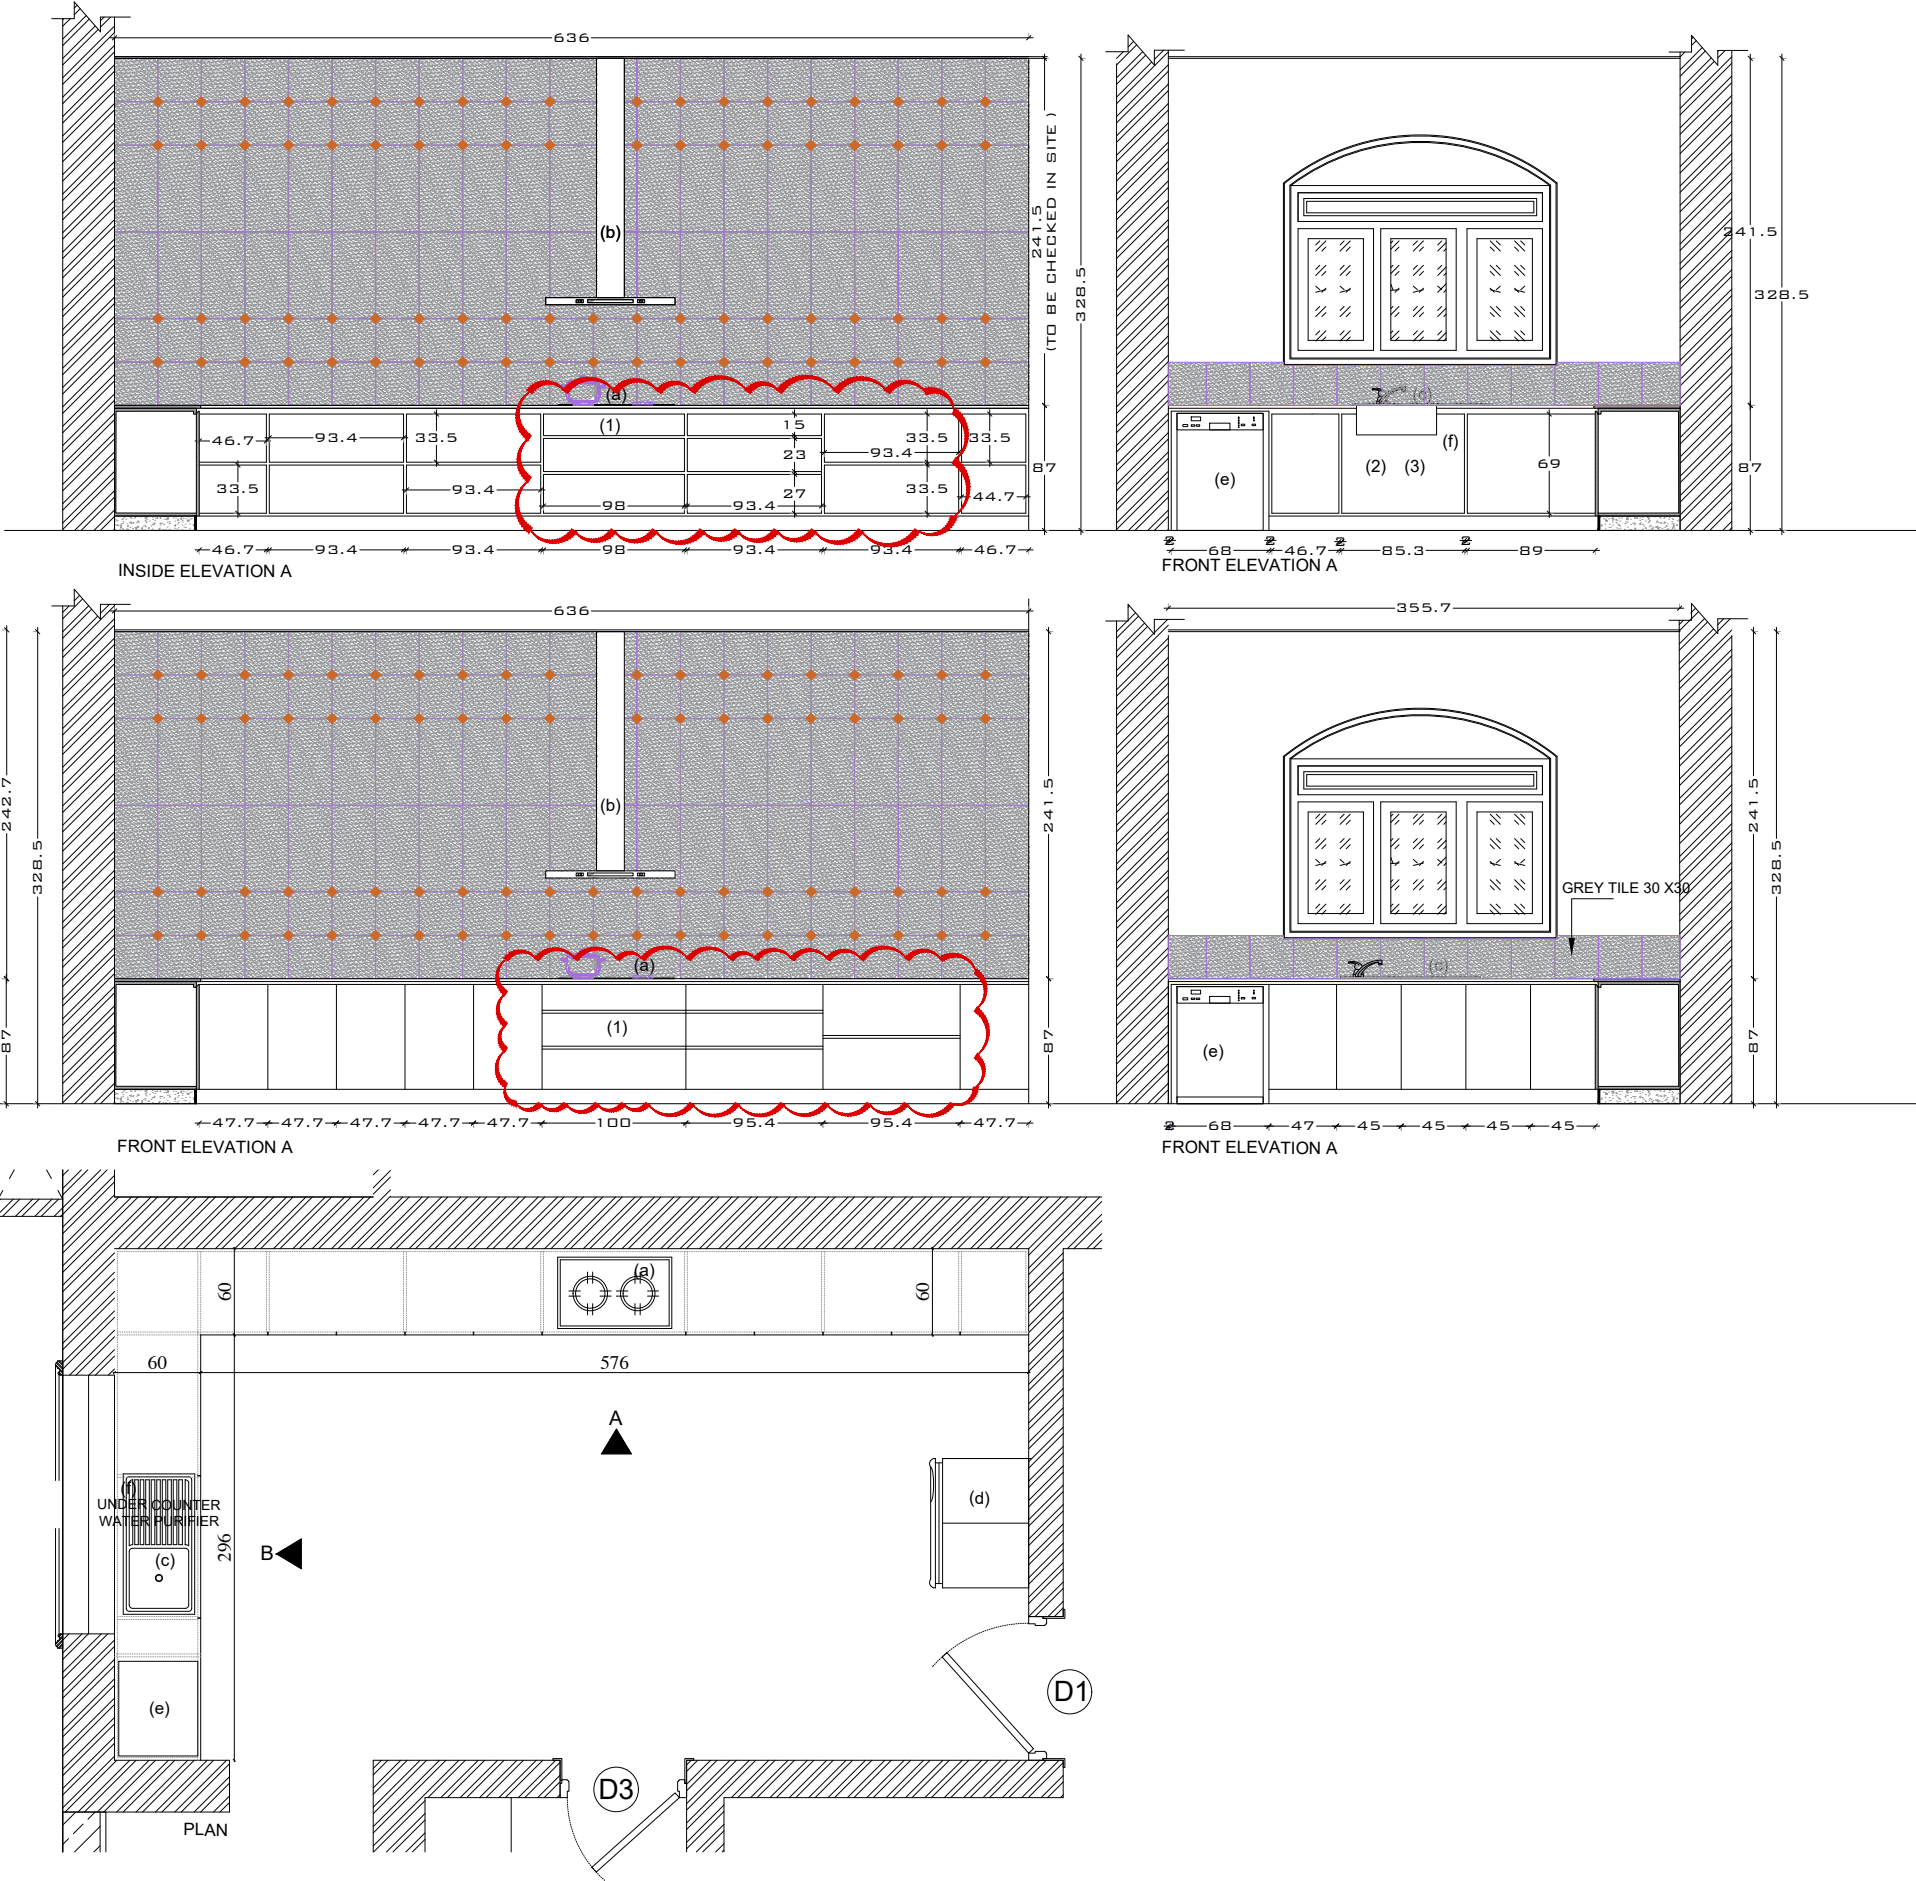

GENERAL NOTES:		ARCHITECTURAL/INTERIOR DESIGN CONSULTANT:		KEY PLAN:		CARDINAL DIRECTION:	
○ ALL DIMENSIONS ARE IN MM,UNLESS OTHERWISE SPECIFIED. ○ DIMENSIONS SHALL NOT BE MEASURED DIRECTLY FROM-THIS DRAWINGS. FOLLOW ONLY WRITTEN DIMENSIONS. ○ IN THE EVENT OF ANY DISCREPANCY OR DIFFERENCE-BETWEEN ANY DRAWINGS OR SITE CONDITIONS /OTHERWISE IMMEDIATE REFERENCE IS TO BE MADE TO THE DESIGNER-FOR CLARIFICATION PRIOR TO EXECUTION OF WORK AT SITE. ○ ALL THE CIVIL/INTERIOR WORKS SHOULD BE IN LINE LEVEL AND PLUMB. ○ PLASTERING TO BE CUT AT SKIRTING LEVEL(AS PER SPECIFICATION).		 33/1622A, 'NAVAM' Haritha By-Lane Vennala P.O, Kochi 682 028 Email: ahanas@ahanas.com AHANAS DESIGN 4 SPACE					
REVISION NOTES:		STRUCTURAL CONSULTANT: /MEP CONSULTANT:		PROJECT:		DRAWN:	
22/02/2025 BOTTOM CABINET REVISION				FARMHOUSE AT TIRUNELVELI		AA	
				STATUS/ISSUED FOR:		CHECKED:	
				REFERENCE		AP	
		CLIENT:		PROJECT NO:		REVISION:	
				563		R1	
		MR. SHABAREESH		DRAWING TITLE:		DRAWING NO:	
				KITCHEN LAYOUT		-	
						SCALE:	
						NTS	
						SHEET SIZE:	
						A3	
						DATE:	
						22/02/2025	