
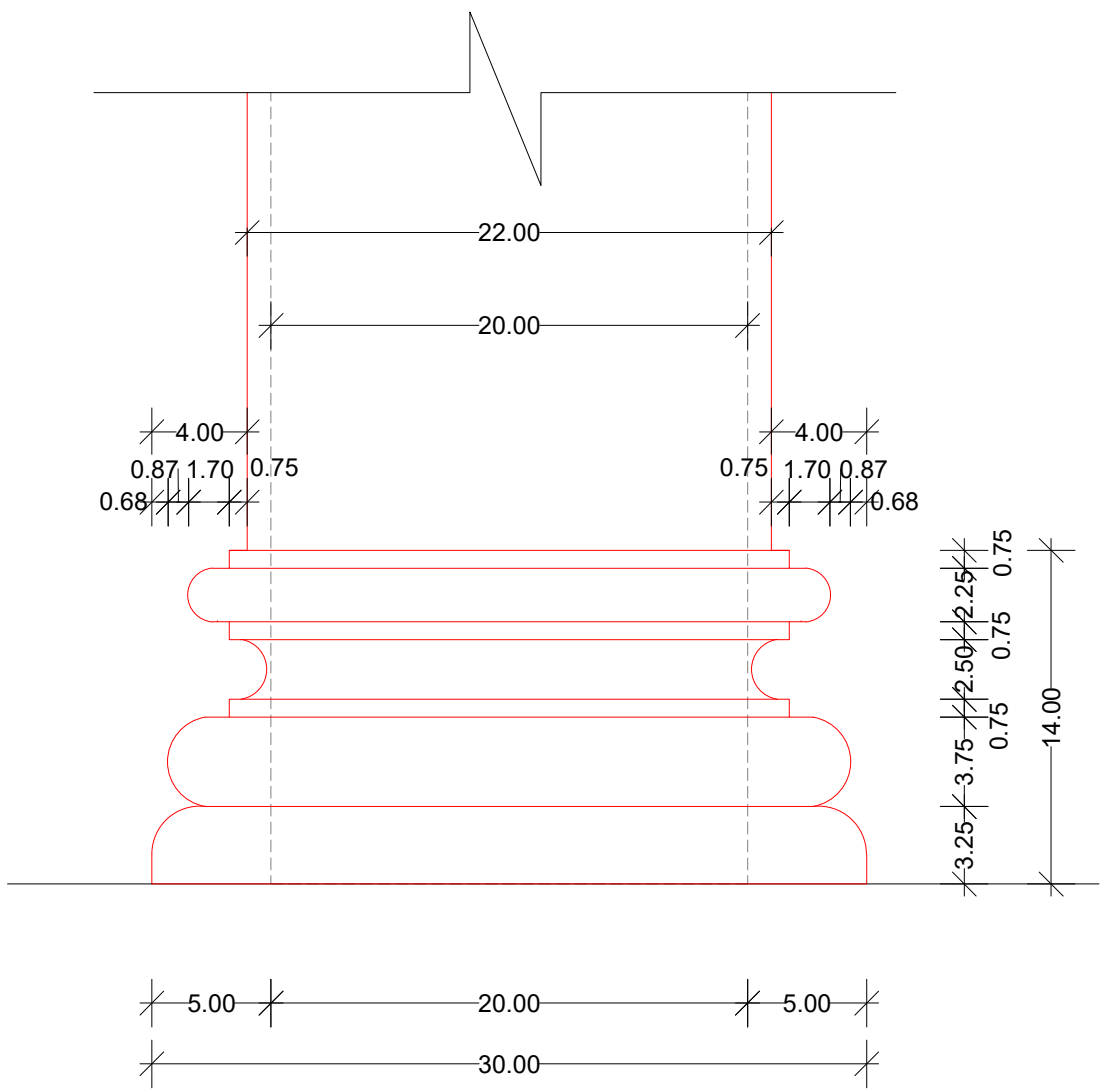


PILLAR MOLDING DETAILS

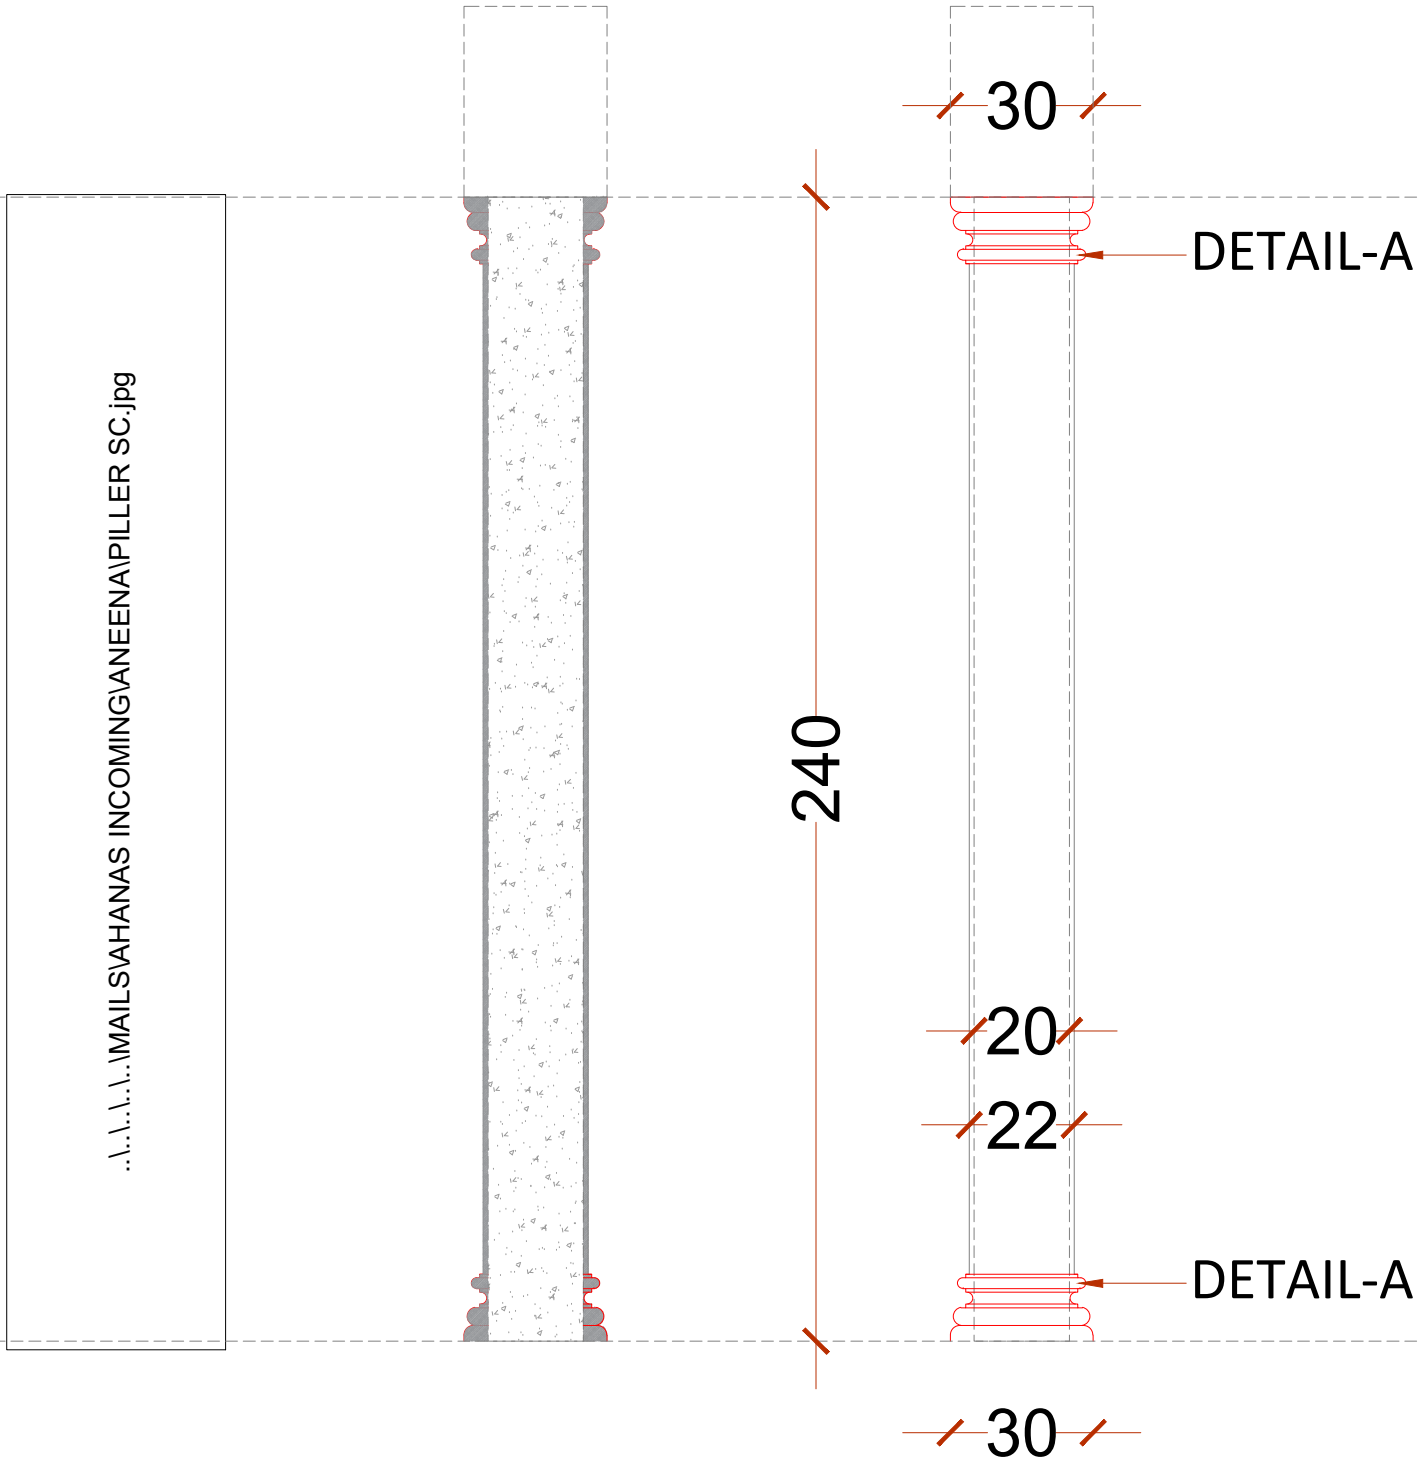

DETAIL-A

AHANAS		DATE: 06.03.2023		PROJECT: RESIDENTIAL PROJECT AT TIRUNELVELI	REVISION:	
		SCALE : NA				
		DRAWN: JJ		CLIENT: SHABREESH		
		CHECKED: JAMESLEE		DRAWING TITLE: CEMENT PILLAR DETAILING		
		PROJECT NO:563	DRAWING NO:			
			ADFS/AR/ 563/FH-13			
NOTES: ○ ALL DIMENSIONS ARE IN CMS, UNLESS OTHERWISE SPECIFIED ○ DIMENSIONS SHALL NOT BE MEASURED DIRECTLY FROM THIS DRAWINGS. FOLLOW ONLY WRITTEN DIMENSIONS ○ IN THE EVENT OF ANY DISCREPANCY OR DIFFERENCE BETWEEN ANY DRAWINGS OR SITE CONDITIONS OR OTHERWISE IMMEDIATE REFERENCE IS TO BE MADE TO THE DESIGNER FOR CLARIFICATION PRIOR TO EXECUTION OF WORK AT SITE ○ ALL THE CIVIL WORKS SHOULD BE IN LINE LEVEL AND PLUMB. ○ PLASTERING TO BE CUT AT SKIRTING LEVEL.						