



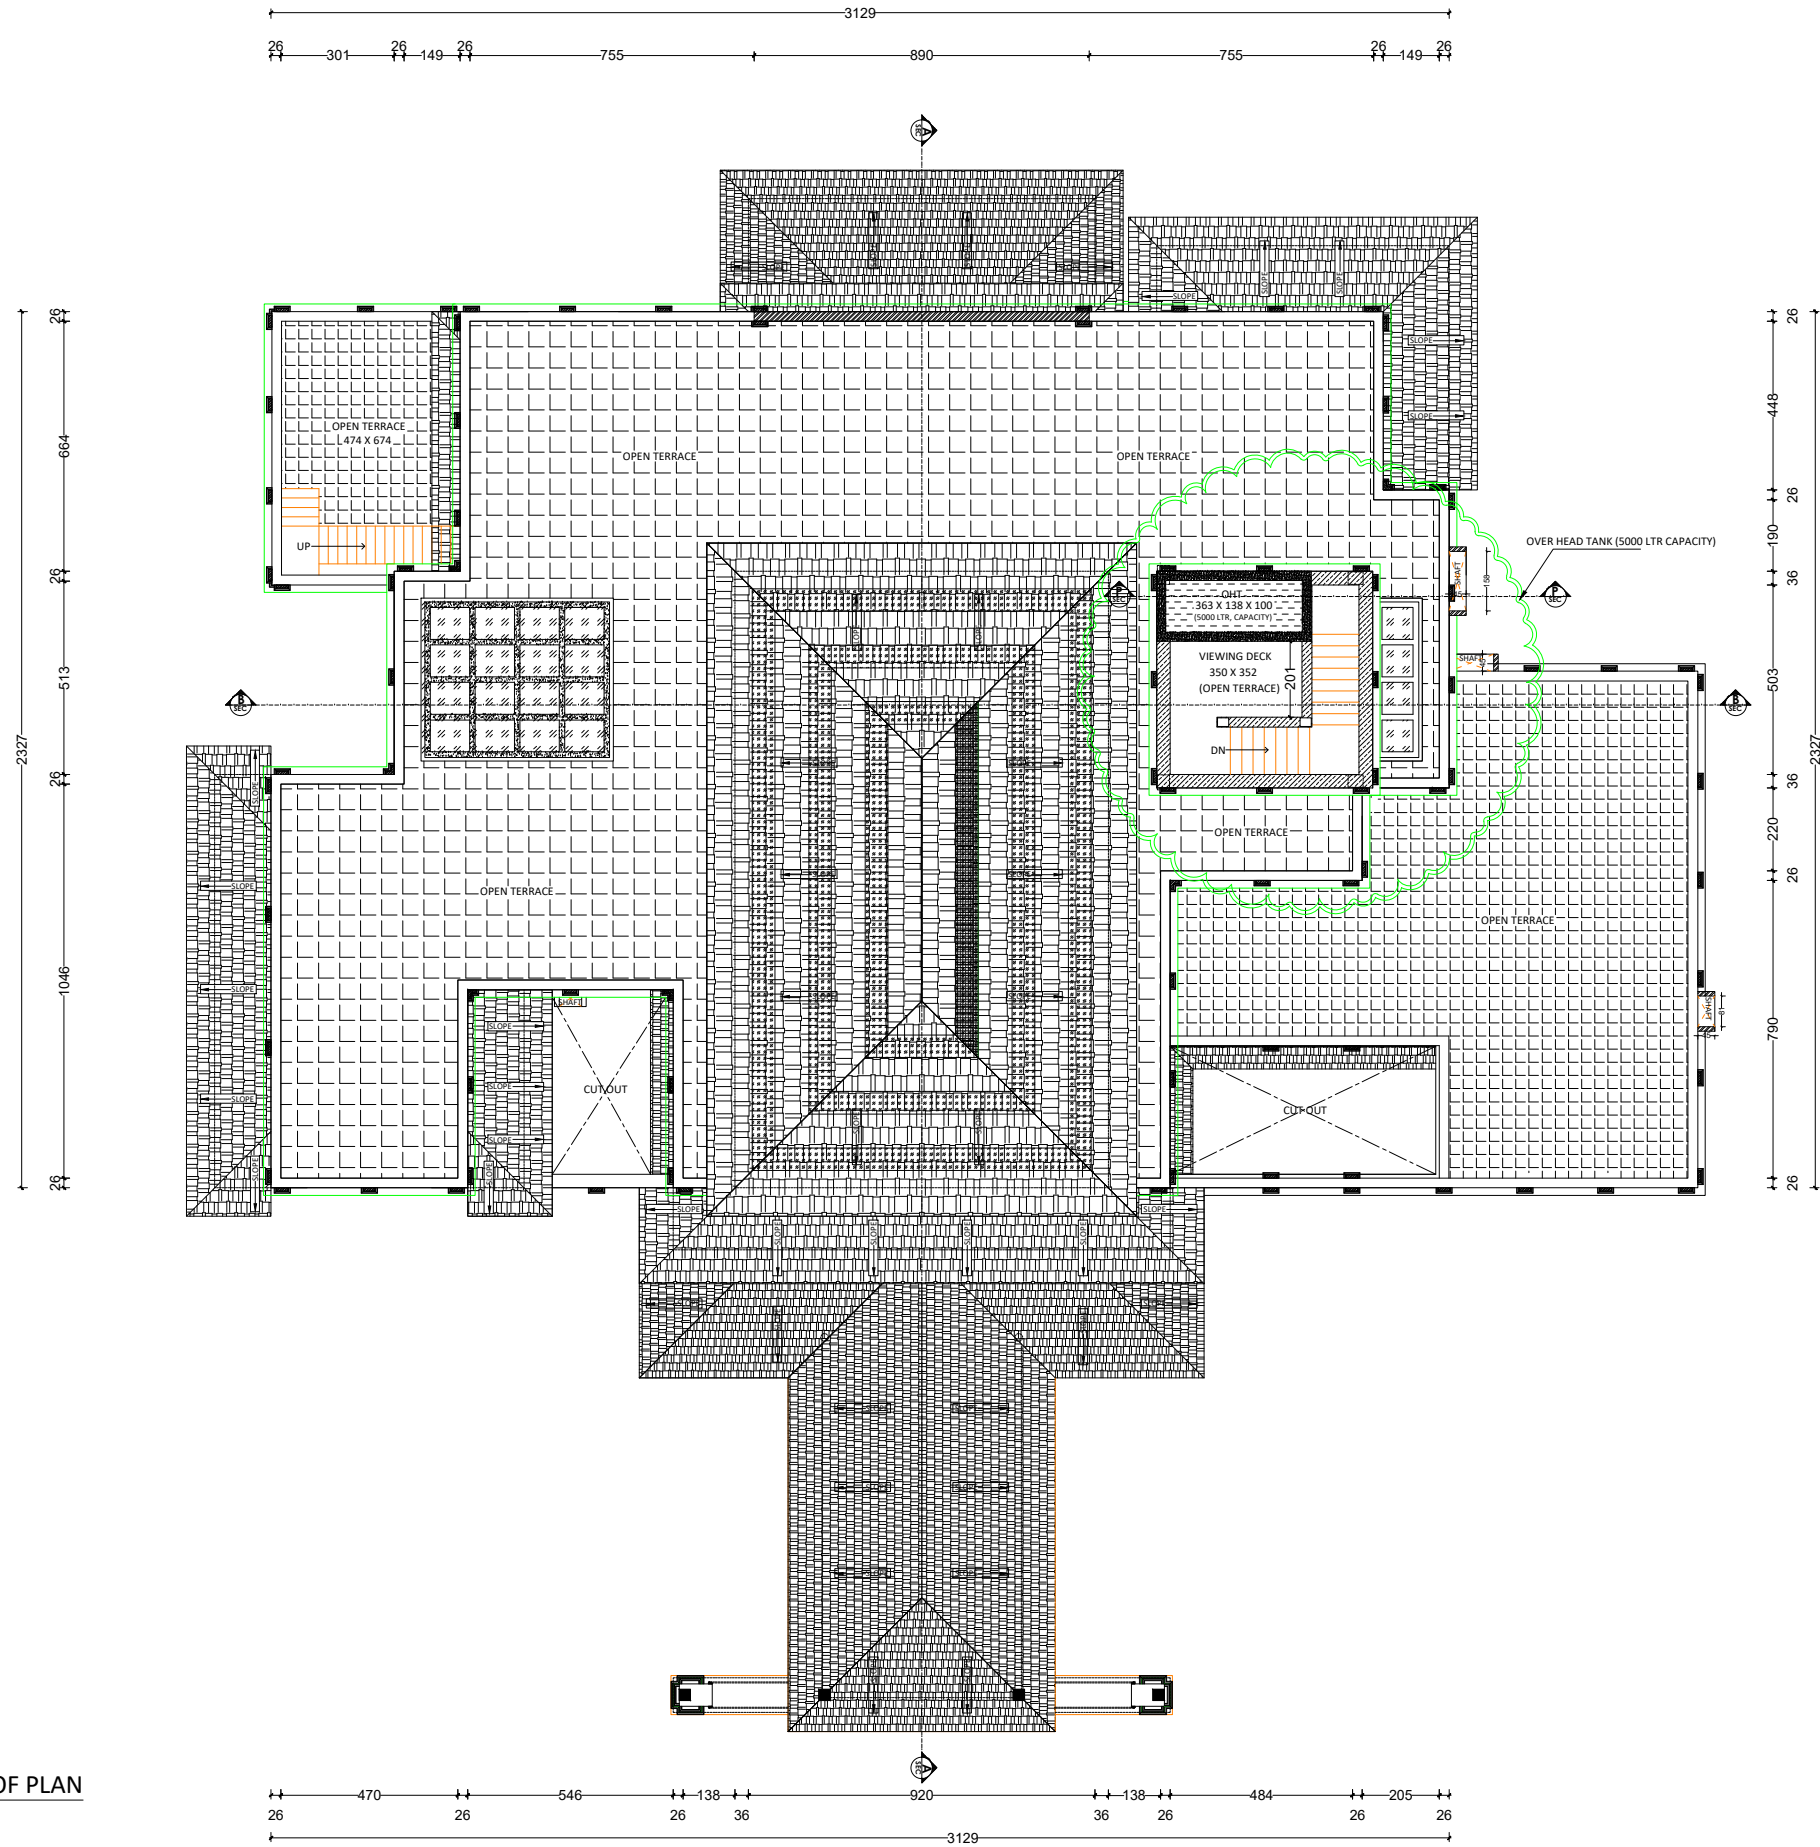

ROOF PLAN

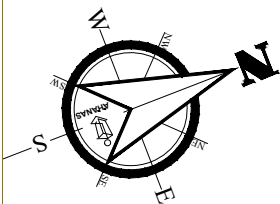

DATE: 16.03.2023	
SCALE : NA	
DRAWN: AP	
CHECKED: ANEENA	
PROJECT NO:563	DRAWING NO: ADFS/AR/ 563/FH-06

PROJECT: RESIDENTIAL PROJECT AT TIRUNELVELI	
CLIENT: SHABREESH	
DRAWING TITLE:	
ROOF PLAN	

REVISION:	
1	13-05-24- WALL EXTENSION OF TOILET FOR PROVIDING TV CHANGES IN SHAFT LOCATION/ SIZE AS PER HVAC CONSULTANT REQUIREMENT



NOTES:
○ ALL DIMENSIONS ARE IN CMS, UNLESS OTHERWISE SPECIFIED
○ DIMENSIONS SHALL NOT BE MEASURED DIRECTLY FROM THIS DRAWINGS. FOLLOW ONLY WRITTEN DIMENSIONS
○ IN THE EVENT OF ANY DISCREPANCY OR DIFFERENCE BETWEEN ANY DRAWINGS OR SITE CONDITIONS OR OTHERWISE IMMEDIATE REFERENCE IS TO BE MADE TO THE DESIGNER FOR CLARIFICATION PRIOR TO EXECUTION OF WORK AT SITE
○ ALL THE CIVIL WORKS SHOULD BE IN LINE LEVEL AND PLUMB.
○ PLASTERING TO BE CUT AT SKIRTING LEVEL.