



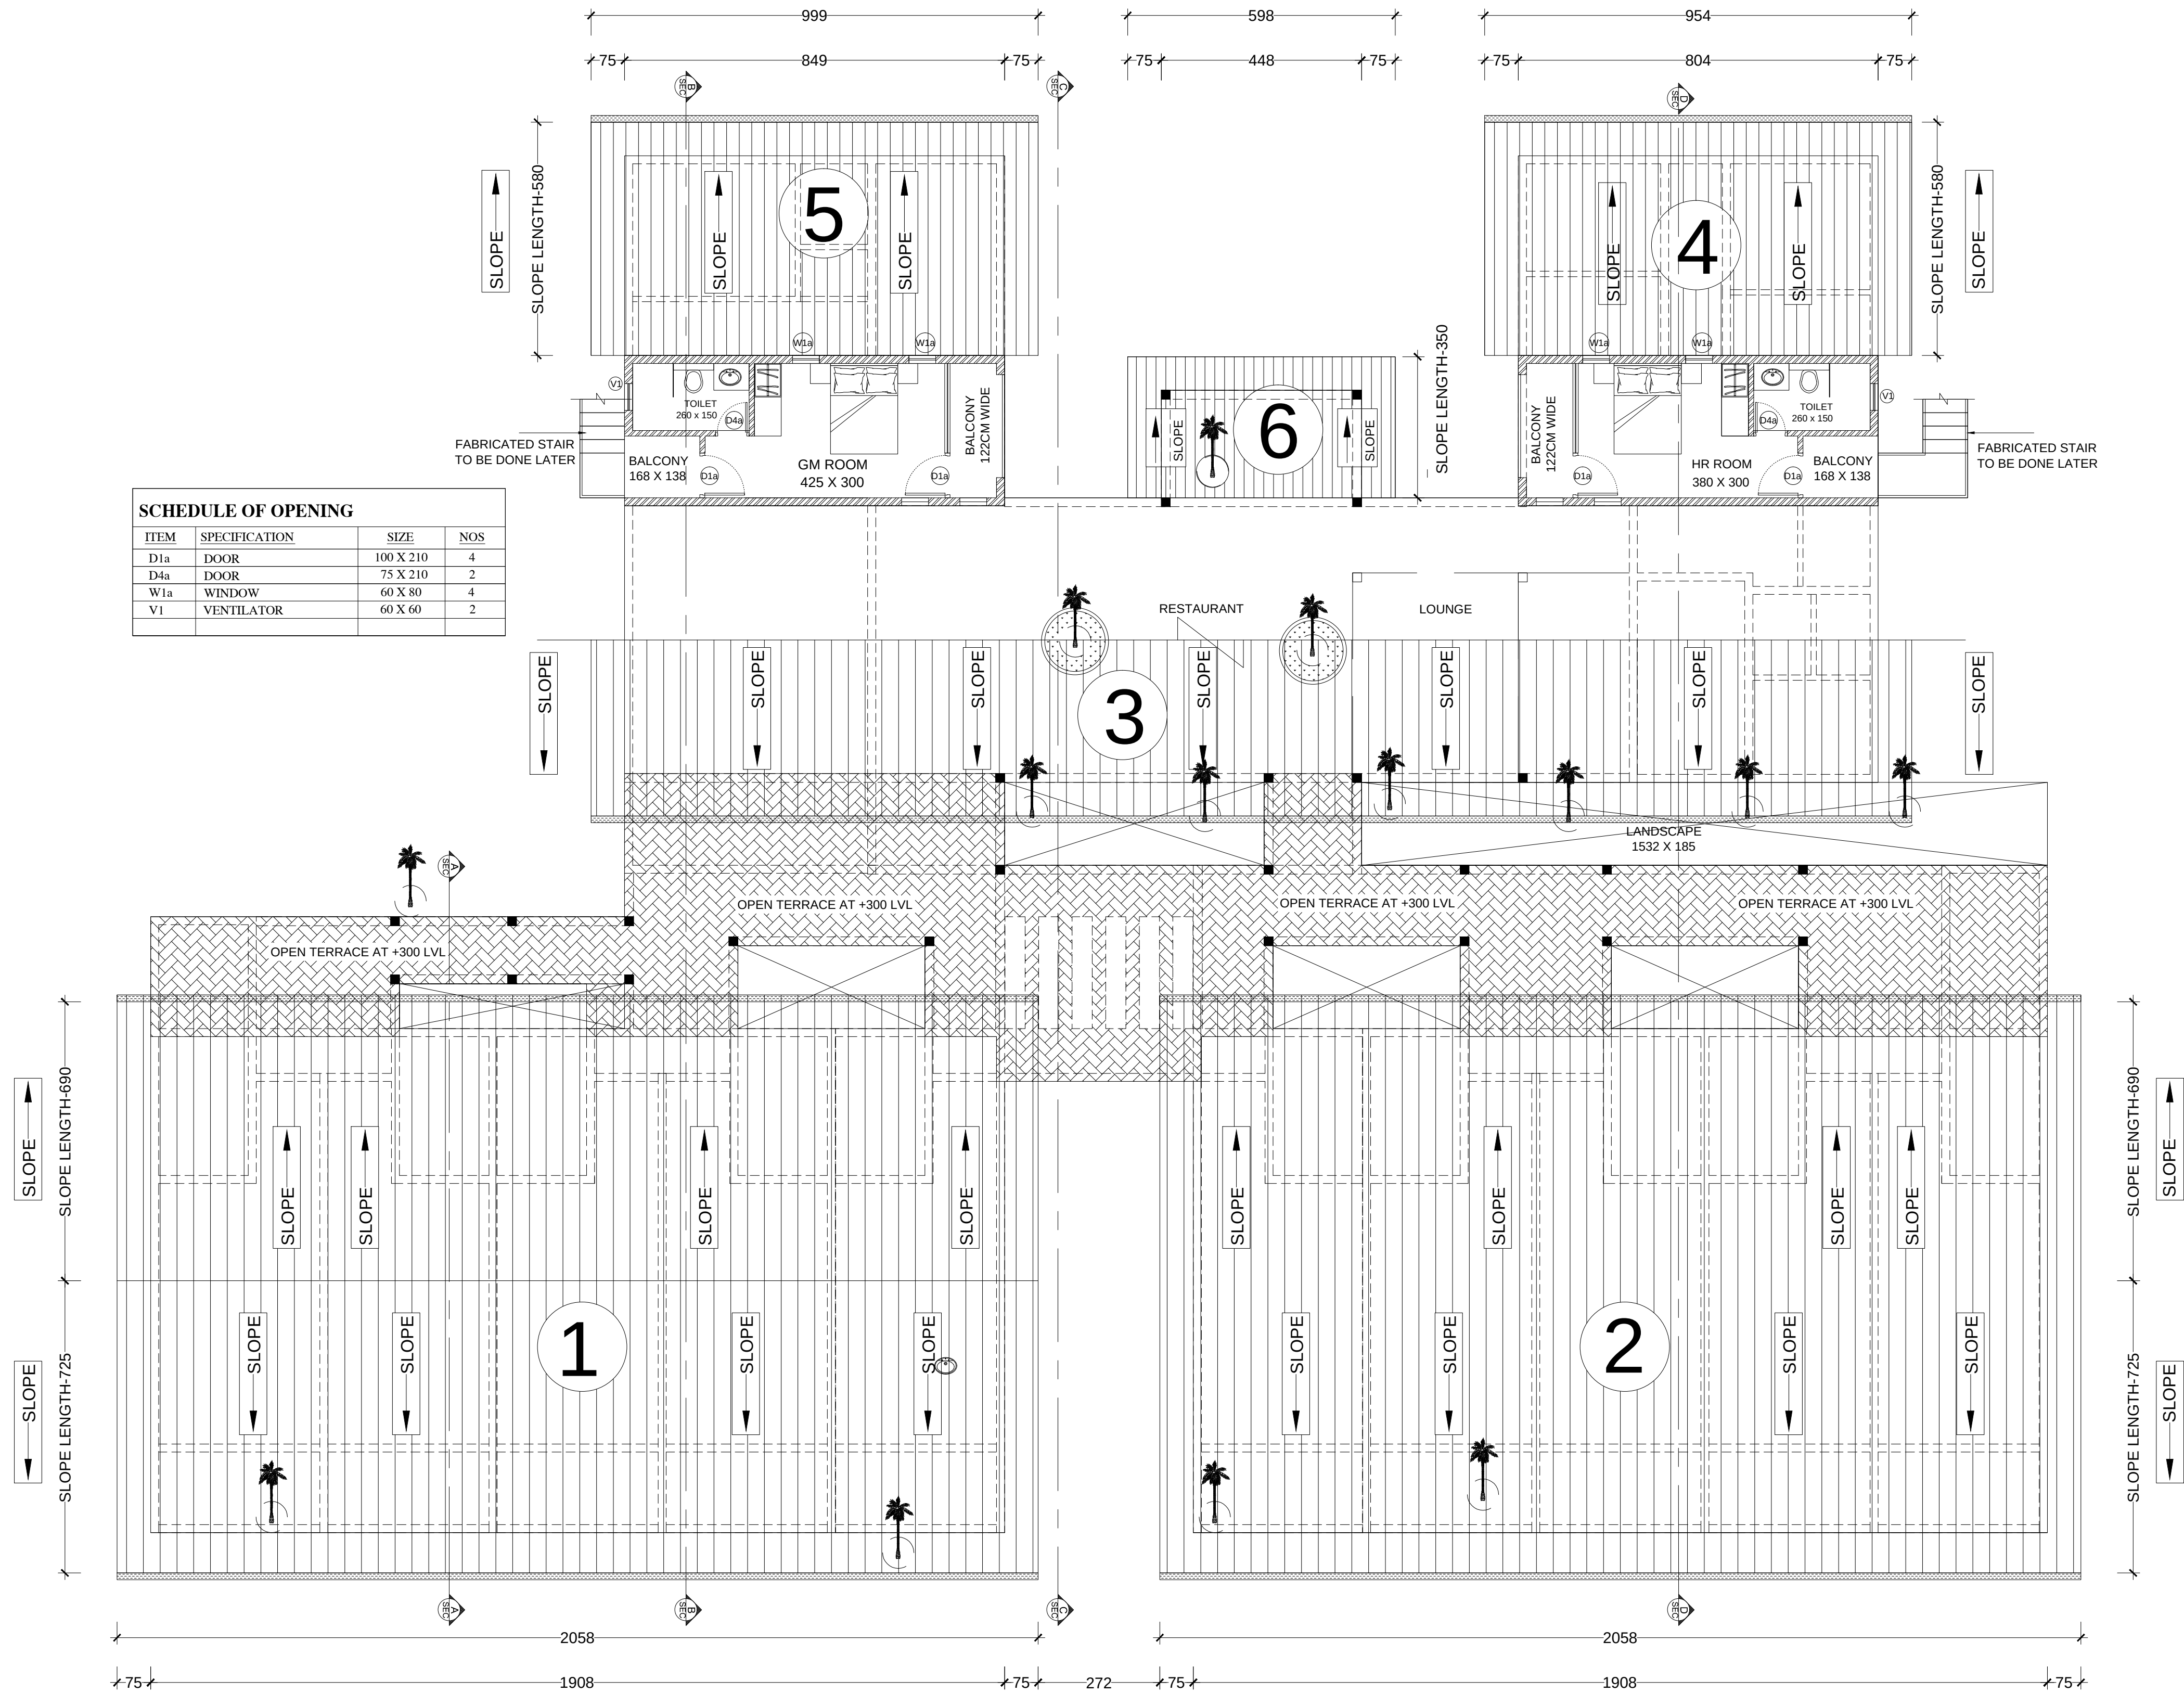

SCHEDULE OF OPENING			
ITEM	SPECIFICATION	SIZE	NOS
D1a	DOOR	100 X 210	4
D4a	DOOR	75 X 210	2
W1a	WINDOW	60 X 80	4
V1	VENTILATOR	60 X 60	2

MEZZANINE FLOOR PLAN
AREA:-55.54M2(597 SQFT)

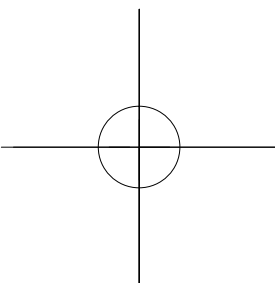

DATE: 01-5-2018

SCALE : Nts

DRAWN: Jameslee

CHECKED: Aneena

PROJ.NO- SPL 48


CLIENT: Mr. MUTHUKOYA

PROJECT : TOURIST HOME ,
AGATTI

DRAWING TITLE:
MEZZANINE FLOOR PLAN

REVISION:

- FOUNDATION REVISED IN TO FOOTING & PLINTH BEAM
AS PER CLIENT REQUEST DUE TO MATERIAL AVAILABILITY
(21-02-19)
- AS PER CLIENT REQUEST LAYOUT CHANGED 18-05-19
(FOR LIMITING CUTTING OF COCONUT TREES)

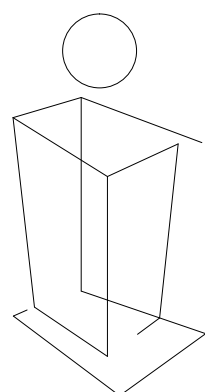

AHANAS

ALL DIMENSIONS ARE IN CMS
NO DIMENSIONS TO BE SCALED OFF FROM
DRAWINGS ONLY WRITTEN DIMENSIONS TO BE

IN THE EVENT OF ANY DISCREPANCY OR
DIFFERENCE BETWEEN ANY INTERIOR DRAWINGS
OR SITE CONDITIONS OR OTHERWISE IMMEDIATE
REFERENCE IS TO BE MADE TO THE DESIGNER
FOR CLARIFICATION PRIOR TO EXECUTION OF
WORK AT SITE

AREA :