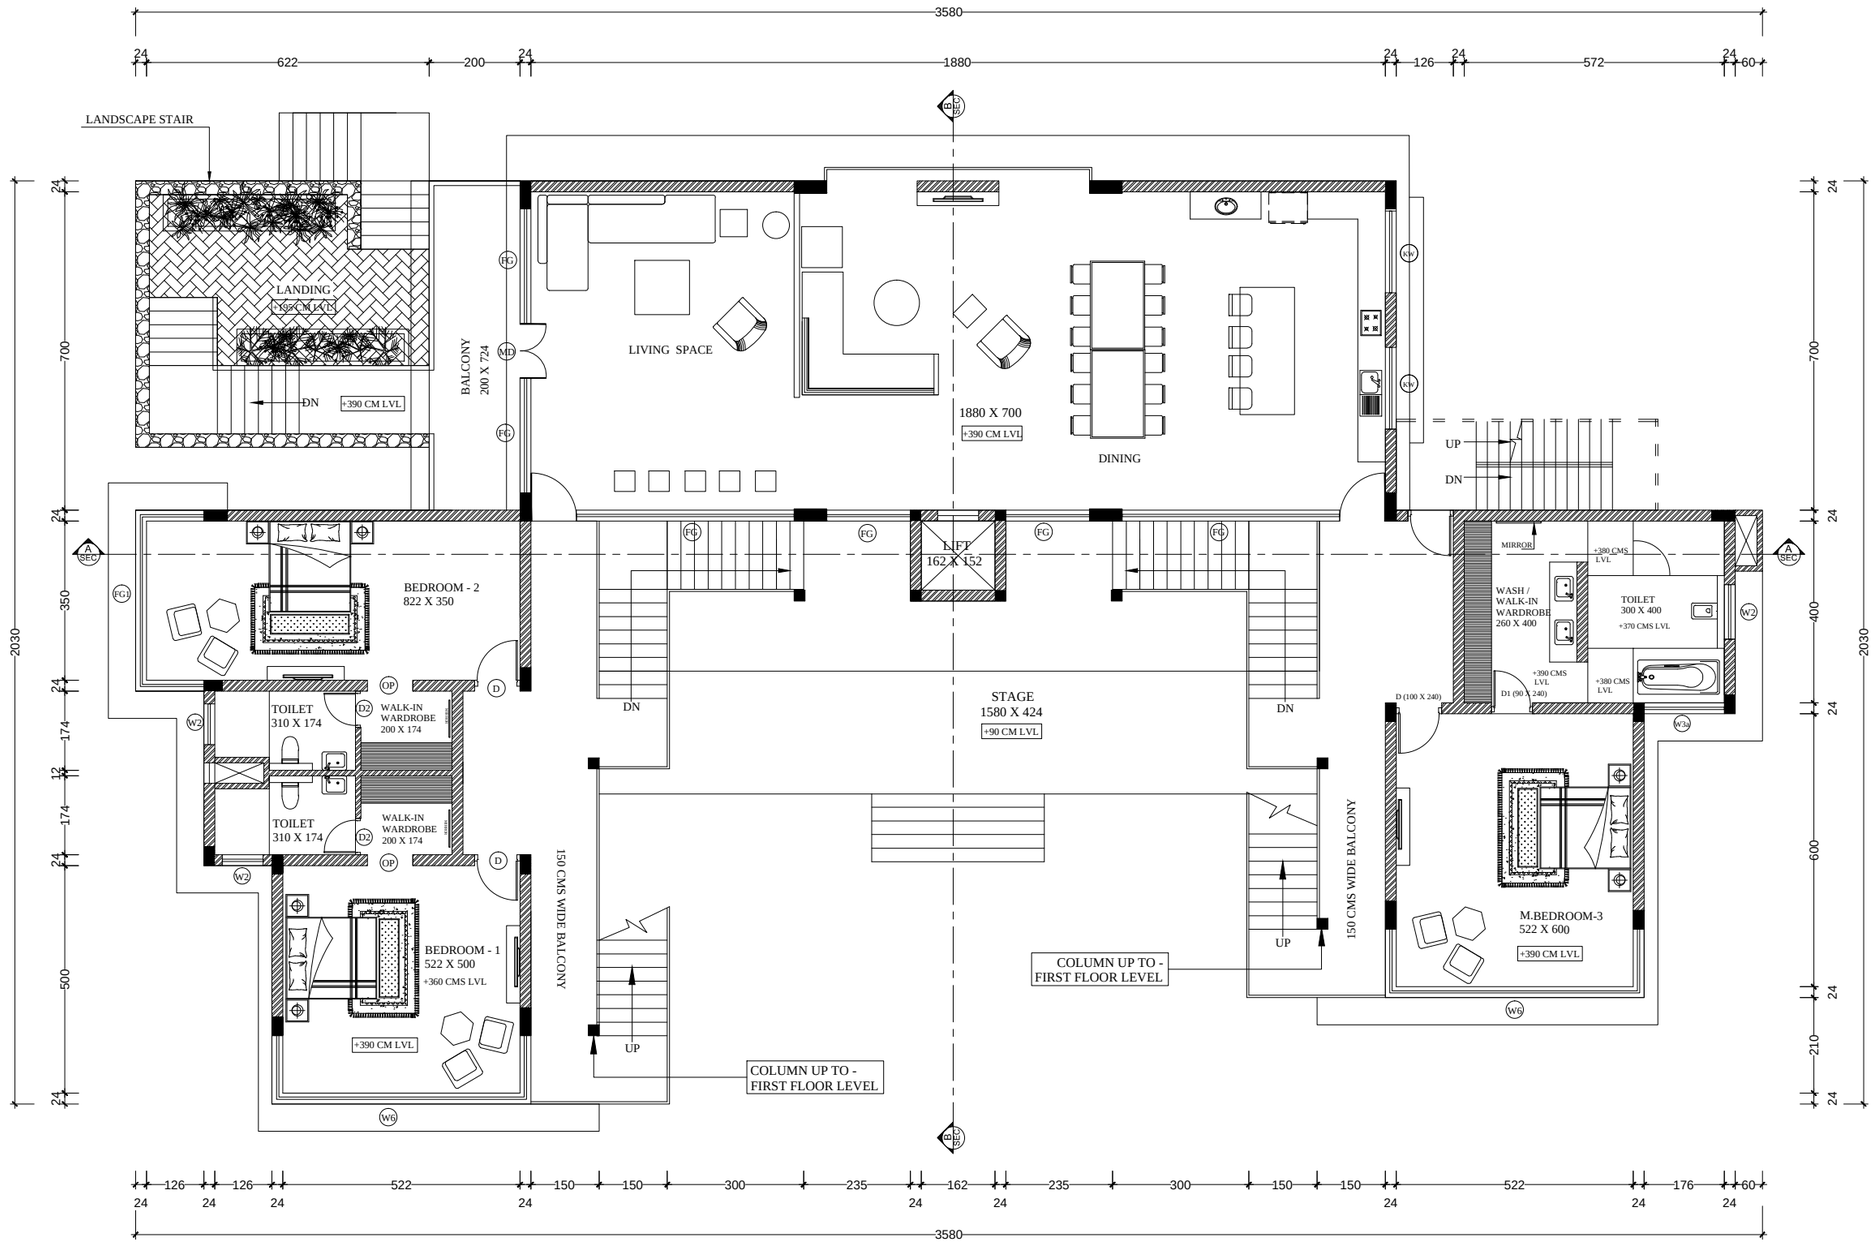


# FIRST FLOOR PLAN

| | | | |
|---|---|---|---|
| DATE: 12.07.2019 | CLIENT: ABEESH MUHAMMAD | REVISION: | ALL DIMENSIONS ARE IN CMS |
| SCALE : NA | | 1 REV. AS PER CLIENT REQUIREMENT - 1.4.19 | NO DIMENSIONS TO BE SCALED OFF FROM DRAWINGS ONLY WRITTEN DIMENSIONS TO BE |
| DRAWN:JJ | PROJECT: RESIDENTIAL PROJECT AT VAYALKKARA, MANJALY | 2 REV. FOR BALCONY AS PER CLIENT REQUIREMENT - 3.4.19 | IN THE EVENT OF ANY DISCREPANCY OR DIFFERENCE BETWEEN ANY INTERIOR DRAWINGS OR SITE CONDITIONS OR OTHERWISE IMMEDIATE REFERENCE IS TO BE MADE TO THE DESIGNER FOR CLARIFICATION PRIOR TO EXECUTION OF WORK AT SITE |
| CHECKED: ANEENA | | | |
| PROJECT NO: | DRAWING TITLE: FIRST FLOOR | | |

N E W S

AHANAS