





GROUND FLOOR PLAN -COLUMN LAYOUT

Note:- C1 columns up to plinth beam only

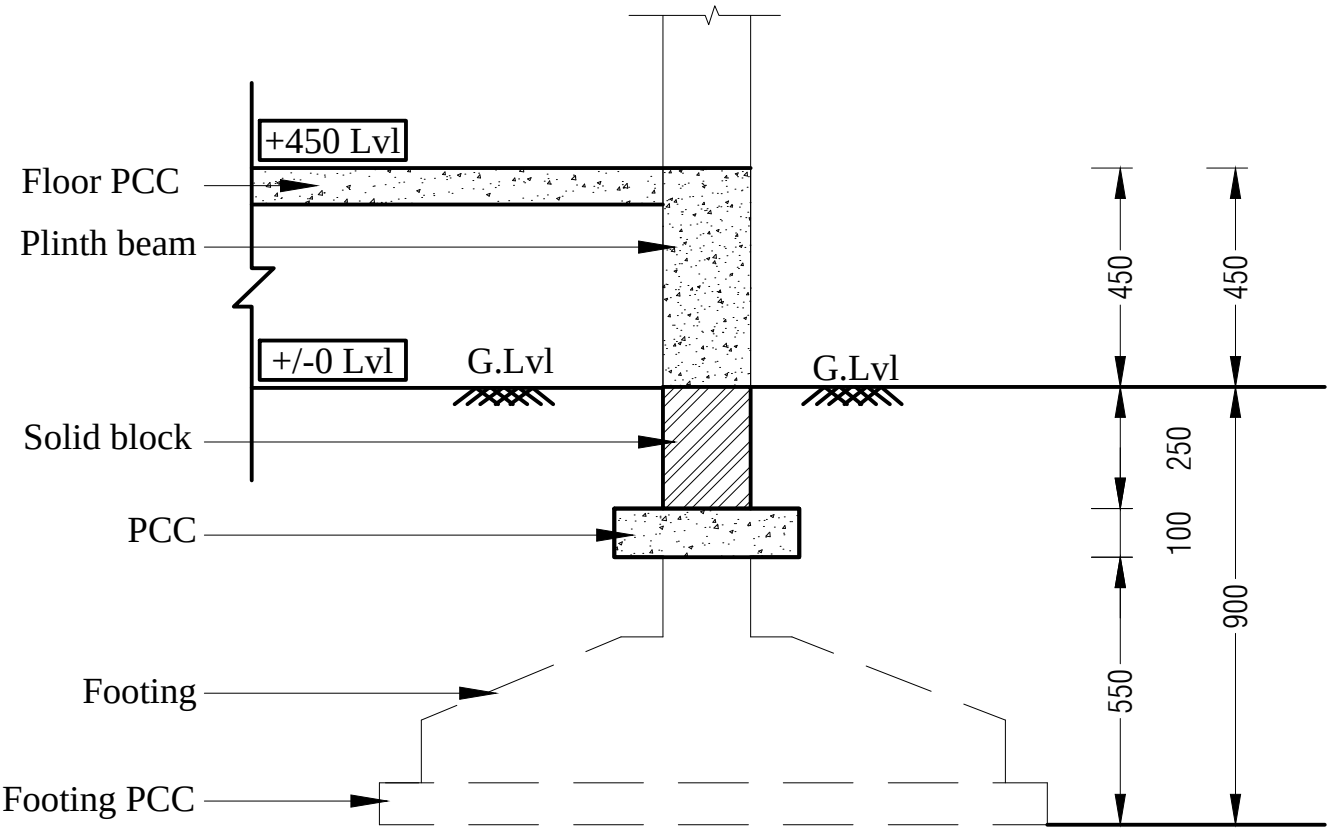

SECTION ALONG-PB(200 x 450)

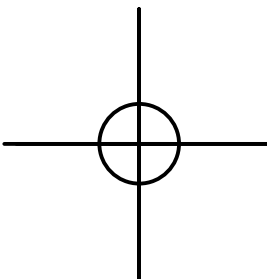

DATE: 08-2-2019
SCALE : Nts
DRAWN: Jameslee
CHECKED: Aneena
PROJ.NO- SPL 48

CLIENT: Mr. MUTHUKOYA
PROJECT : TOURIST HOME , AGATTI
DRAWING TITLE: GROUND FLOOR PLAN-COLUMN LAYOUT

REVISION:
1, FOUNDATION REVISED IN TO FOOTING & PLINTH BEAM AS PER CLIENT REQUEST DUE TO MATERIAL AVAILABILITY (21-02-19)
2, AS PER CLIENT REQUEST LAYOUT CHANGED 18-05-19 (FOR LIMITING CUTTING OF COCONUT TREES)



ALL DIMENSIONS ARE IN CMS
NO DIMENSIONS TO BE SCALED OFF FROM
DRAWINGS ONLY WRITTEN DIMENSIONS TO BE
IN THE EVENT OF ANY DISCREPANCY OR
DIFFERENCE BETWEEN ANY INTERIOR DRAWINGS
OR SITE CONDITIONS OR OTHERWISE IMMEDIATE
REFERENCE IS TO BE MADE TO THE DESIGNER
FOR CLARIFICATION PRIOR TO EXECUTION OF
WORK AT SITE

AREA :