

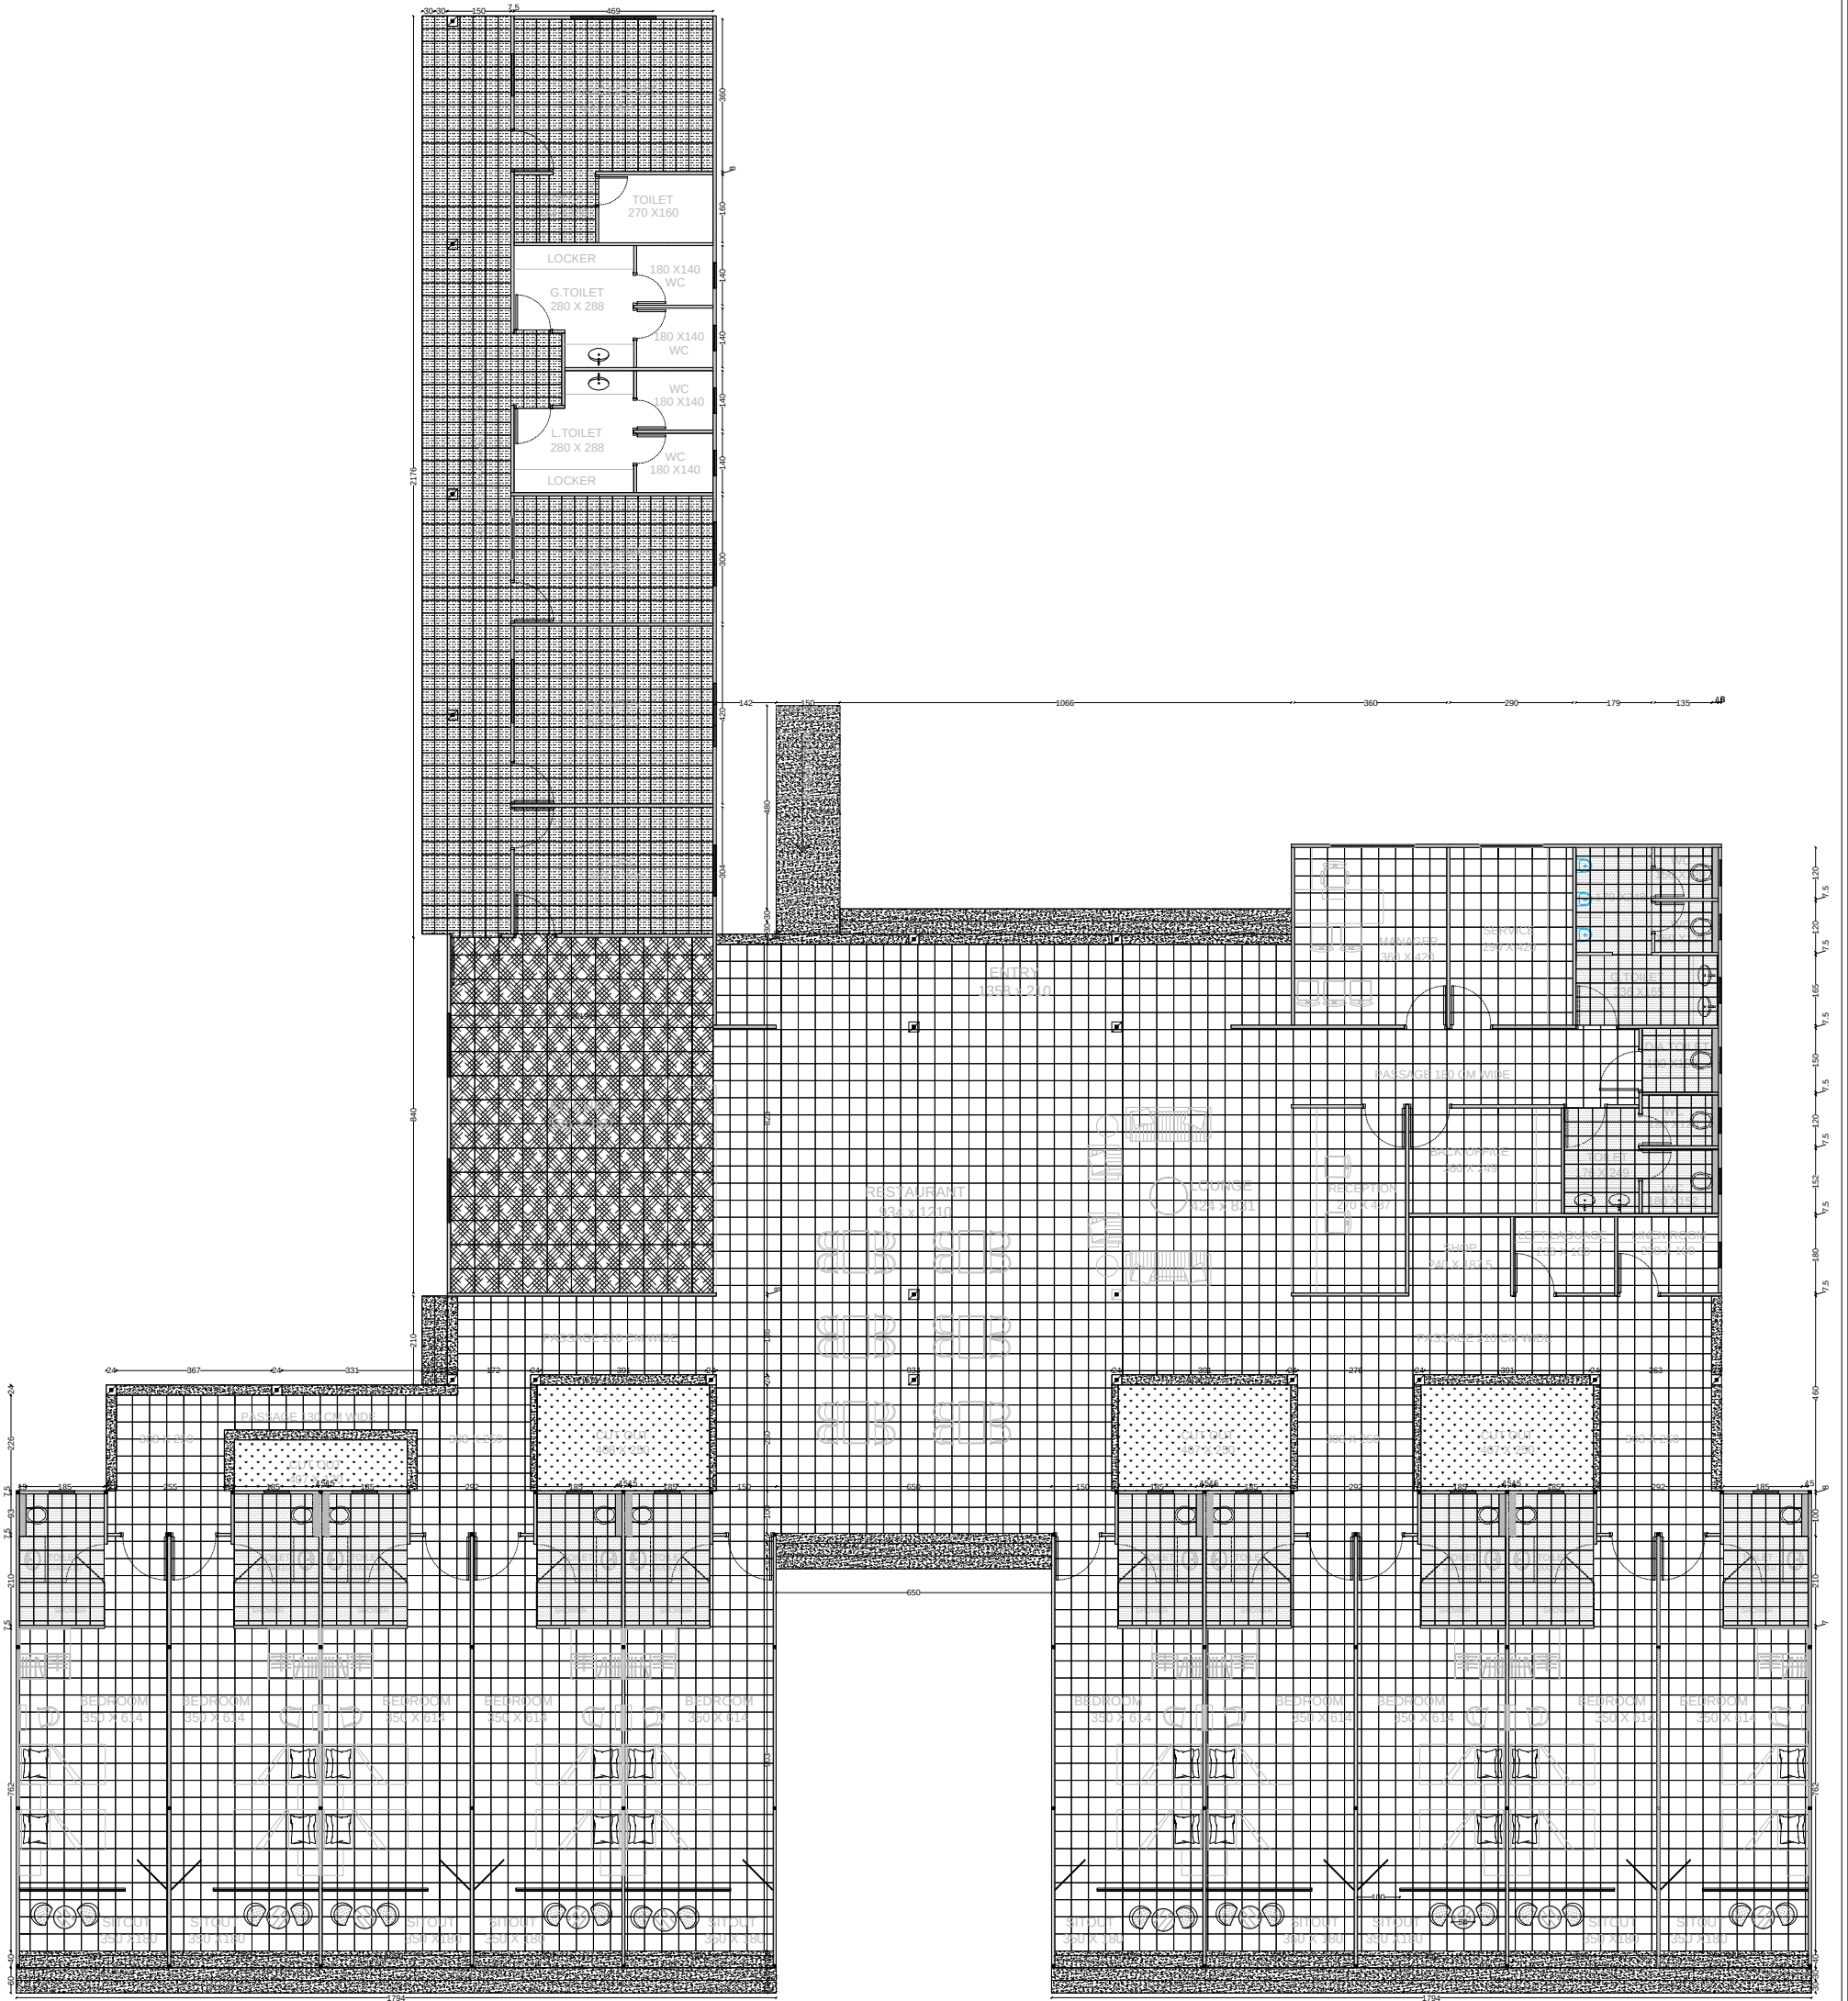


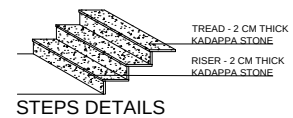

GROUND FLOOR PLAN :-986.91 M2(10619 SQFT)

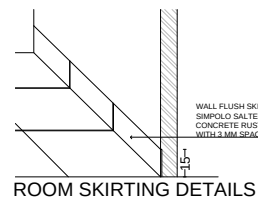

	SIMPOLO - SALTED CONCRETE RUST 10MM WITH 3 MM SPACER 40x40CM
	2 CM THICK KADAPPA STONE
	VR 86387 33x33 CM
	2 CM THICK KOTTAH STONE SEMI POLISHED 57x57CM
	30x30 CM ENDURA TERRACOTTA TILE

	DATE: 28-05-2018	CLIENT: Mr. MUTHUKOYA	REVISION:		ALL DIMENSIONS ARE IN CMS NO DIMENSIONS TO BE SCALED OFF FROM DRAWINGS ONLY WRITTEN DIMENSIONS TO BE IN THE EVENT OF ANY DISCREPANCY OR DIFFERENCE BETWEEN ANY INTERIOR DRAWINGS OR SITE CONDITIONS OR OTHERWISE IMMEDIATE REFERENCE IS TO BE MADE TO THE DESIGNER FOR CLARIFICATION PRIOR TO EXECUTION OF WORK AT SITE	AREA :
	SCALE: 1:150	PROJECT: TOURIST HOME AT AGATTI				
	DRAWN: NA	DRAWING TITLE: FLOORING LAYOUT				
	CHECKED:					
	PROJECT NO:					