



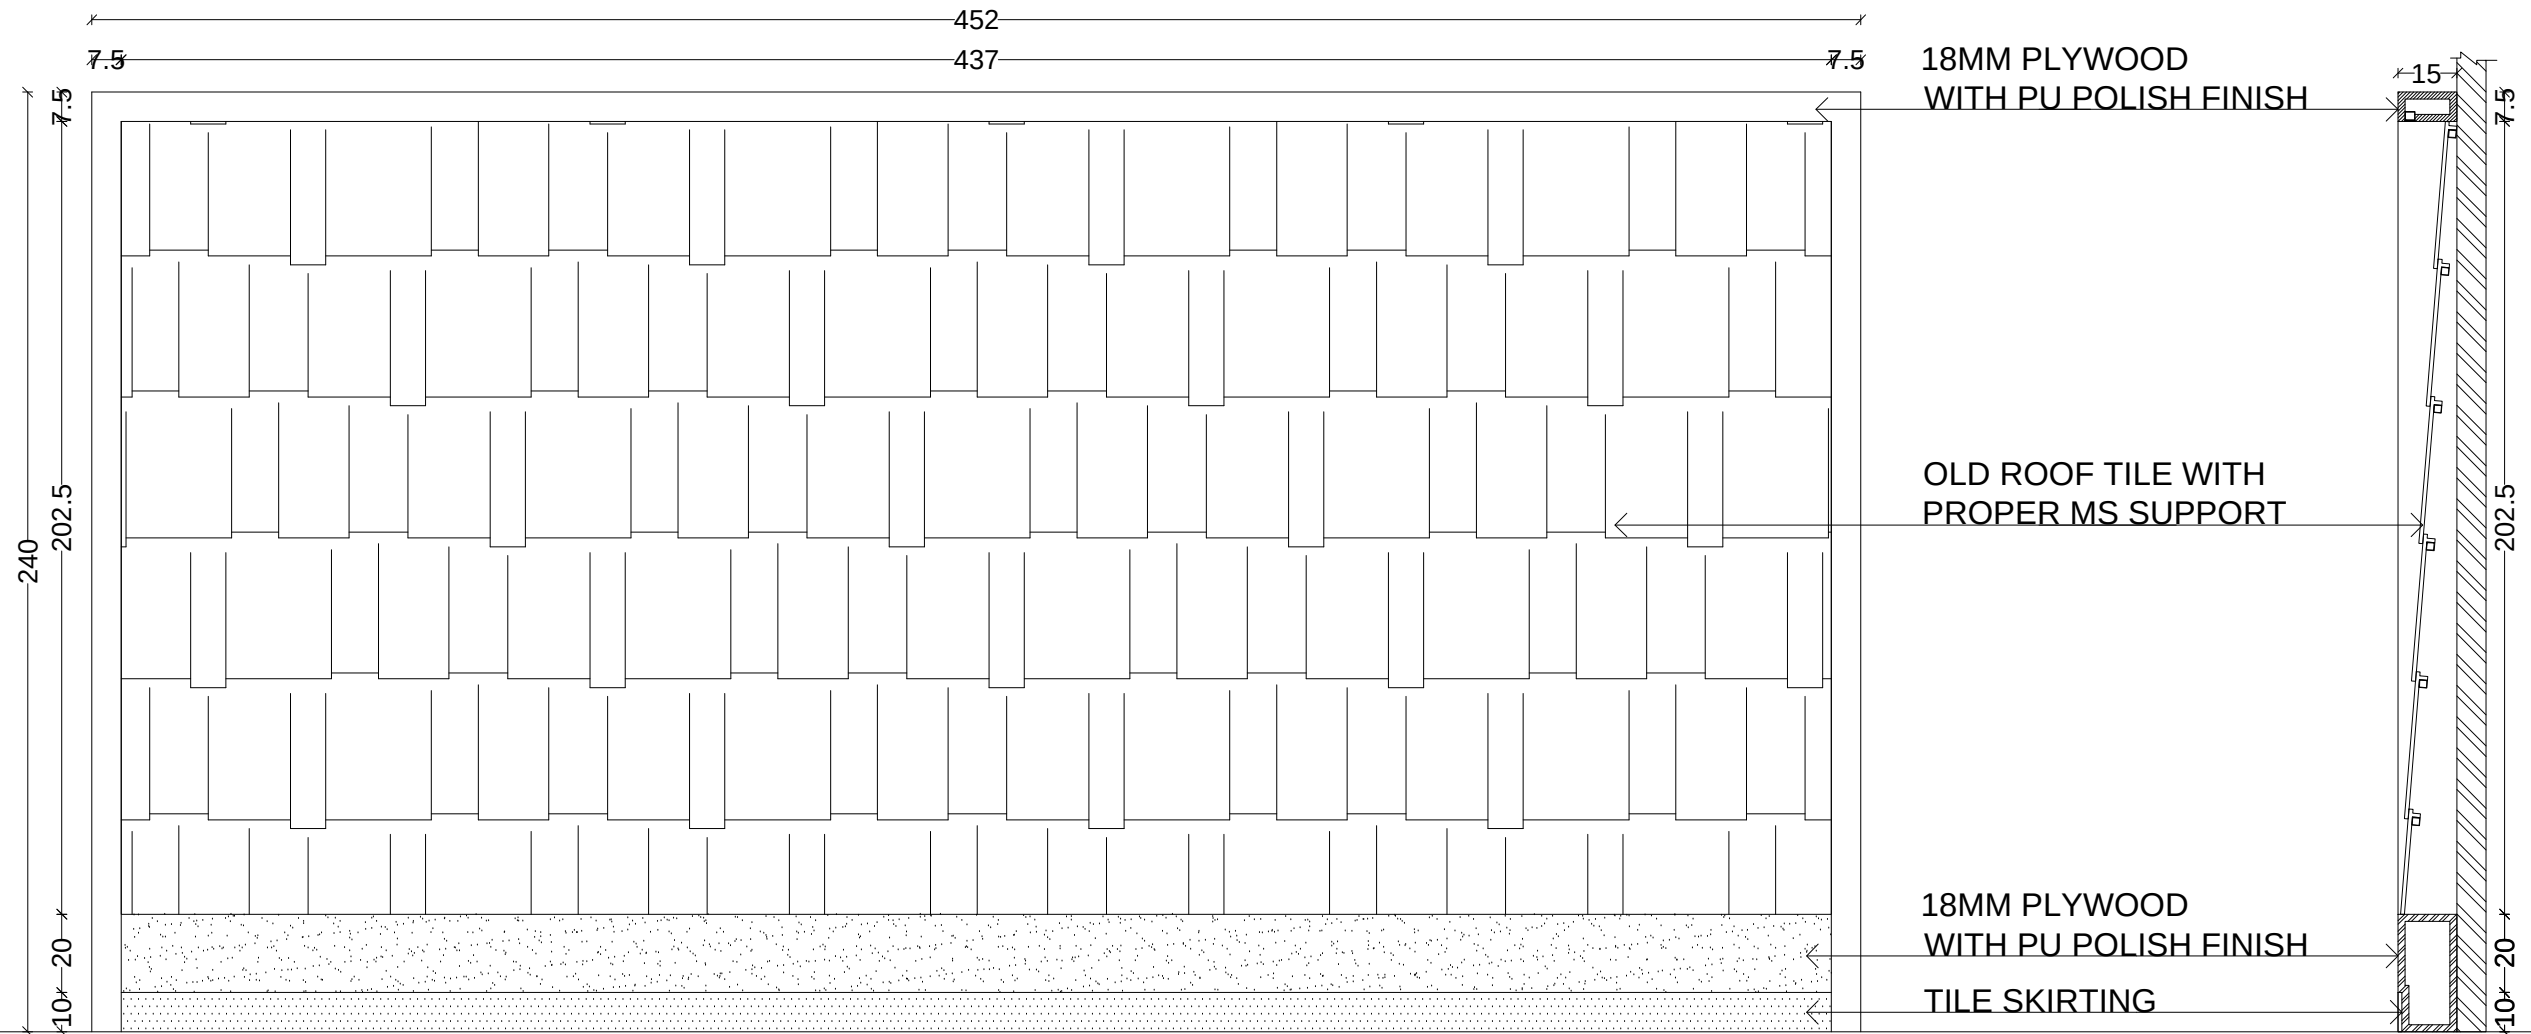

FRONT ELEVATION

SECTION AA

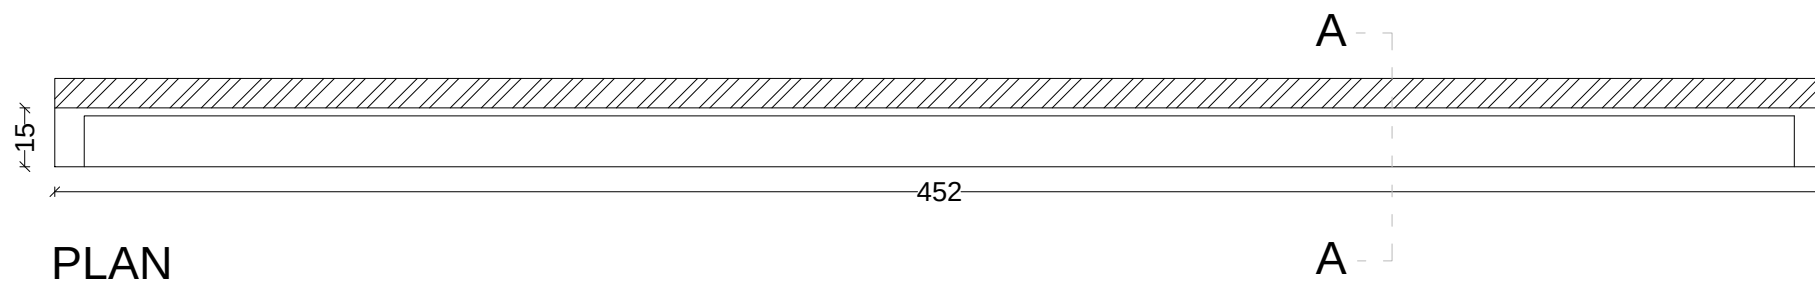

PLAN



PROJECT: TOURIST HOME STAY AGATTI	DWG TITLE: RECEPTION BACK SPLASH	DRAWN: NILUFER	REVISED DATE:	ALL DIMENSIONS ARE IN CMS No dimensions to be scaled off from the drawings only written dimensions to be. In the event of any discrepancy or difference between any interior drawings or site conditions or other wise immediate reference is to be made to the designer for clarification prior to execution of work at site
DWG NO: 2	DATE: 21.06.2018	CHECKED: NA	REVISION NO:	
REVISION:			SCALE: 1:25	