


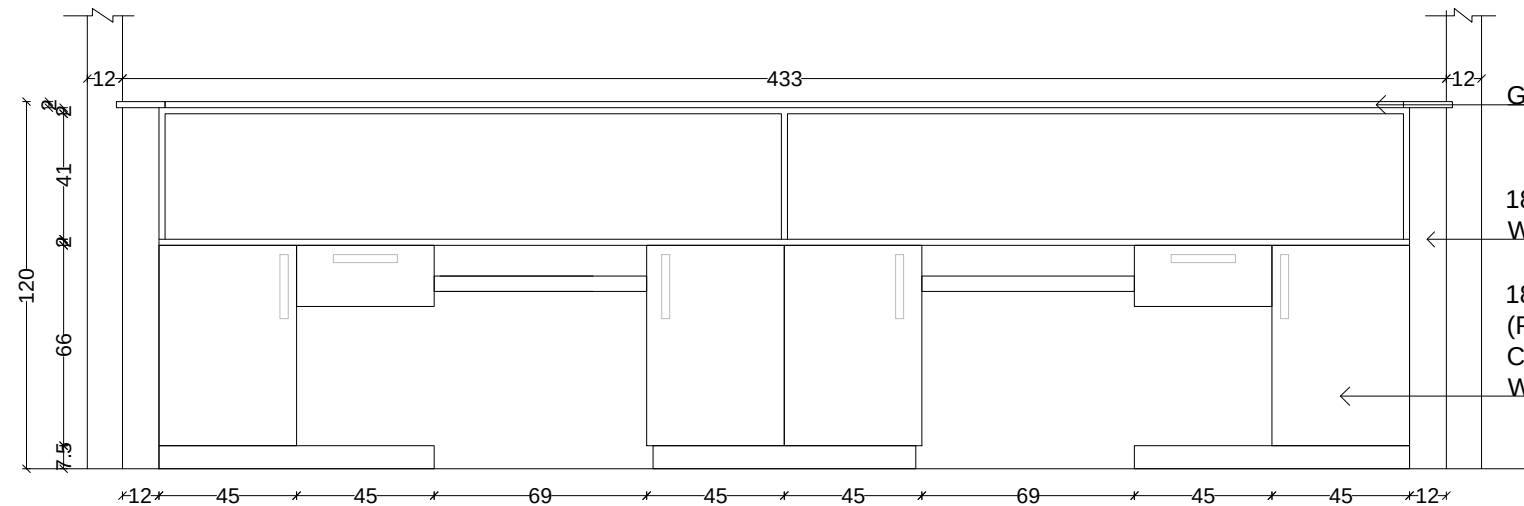


REAR ELEVATION


GRANITE / TILE TOP

18MM PLYWOOD WITH PU POLISH FINISH

18MM PLYWOOD DOOR (PROVIDE MATCHING COLOR EDGE BAND) WITH PU POLISH FINISH

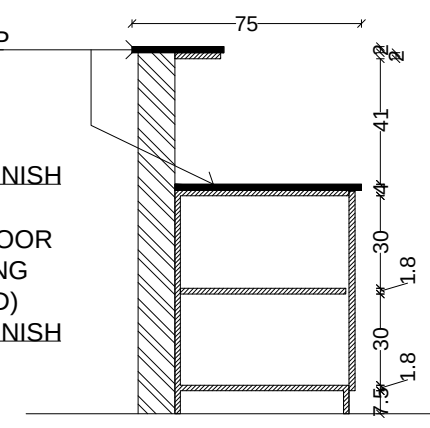


SECTION CC

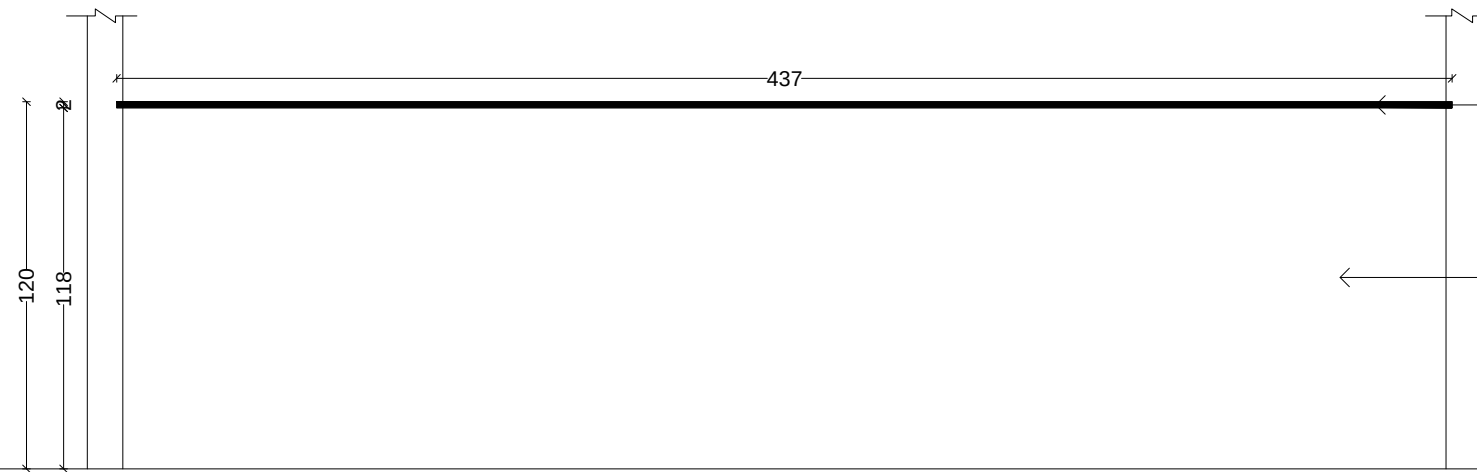


FRONT ELEVATION

GRANITE / TILE TOP


WHITE EMULSION PAINT FINISH

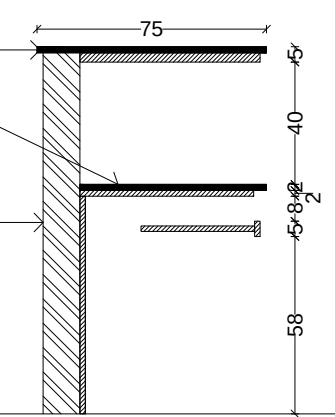

SECTION BB

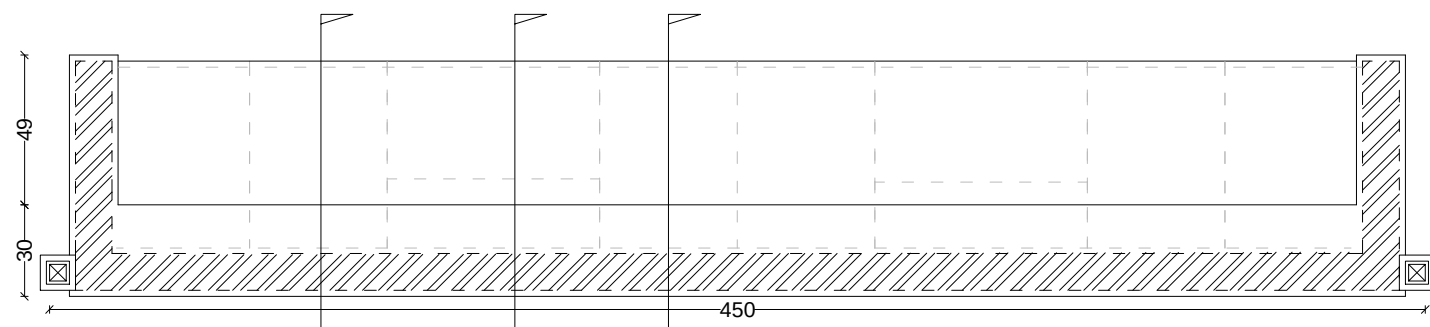

PLAN

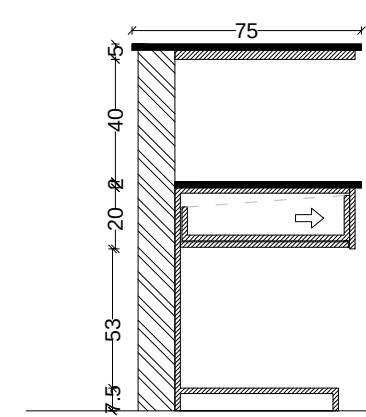

SECTION AA

	PROJECT: TOURIST HOME STAY AGATTI	DWG TITLE: RECEPTION TABLE DETAIL	DRAWN: NILUFER	REVISED DATE:	ALL DIMENSIONS ARE IN CMS No dimensions to be scaled off from the drawings only written dimensions to be. In the event of any discrepancy or difference between any interior drawings or site conditions or other wise immediate reference is to be made to the designer for clarification prior to execution of work at site
	DWG NO: 1	DATE: 21.06.2018	CHECKED: NA	REVISION NO:	
	REVISION:			SCALE: 1:40	