



ROOF AREA DETAILS (ACTUAL)		
No.	AREA	
	M2	SQFT
①	291.21	3133.42
②	291.21	3133.42
③	319.19	3434.38
④	55.33	595.35
⑤	57.94	623.43
⑥	20.93	225.20
⑦	6.60 (Shade)	71.02
TOTAL	1042.41	11216.22
COLOR- GRAY (50MM THICK)		

ROOF SHEET DETAILS -AGATTI			
SL.NO	LENGTH	WIDTH	NOS
1,	7.25 M	1	42 NOS
2,	6.90 M	1	42 NOS
3a,	8.50 M	1	10 NOS
3b,	12.00 M	1	20 NOS
4,	5.80 M	1	10 NOS
5,	5.80 M	1	10 NOS
6,	3.50 M	1	6+2+2 NOS
PUFF PANEL-50MM THICK (ALUMINIUM) COLOUR-GREY			

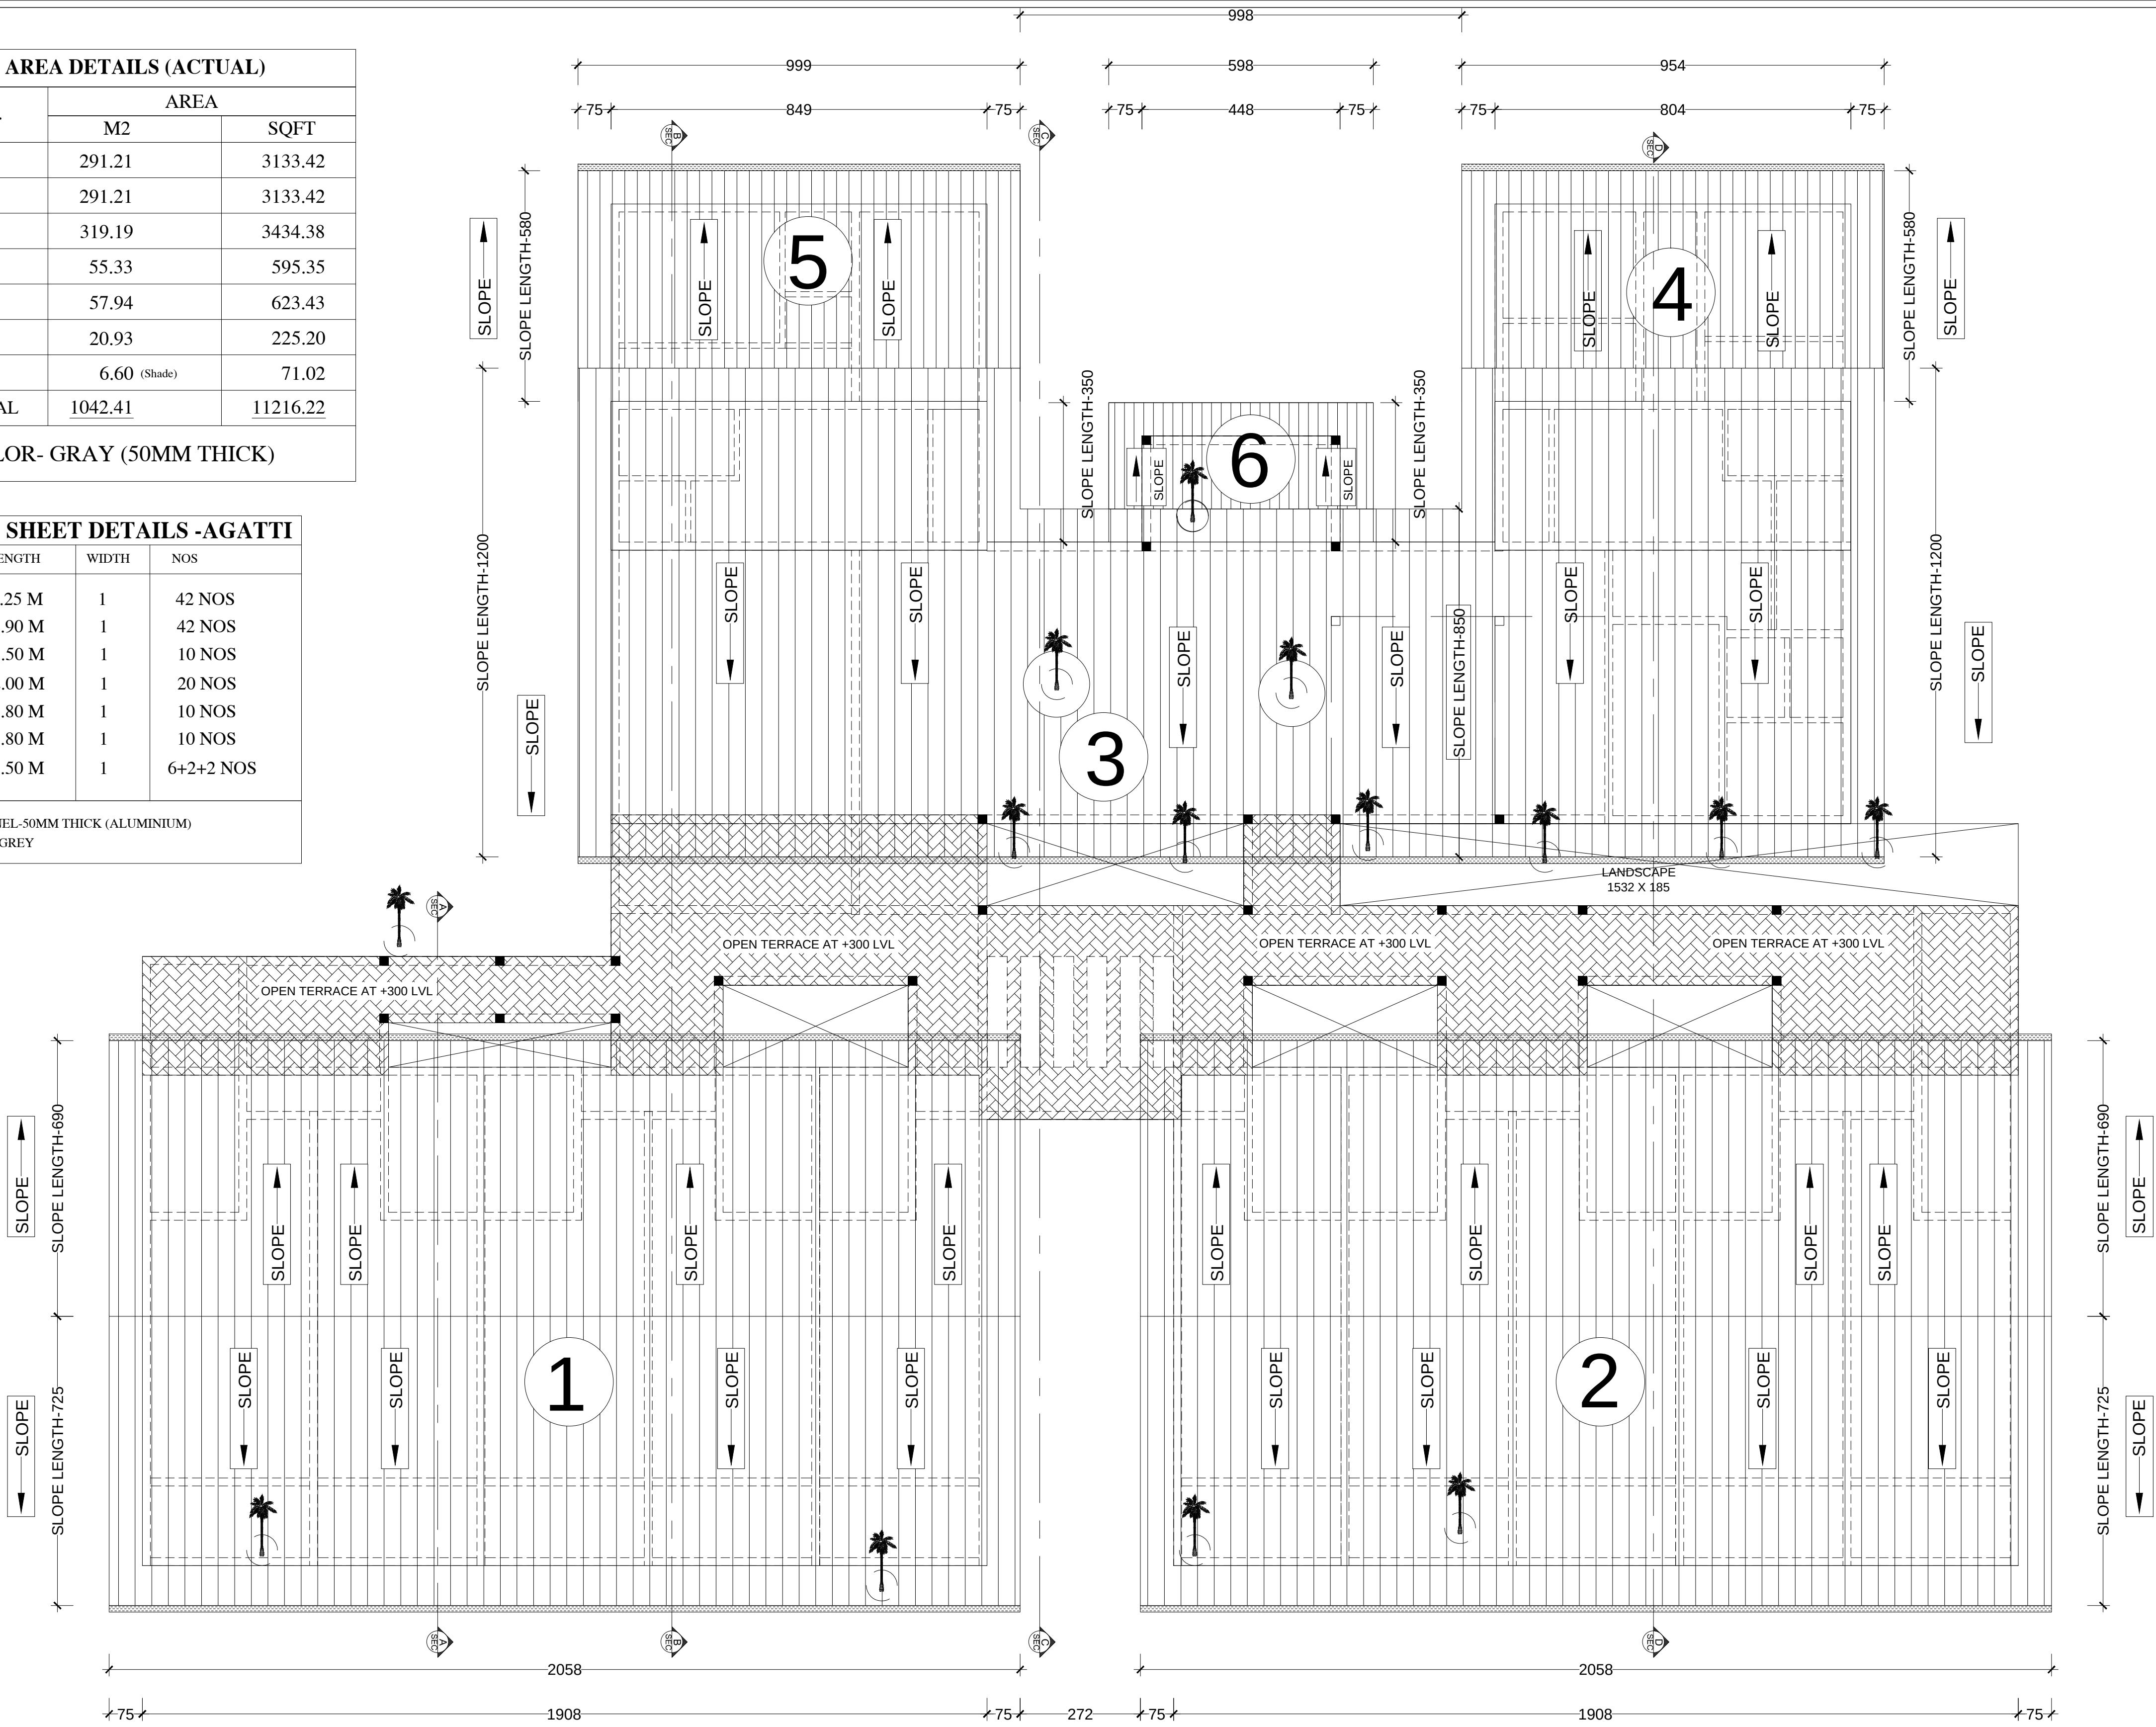

ROOF PLAN

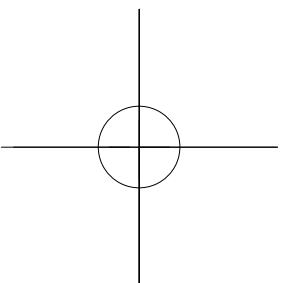

DATE: 01-5-2018

SCALE : Nts

DRAWN: Jameslee

CHECKED: Aneena

PROJ.NO- SPL 48


CLIENT: Mr. MUTHUKOYA

PROJECT : TOURIST HOME ,
AGATTI

DRAWING TITLE:
ROOF PLAN

REVISION:

- FOUNDATION REVISED IN TO FOOTING & PLINTH BEAM
AS PER CLIENT REQUEST DUE TO MATERIAL AVAILABILITY
(21-02-19)
- AS PER CLIENT REQUEST LAYOUT CHANGED 18-05-19
(FOR LIMITING CUTTING OF COCONUT TREES)

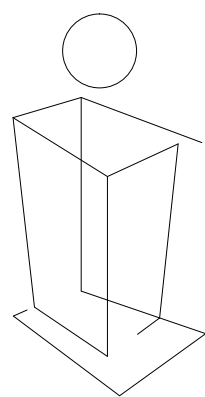

AHANAS

ALL DIMENSIONS ARE IN CMS

NO DIMENSIONS TO BE SCALED OFF FROM
DRAWINGS ONLY WRITTEN DIMENSIONS TO BE

IN THE EVENT OF ANY DISCREPANCY OR
DIFFERENCE BETWEEN ANY INTERIOR DRAWINGS
OR SITE CONDITIONS OR OTHERWISE IMMEDIATE
REFERENCE IS TO BE MADE TO THE DESIGNER
FOR CLARIFICATION PRIOR TO EXECUTION OF
WORK AT SITE

AREA :