



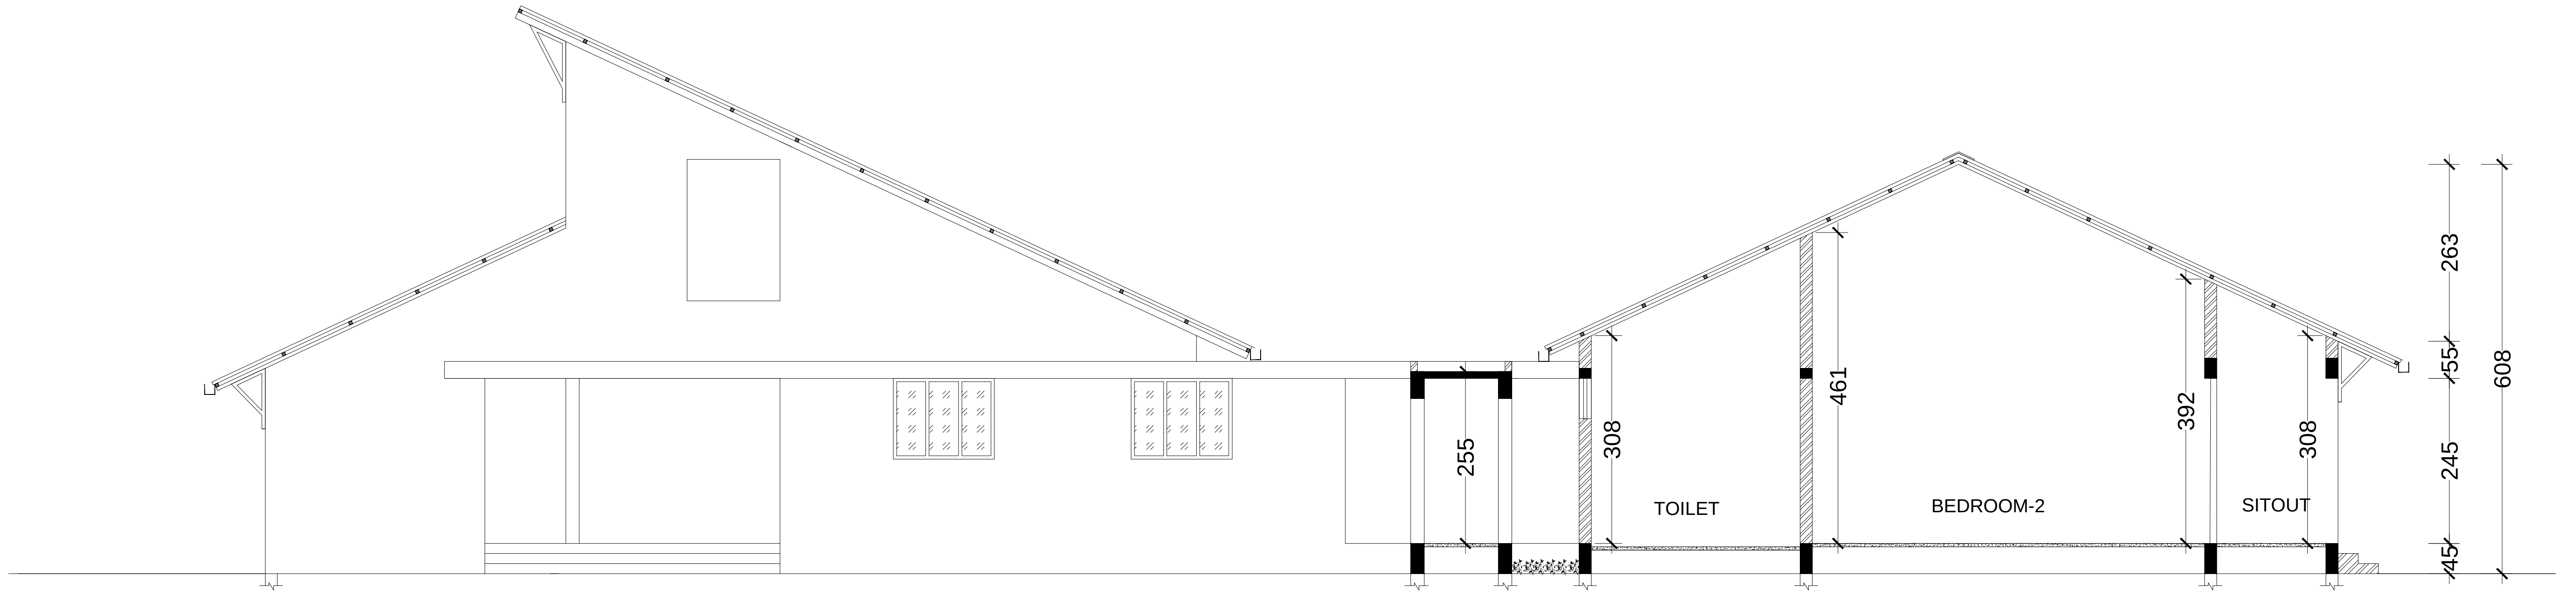

SECTION -AA

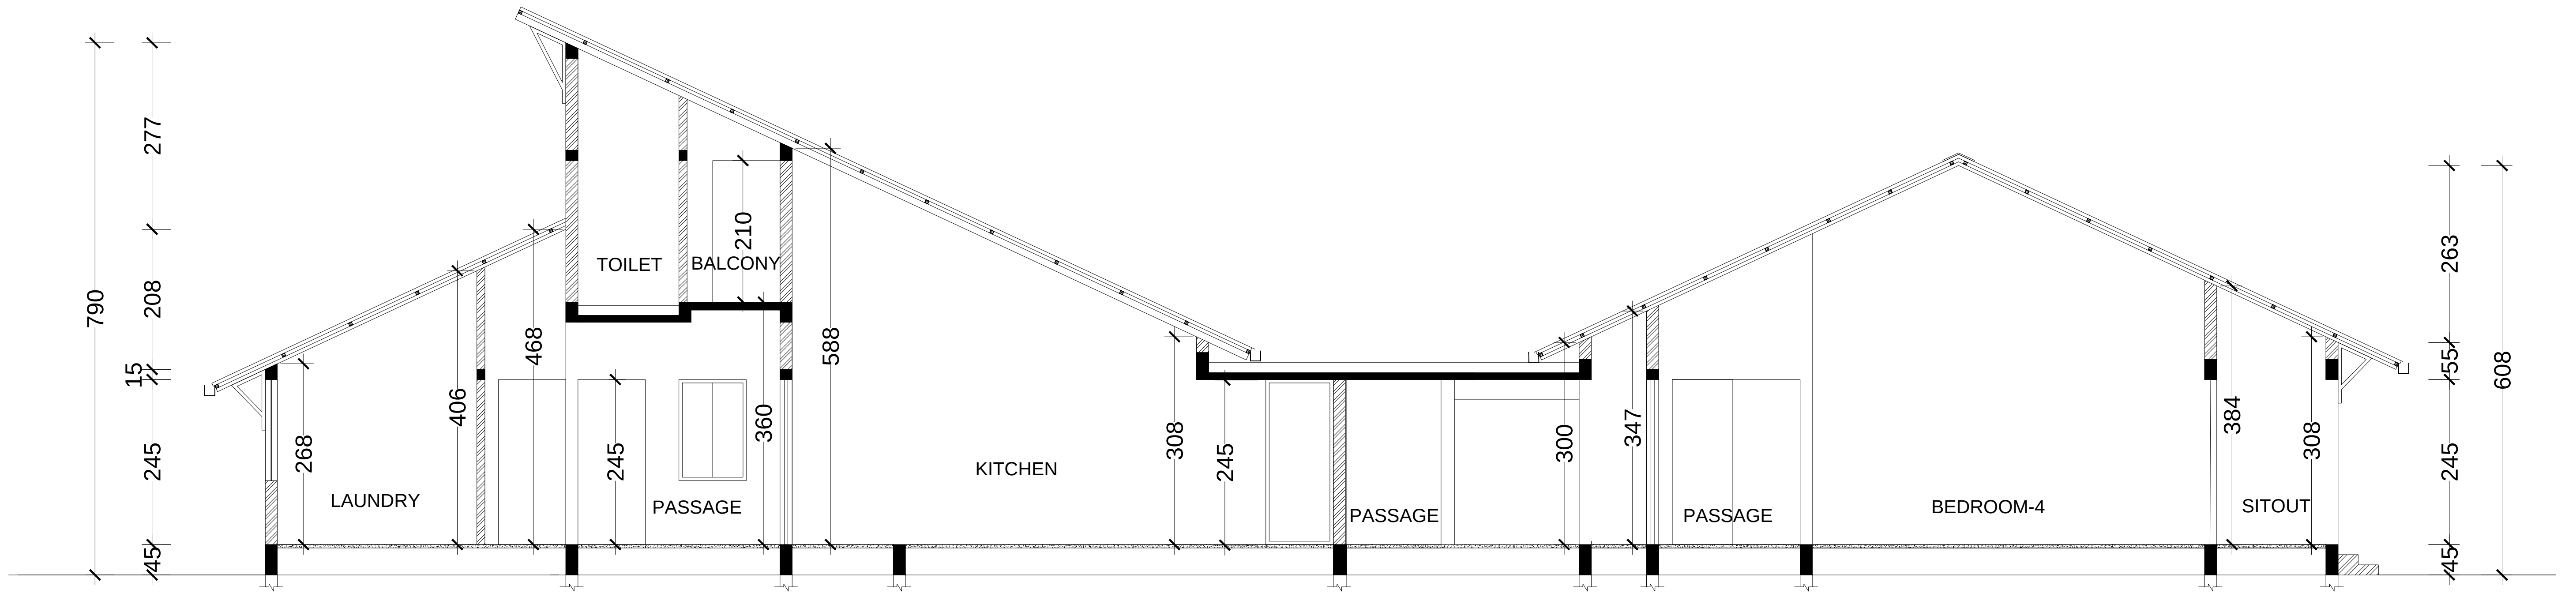

SECTION -BB

	DATE: 01-4-2019	CLIENT: Mr. MUTHUKOYA	REVISION:		 AHANAS	ALL DIMENSIONS ARE IN MM NO DIMENSIONS TO BE SCALED OFF FROM DRAWINGS ONLY WRITTEN DIMENSIONS TO BE IN THE EVENT OF ANY DISCREPANCY OR DIFFERENCE BETWEEN ANY INTERIOR DRAWINGS OR SITE CONDITIONS OR OTHERWISE IMMEDIATE REFERENCE IS TO BE MADE TO THE DESIGNER FOR CLARIFICATION PRIOR TO EXECUTION OF WORK AT SITE	AREA :
	SCALE : Nts		1,	FOUNDATION REVISED IN TO FOOTING & PLINTH BEAM AS PER CLIENT REQUEST DUE TO MATERIAL AVAILABILITY (21-02-19)			
	DRAWN: Jameslee	PROJECT : TOURIST HOME , AGATTI	2,	AS PER CLIENT REQUEST LAYOUT CHANGED 18-05-19 (FOR LIMITING CUTTING OF COCONUT TREES)			
	CHECKED: Aneena						
	PROJ.NO- SPL 48	DRAWING TITLE:SECTION AA& BB					