
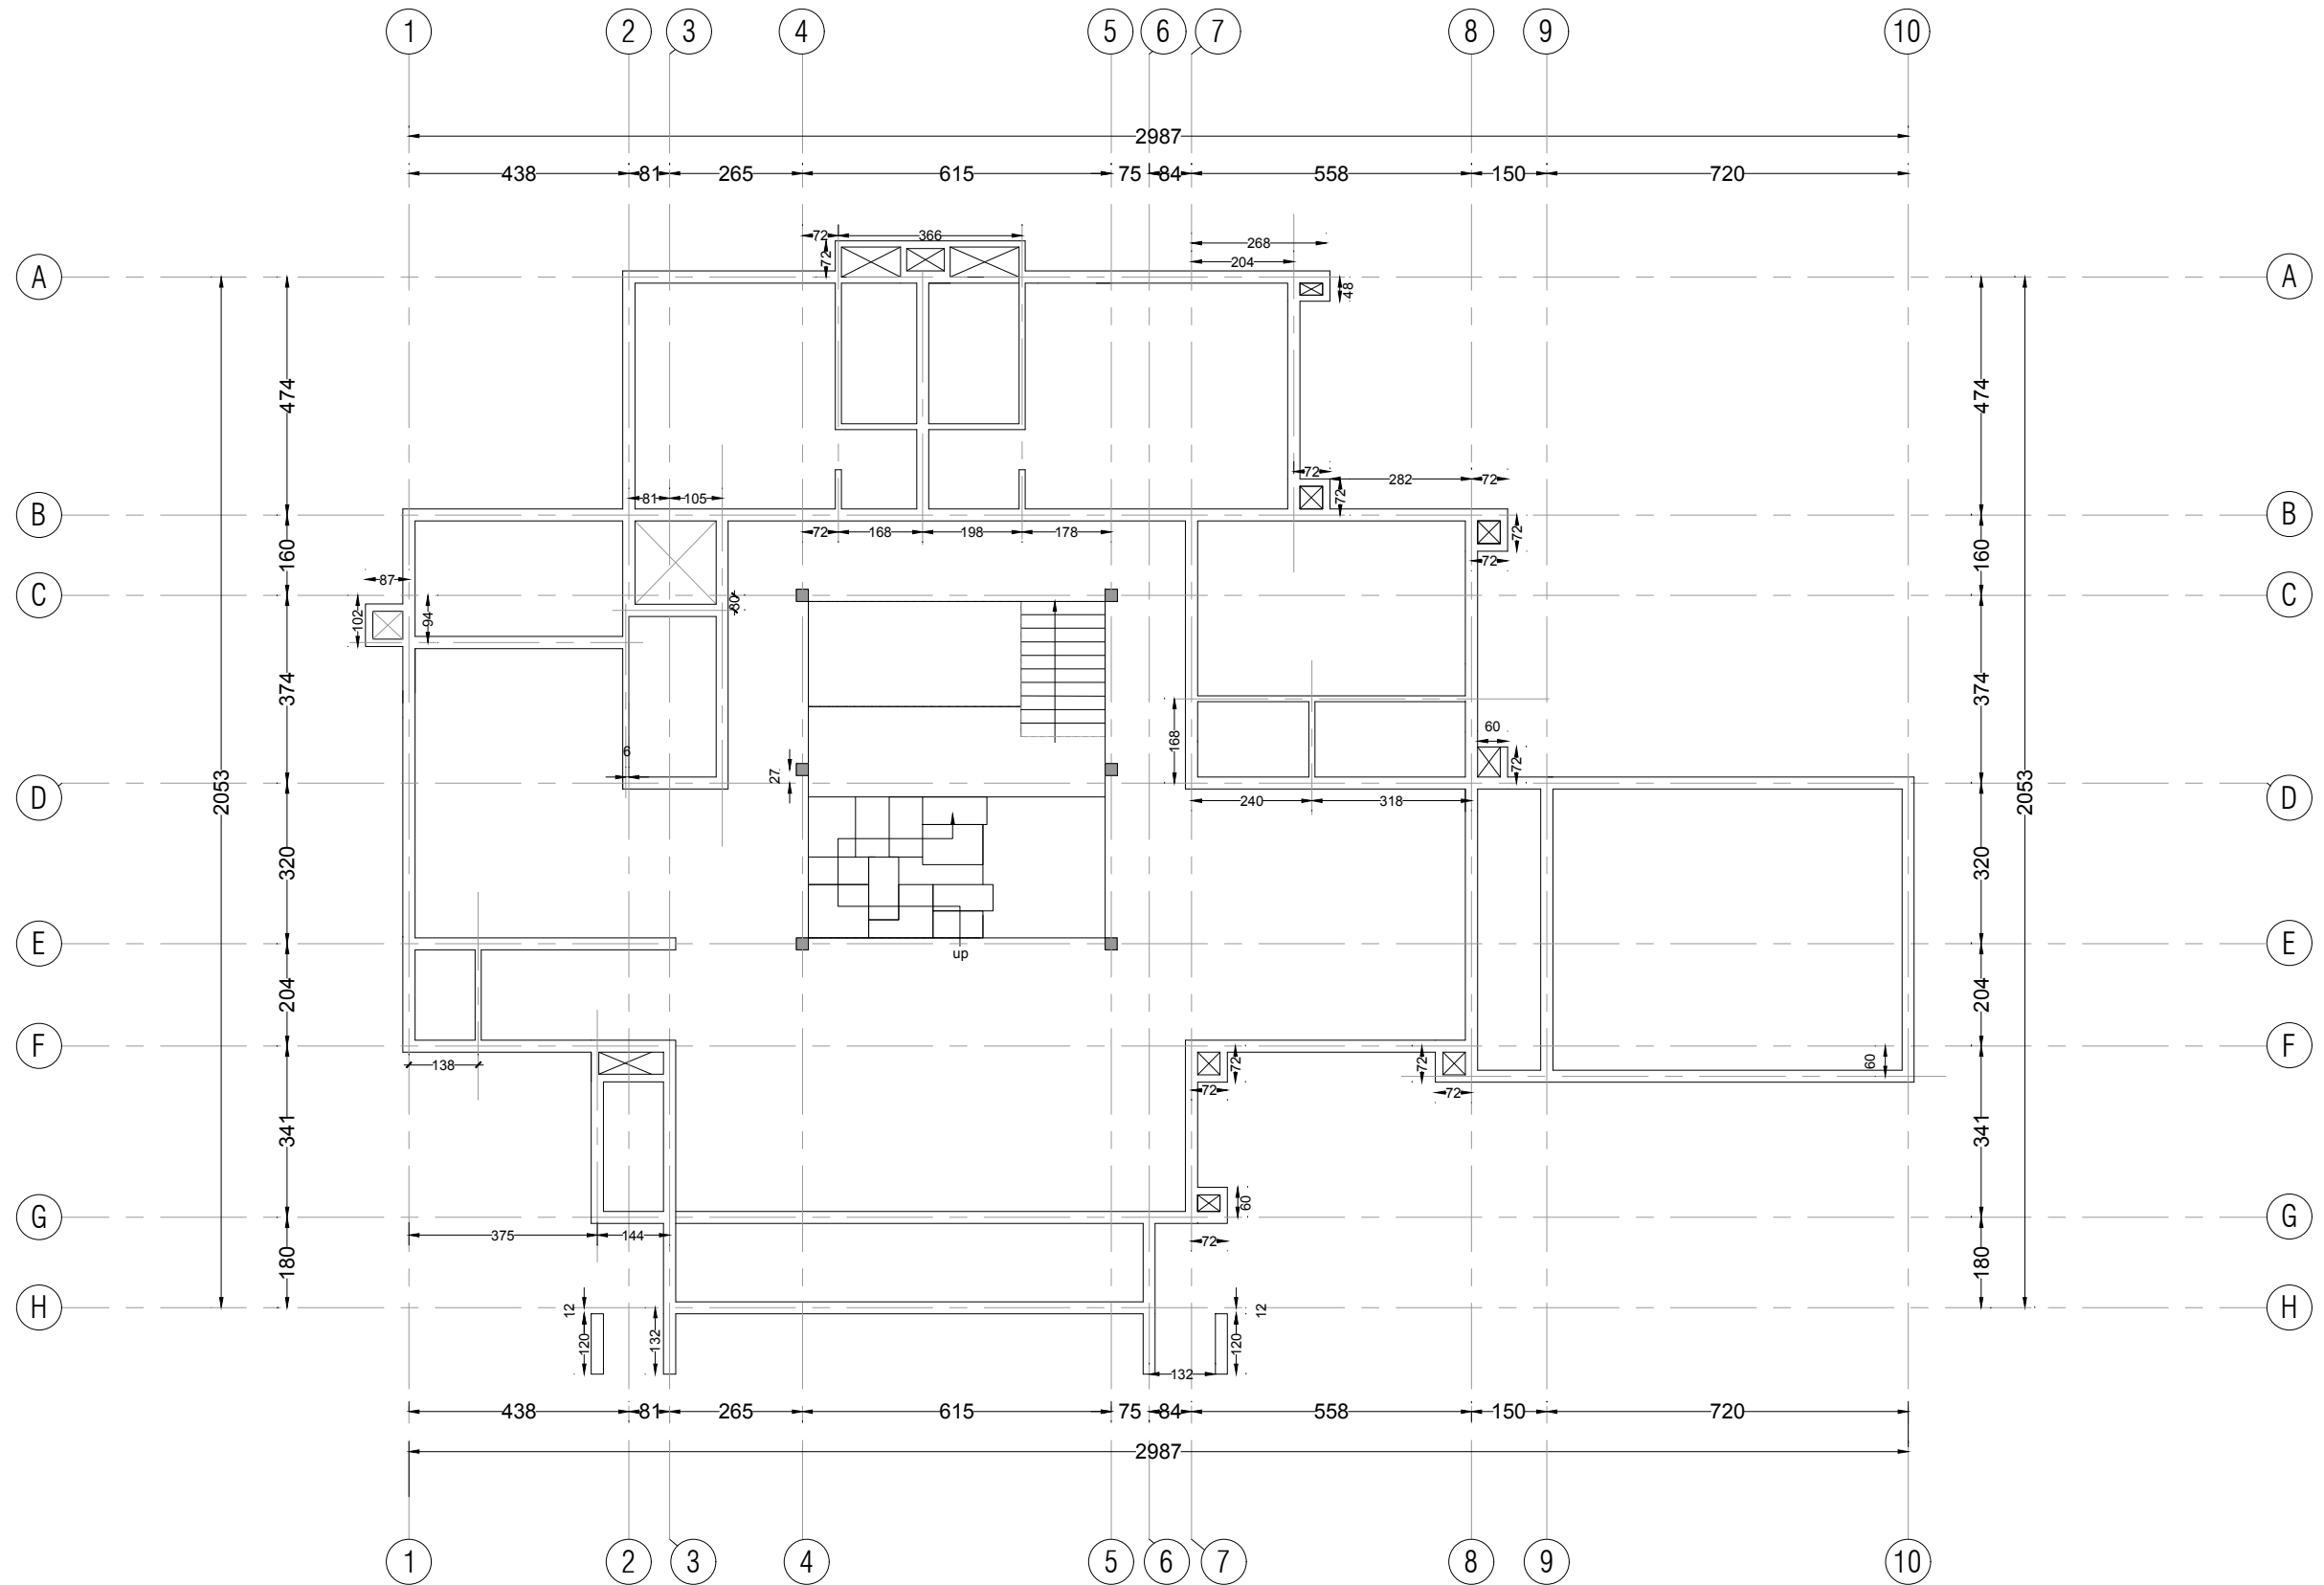


DATE: 06/03/2021
SCALE : NTS
DRAWN: AYESHA
CHECKED: AP
PROJECT NO: 496

CLIENT:
MR. MIJULAL AND
MRS. RADHIKA
PROJECT:
RESIDENCE AT THOPUMPADY
DRAWING TITLE:
CENTRELINE DRAWING

REVISION:

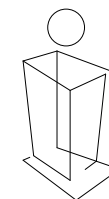

AHANAS

ALL DIMENSIONS ARE IN CMS
NO DIMENSIONS TO BE SCALED OFF FROM
DRAWINGS ONLY WRITTEN DIMENSIONS TO BE
IN THE EVENT OF ANY DISCREPANCY OR
DIFFERENCE BETWEEN ANY INTERIOR DRAWINGS
OR SITE CONDITIONS OR OTHERWISE IMMEDIATE
REFERENCE IS TO BE MADE TO THE DESIGNER
FOR CLARIFICATION PRIOR TO EXECUTION OF
WORK AT SITE