



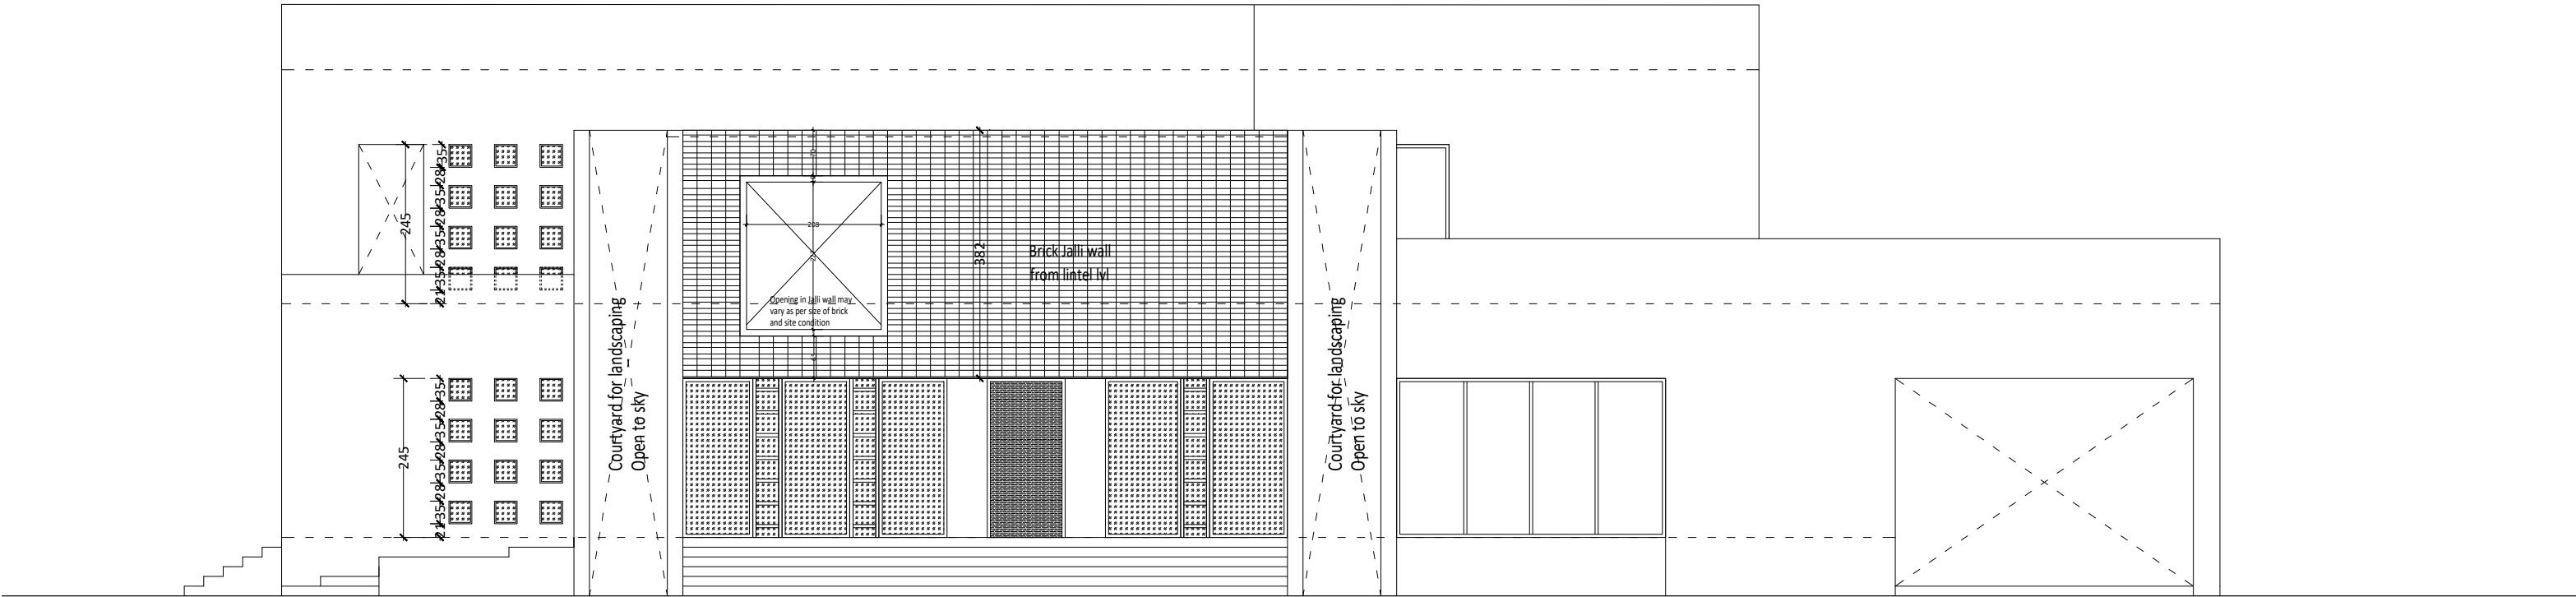

ELEVATION A

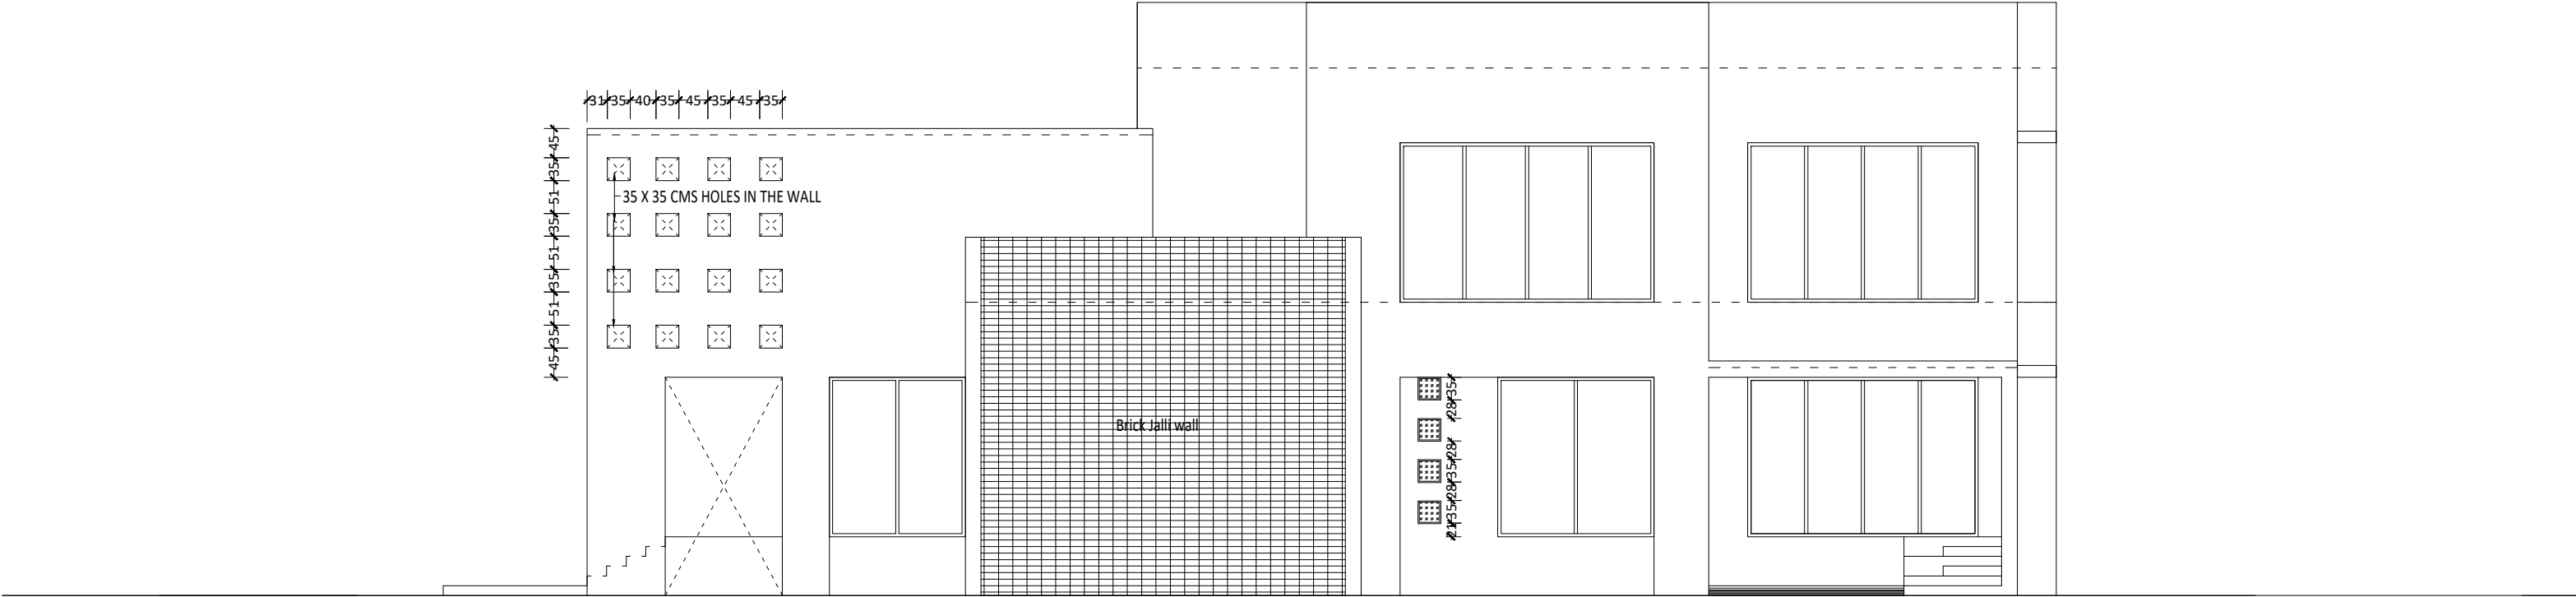

ELEVATION B

	DATE: 03.05.2021	PROJECT: RESIDENTIAL PROJECT AT RAMESHWARAM	REVISION:19.12.2022			NOTES:
	SCALE : NA		R1	Changes as per Interiors		o ALL DIMENSIONS ARE IN CMS, UNLESS OTHERWISE SPECIFIED
	DRAWN: AP	CLIENT: MIJULAL AND RADHIKA	R2	Measurements for cutouts		o DIMENSIONS SHALL NOT BE MEASURED DIRECTLY FROM THIS DRAWINGS. FOLLOW ONLY WRITTEN DIMENSIONS
	CHECKED: ANEENA					o IN THE EVENT OF ANY DISCREPANCY OR DIFFERENCE BETWEEN ANY DRAWINGS OR SITE CONDITIONS OR OTHERWISE IMMEDIATE REFERENCE IS TO BE MADE TO THE DESIGNER FOR CLARIFICATION PRIOR TO EXECUTION
	PROJECT NO:496	DRAWING TITLE: ELEVATION A AND B				OF WORK AT SITE
						o ALL THE CIVIL WORKS SHOULD BE IN LINE LEVEL AND PLUMB.
						o PLASTERING TO BE CUT AT SKIRTING LEVEL.