




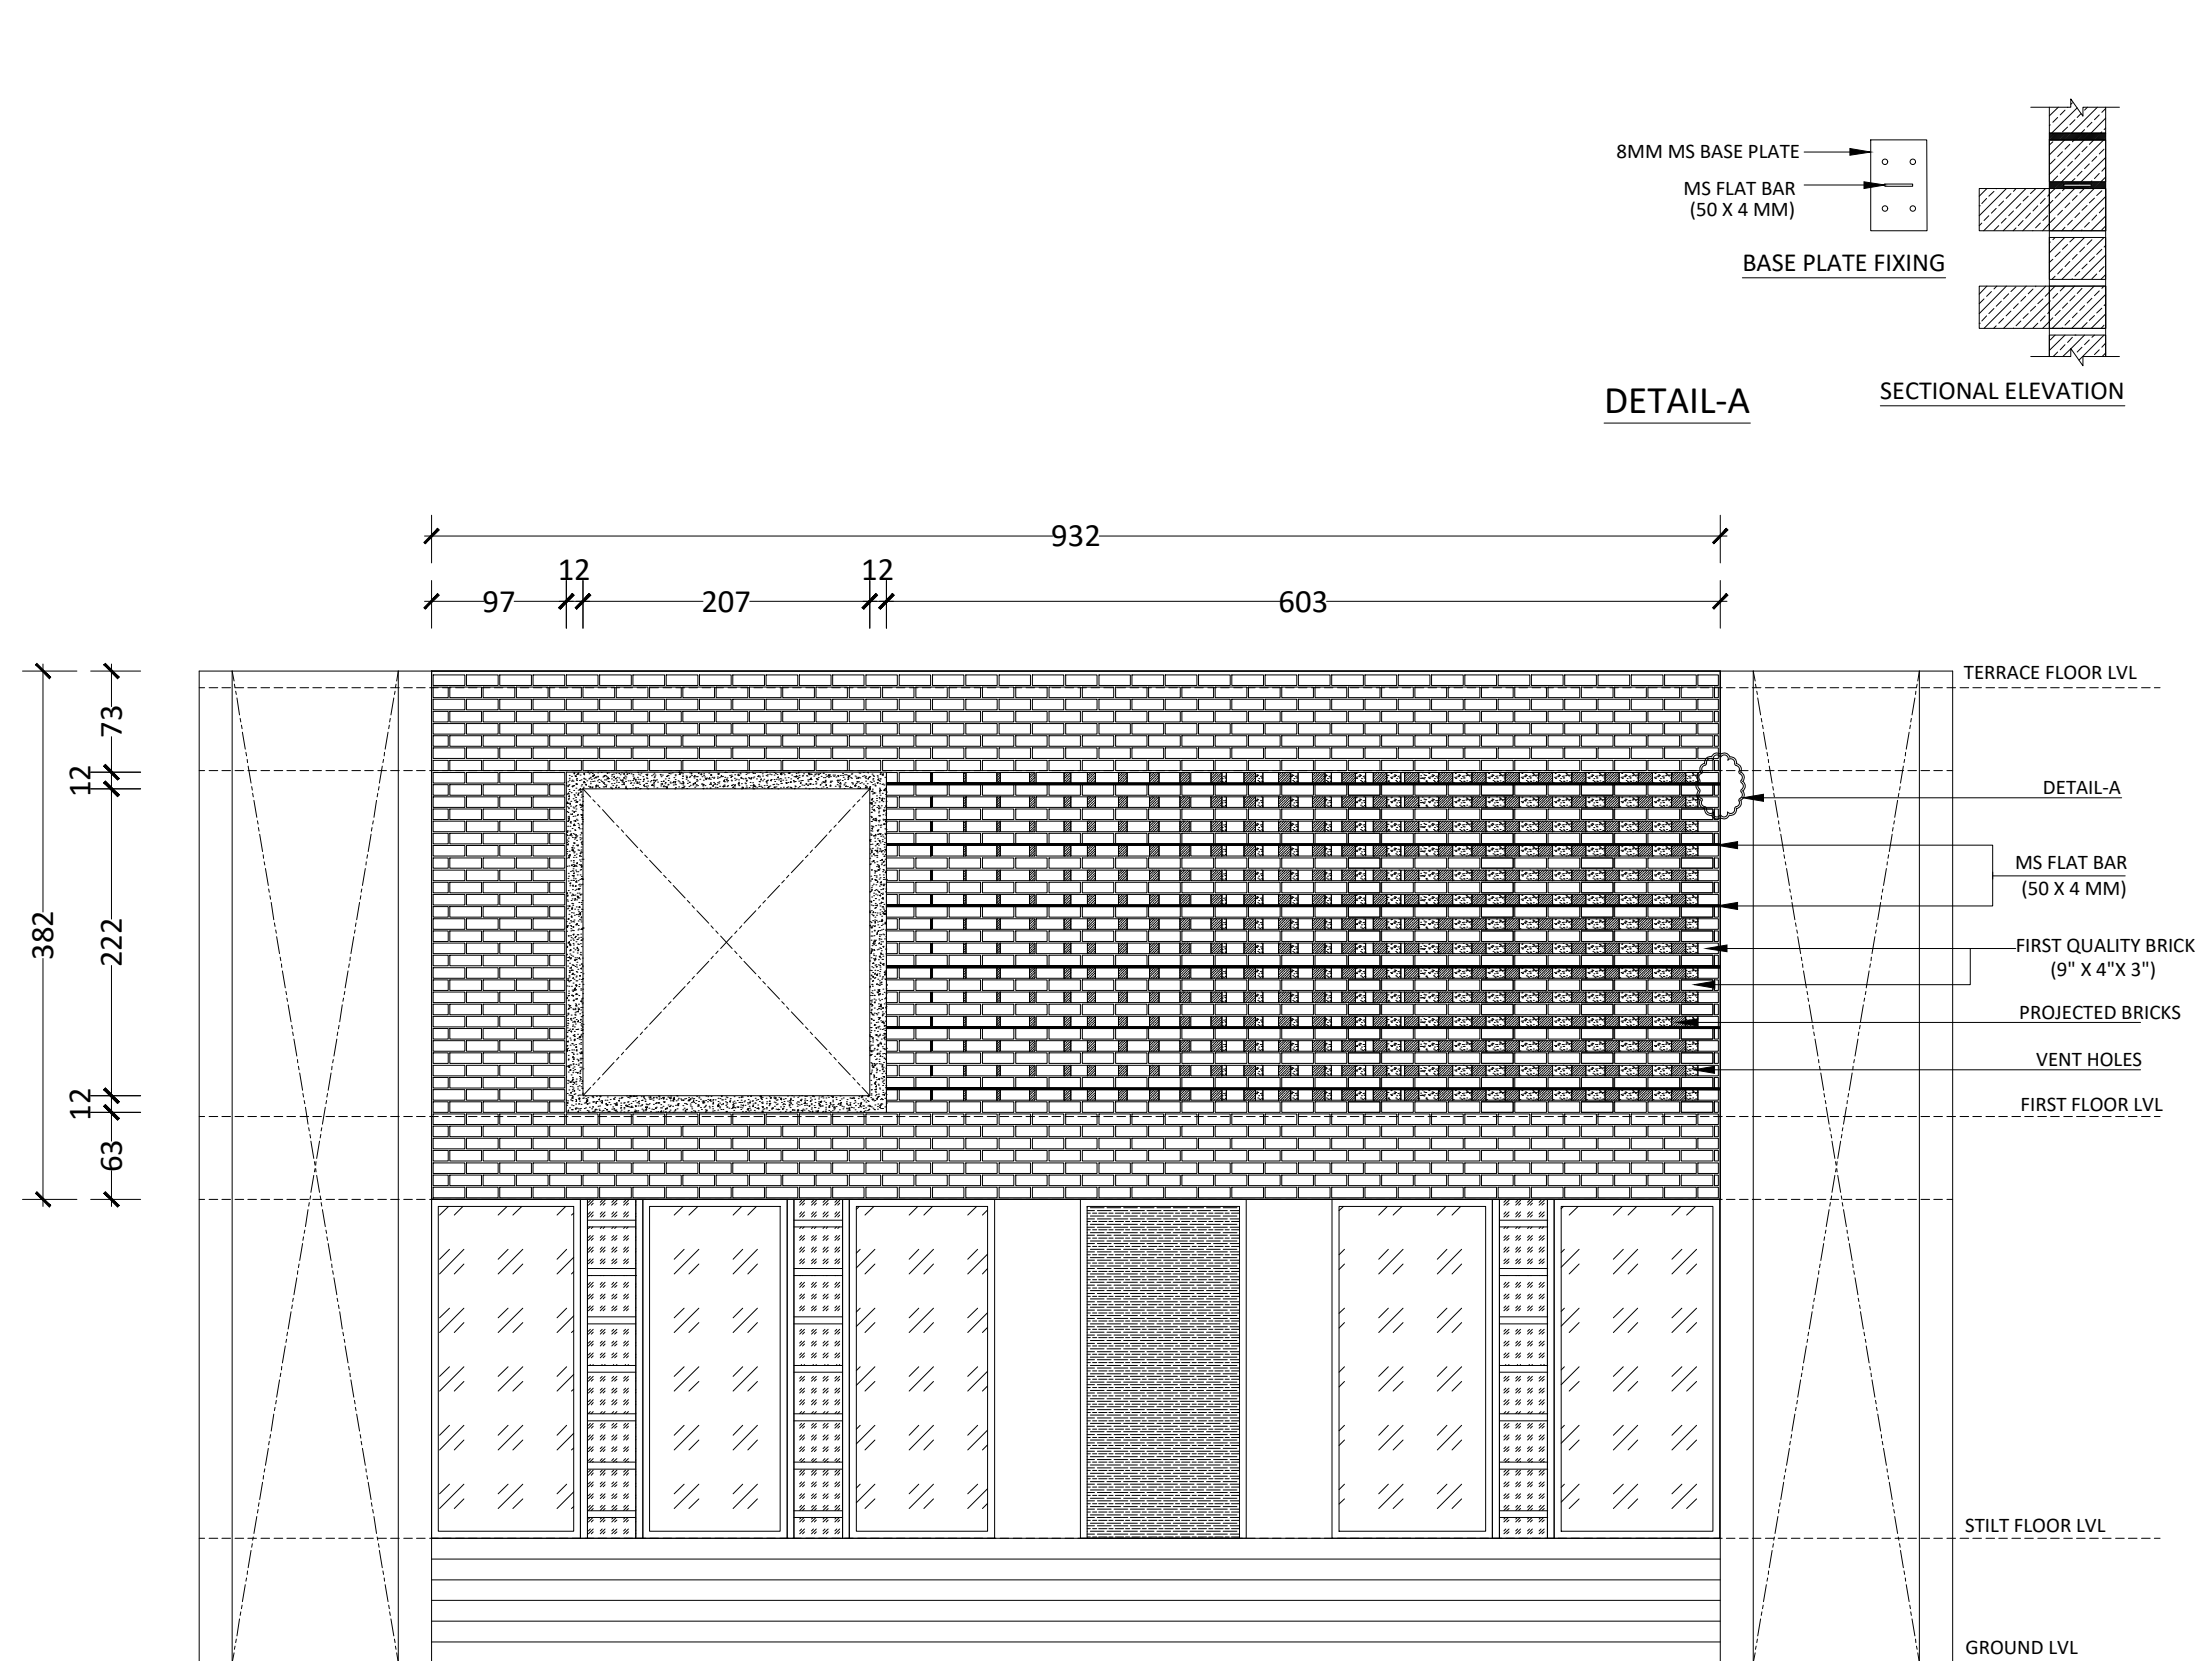

FRONT ELEVATION

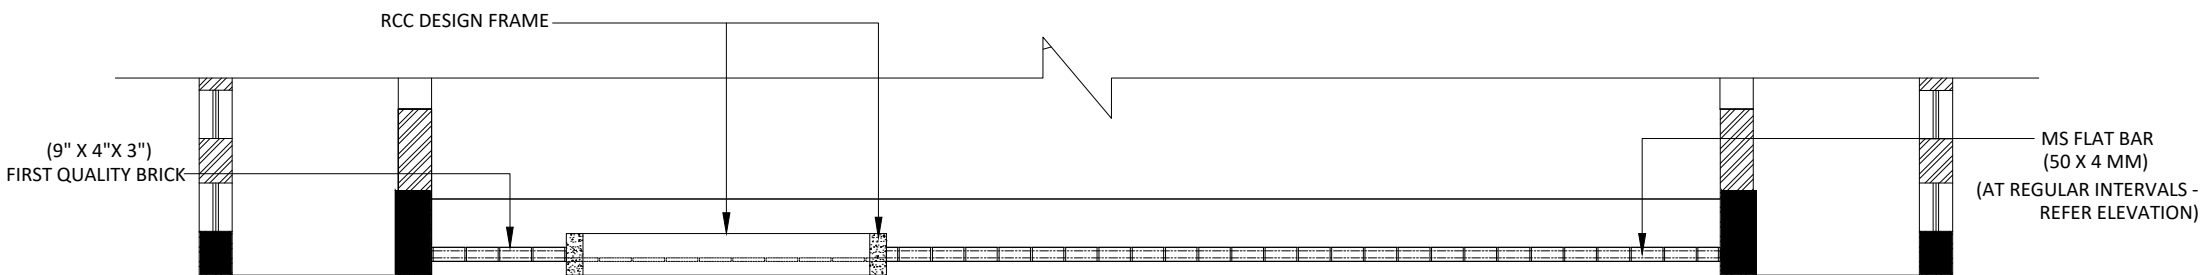

PART PLAN

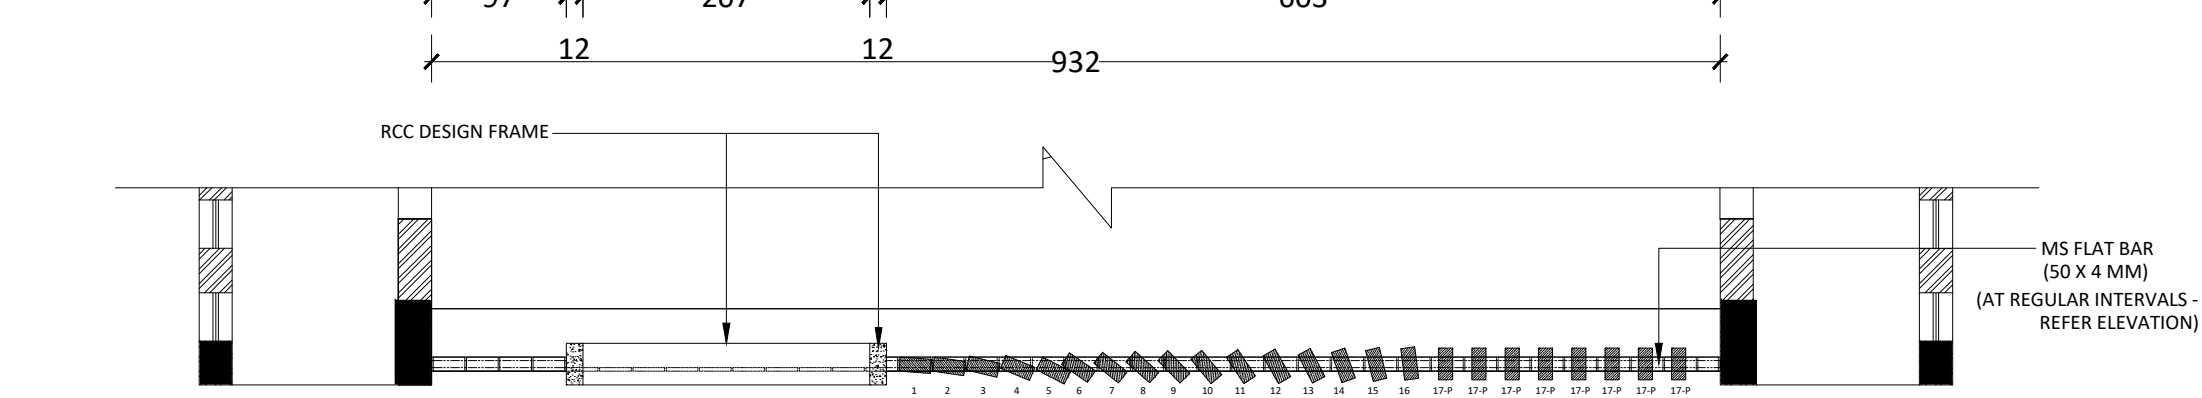

PART PLAN(Projected brick laying)

MAIN RESIDENCE-FRONT SIDE BRICK DESIGN WORK DETAILS

PROVIDE CHIKEN MESH IN EACH LAYER WHILE LAYING

	DATE: 07/07/2023	PROJECT: RESIDENTIAL PROJECT - AT RAMESHWARAM	REVISION:			NOTES:
	SCALE :NTS					○ ALL DIMENSIONS ARE IN CMS, UNLESS OTHERWISE SPECIFIED
	DRAWN: JJ					○ DIMENSIONS SHALL NOT BE MEASURED DIRECTLY FROM THIS DRAWINGS. FOLLOW ONLY WRITTEN DIMENSIONS
	CHECKED:AP	CLIENT: MIJULAL AND RADHIKA				○ IN THE EVENT OF ANY DISCREPANCY OR DIFFERENCE BETWEEN ANY DRAWINGS OR SITE CONDITIONS OR OTHERWISE IMMEDIATE REFERENCE IS TO BE MADE TO THE DESIGNER FOR CLARIFICATION PRIOR TO EXECUTION OF WORK AT SITE
	PROJECT NO: 496					○ ALL THE CIVIL WORKS SHOULD BE IN LINE LEVEL AND PLUMB.
		DRAWING TITLE: MAIN RESIDENCE-BRICK DESIGN DETAILS-1				○ PLASTERING TO BE CUT AT SKIRTING LEVEL.