




PROPOSED RESIDENCE FOR Mr. MIJULAL . P

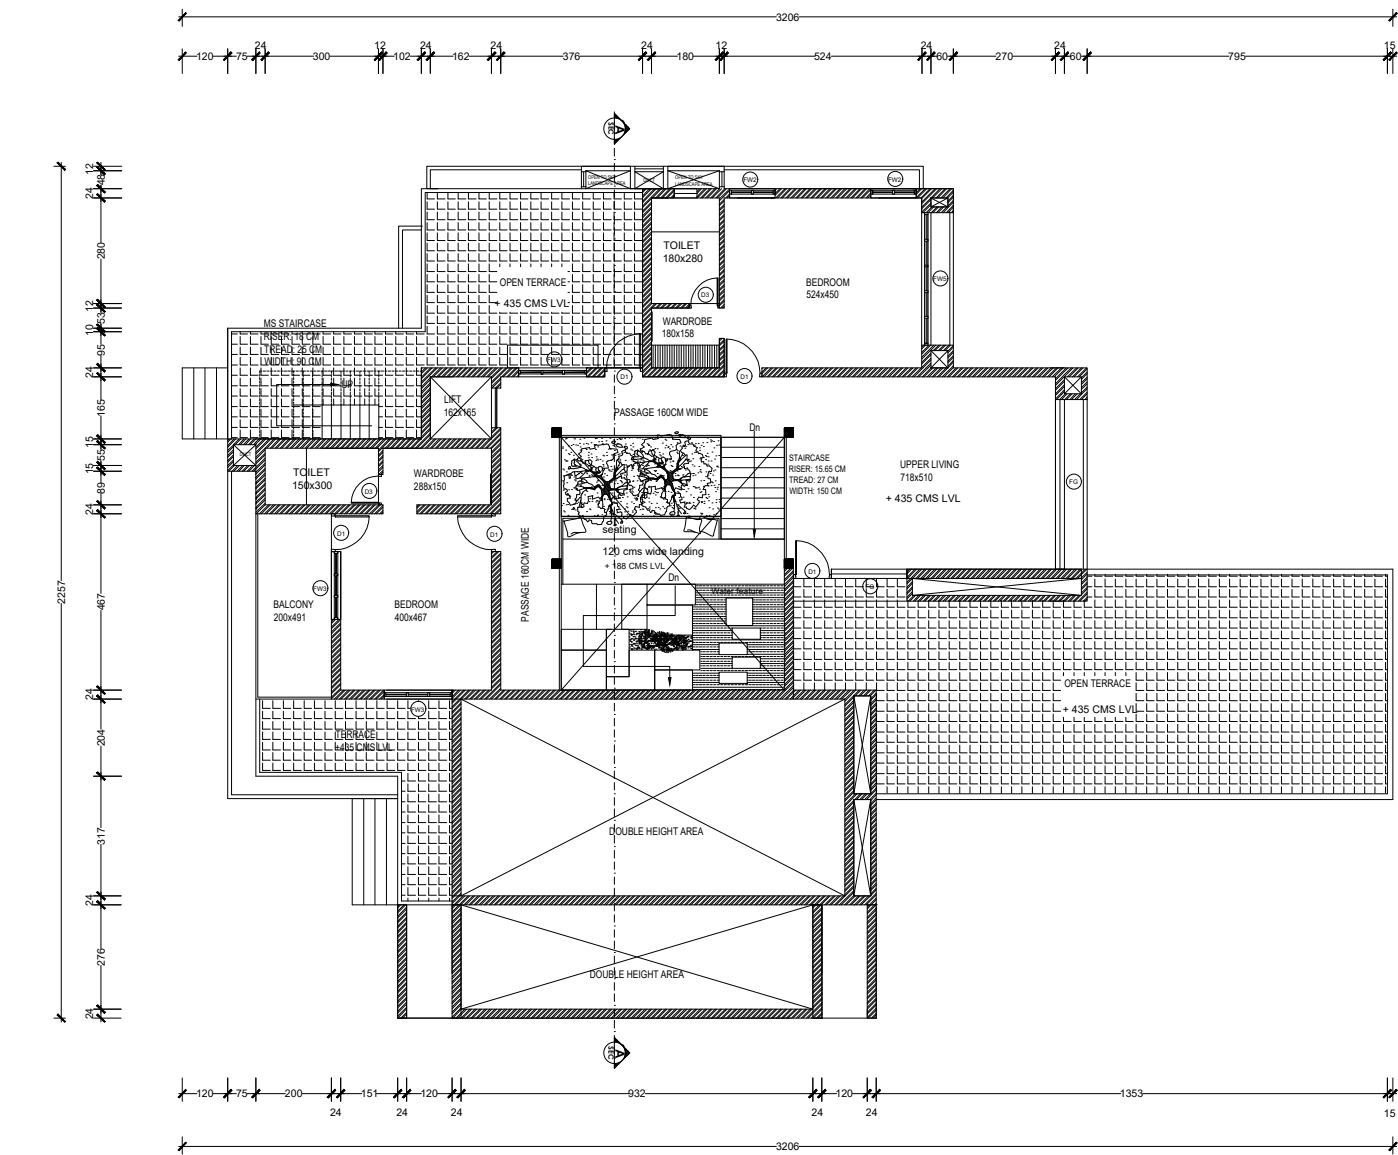


FIRST FLOOR
SCALE 1:100

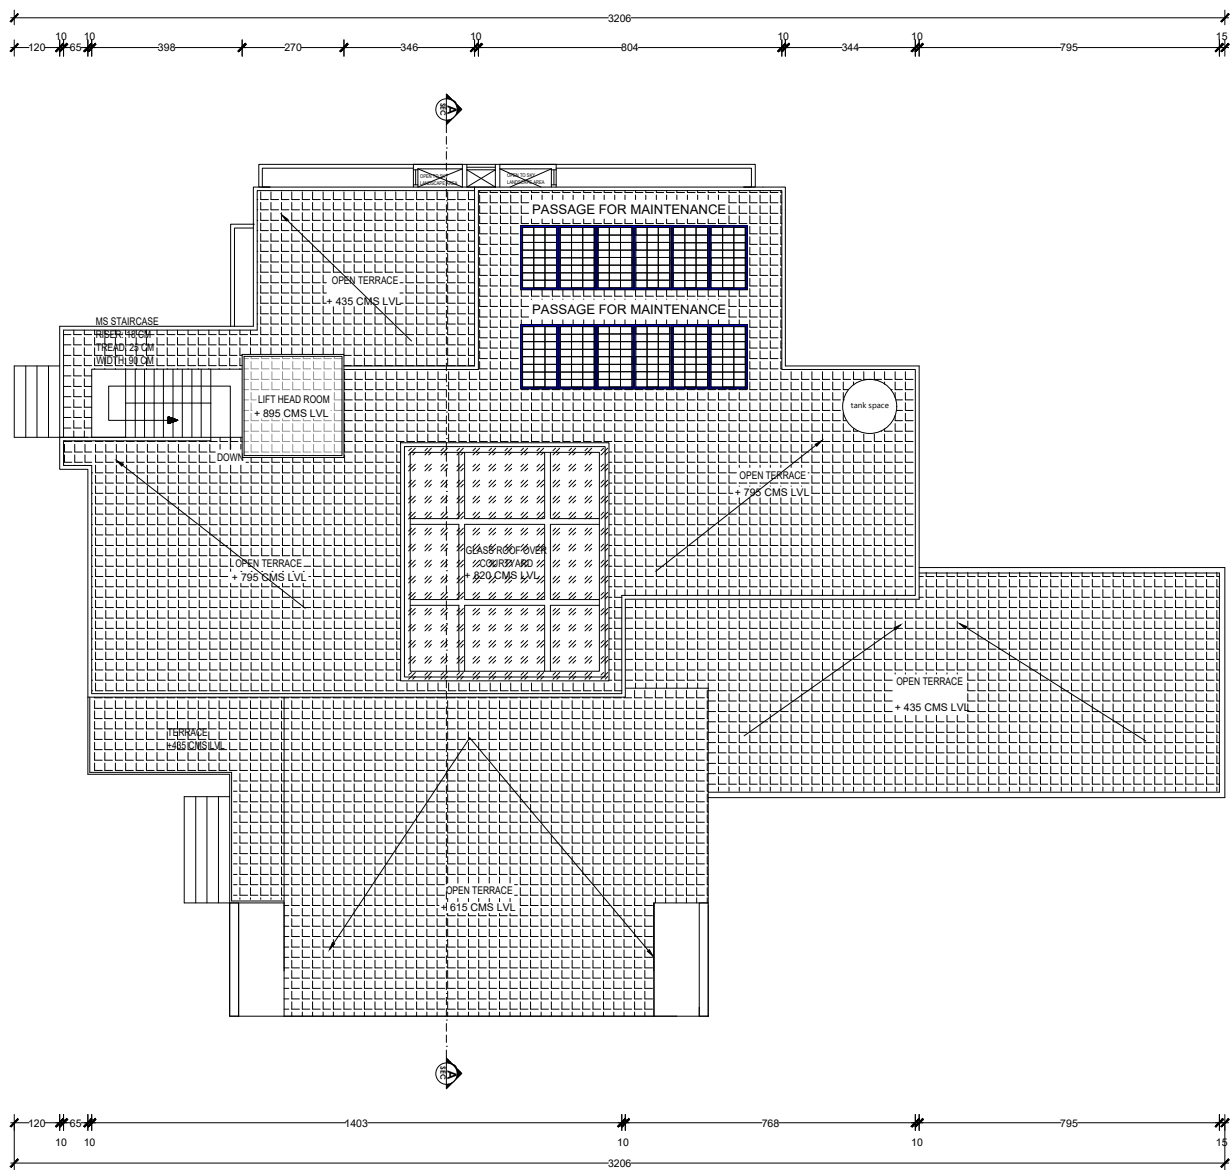

TERRACE FLOOR
SCALE 1:100

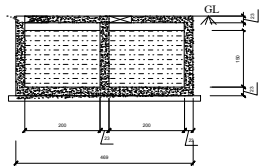


SECTION PP

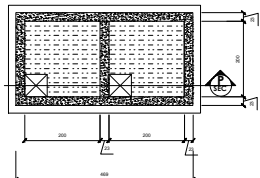

PLAN


RWH TANK 11755 LITRES CAPACITY
SCALE 1:100

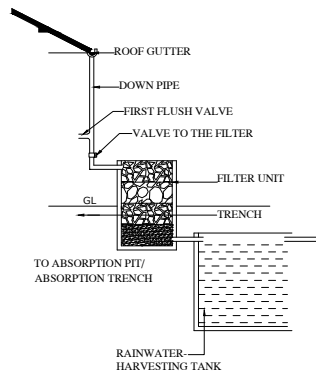


SCHEMATIC SECTION

SCHEMATIC DETAILS SHOWING RAIN WATER HARVESTING TANK

TYPICAL DETAILS OF RAIN WATER TANK

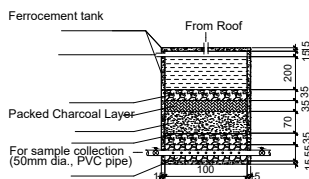

CROSS SECTION ON BB

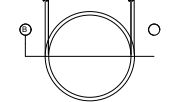

PLAN

SECTION DETAILS
OF FILTER TANK - not to scale

CERTIFICATE :

- CERTIFIED THAT THE SITE PLAN IS PREPARED AFTER VERIFICATION OF OWNERSHIP DOCUMENT & SITE AND THE MEASUREMENTS SHOWN ARE FOUND TO BE CORRECT.
- CERTIFIED THAT THE BUILDING PLAN IS PREPARED IN ACCORDANCE WITH THE KMBR 2019, KERALA MUNICIPALITY ACT 1994 & THE PROVISIONS CONTAINED IN THE SANCTIONED TOWN PLANNING SCHEME.
- CERTIFIED THAT THERE IS NO WELL WITHIN 7.50m RADIUS FROM PROPOSED SEPTIC TANK.

SPECIFICATIONS	SCHEDULE OF OPENING	LAND DETAILS	AREA STATEMENT	ADDRESS&SIGNATURE OF THE OWNER	SIGNATURE OF THE ARCHITECT	PROJECT :	DRG : SANCTION DRAWING
1. Foundation bed :- PCC 15CM thick 2. Foundation :- Pile foundation 3. Superstructure :- RCC columns and beams with first class brick masonry and throughout lintel above 4. Flooring :- Tile&Granite finish 5. Joinary works :- Glazed ,Aluminium&Wood 6. Plastering :- 12mm thick CM 1:4 7. Roofing :- RCC Slab ,15cm Thick 8. Stair case :- 12cm thick RCC slab and MS with Rise :-15cm Tread :-30cm Stair width:-1.50cm 9. Hand rail :- SS,MS&Wood hand rail 90cm height 10. Parapet wall :- 15cm thick masonry 120cm height 11. Ventilation :- Mechanical(forced) / Natural 12. Water Supply :- Bore well & Public water supply 13. Drainage :- To Public drain& Diverted to soak pit 14. Access :- Road 15. Sewage :- Disposed to STP& Septic tank	DD DOUBLE LEAF DOOR 120 X 240 D1 DOOR 100 X 240 D2 DOOR 90 X 240 D3 DOOR 80 X 240 FG FIXED GLASS WINDOW L X 240 FW2 WINDOW 120 X 240 FW3 WINDOW 180 X 240 FW4 WINDOW 240 X 240 FW5 WINDOW 300 X 240 KW3 KITCHEN WINDOW 180 X 120 KW4 KITCHEN WINDOW 240 X 120 V VENTILATOR 60 X 60 GR GRILL OPENING L X 120	DISTRICT : ERNAKULAM TALUK : KOCHI VILLAGE : RAMESHWARAM SURVEY NO : 772/3 part , 1662 part EXTENT : 1427 SQM (14.27 ARES)	FOR AREA STATEMENT REFER TO SHEET NO:3/3	Mr. MIJULAL . P S/o LALAN PRADEEPS HOUSE THOPUMPADY PALLURUTHY, VADAKKU MURI 682005	 AHANAS	33/1622 A , Navam , Haritha By Lane Vennala p.o,Kochi 682028 T:0484 2808673,2808517 F:0484 2809246 ahanas@ahanas.com	PROPOSED RESIDENTIAL BUILDING AT THOPUMPADY <