



PROPOSED RESIDENCE FOR Mr. MIJULAL . P

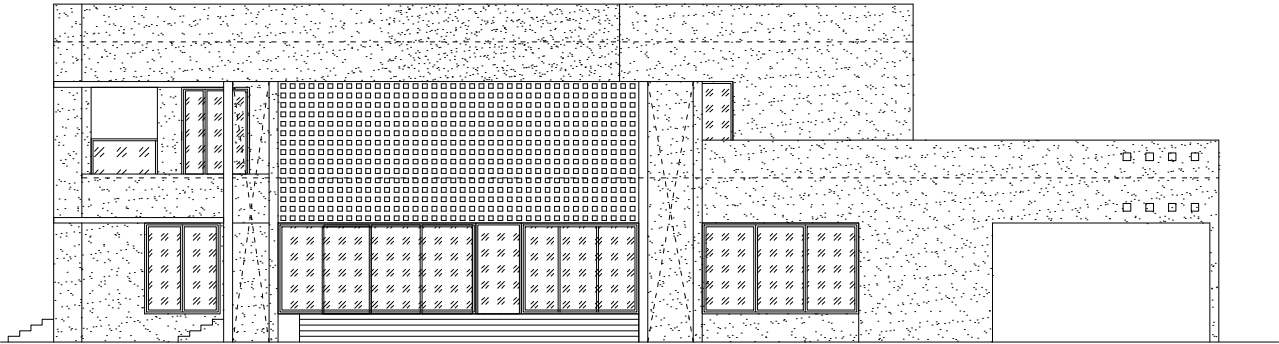


ELEVATION

SCALE 1:100

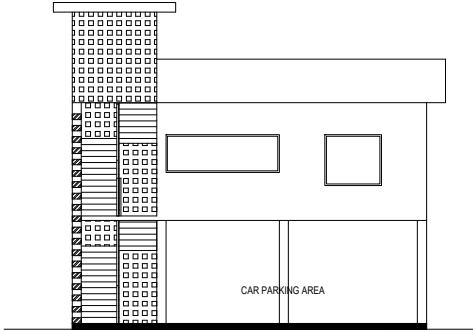


OUTHOUSE ELEVATION

SCALE 1:100

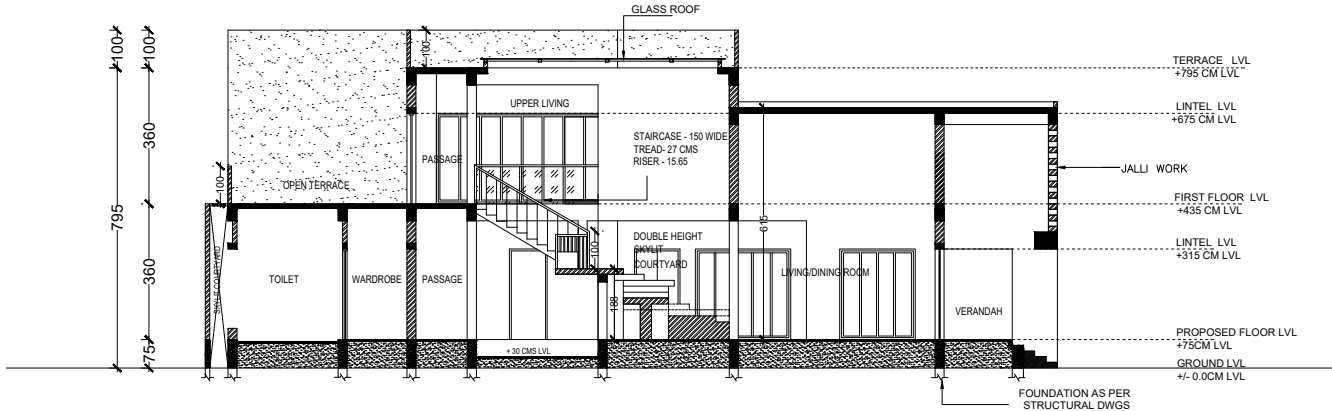


SECTION A-A

SCALE 1:100

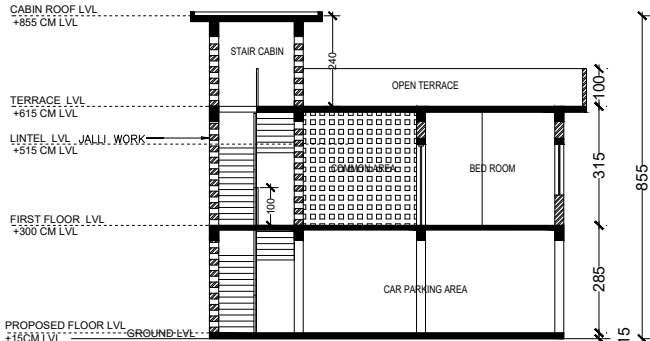



SECTION B-B

SCALE 1:100

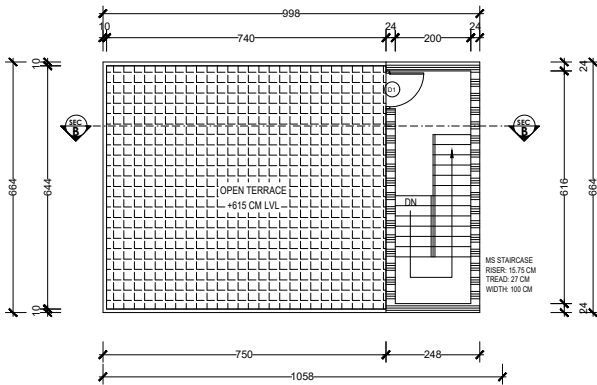


TERRACE FLOOR PLAN

SCALE 1:100

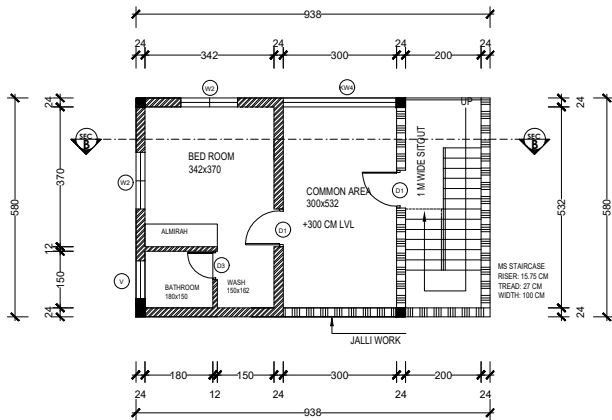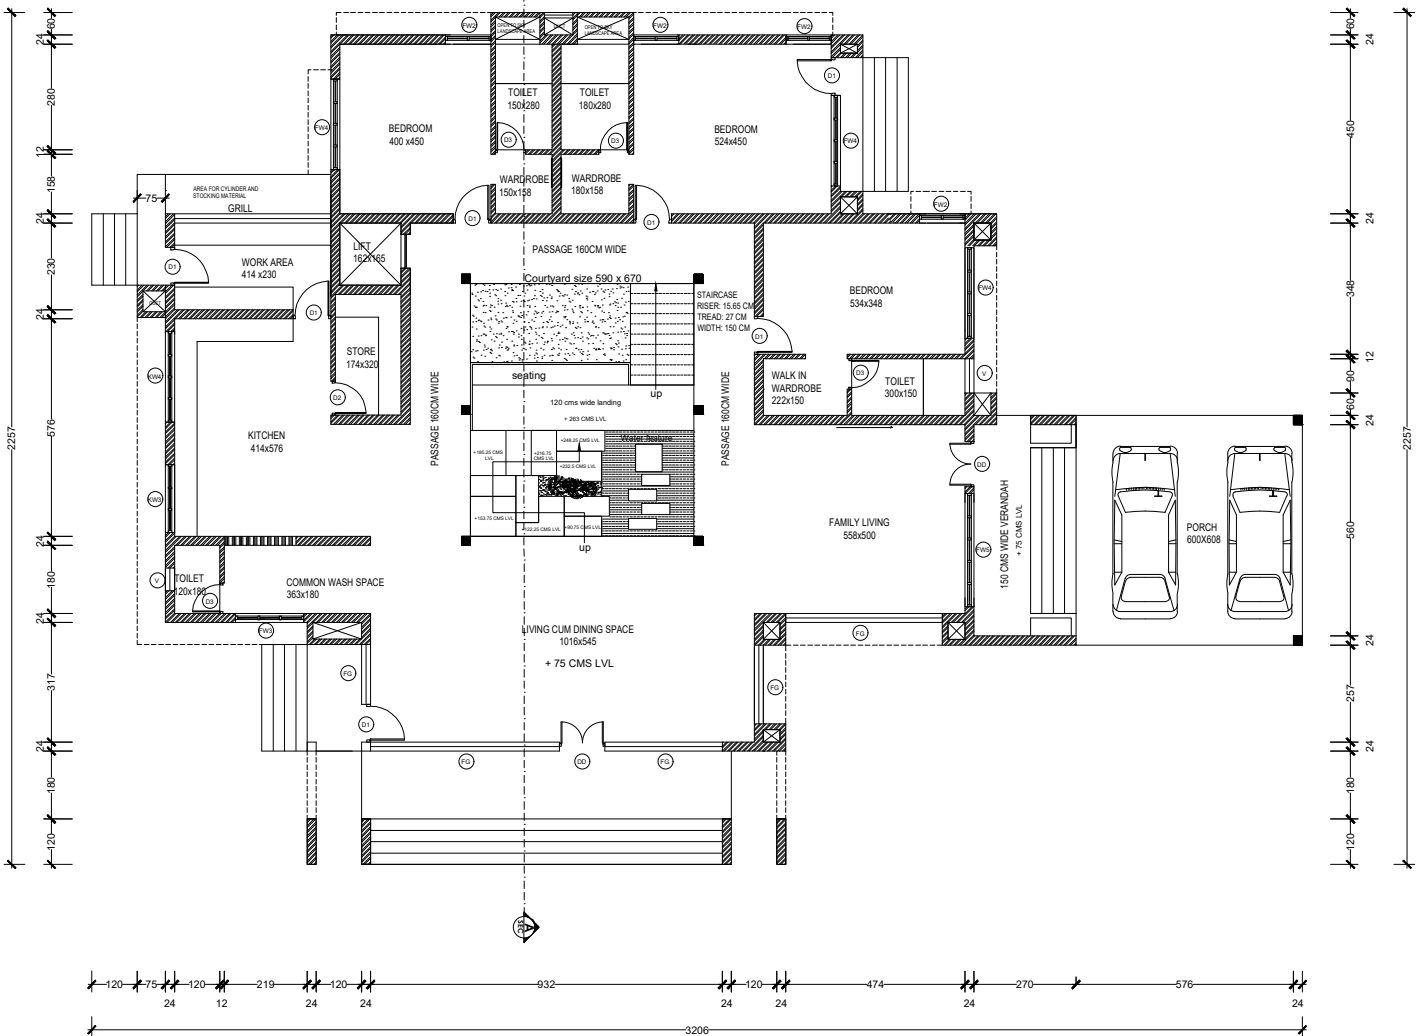

FIRST FLOOR PLAN

SCALE 1:100

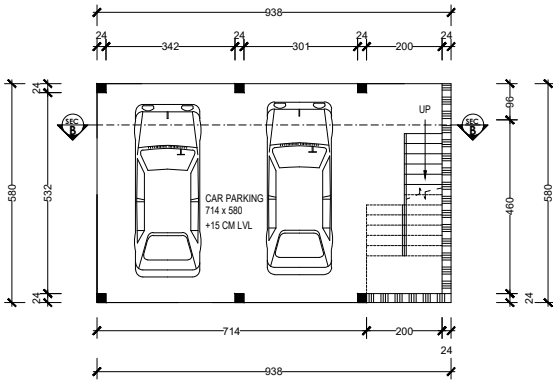

GROUND FLOOR PLAN

SCALE 1:100

GROUND FLOOR

SCALE 1:100

SPECIFICATIONS	SCHEDULE OF OPENINGS	LAND DETAILS	AREA STATEMENT	ADDRESS&SIGNATURE OF THE OWNER	SIGNATURE OF THE ARCHITECT	PROJECT :	DRG : SANCTION DRAWING
1. Foundation bed :- PCC 15CM thick 2. Foundation :- Pile foundation 3. Superstructure :- RCC columns and beams with first class brick masonry and throughout lintel above 4. Flooring :- Tile&Granite finish 5. Joinary works :- Glazed ,Aluminium&Wood 6. Plastering :- 12mm thick CM 1:4 7. Roofing :- RCC Slab ,15cm Thick 8. Stair case :- 12cm thick RCC slab and MS with Rise :-15cm Tread :-30cm Stair width :-1.50cm 9. Hand rail :- SS,MS&Wood hand rail 90cm height 10. Parapet wall :- 15cm thick masonry 120cm height 11. Ventilation :- Mechanical(forced) / Natural 12. Water Supply :- Bore well & Public water supply 13. Drainage :- To Public drain& Diverted to soak pit 14. Access :- Road 15. Sewage :- Disposed to STP& Septic tank	DD DOUBLE LEAF DOOR 120 X 240 D1 DOOR 100 X 240 D2 DOOR 90 X 240 D3 DOOR 80 X 240 FG FIXED GLASS WINDOW L X 240 FW2 WINDOW 120 X 240 FW3 WINDOW 180 X 240 FW4 WINDOW 240 X 240 FW5 WINDOW 300 X 240 KW3 KITCHEN WINDOW 180 X 120 KW4 KITCHEN WINDOW 240 X 120 V VENTILATOR 60 X 60 GR GRILL OPENING L X 120	DISTRICT : ERNAKULAM TALUK : KOCHI VILLAGE : RAMESHWARAM SURVEY NO : 772/3 part , 1662 part EXTENT : 1427 SQM (14.27 ARES)	FOR AREA STATEMENT REFER TO SHEET NO:3/3	Mr. MIJULAL . P S/o LALAN PRADEEPS HOUSE THOPUMPADY PALLURUTHY, VADAKKU MURI 682005	 AHANAS	PROPOSED RESIDENTIAL BUILDING AT THOPUMPADY	Drawing Title : MAIN HOUSE FLOOR PLAN, ELEVATION AND SECTION OUTHOUSE FLOOR PLANS ELEVATION AND SECTION ALL DIMENSIONS IN CMS Date : 08/03/2021 Scale: 1:100 Dwg.No : SD/RD - 09 SHEET NO: 1/3 Drawn : Aneena Checked : AP