


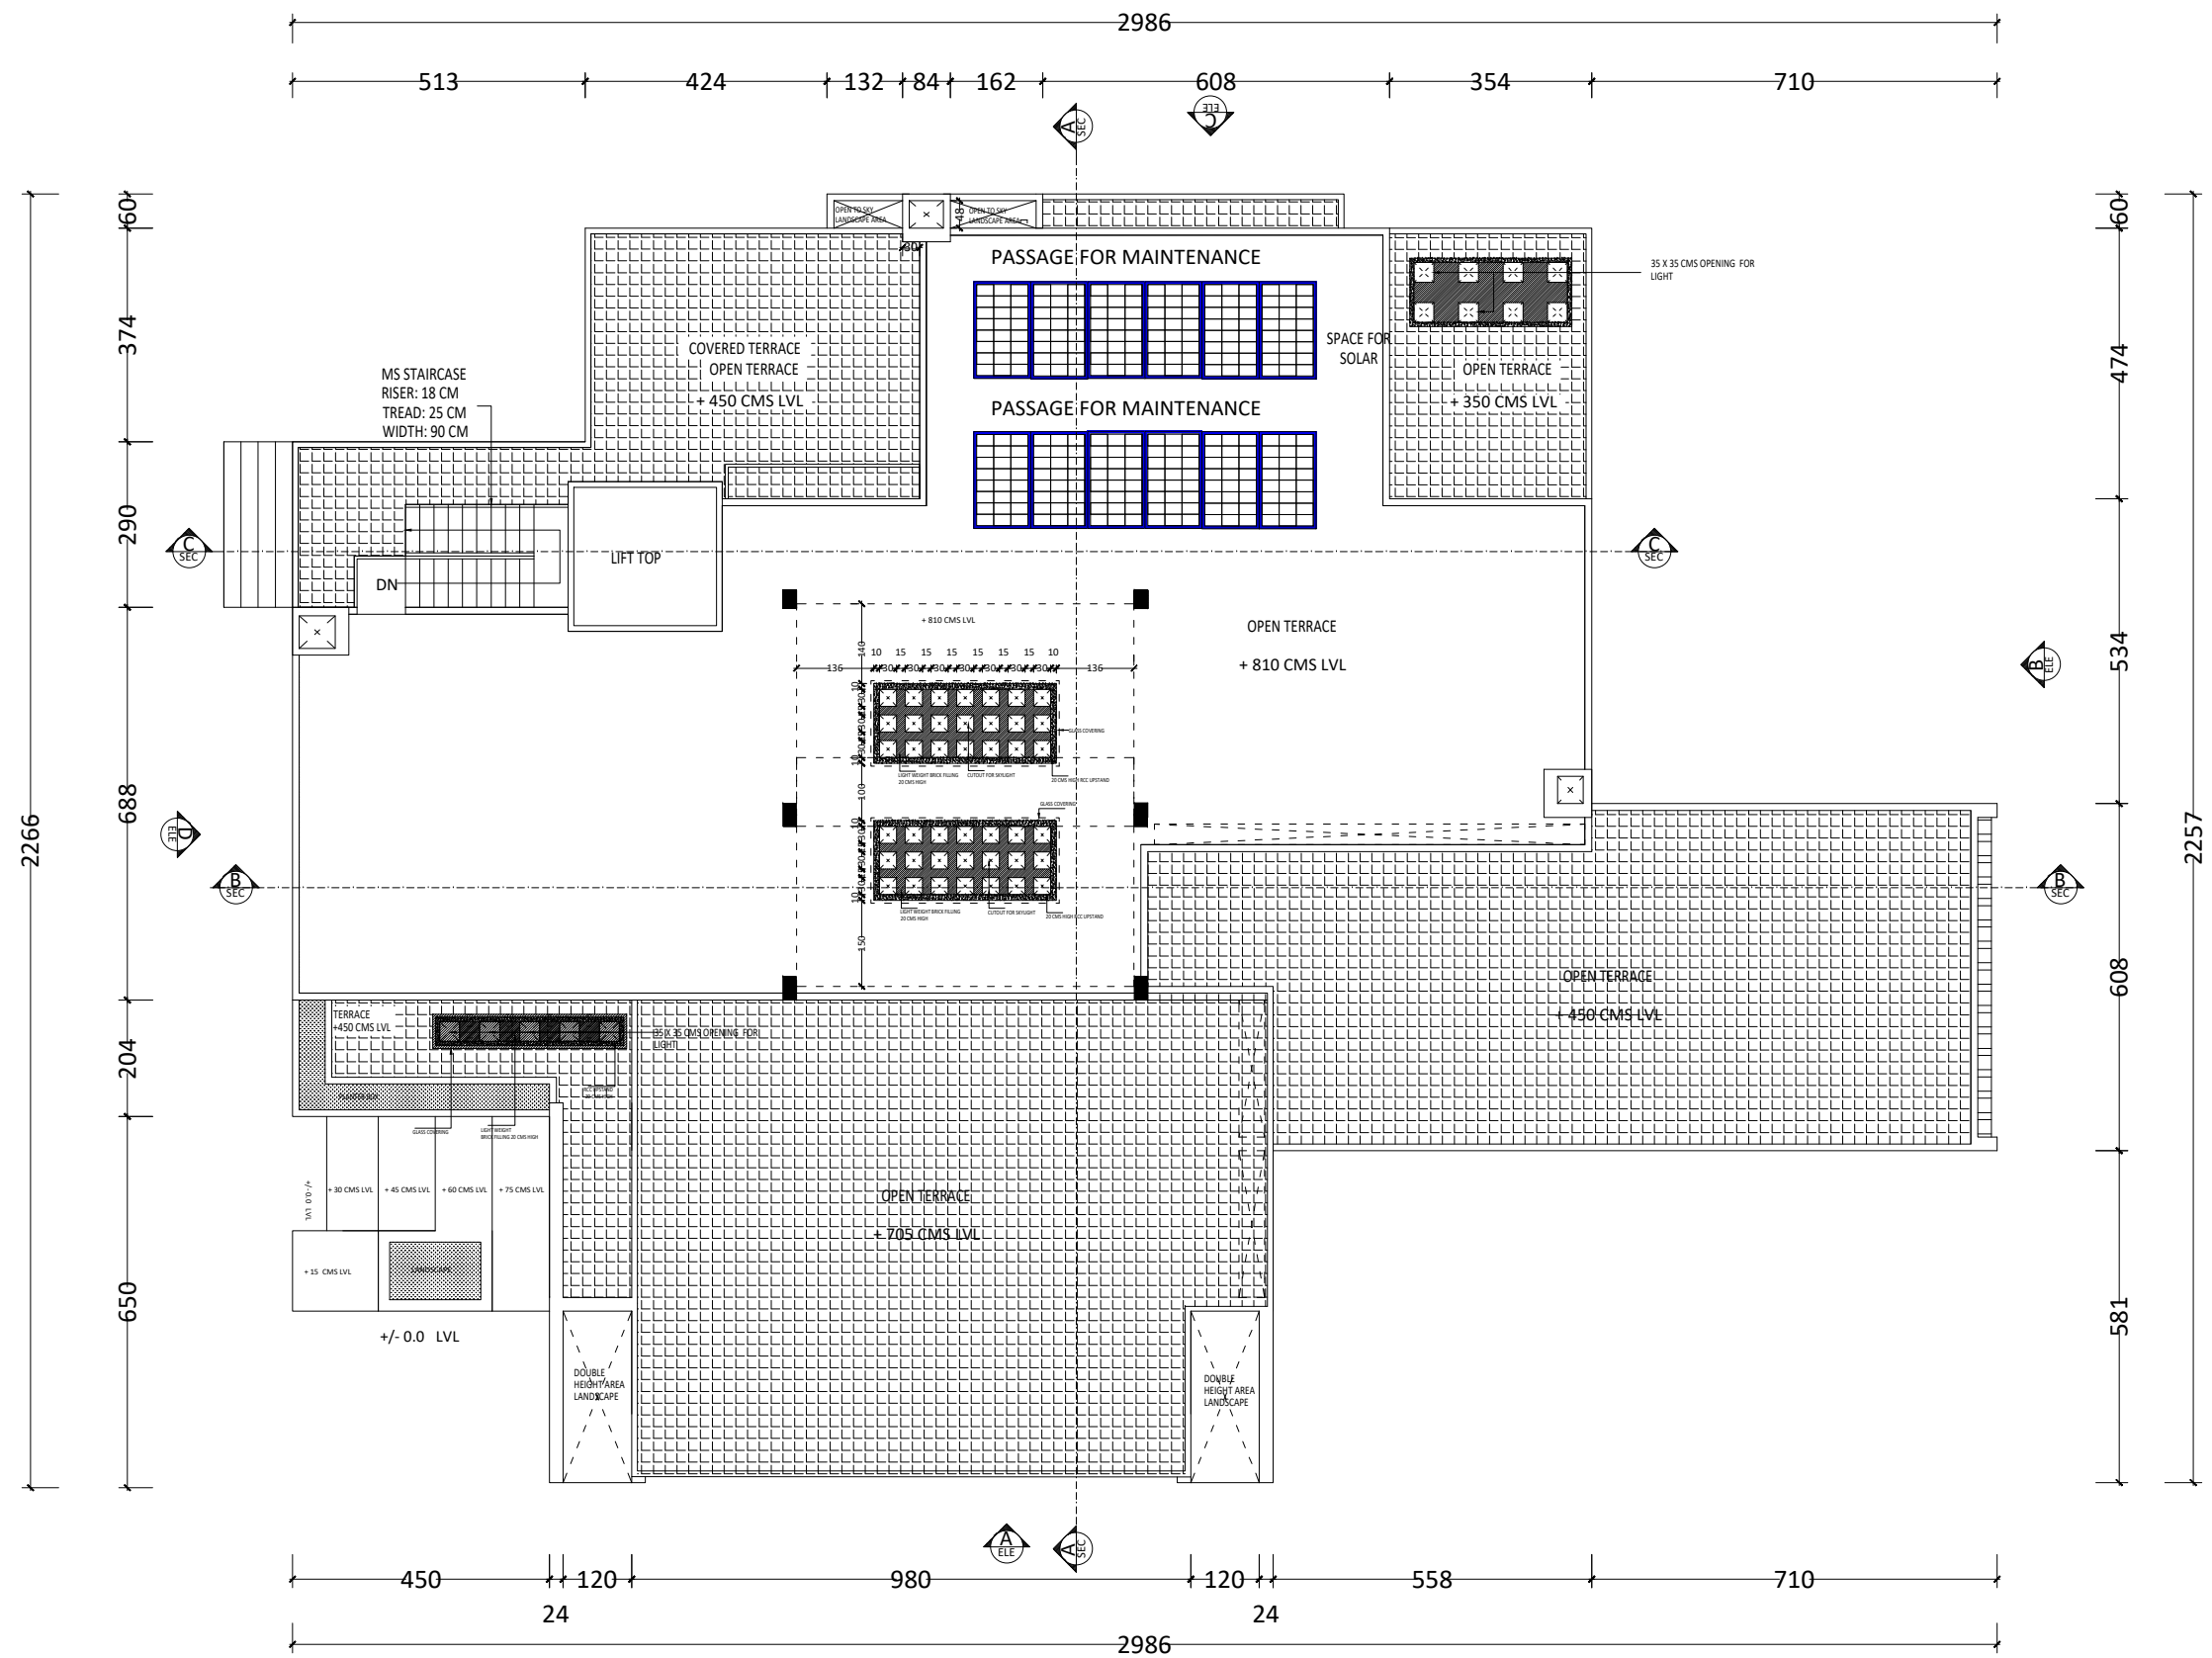

TERRACE FLOOR

DATE: 03.05.2021

SCALE : NA

DRAWN: AP

CHECKED: ANEENA

PROJECT NO:496

PROJECT: RESIDENTIAL PROJECT AT
RAMESHWARAM

CLIENT: MIJULAL AND RADHIKA

DRAWING TITLE:
TERRACE FLOOR PLAN - BRICK WORK

REVISION:26.08.2022

R1 Changes as per Interiors



NOTES:

- ALL DIMENSIONS ARE IN CMS, UNLESS OTHERWISE SPECIFIED
- DIMENSIONS SHALL NOT BE MEASURED DIRECTLY FROM THIS DRAWINGS.
FOLLOW ONLY WRITTEN DIMENSIONS
- IN THE EVENT OF ANY DISCREPANCY OR DIFFERENCE BETWEEN ANY
DRAWINGS OR SITE CONDITIONS OR OTHERWISE IMMEDIATE REFERENCE
IS TO BE MADE TO THE DESIGNER FOR CLARIFICATION PRIOR TO EXECUTION
OF WORK AT SITE
- ALL THE CIVIL WORKS SHOULD BE IN LINE LEVEL AND PLUMB.
- PLASTERING TO BE CUT AT SKIRTING LEVEL.