



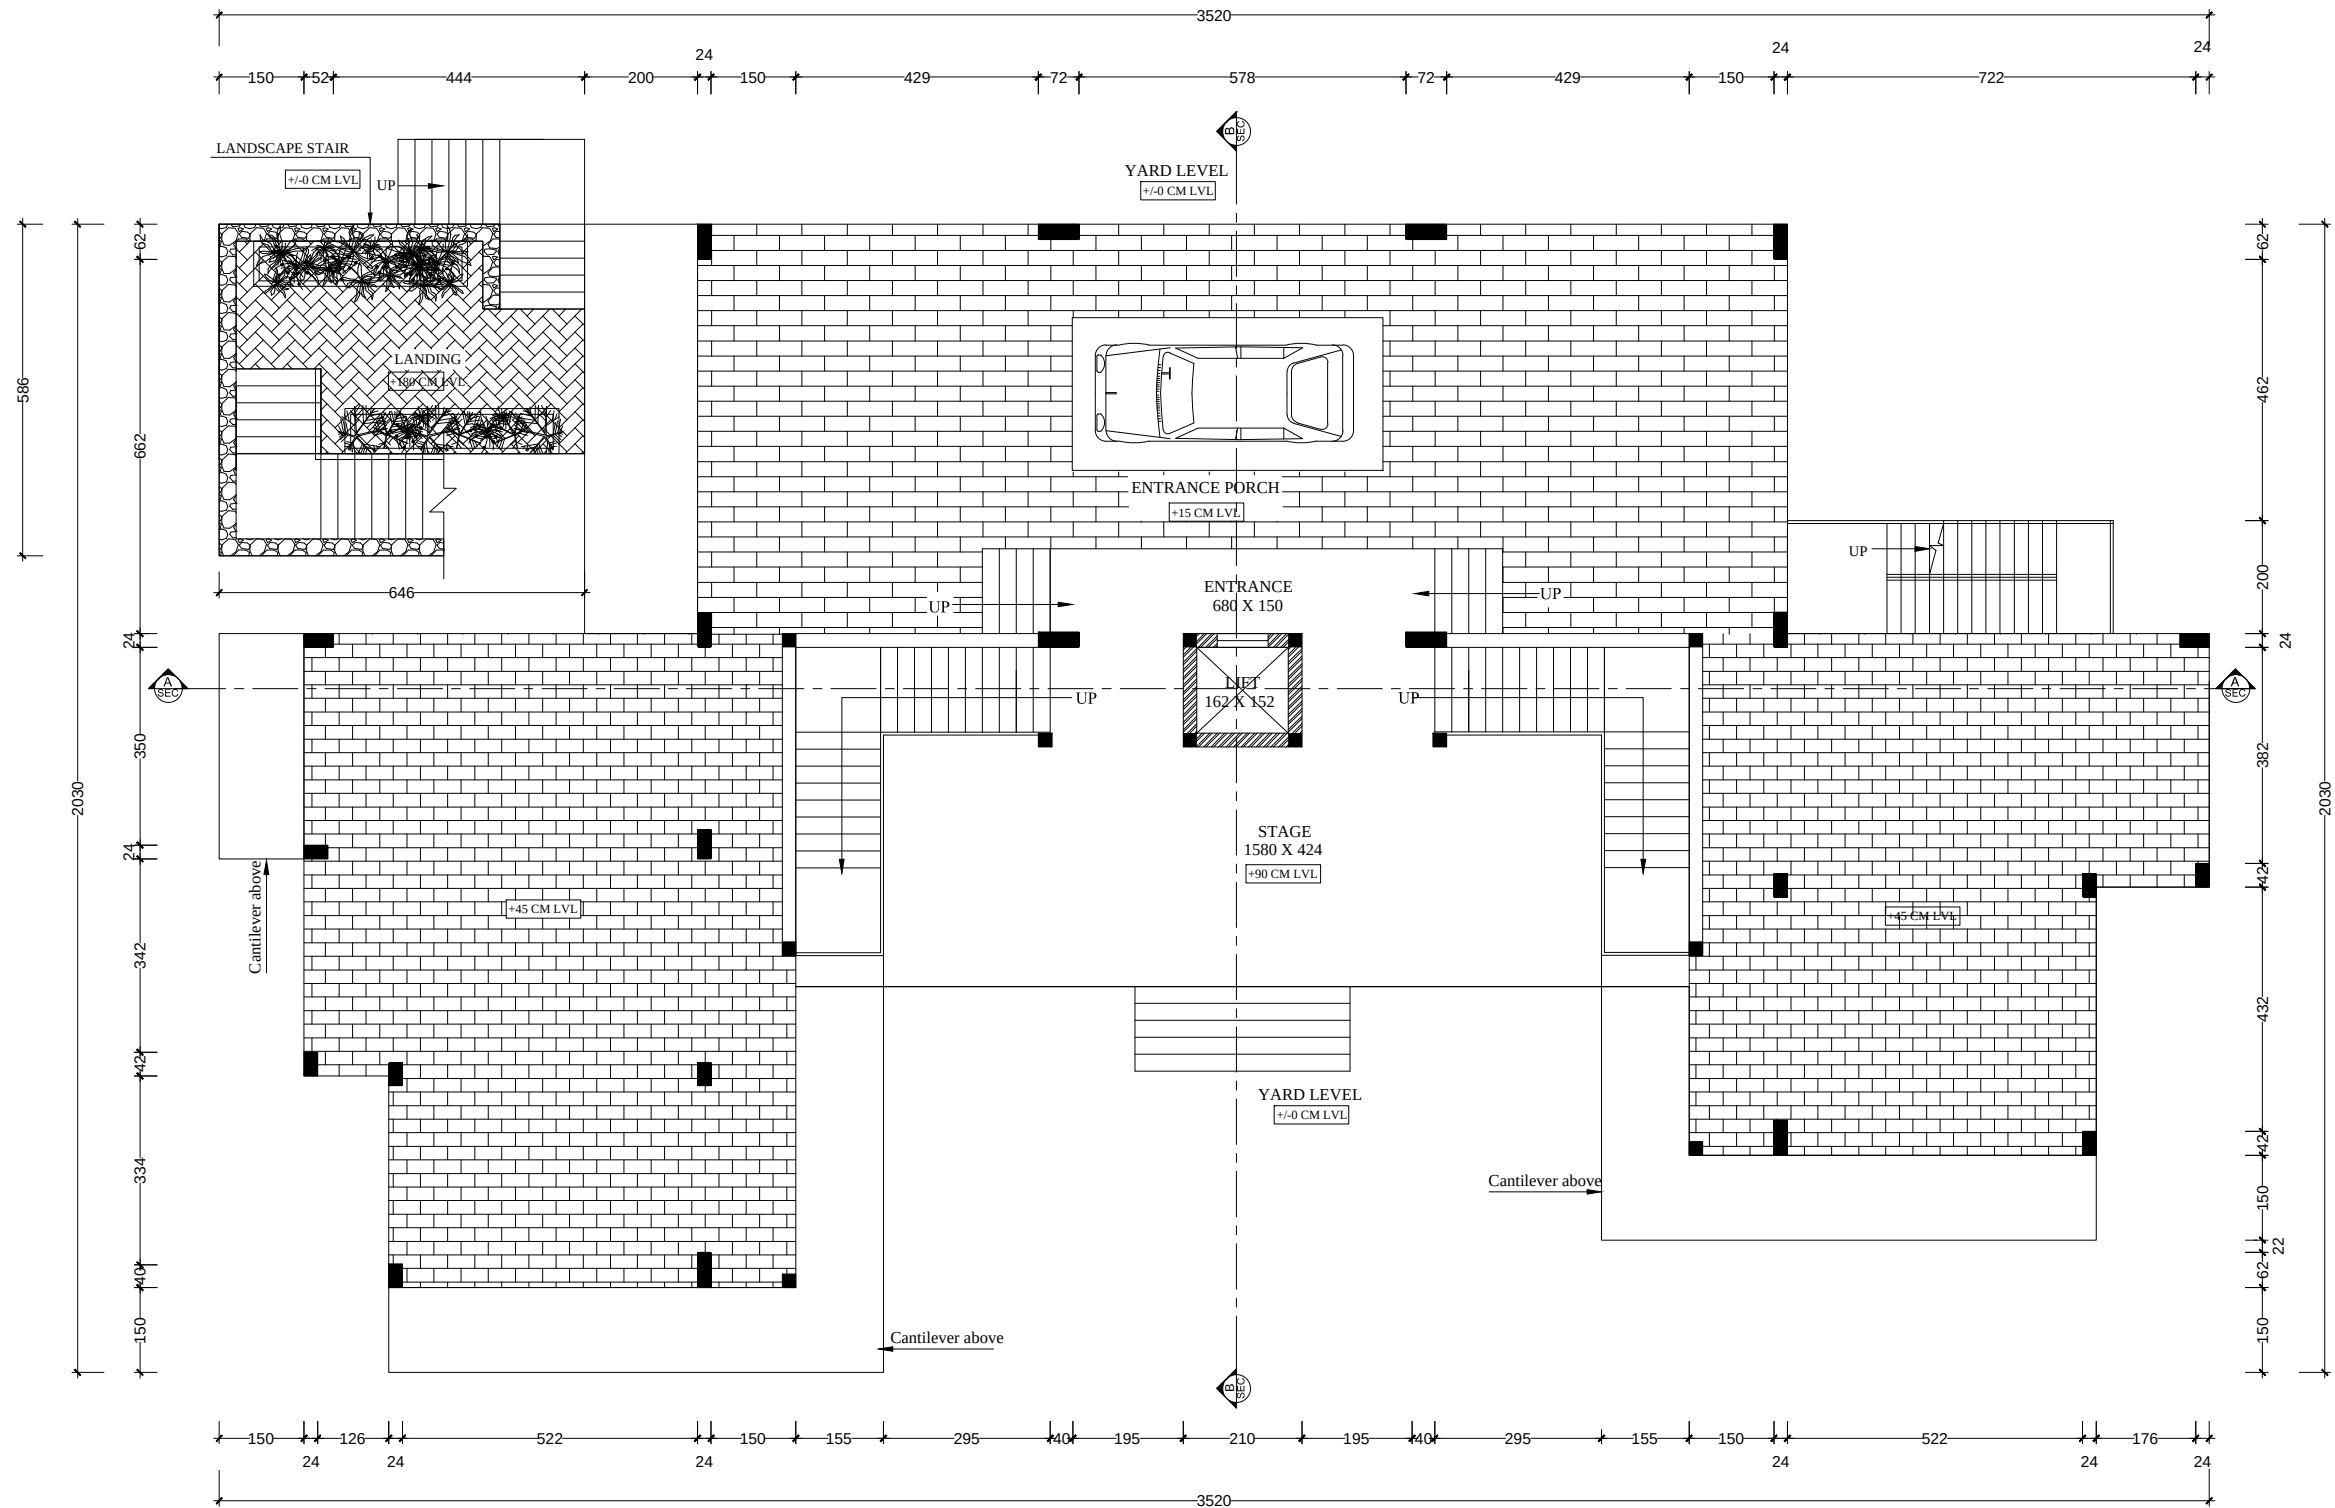

GROUND (STILT) FLOOR PLAN

Area:-358.78 M2 (3860 SQFT)

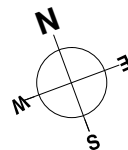

DATE: 12.07.2019

SCALE : NA

DRAWN: JJ

CHECKED: ANEENA

PROJECT NO:


CLIENT: ABEESH MUHAMMAD

PROJECT: RESIDENTIAL PROJECT AT
VAYALKKARA, MANJALY

DRAWING TITLE: STILT/GROUND FLOOR PLAN

REVISION:

- | | |
|---|---|
| 1 | REV. AS PER CLIENT REQUIREMENT - 1.4.19 |
| 2 | REV. FOR BALCONY AS PER CLIENT REQUIREMENT - 3.4.19 |

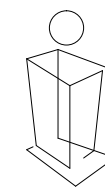

AHANAS

ALL DIMENSIONS ARE IN CMS

NO DIMENSIONS TO BE SCALED OFF FROM
DRAWINGS ONLY WRITTEN DIMENSIONS TO BE

IN THE EVENT OF ANY DISCREPANCY OR
DIFFERENCE BETWEEN ANY INTERIOR DRAWINGS
OR SITE CONDITIONS OR OTHERWISE IMMEDIATE
REFERENCE IS TO BE MADE TO THE DESIGNER
FOR CLARIFICATION PRIOR TO EXECUTION OF
WORK AT SITE