

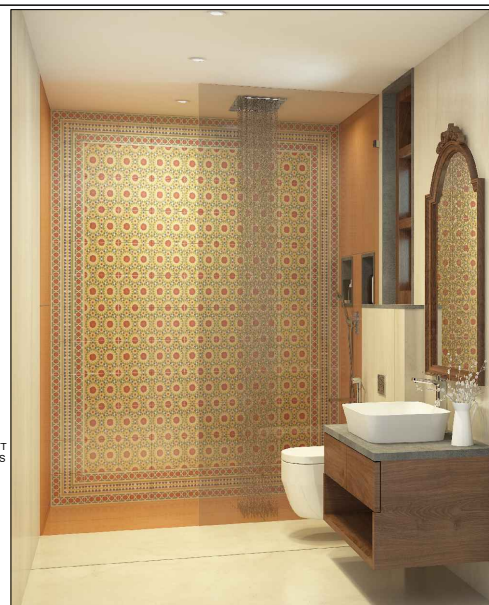
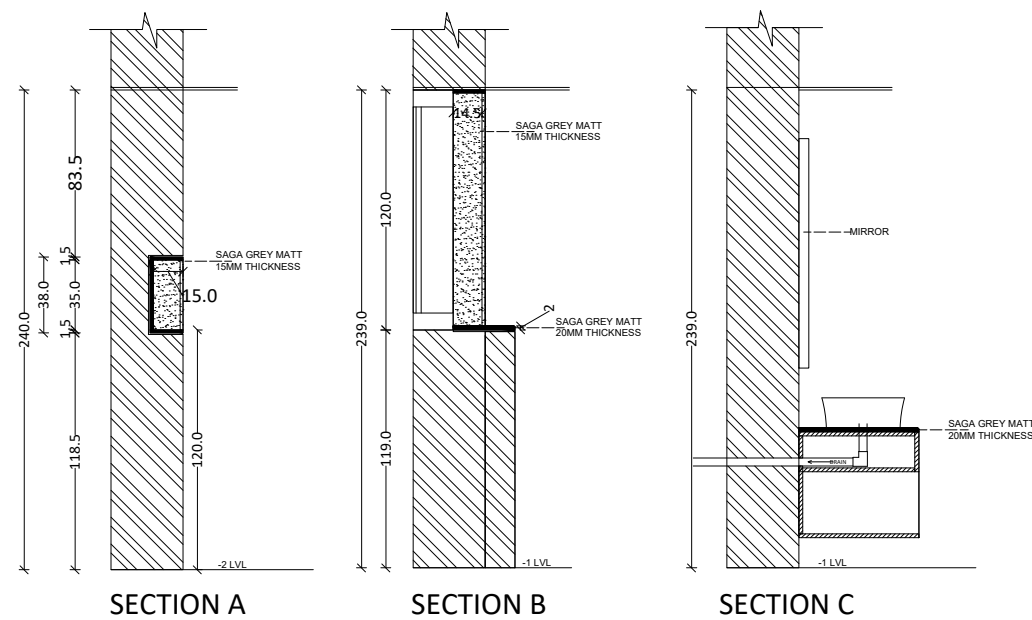
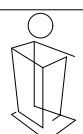
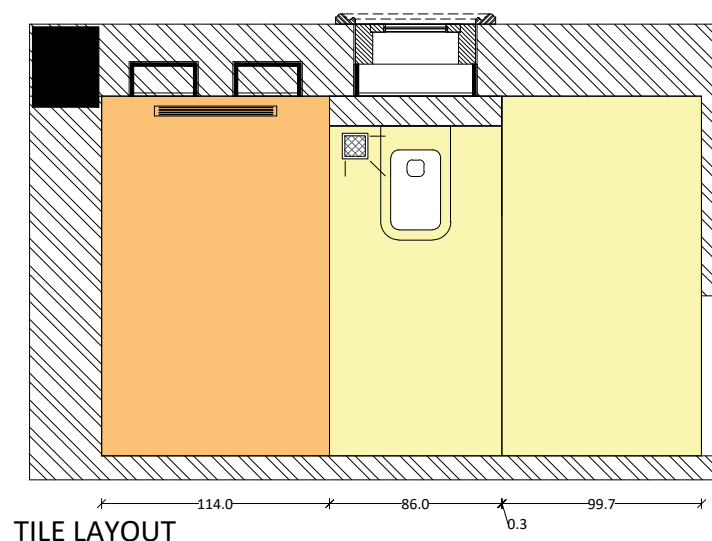
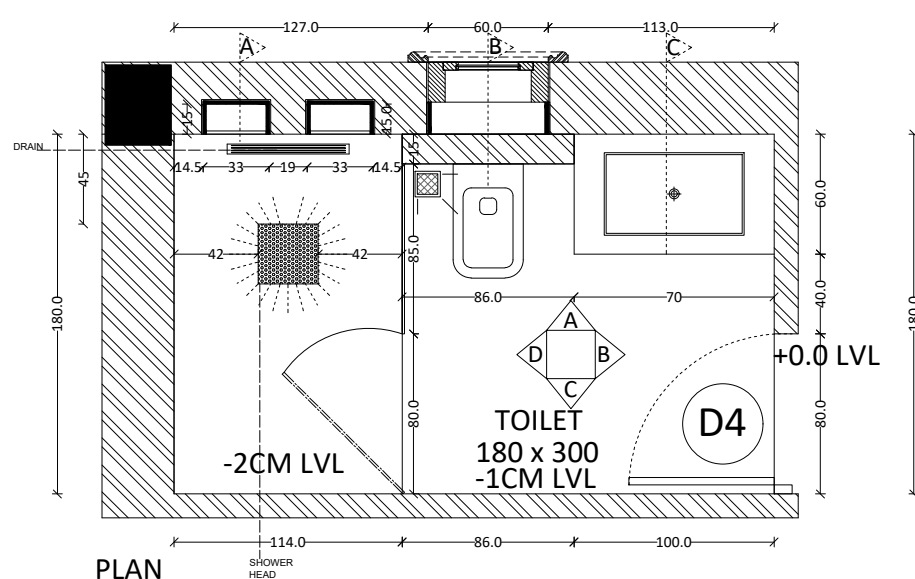
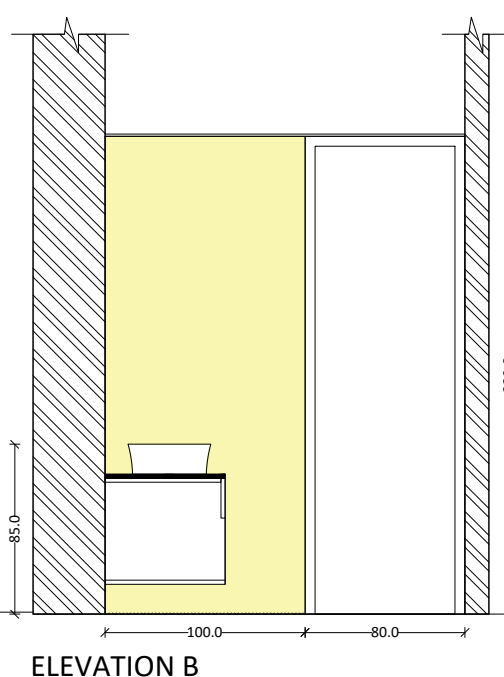
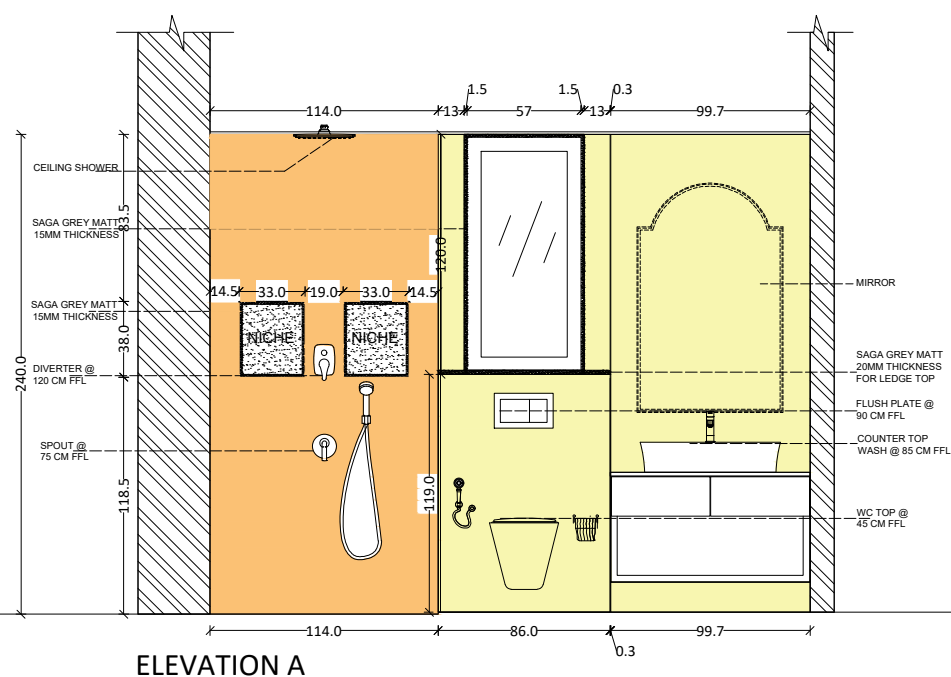


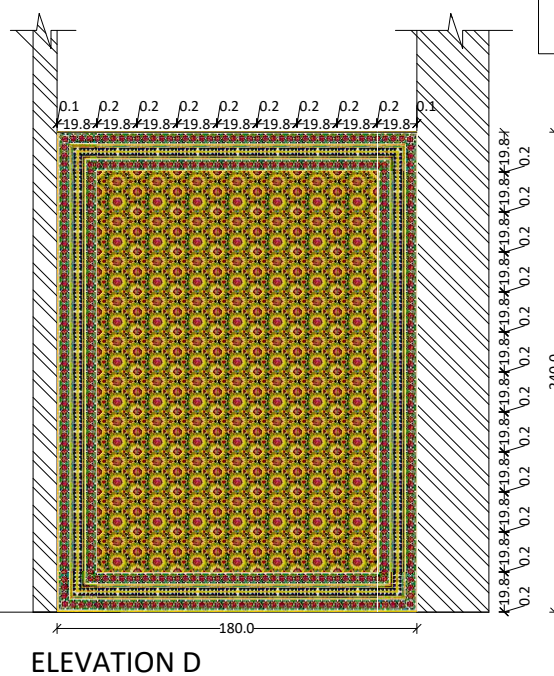

	WET AREA FLOOR & WALL - SIMPOLO SPECTRA CHILLI 240x120 CM WITH 3MM SPACER
	DRY AREA FLOOR & WALL (WC & WASH)- NEXION CREMA EUROPA 240 x 120 CM WITH 3MM SPACER
	NICHE & TOP OF LEDGE WALL - SAGA GREY POLISH 300x80 CM 15MM & 20MM THICKNESS
	HIGHLIGHT WALL WET AREA - FOLKSTAR CORNER 19.8CM x 19.8CM WITH 2MM SPACER
	HIGHLIGHT WALL WET AREA - FOLKSTAR BORDER 19.8CMx19.8CM WITH 2MM SPACER
	HIGHLIGHT WALL WET AREA - FOLKSTAR BASE 19.8CM x 19.8CM WITH 2MM SPACER

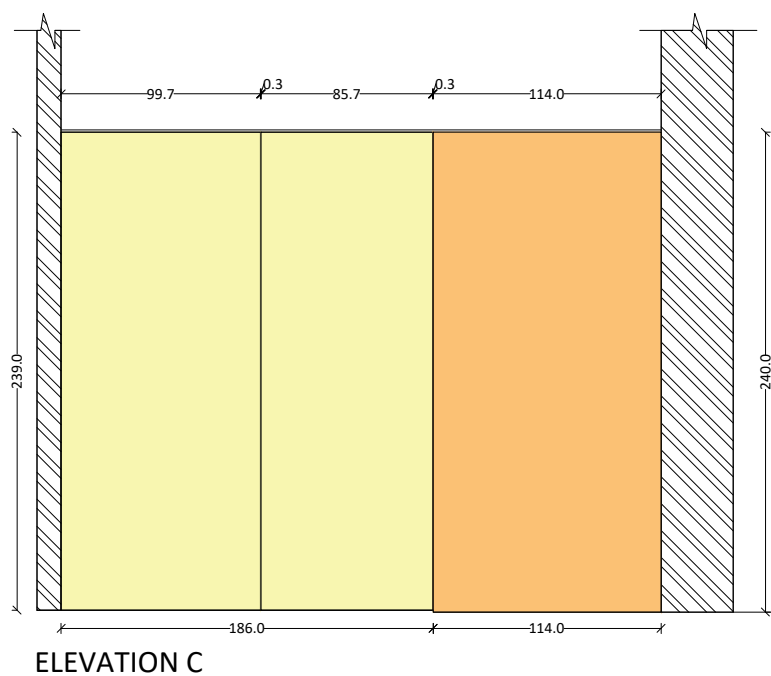

A'HANAS

PROJECT:
FARM HOUSE @ TIRUNELVELI

REVISION:

DWG TITLE:BED1 TOILET DETAILS
(NEAR KITCHEN)

DRAWN: AA

DATE: 23.05.2024

CHECKED:

REVISÉD DATE: 28 06 2024

REVISION NO:

SCALE: NTS

ALL DIMENSIONS ARE IN CMS
No dimensions to be scaled off from the drawings only written dimensions to be.
In the event of any discrepancy or difference between any interior drawings or site conditions or other wise immediate reference is to be made to the designer for clarification prior to execution of work at site