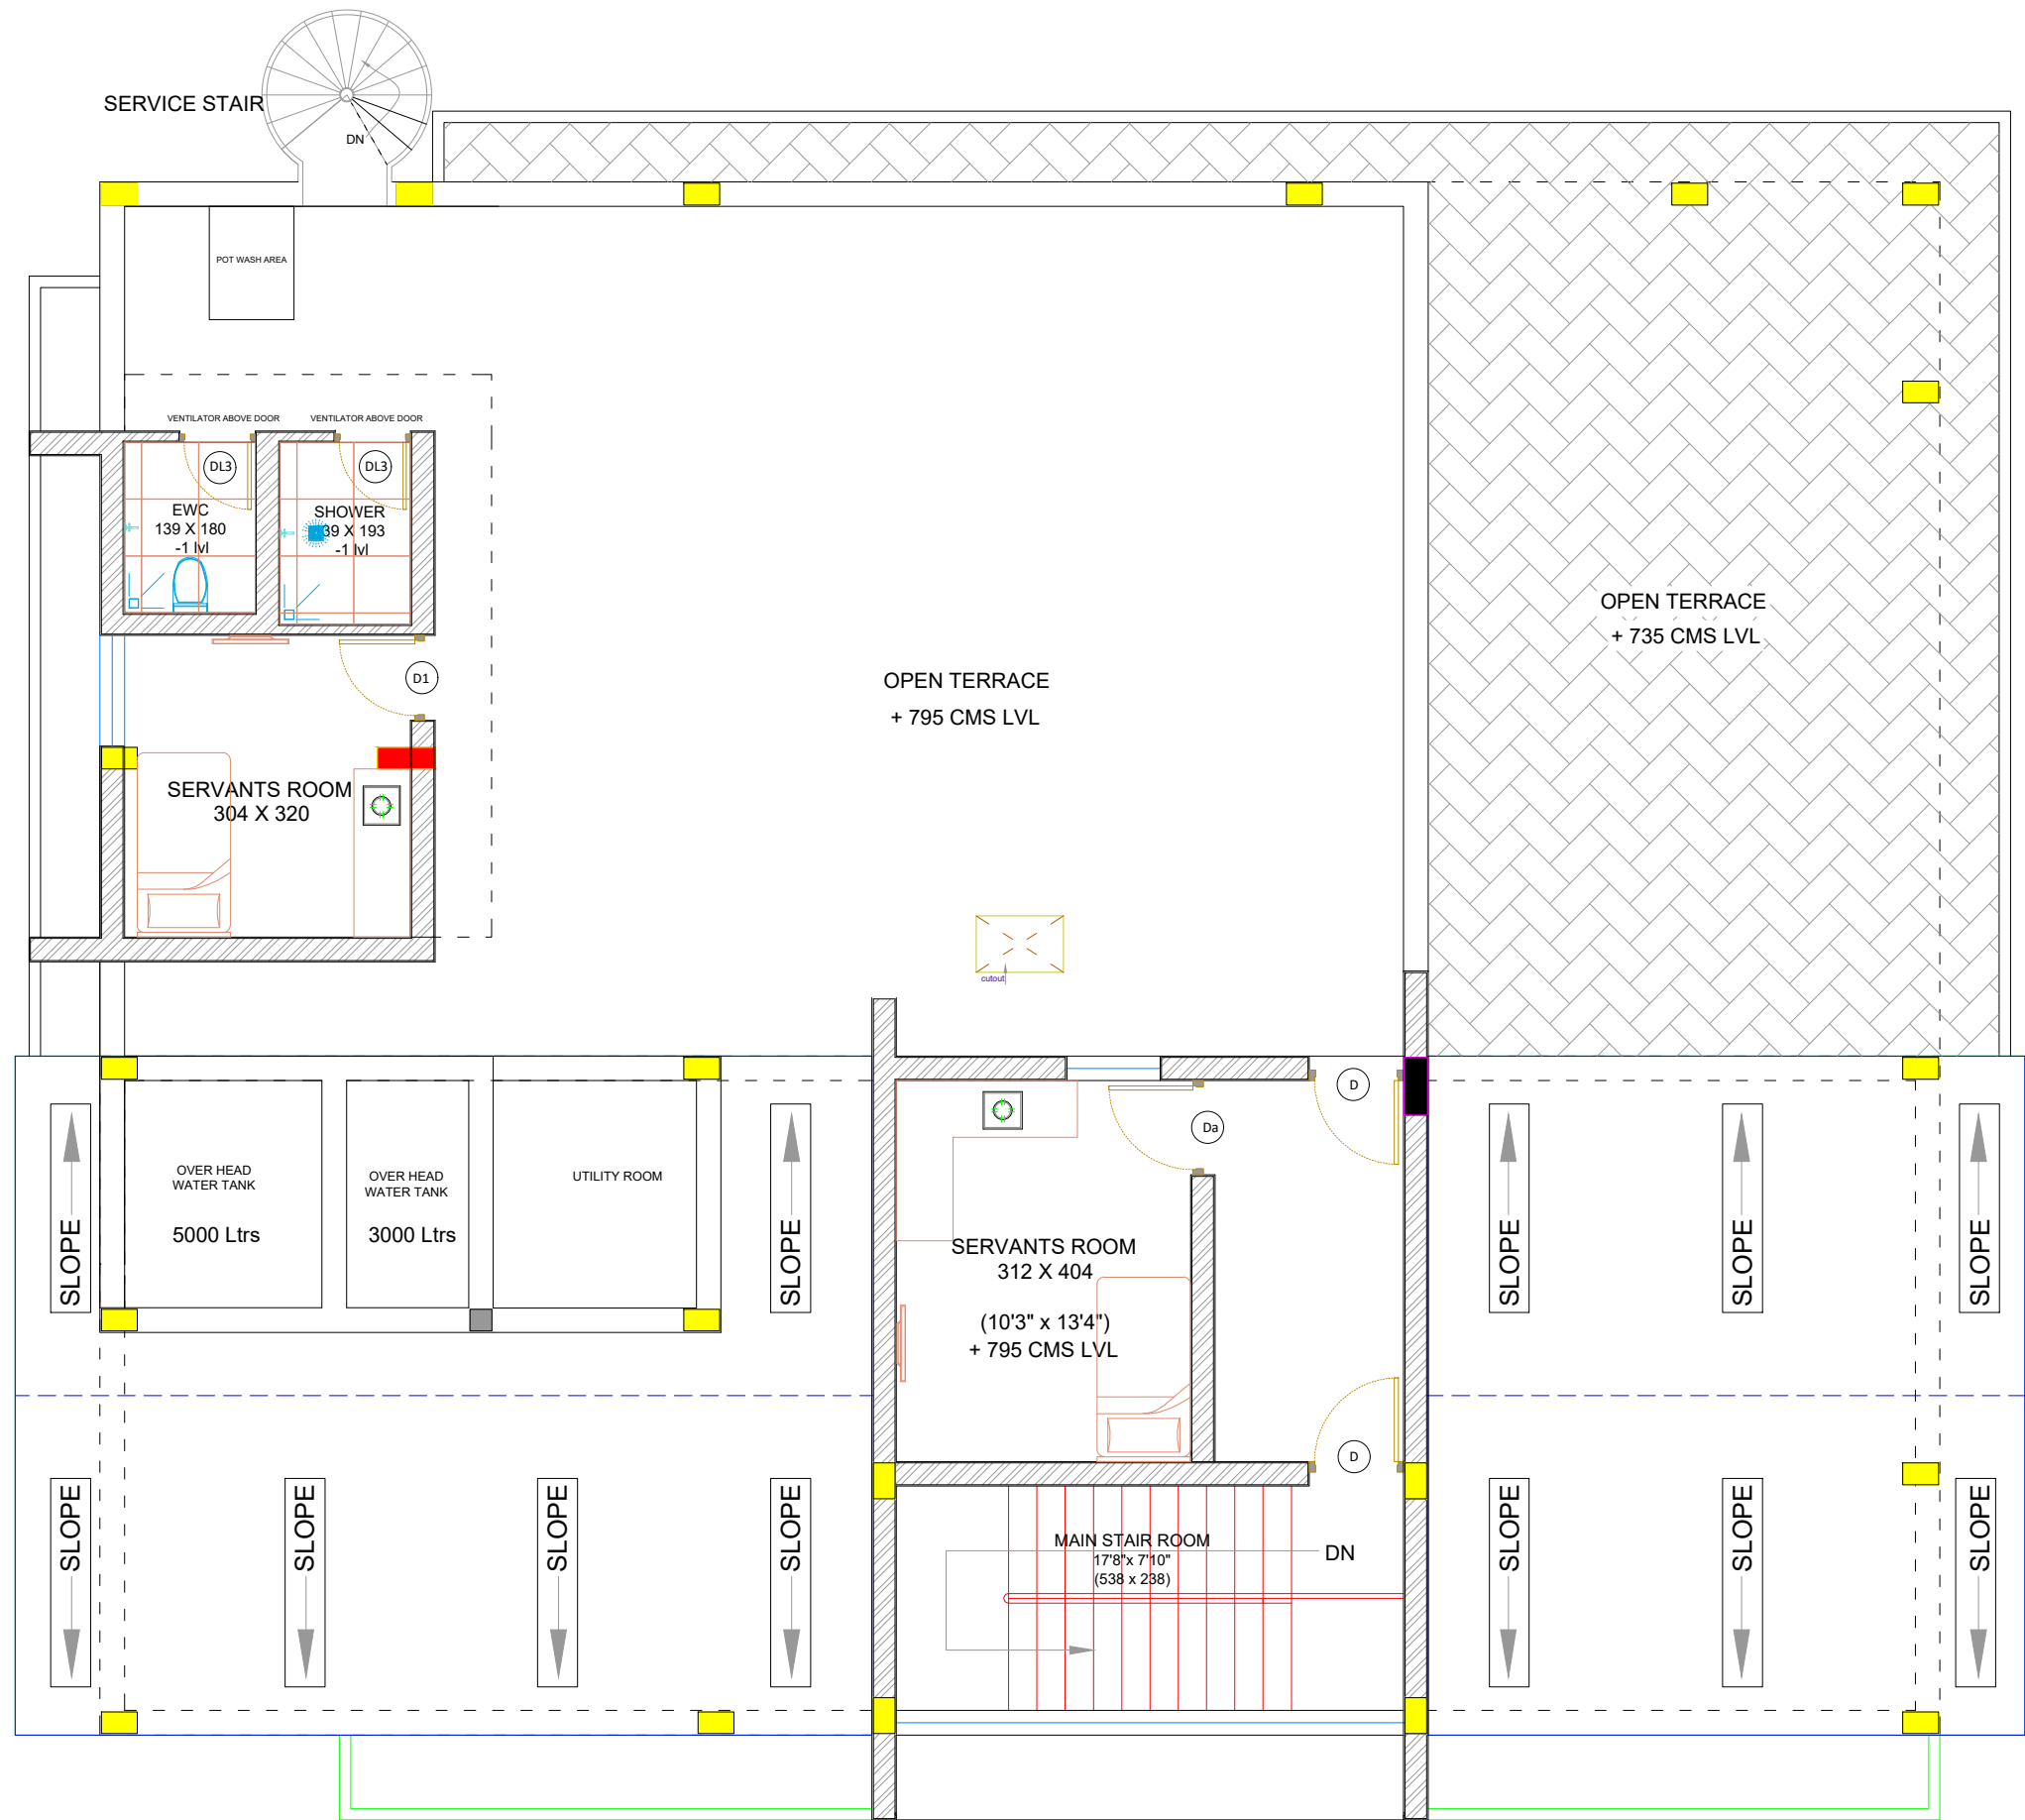


DATE: 02/02/2024

SCALE :NTS

DRAWN: ARYA

CHECKED:


PROJECT : NATARAJ NILAYAM
(RESIDENCE AT TIRUPPUR)

CLIENT: MR. VIJAYARAGHAVAN

DRAWING TITLE: TERRACE FLOOR PLAN
(WORKING DRAWING)

REVISION: R2

SERVANT ROOM ADDED IN TERRACE

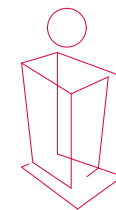

AH'ANAS

NOTES:

- ALL DIMENSIONS ARE IN CMS, UNLESS OTHERWISE SPECIFIED
- DIMENSIONS SHALL NOT BE MEASURED DIRECTLY FROM THIS DRAWINGS.
FOLLOW ONLY WRITTEN DIMENSIONS
- IN THE EVENT OF ANY DISCREPANCY OR DIFFERENCE BETWEEN ANY
DRAWINGS OR SITE CONDITIONS OR OTHERWISE IMMEDIATE REFERENCE
IS TO BE MADE TO THE DESIGNER FOR CLARIFICATION PRIOR TO EXECUTION
OF WORK AT SITE
- ALL THE CIVIL WORKS SHOULD BE IN LINE LEVEL AND PLUMB.
- PLASTERING TO BE CUT AT SKIRTING LEVEL.