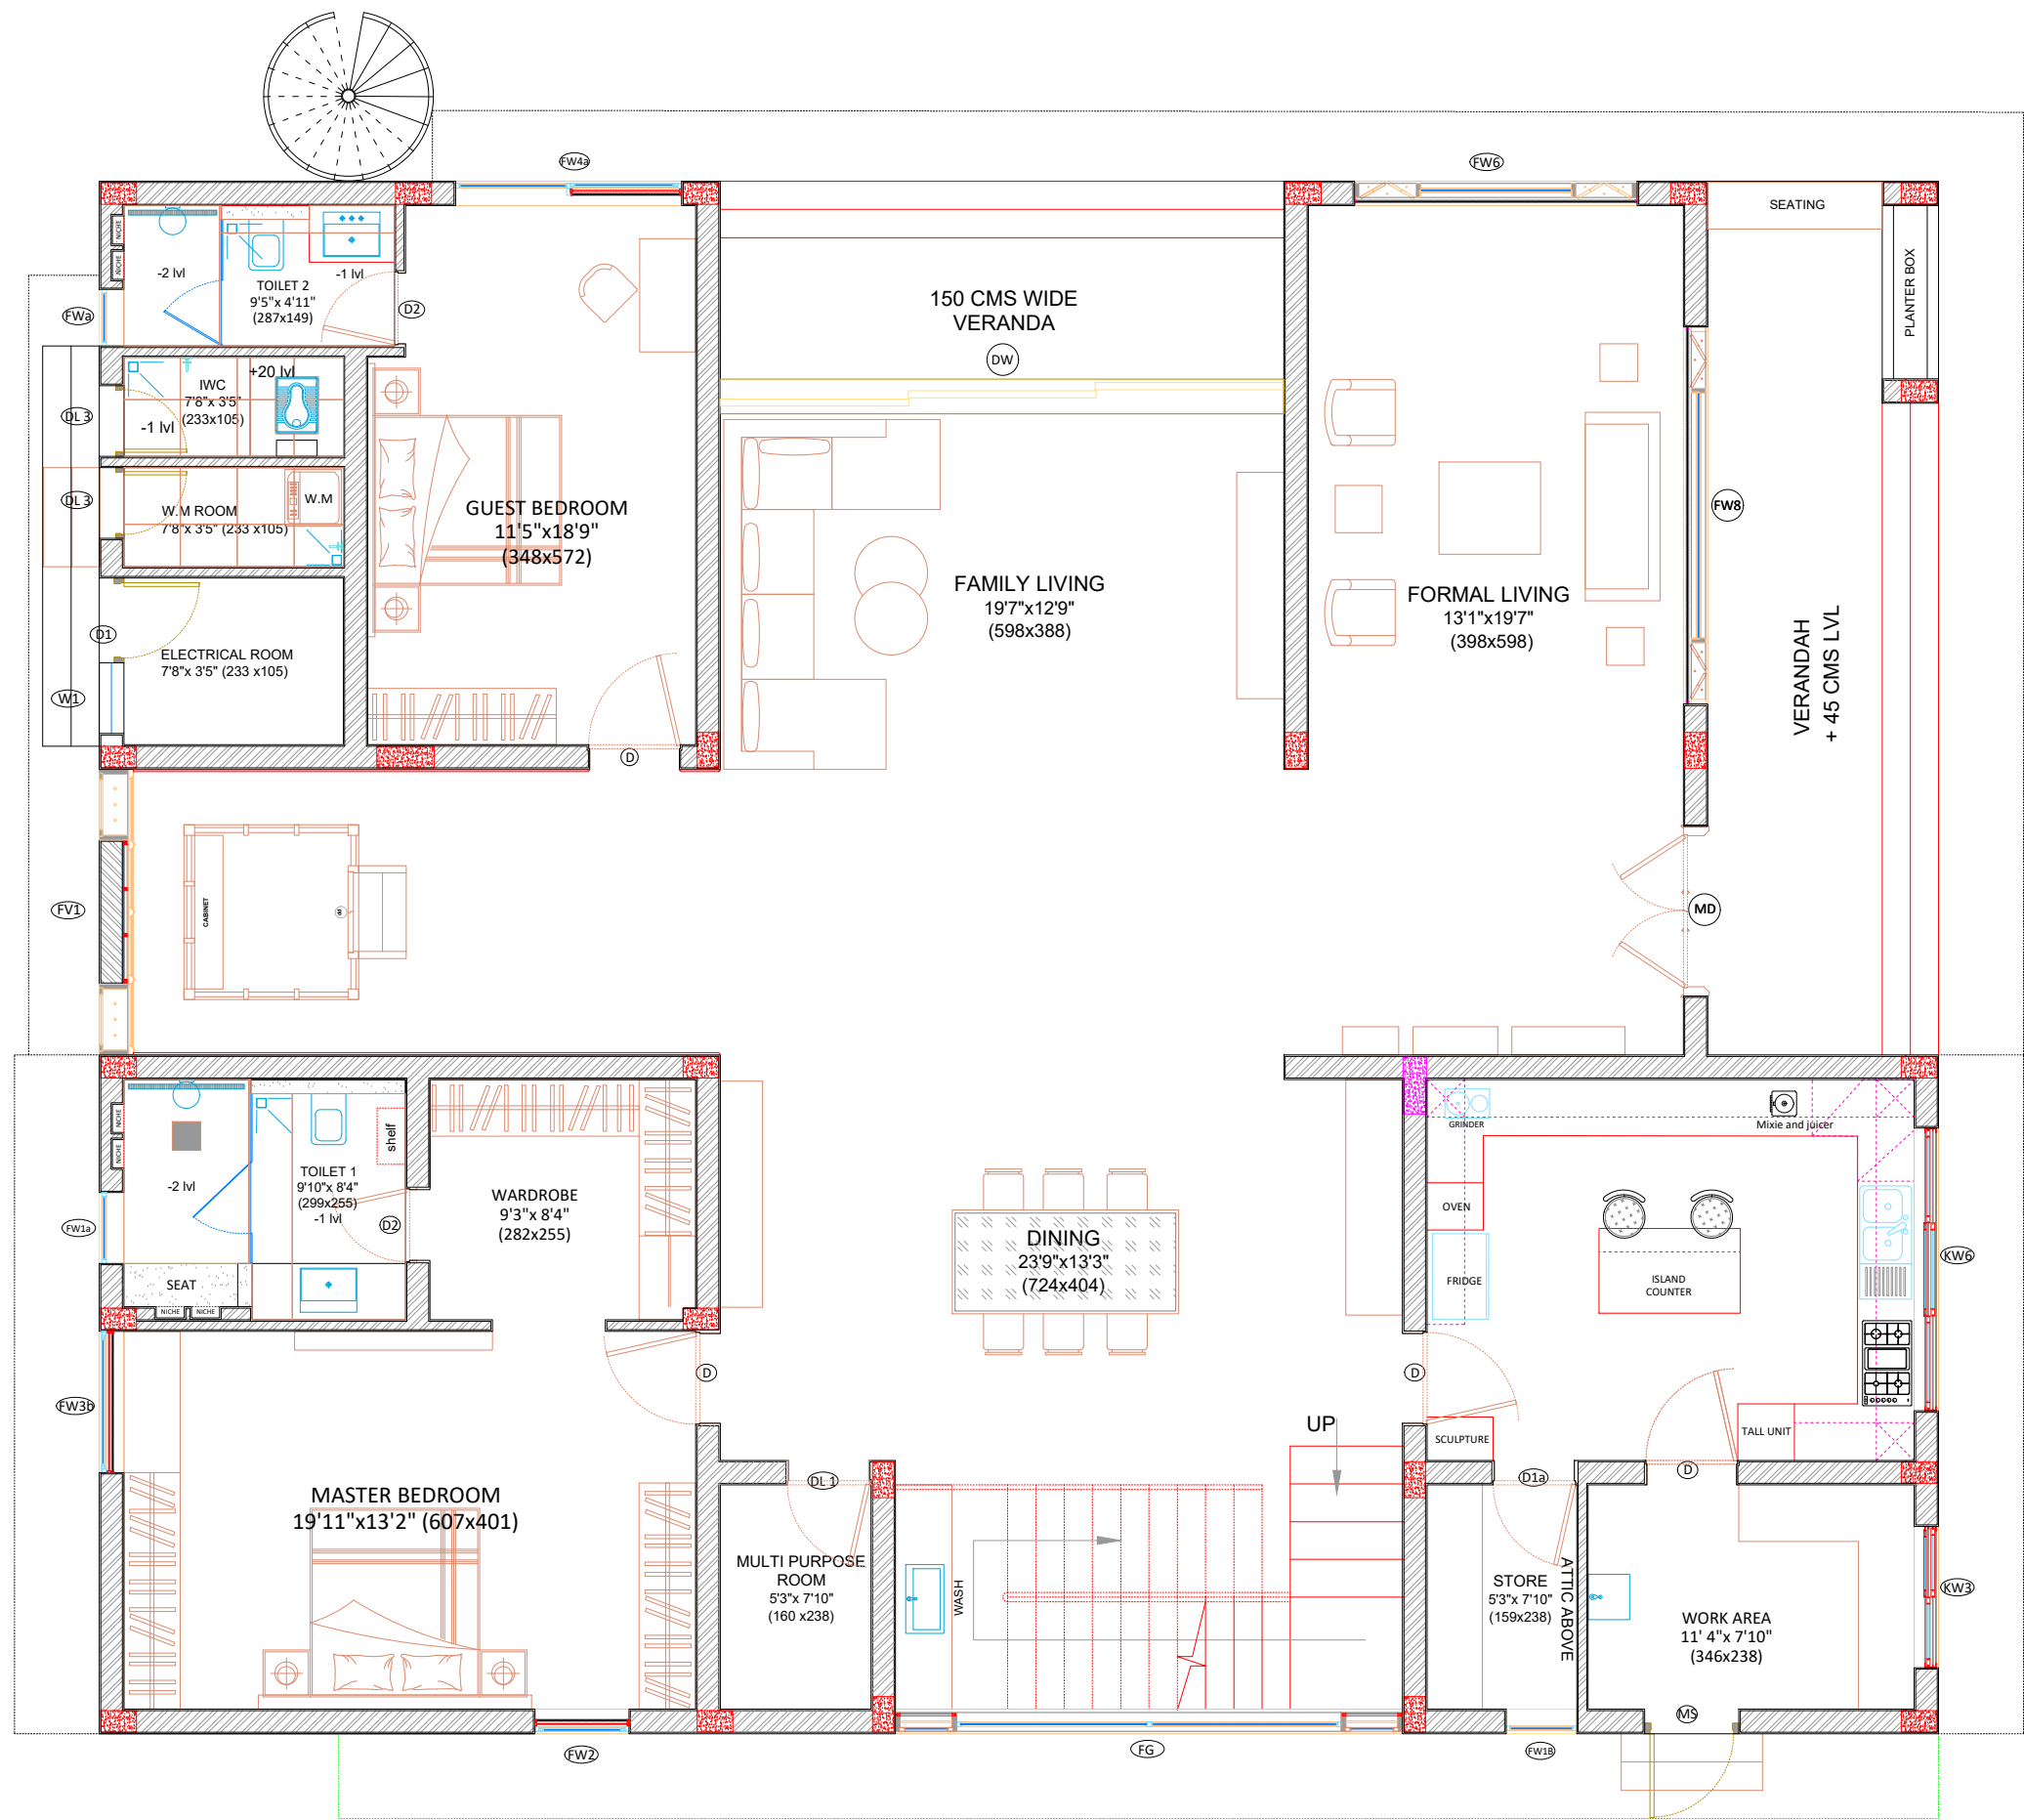


DATE: 02/02/2024

SCALE :NTS

DRAWN: ARYA

CHECKED:


PROJECT : NATARAJ NILAYAM
(RESIDENCE AT TIRUPPUR)

CLIENT: MR. VIJAYARAGHAVAN

DRAWING TITLE: GROUND FLOOR PLAN
(INTERIOR)

REVISION: R4

05/09/22	REVISED WALL THICKNESS AS PER BRICK SIZE
16/01/23	REVISED SERVANT ROOM AND TOILETS
27/01/23	ADDED INNER WALL BRICKWORK MEASUREMENT
10/02/23	INCREASED WALL TK OF M. TOILET DOOR AREA TO 9 INCH. MASTER-BEDROOM WINDOW POSITION CHANGED. KITCHEN DOOR POSITION ADJUSTED AS PER VASTU REQUIREMENTS
16/02/23	ADJUSTED THE DOOR AND WINDOW IN GUESTROOM AS PER VASTU SUGGESTION. M. TOILET LAYOUT CHANGED AS PER CLIENT REQUEST

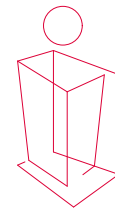

A'HANAS

NOTES:

- ALL DIMENSIONS ARE IN CMS, UNLESS OTHERWISE SPECIFIED
- DIMENSIONS SHALL NOT BE MEASURED DIRECTLY FROM THIS DRAWINGS. FOLLOW ONLY WRITTEN DIMENSIONS
- IN THE EVENT OF ANY DISCREPANCY OR DIFFERENCE BETWEEN ANY DRAWINGS OR SITE CONDITIONS OR OTHERWISE IMMEDIATE REFERENCE IS TO BE MADE TO THE DESIGNER FOR CLARIFICATION PRIOR TO EXECUTION OF WORK AT SITE
- ALL THE CIVIL WORKS SHOULD BE IN LINE LEVEL AND PLUMB.
- PLASTERING TO BE CUT AT SKIRTING LEVEL.