



PROPOSED TOURIST HOME AT AGATTI

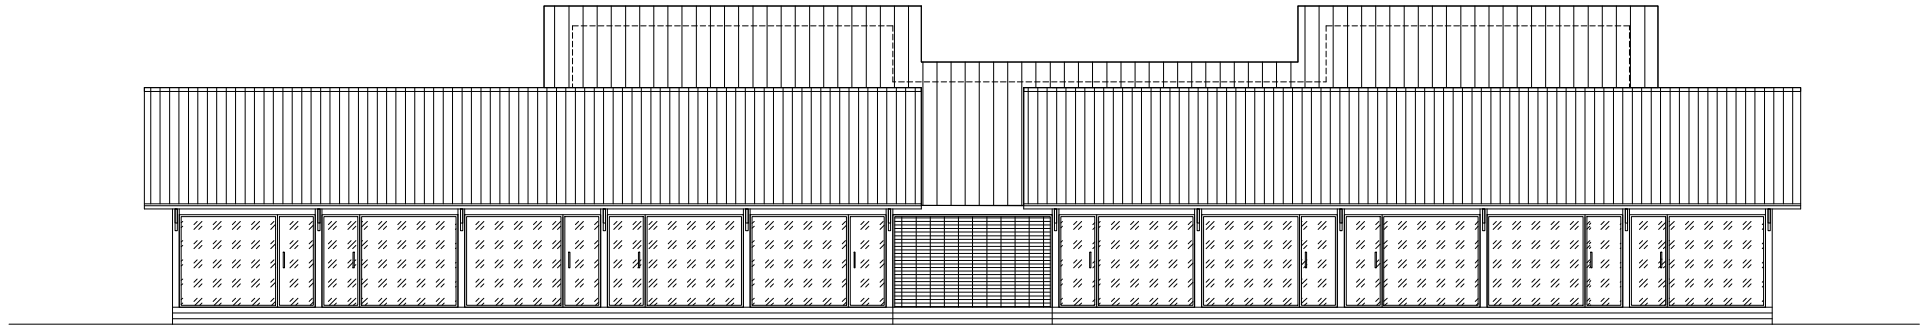



FRONT ELEVATION

SCALE 1:100

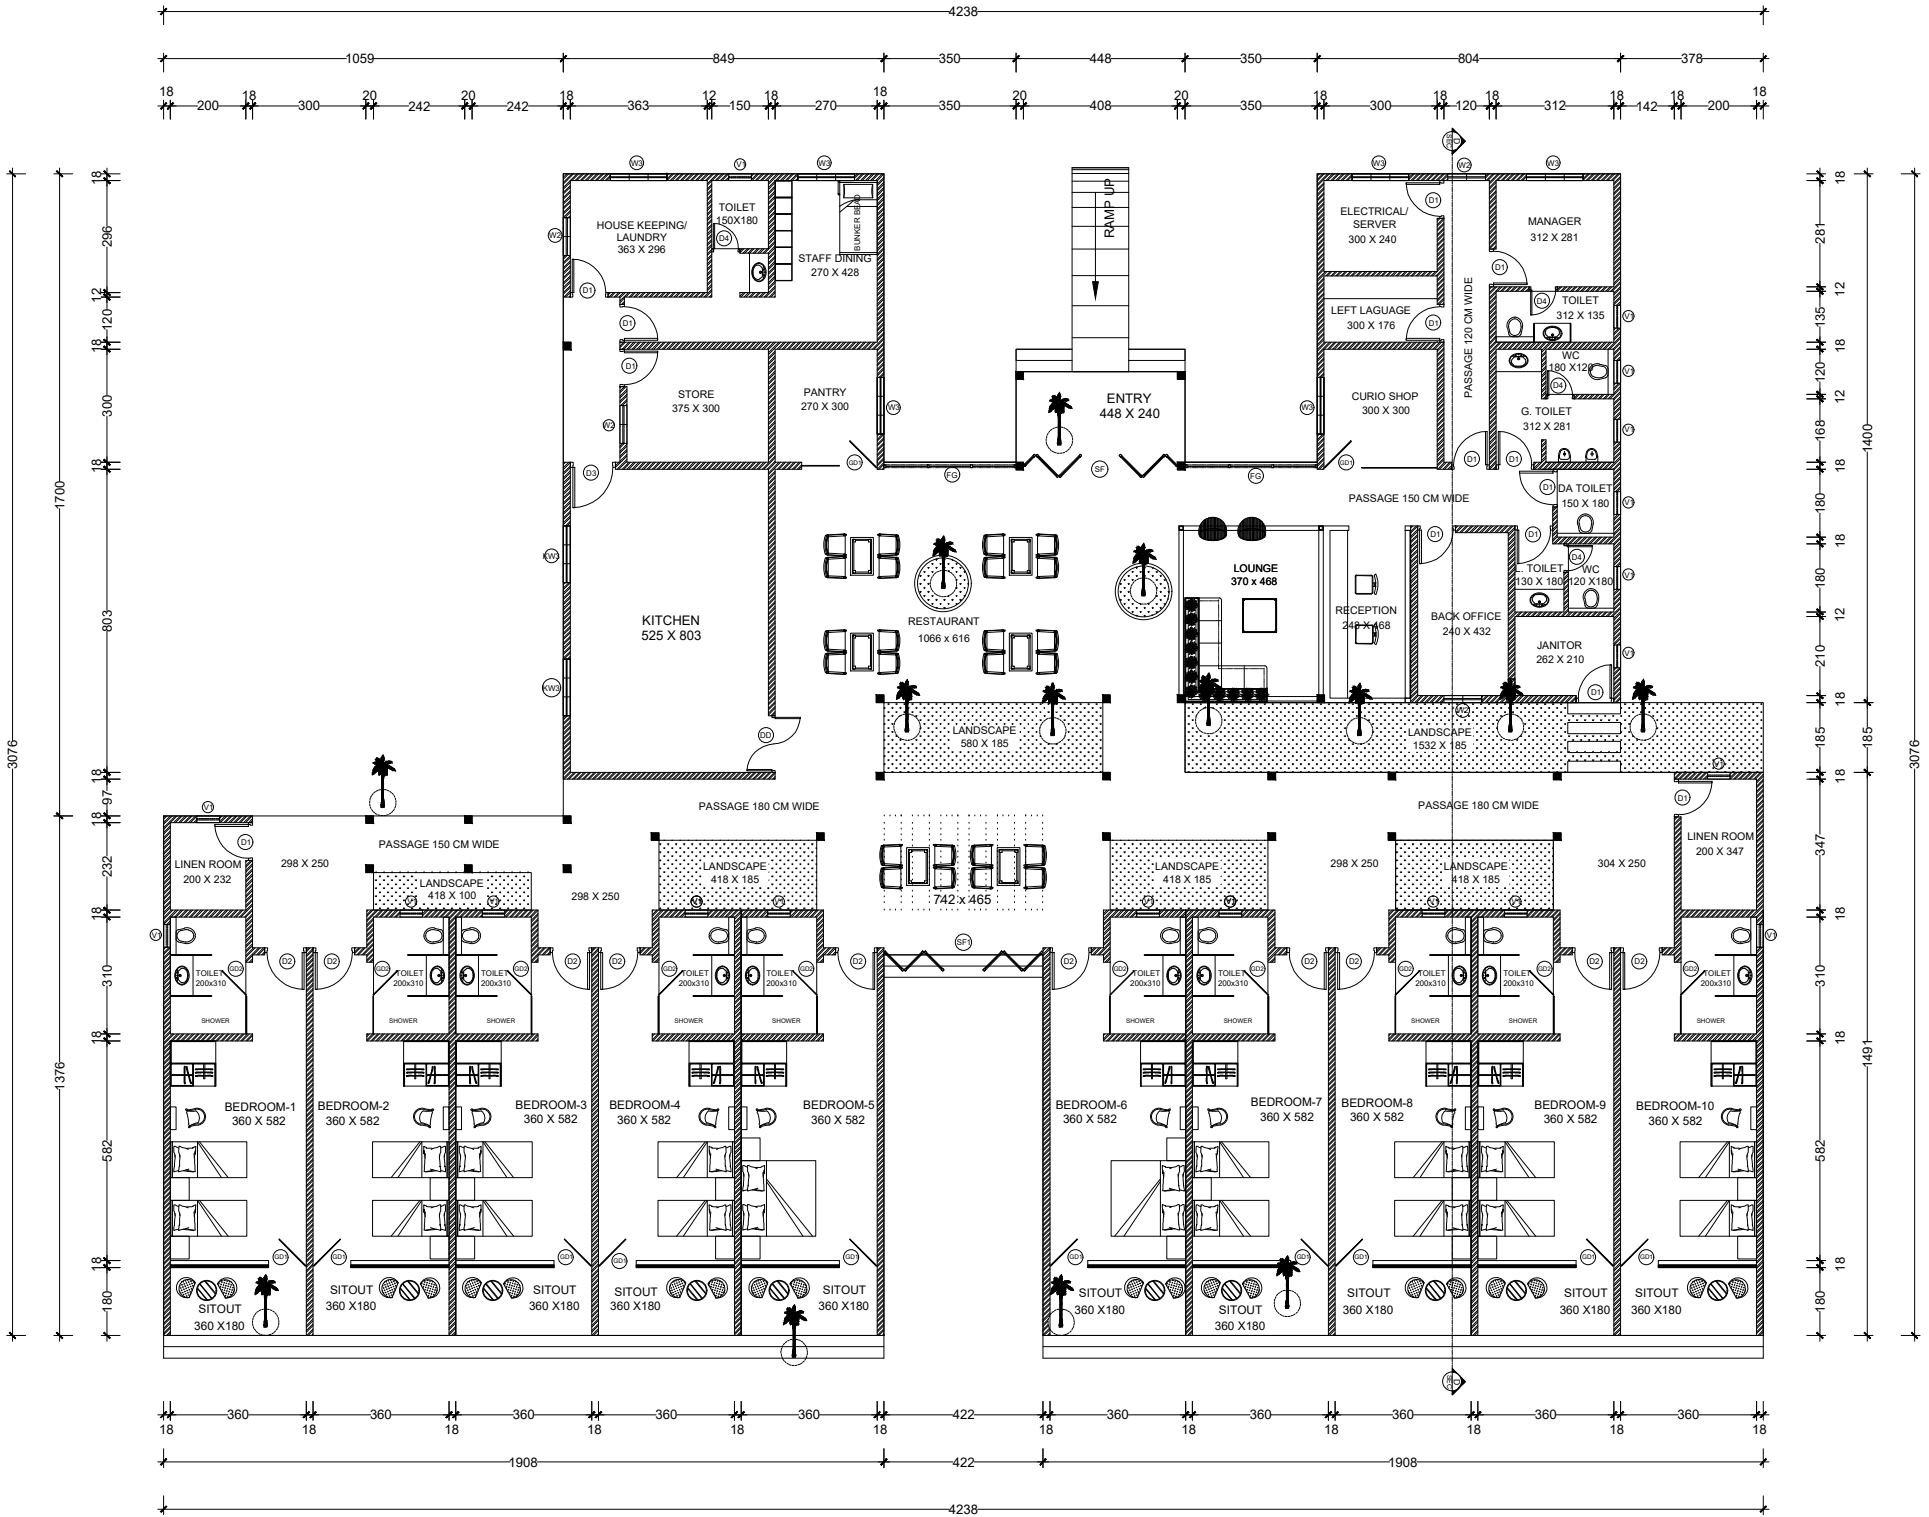

GROUND FLOOR PLAN


SCALE 1:100

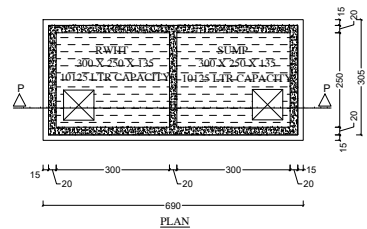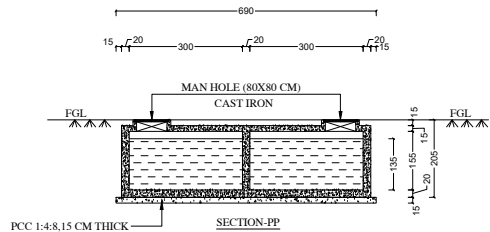

RWH TANK 20250 LITRES CAPACITY


DETAILS OF RAINWATER HARVESTING/ SUMP TANK

SCALE 1:100

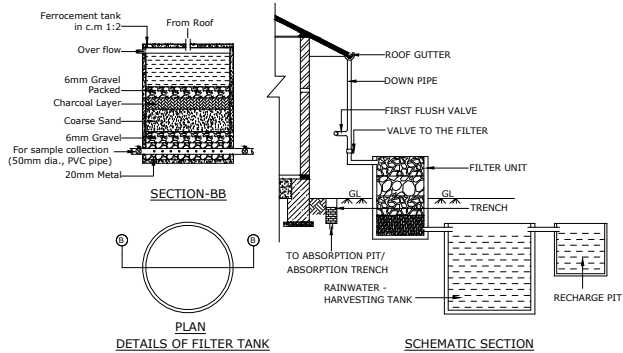

GROUND WATER RECHARGING ARRANGEMENT

SCALE: NTS

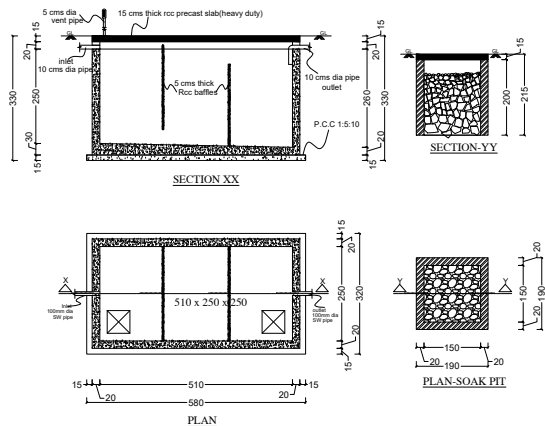

DETAILS OF SEPTIC TANK & SOAK PIT

SCALE 1:100

SPECIFICATIONS

- Foundation bed :- PCC 15CM thick
- Foundation :- RCC Footing & Plinth beam
- Superstructure :- RCC columns and beams with first calss brick masonry and throughout lintel above
- Flooring :- Tile&Granite finish
- Joinary works :- Glazed ,Aluminium&Wood
- Plastering :- 12mm thick CM 1:4
- Roofing :- Tile roof over steel frame, RCC Slab
- Stair case :- 12cm thick RCC slab with Rise :-15cm Tread :-30cm Stair width :-100cm
- Hand rail :- SS,MS&Wood hand rail120cm height
- Parepet wall :- 15cm thick masonry 120cm height
- Ventilation :- Mechanical(forced) / Natural
- Water Supply :- well & Public water supply
- Drainage :- To Public drain& Diverted to soak pit
- Access :- Road
- Sewage :- Disposed to STP& Septic tank

SCHEDULE OF OPENING

ITEM	SPECIFICATION	SIZE
D1	DOOR	100 X 240
D2	DOOR	110 X 240
D3	DOOR	120 X 240
D4	DOOR	75 X 240
GD1	GLASS DOOR	100 X 240
GD2	GLASS DOOR	90 X 240
RS	ROLLING SHUTTER	350 X 240
RS1	ROLLING SHUTTER	408 X 240
RS2	ROLLING SHUTTER	422 X 240
W3	WINDOW	150 X 150
W2	WINDOW	100 X 150
KW3	KITCHEN WINDOW	150 X 110
V1	VENTILATOR	60 X 60

LAND DETAILS

DISTRICT : LAKSHADWEEP
TALUK : AGATTI
VILLAGE : AGATTI
SURVEY NO : 1305/1 ,1305/2A ,1305/3A,1305/4A ,1305/6
EXTENT : 1050 + 1380 + 1180 + 1150 = 4760 M2 (47.60ARES)

AREA STATEMENT

FOR AREA STATEMENT REFER SHEET NO 3/3

ADDRESS & SIGNATURE OF LAND OWNER

- ALIKOYA KOODATHAPADA ,AGATTI
- KOYA ASHAKADA ,AGATTI
- BEEBI KADEEJA ASHAKADA ,AGATTI
- MARIYOMMABI ASHAKADA ,AGATTI
- KOYA UMMACHAMADA , AGATTI
- ALIKOYA UMMACHAMADA , AGATTI
- MOHAMMED KOYA UMMACHAMADA , AGATTI
- BEEFATHIMA UMMACHAMADA , AGATTI
- MUTHUKOYA THOOPIYAKAL , AGATTI

SIGNATURE OF ARCHITECT



ATHANAS

PROJECT :
PROPOSED TOURIST HOME AT AGATTI

DRG :
SANCTION DRAWING

DRAWING TITLE :
GROUND FLOOR PLAN, ELEVATION
SEPTIC TANK DETAIL, RWHT DETAIL

ALL DIMENSIONS IN CM	SHEET NO: 1/3
Date : 02/06/2020	
Scale: : 1:100	Drawn : JJ
Dwg.No: SD/TA-01	Checked : AP