



PROPOSED TOURIST HOME AT AGATTI

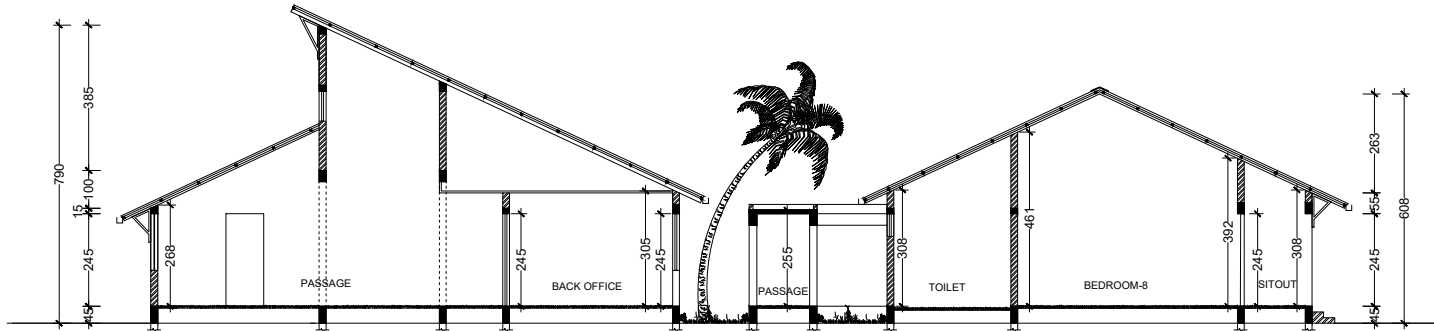


SECTION- AA
SCALE 1:100



ROOF PLAN
SCALE 1:100

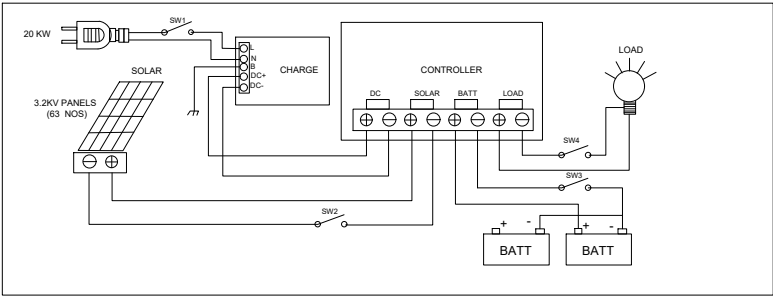

SOLAR ELECTIC POWER GENERATING SYSTEM
NTS

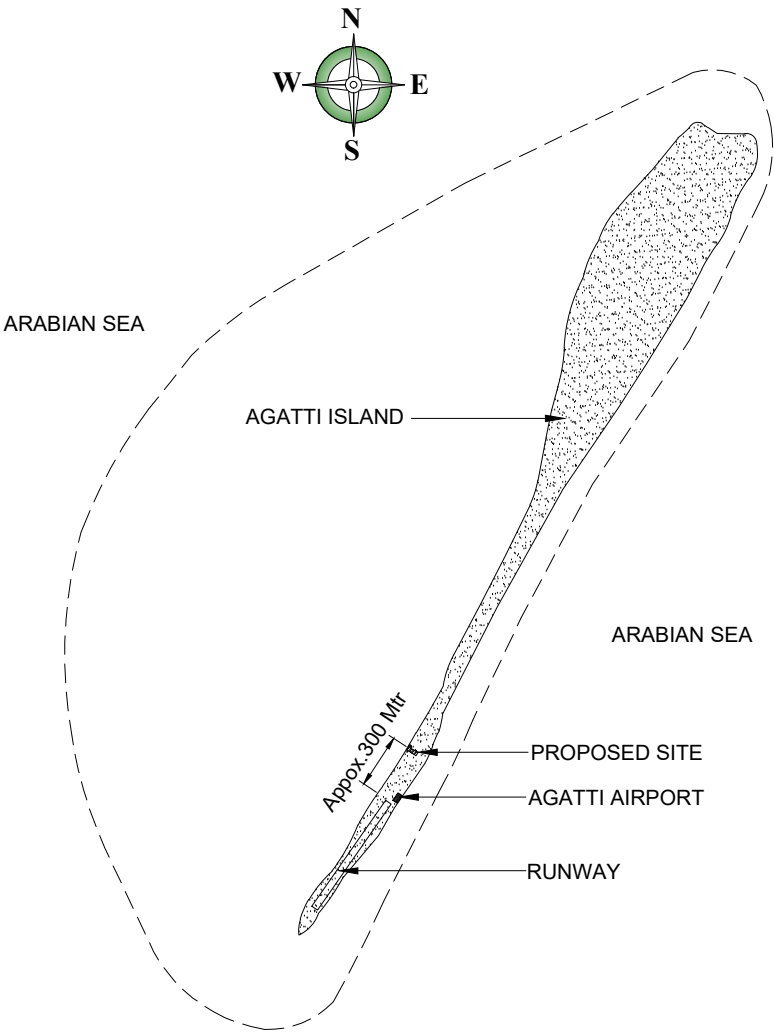

LOCATION PLAN
NTS

SPECIFICATIONS

- 1, Foundation bed :- PCC 15CM thick
- 2, Foundation :- RCC Footing & Plinth beam
- 3, Superstructure :- RCC columns and beams with first calss brick masonry and throughout lintel above
- 4, Flooring :- Tile&Granite finish
- 5, Joinary works :- Glazed ,Aluminium&Wood
- 6, Plastering :- 12mm thick CM 1:4
- 7, Roofing :- Tile roof over steel frame, RCC Slab
- 8, Stair case :- 12cm thick RCC slab with Rise :-15cm Tread :-30cm Stair width :-100cm
- 9, Hand rail :- SS,MS&Wood hand rail120cm height
- 10, Parepet wall :- 15cm thick masonry 120cm height
- 11, Ventilation :- Mechanical(forced) / Natural
- 12, Water Supply :- well & Public water supply
- 13, Drainage :- To Public drain& Diverted to soak pit
- 14, Access :- Road
- 15, Sewage :- Disposed to STP& Septic tank

SCHEDULE OF OPENING

ITEM	SPECIFICATION	SIZE
D1	DOOR	100 X 240
D2	DOOR	110 X 240
D3	DOOR	120 X 240
D4	DOOR	75 X 240
GD1	GLASS DOOR	100 X 240
GD2	GLASS DOOR	90 X 240
RS	ROLLING SHUTTER	350 X 240
RS1	ROLLING SHUTTER	408 X 240
RS2	ROLLING SHUTTER	422 X 240
W3	WINDOW	150 X 150
W2	WINDOW	100 X 150
KW3	KITCHEN WINDOW	150 X 110
V1	VENTILATOR	60 X 60

LAND DETAILS

DISTRICT : LAKSHADWEEP
TALUK : AGATTI
VILLAGE : AGATTI
SURVEY NO : 1305/1 ,1305/2A ,1305/3A,1305/4A ,1305/6
EXTENT : 1050 + 1380 + 1180 + 1150 = 4760 M2 (47.60ARES)

AREA STATEMENT

FOR AREA STATEMENT REFER SHEET NO 3/3

ADDRESS & SIGNATURE OF LAND OWNER

- 1, ALIKOYA KOODATHAPADA ,AGATTI
- 2, KOYA ASHAKADA ,AGATTI
- 3, BEEBI KADEEJA ASHAKADA ,AGATTI
- 4, MARIYOMMABI ASHAKADA ,AGATTI
- 5, KOYA UMMACHAMADA , AGATTI
- 6, ALIKOYA UMMACHAMADA , AGATTI
- 7, MOHAMMED KOYA UMMACHAMADA , AGATTI
- 8, BEEFATHIMA UMMACHAMADA , AGATTI
- 9, MUTHUKOYA THOOPIYAKAL , AGATTI

SIGNATURE OF ARCHITECT



AHANAS

PROJECT :
PROPOSED TOURIST HOME AT AGATTI

DRG :
SANCTION DRAWING

DRAWING TITLE :
ROOF PLAN, LOCATION PLAN, SECTION,
SOLAR SYSTEM DETAIL

ALL DIMENSIONS IN CM	SHEET NO: 2/3
Date : 02/06/2020	Drawn : JJ
Scale: : 1:100	Checked : AP
Dwg.No: SD/VSA-01	