



PROPOSED TOURIST HOME AT AGATTI

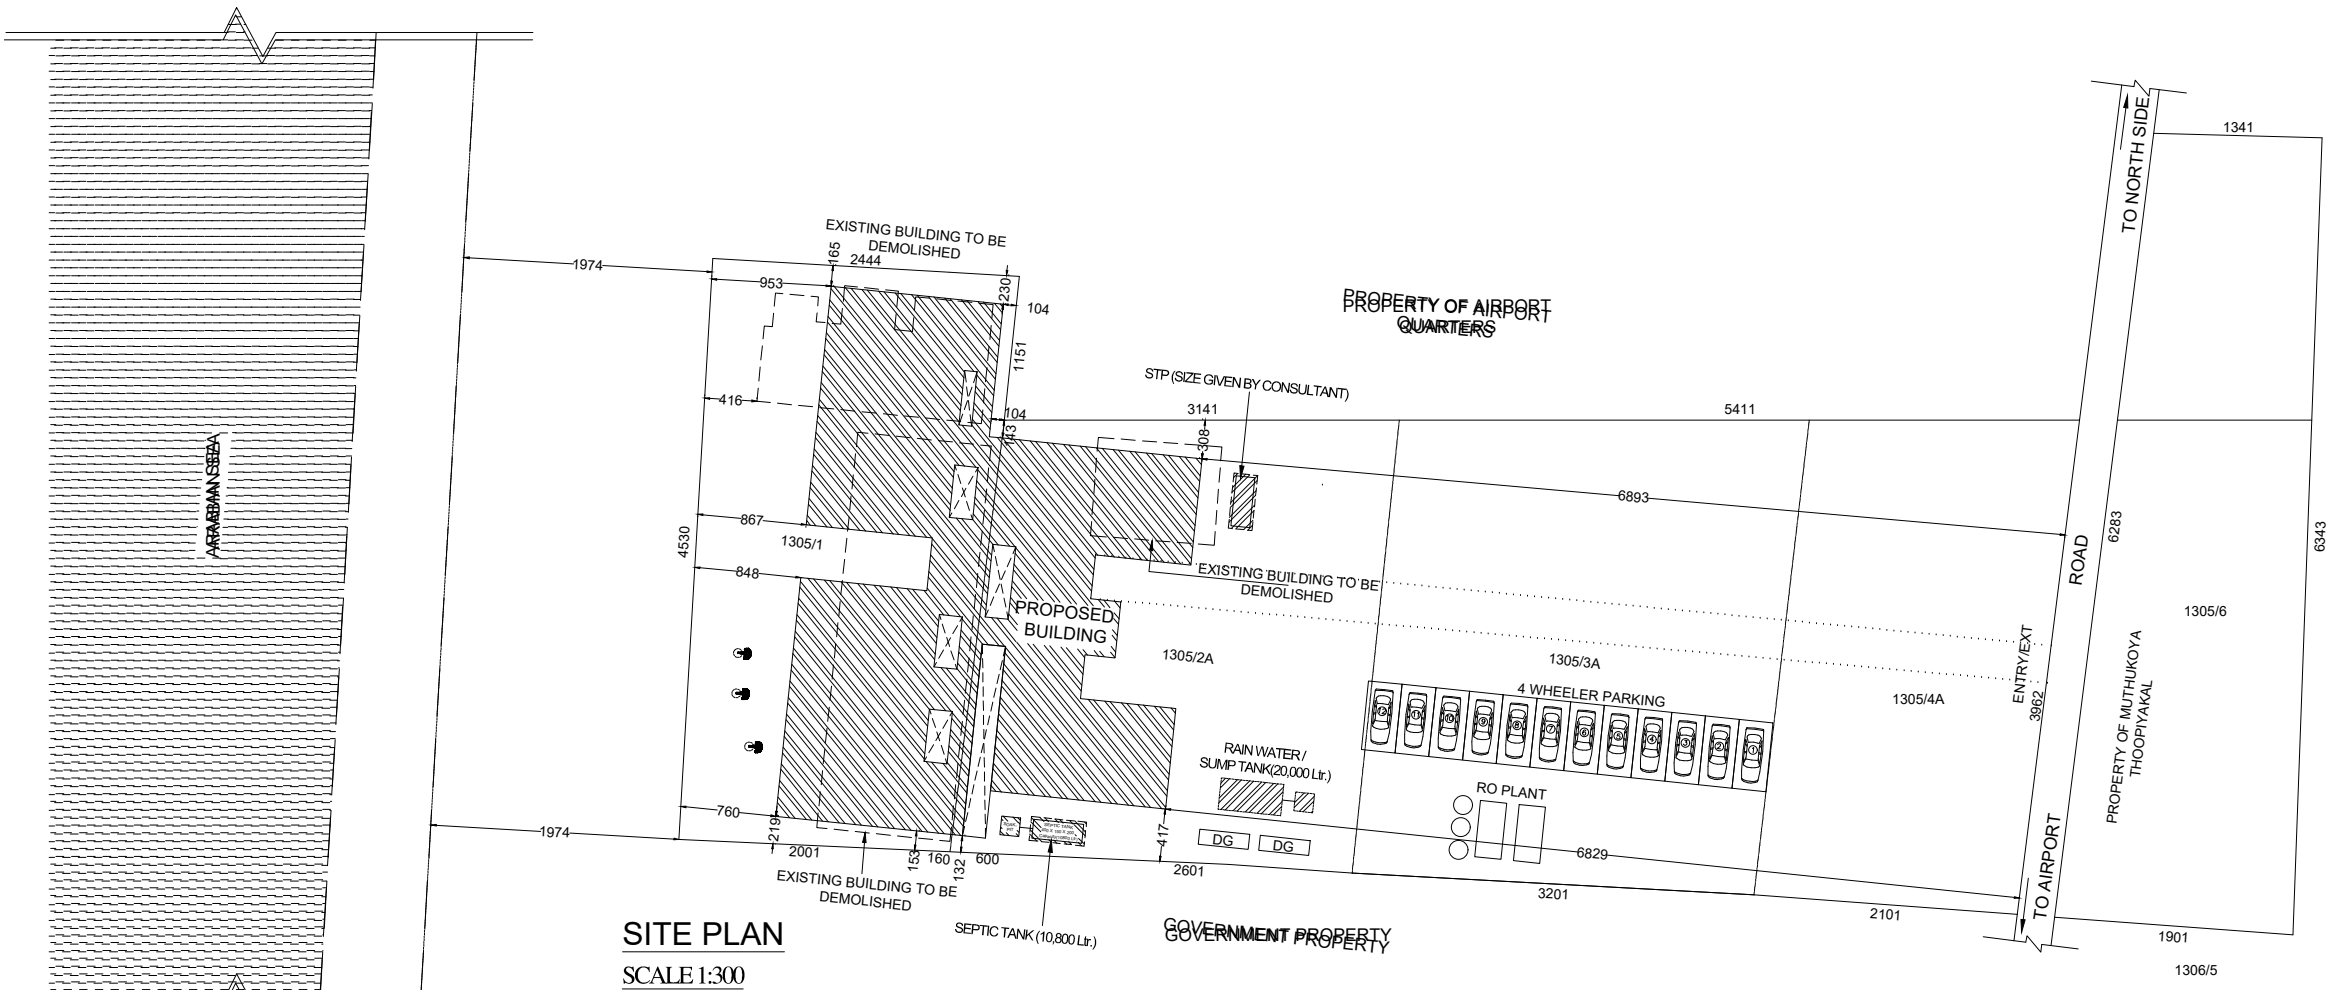

SITE PLAN
SCALE 1:300

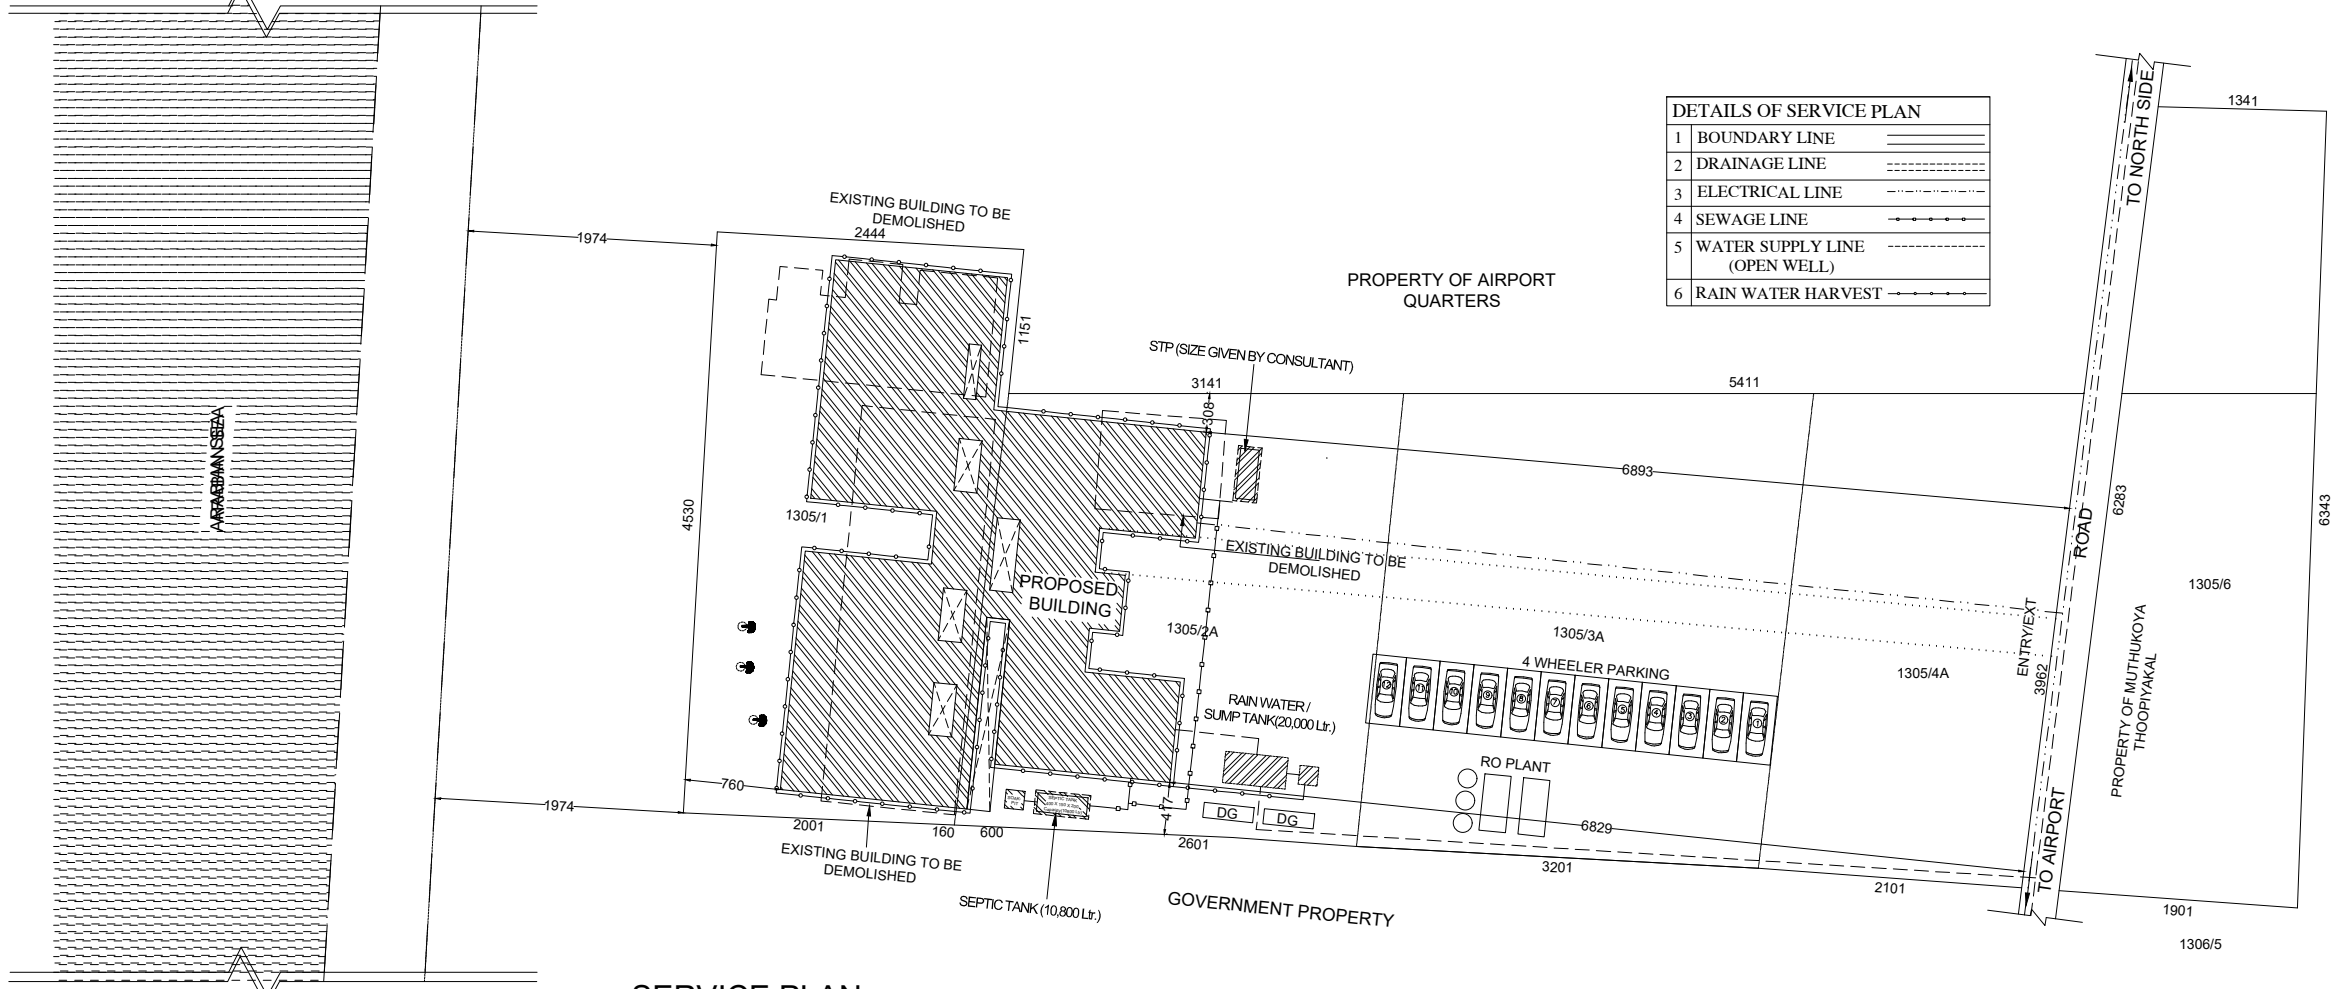

SERVICE PLAN
SCALE 1:1300

SPECIFICATIONS

- Foundation bed :- PCC 15CM thick
- Foundation :- RCC Footing & Plinth beam
- Superstructure :- RCC columns and beams with first calss brick masonry and throughout lintel above
- Flooring :- Tile&Granite finish
- Joinary works :- Glazed ,Aluminium&Wood
- Plastering :- 12mm thick CM 1:4
- Roofing :- Tile roof over steel frame, RCC Slab
- Stair case :- 12cm thick RCC slab with Rise :-15cm Tread :-30cm Stair width :-100cm
- Hand rail :- SS,MS&Wood hand rail120cm height
- Parepet wall :- 15cm thick masonry 120cm height
- Ventilation :- Mechanical(forced) / Natural
- Water Supply :- well & Public water supply
- Drainage :- To Public drain& Diverted to soak pit
- Access :- Road
- Sewage :- Disposed to STP& Septic tank

LAND DETAILS

DISTRICT : LAKSHADWEEP
TALUK : AGATTI
VILLAGE : AGATTI
SURVEY NO : 1305/1 ,1305/2A ,1305/3A,1305/4A ,1305/6
EXTENT : 1050 + 1380 + 1180 + 1150 = 4760 M2 (47.60ARES)

AREA STATEMENT

No.	FLOORS	Plinth area (M2)	Area for F.A.R(M2)	Carpet area (M2)
1.	GROUND FLOOR	883.18	883.18	706.54

F.A.R - 0.185
COVERAGE - 18.5 %
SITE AREA - 4760 M2
TOTAL BUILT UP AREA - 883.18 SQM

ADDRESS & SIGNATURE OF LAND OWNER

- ALIKOYA KOODATHAPADA ,AGATTI
- KOYA ASHAKADA ,AGATTI
- BEEBI KADEEJA ASHAKADA ,AGATTI
- MARIYOMMABI ASHAKADA ,AGATTI
- KOYA UMMACHAMADA , AGATTI
- ALIKOYA UMMACHAMADA , AGATTI
- MOHAMMED KOYA UMMACHAMADA , AGATTI
- BEEFATHIMA UMMACHAMADA , AGATTI
- MUTHUKOYA THOOPIYAKAL , AGATTI

SIGNATURE OF ARCHITECT



ATHANAS

PROJECT :
PROPOSED TOURIST HOME AT AGATTI

DRG :
SANCTION DRAWING

DRAWING TITLE :
SITE & SERVICE PLAN

ALL DIMENSIONS IN CM	SHEET NO: 3/3
Date : 02/06/2020	
Scale : 1:100, 1:300	Drawn : JJ
Dwg.No: SD/VSA-01	Checked : AP