


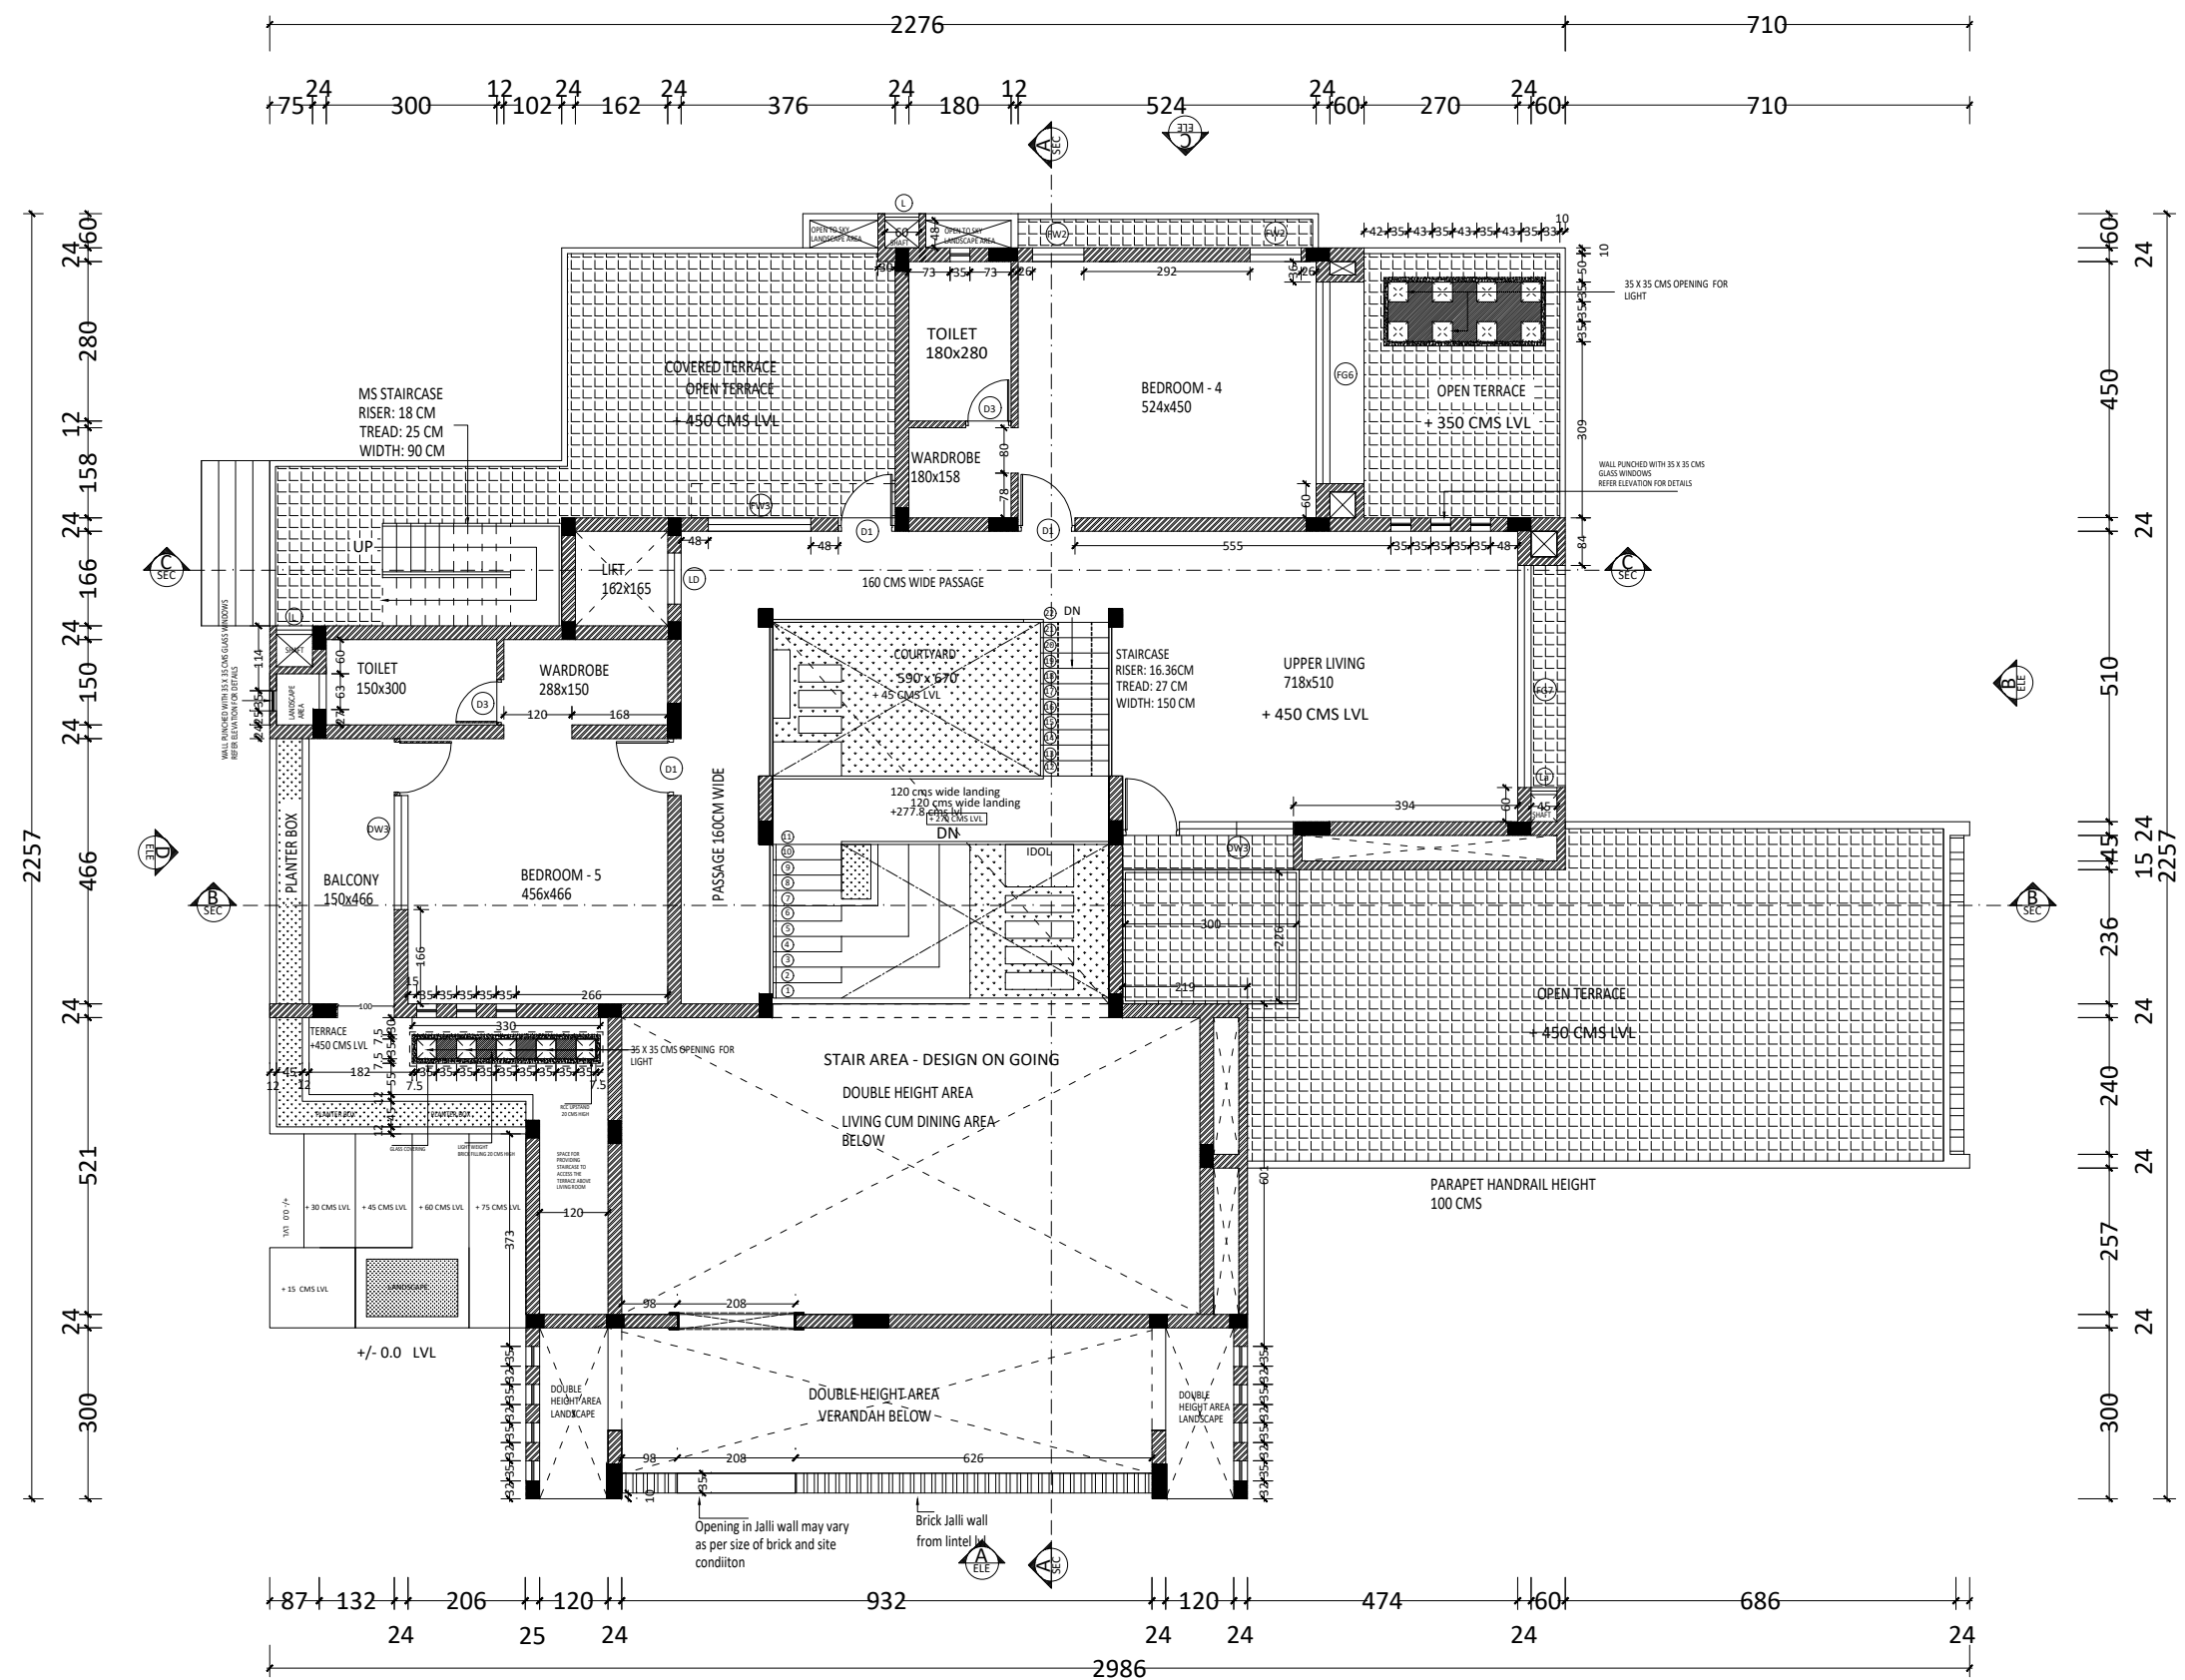

FIRST FLOOR

SCHEDULE OF OPENING
NOTE: LINTEL HEIGHT = 245 CM
OPENING MEASUREMENT IS CLEAR OPENING AFTER FFL AND PLASTERING

DD	DOUBLE LEAF DOOR	120 X 240
D1	DOOR	100 X 240
D2	DOOR	90 X 240
D3	DOOR	80 X 240
DW1	DOOR AND WINDOW	354 X 240
DW2	DOOR AND WINDOW	260 X 240
DW3	DOOR AND WINDOW	300 X 240
FG1	FIXED GLASS WINDOW	403 X 240
FG2	FIXED GLASS WINDOW	277 X 240
FG3	FIXED GLASS WINDOW	209 X 240
FG4	FIXED GLASS WINDOW	414 X 240
FG5	FIXED GLASS WINDOW	245 X 240
FG6	FIXED GLASS WINDOW	354 X 240
FG7	FIXED GLASS WINDOW	390 X 240
FW2	WINDOW	90 X 240
FW3	WINDOW	180 X 240
FW4	WINDOW	240 X 240
FW5	WINDOW	245 X 240
KW	KITCHEN LINEAR WINDOW	356 X 120
GRILL	GRILL OPENING	414 X 120
L	LOUVERED OPENING	60 X h
La	LOUVERED OPENING	45 X h
LD	LIFT DOOR	As per lift manufacturer

DATE: 03.05.2021

SCALE : NA

DRAWN: AP

CHECKED: ANEENA

PROJECT NO:496

PROJECT: RESIDENTIAL PROJECT AT RAMESHWARAM

CLIENT: MIJULAL AND RADHIKA

DRAWING TITLE:
FIRST FLOOR PLAN - BRICK WORK

REVISION:26.08.2022

R1 Changes as per Interiors



NOTES:

- ALL DIMENSIONS ARE IN CMS, UNLESS OTHERWISE SPECIFIED
- DIMENSIONS SHALL NOT BE MEASURED DIRECTLY FROM THIS DRAWINGS.
- FOLLOW ONLY WRITTEN DIMENSIONS
- IN THE EVENT OF ANY DISCREPANCY OR DIFFERENCE BETWEEN ANY DRAWINGS OR SITE CONDITIONS OR OTHERWISE IMMEDIATE REFERENCE IS TO BE MADE TO THE DESIGNER FOR CLARIFICATION PRIOR TO EXECUTION
- OF WORK AT SITE
- ALL THE CIVIL WORKS SHOULD BE IN LINE LEVEL AND PLUMB.
- PLASTERING TO BE CUT AT SKIRTING LEVEL.