



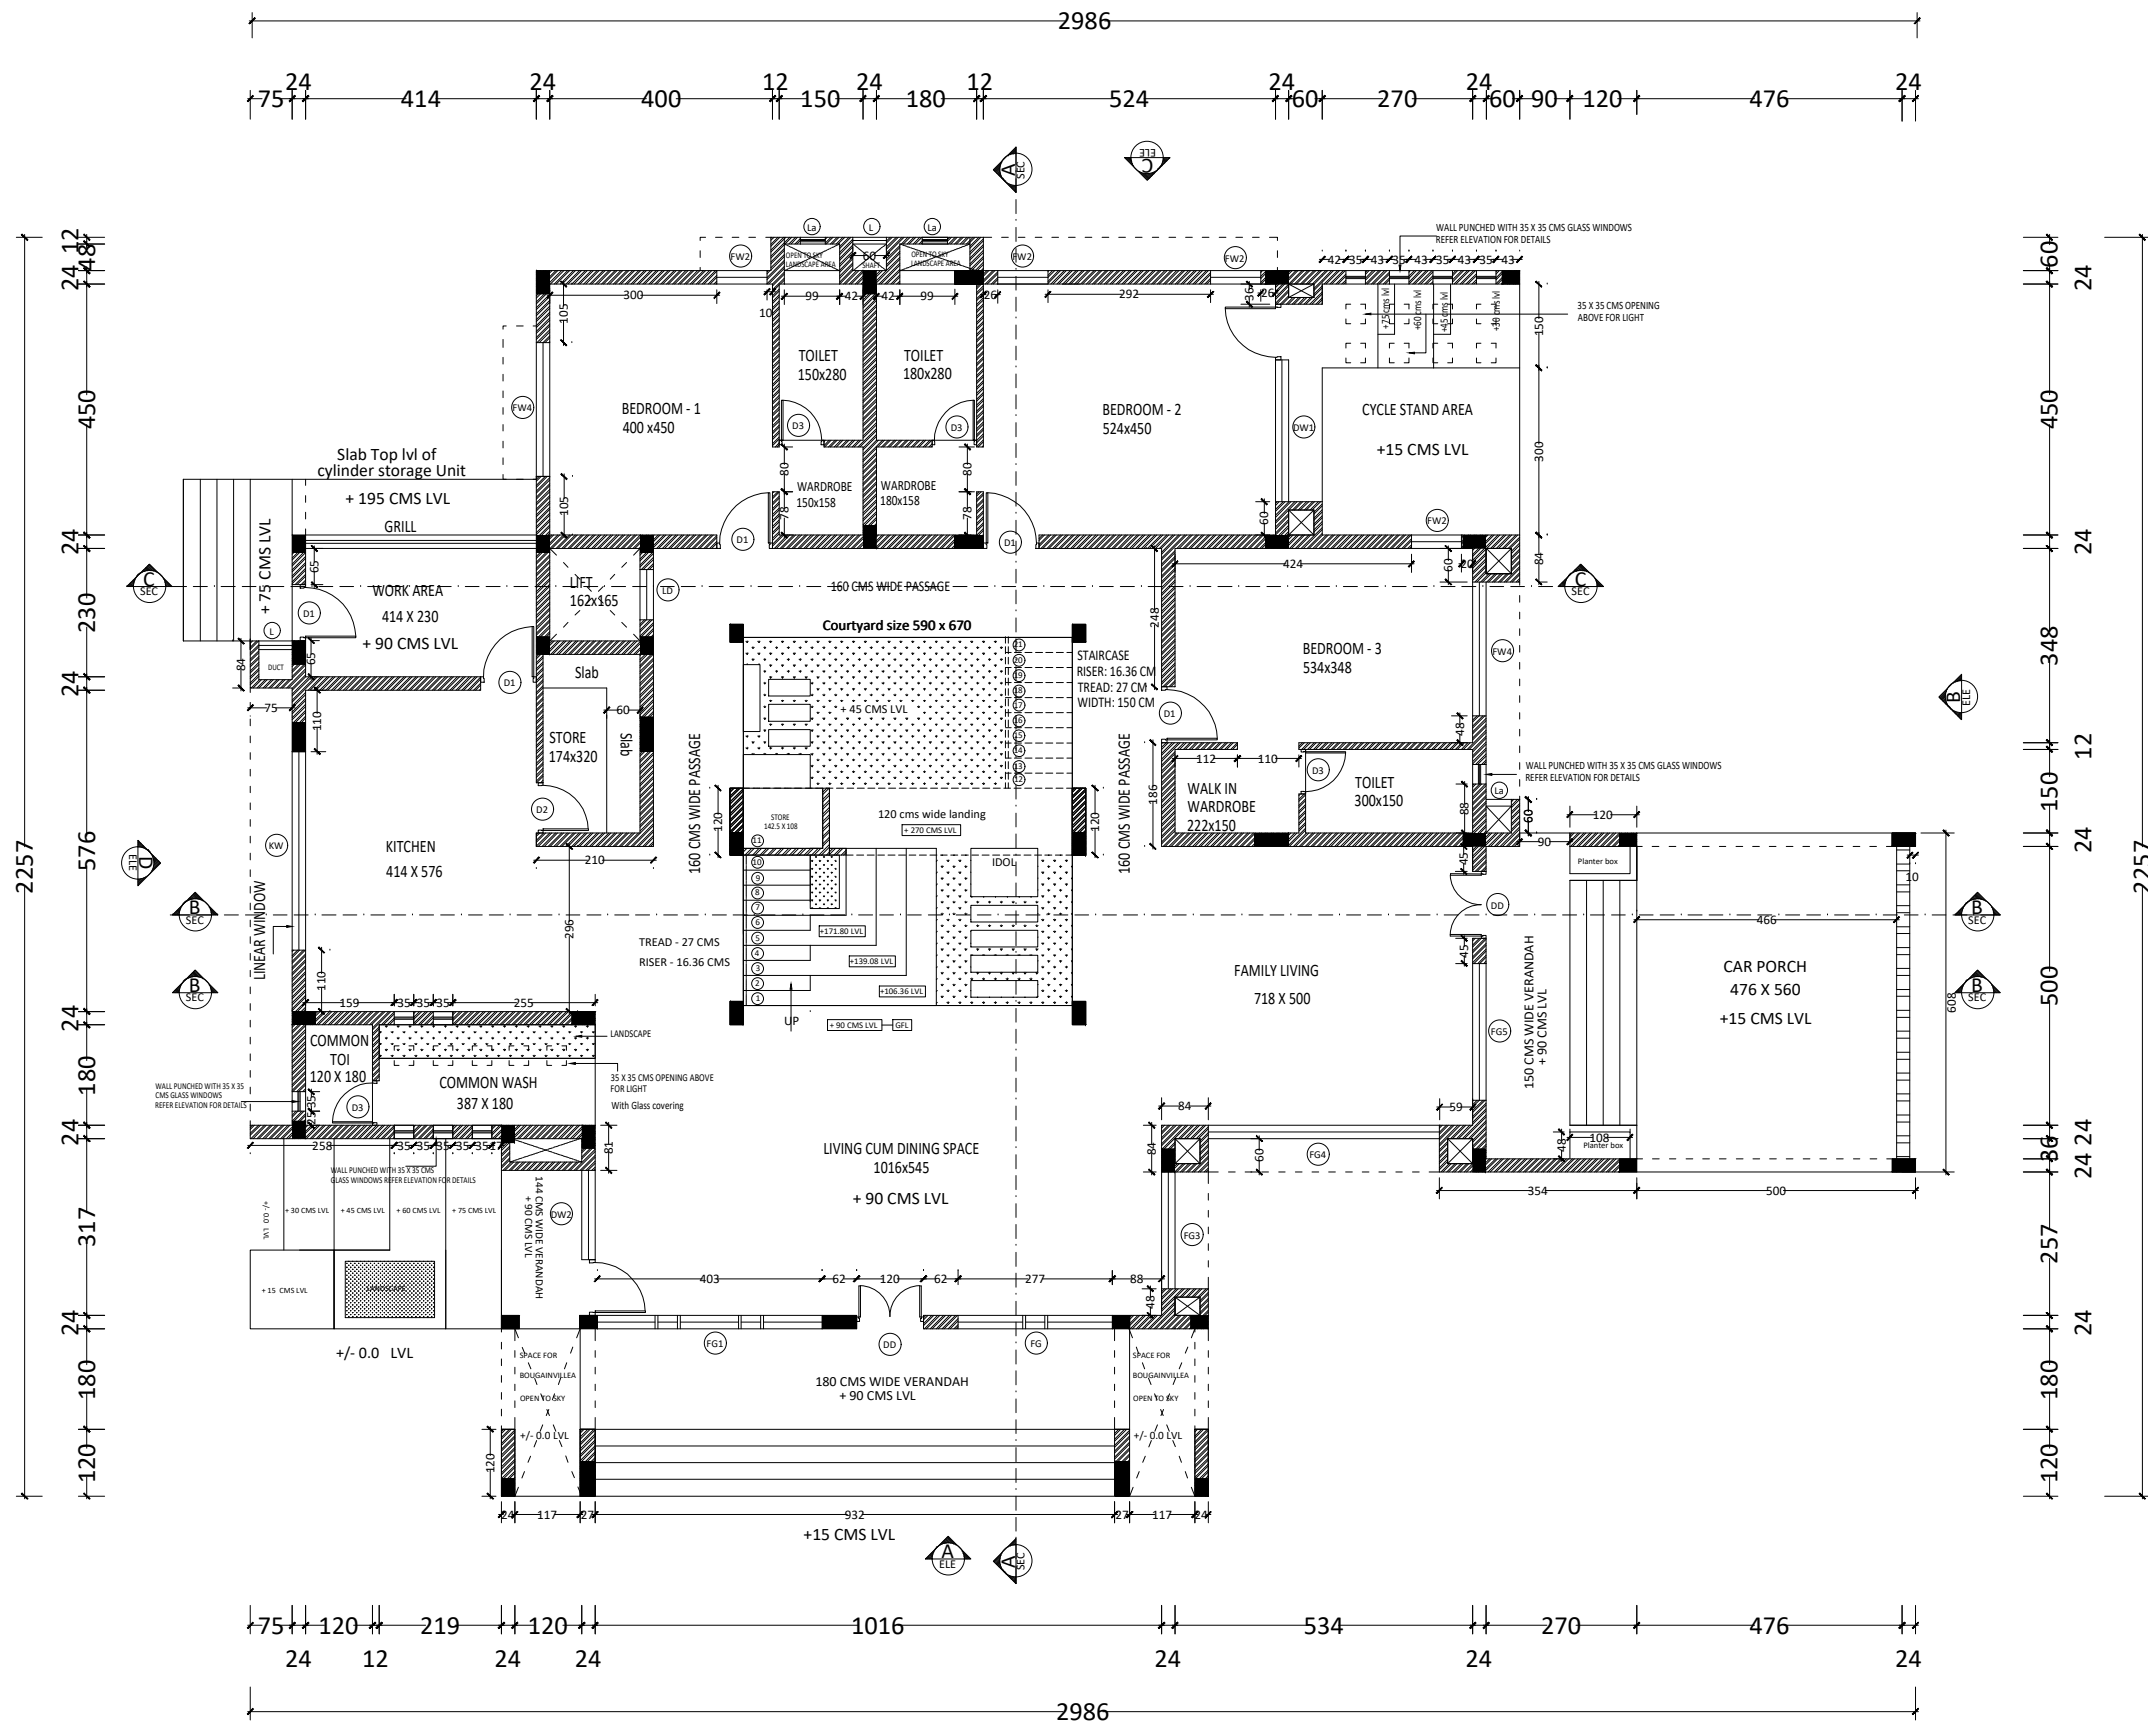

GROUND FLOOR

SCHEDULE OF OPENING		
NOTE: LINTEL HEIGHT = 245 CM		
OPENING MEASUREMENT IS CLEAR OPENING AFTER FFL AND PLASTERING		
DD	DOUBLE LEAF DOOR	120 X 240
D1	DOOR	100 X 240
D2	DOOR	90 X 240
D3	DOOR	80 X 240
DW1	DOOR AND WINDOW	354 X 240
DW2	DOOR AND WINDOW	260 X 240
DW3	DOOR AND WINDOW	300 X 240
FG1	FIXED GLASS WINDOW	403 X 240
FG2	FIXED GLASS WINDOW	277 X 240
FG3	FIXED GLASS WINDOW	209 X 240
FG4	FIXED GLASS WINDOW	414 X 240
FG5	FIXED GLASS WINDOW	245 X 240
FG6	FIXED GLASS WINDOW	354 X 240
FG7	FIXED GLASS WINDOW	390 X 240
FW2	WINDOW	90 X 240
FW3	WINDOW	180 X 240
FW4	WINDOW	240 X 240
FW5	WINDOW	245 X 240
KW	KITCHEN LINEAR WINDOW	356 X 120
GRILL	GRILL OPENING	414 X 120
L	LOUVERED OPENING	60 X h
La	LOUVERED OPENING	45 X h
LD	LIFT DOOR	As per lift manufacturer

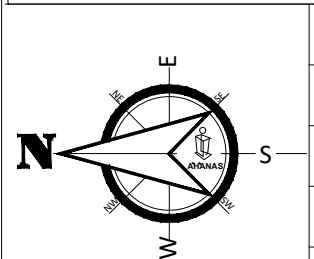

DATE: 03.05.2021

SCALE : NA

DRAWN: AP

CHECKED: ANEENA

PROJECT NO:496

PROJECT: RESIDENTIAL PROJECT AT
RAMESHWARAM

CLIENT: MIJULAL AND RADHIKA

DRAWING TITLE:
GROUND FLOOR PLAN BRICK WORK

REVISION:20.09.2022

R1	Changes as per Interiors
R2	Changes as per Interiors in Courtyard



NOTES:

- ALL DIMENSIONS ARE IN CMS, UNLESS OTHERWISE SPECIFIED
- DIMENSIONS SHALL NOT BE MEASURED DIRECTLY FROM THIS DRAWINGS.
- FOLLOW ONLY WRITTEN DIMENSIONS
- IN THE EVENT OF ANY DISCREPANCY OR DIFFERENCE BETWEEN ANY DRAWINGS OR SITE CONDITIONS OR OTHERWISE IMMEDIATE REFERENCE IS TO BE MADE TO THE DESIGNER FOR CLARIFICATION PRIOR TO EXECUTION OF WORK AT SITE
- ALL THE CIVIL WORKS SHOULD BE IN LINE LEVEL AND PLUMB.
- PLASTERING TO BE CUT AT SKIRTING LEVEL.