




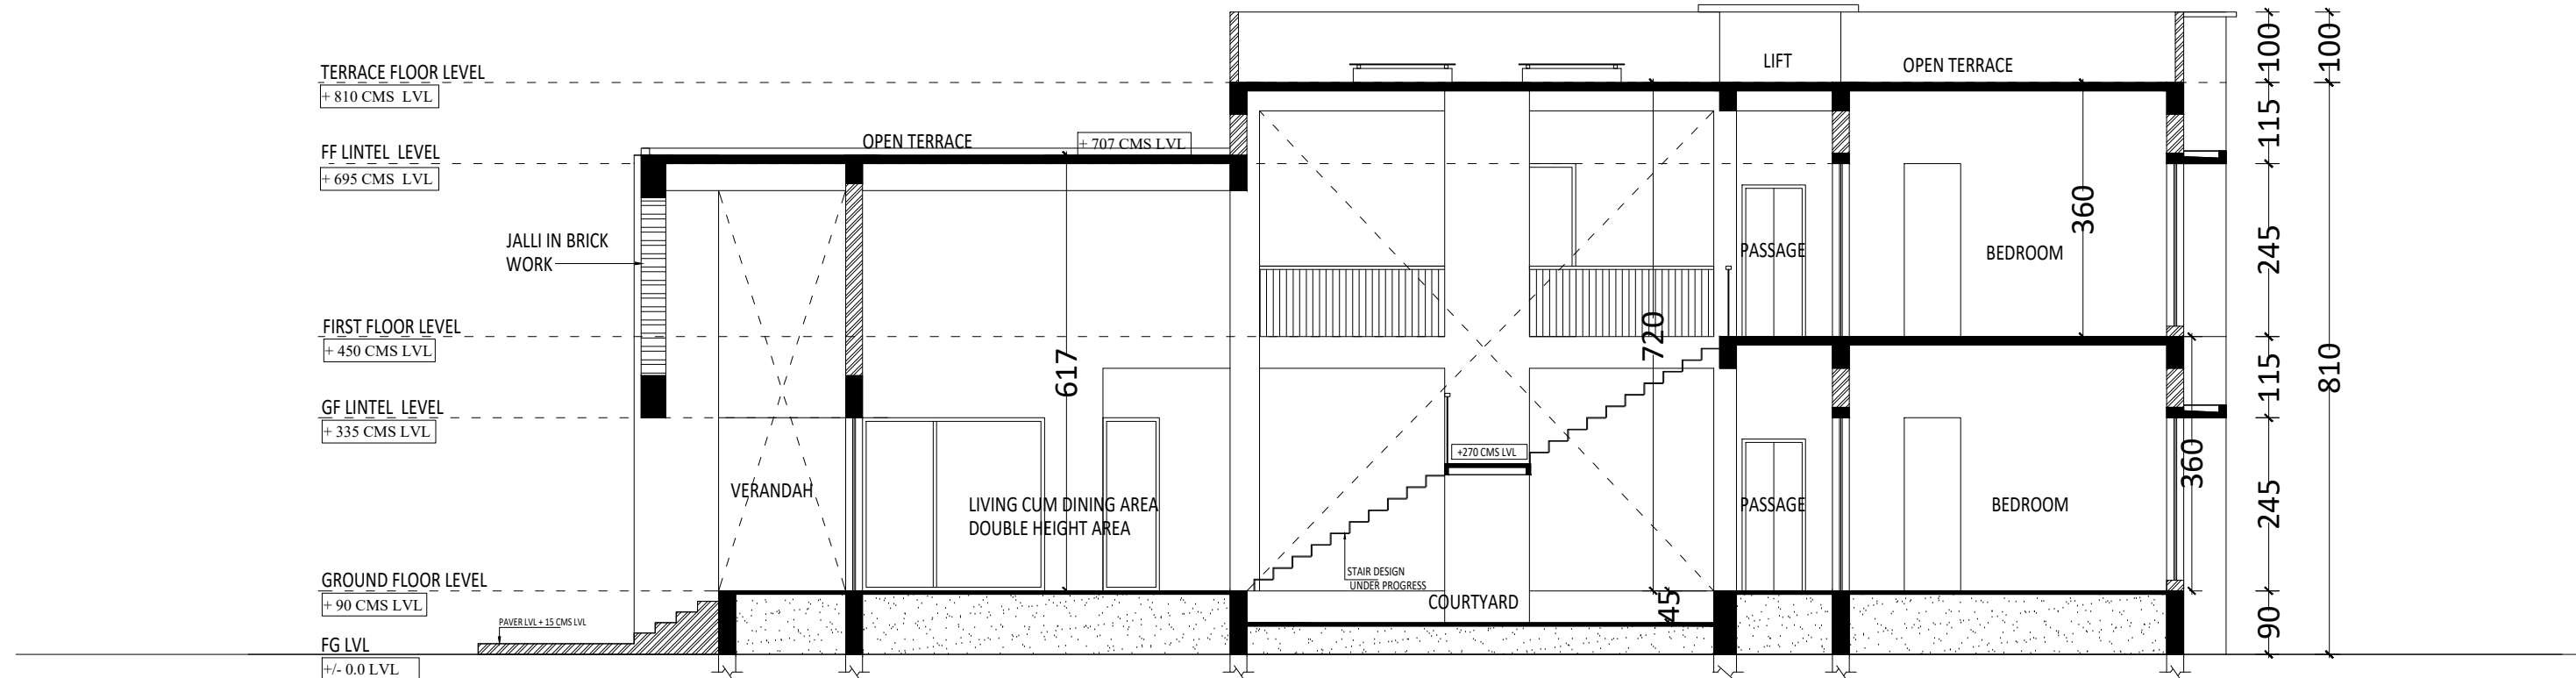

SECTION A-A

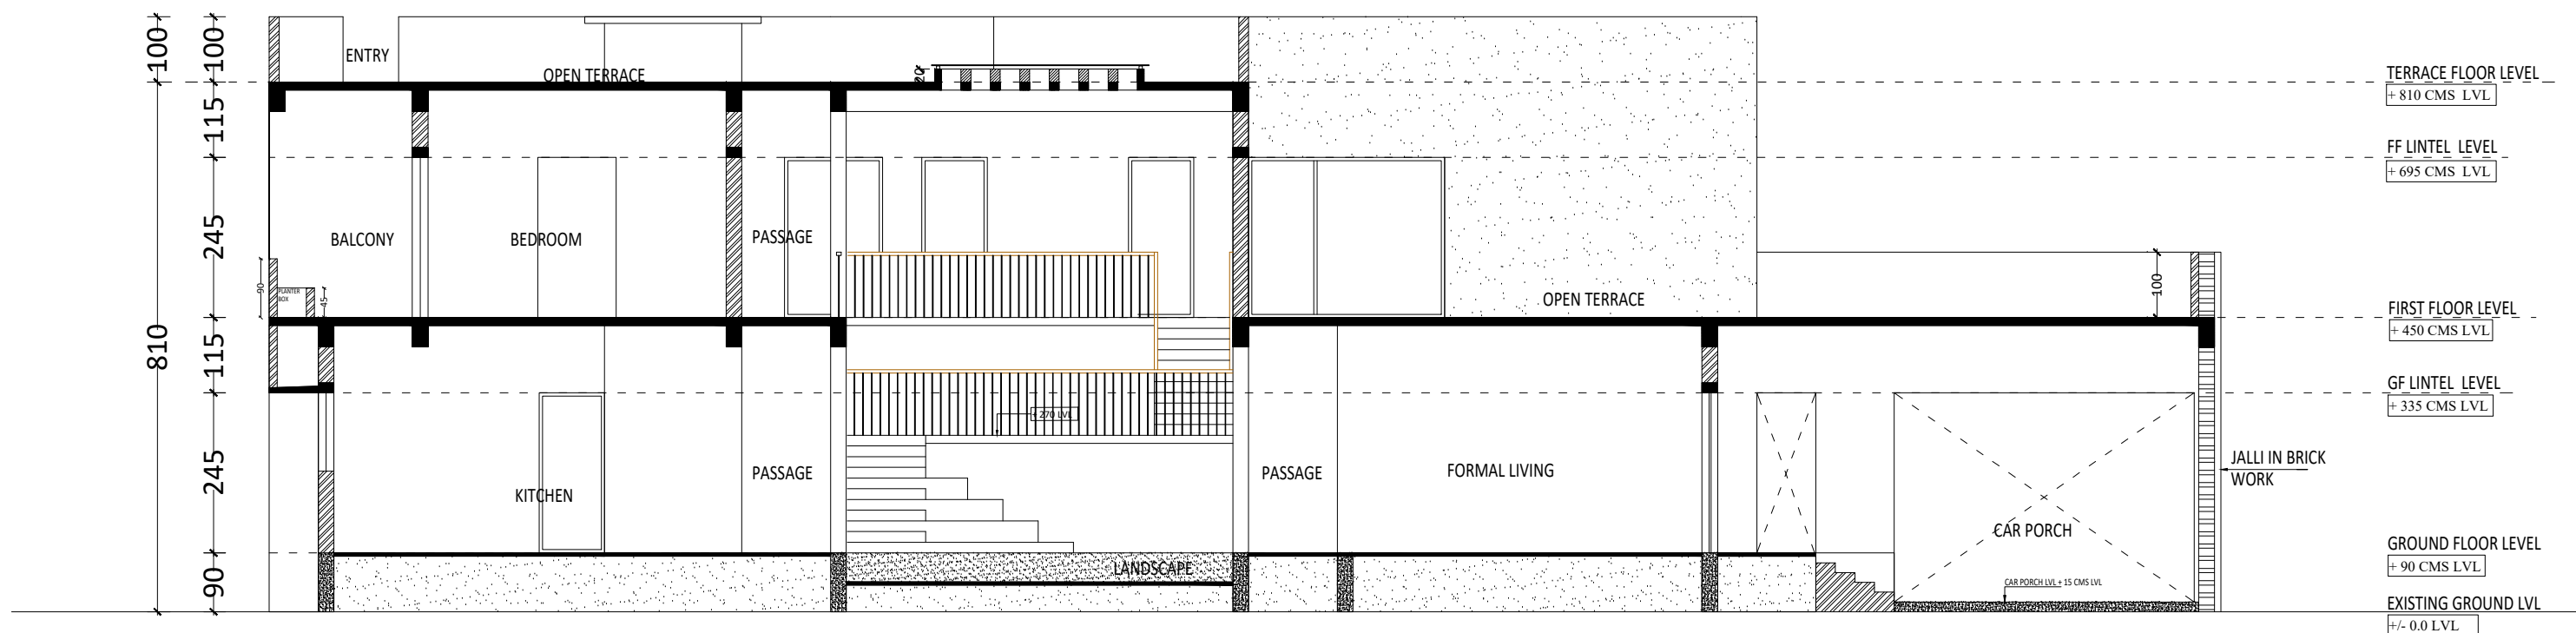

SECTION B-B

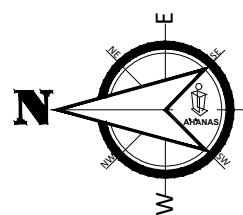

DATE: 03.05.2021

SCALE : NA

DRAWN: AP

CHECKED: ANEENA

PROJECT NO:496

PROJECT: RESIDENTIAL PROJECT AT
RAMESHWARAM

CLIENT: MIJULAL AND RADHIKA

DRAWING TITLE:
SECTION A-A, B-B

REVISION:10.04.2023

R1	Changes as per Interiors
R2	Height of planter box added



NOTES:

- ALL DIMENSIONS ARE IN CMS, UNLESS OTHERWISE SPECIFIED
- DIMENSIONS SHALL NOT BE MEASURED DIRECTLY FROM THIS DRAWINGS.
- FOLLOW ONLY WRITTEN DIMENSIONS
- IN THE EVENT OF ANY DISCREPANCY OR DIFFERENCE BETWEEN ANY DRAWINGS OR SITE CONDITIONS OR OTHERWISE IMMEDIATE REFERENCE IS TO BE MADE TO THE DESIGNER FOR CLARIFICATION PRIOR TO EXECUTION
- OF WORK AT SITE
- ALL THE CIVIL WORKS SHOULD BE IN LINE LEVEL AND PLUMB.
- PLASTERING TO BE CUT AT SKIRTING LEVEL.