


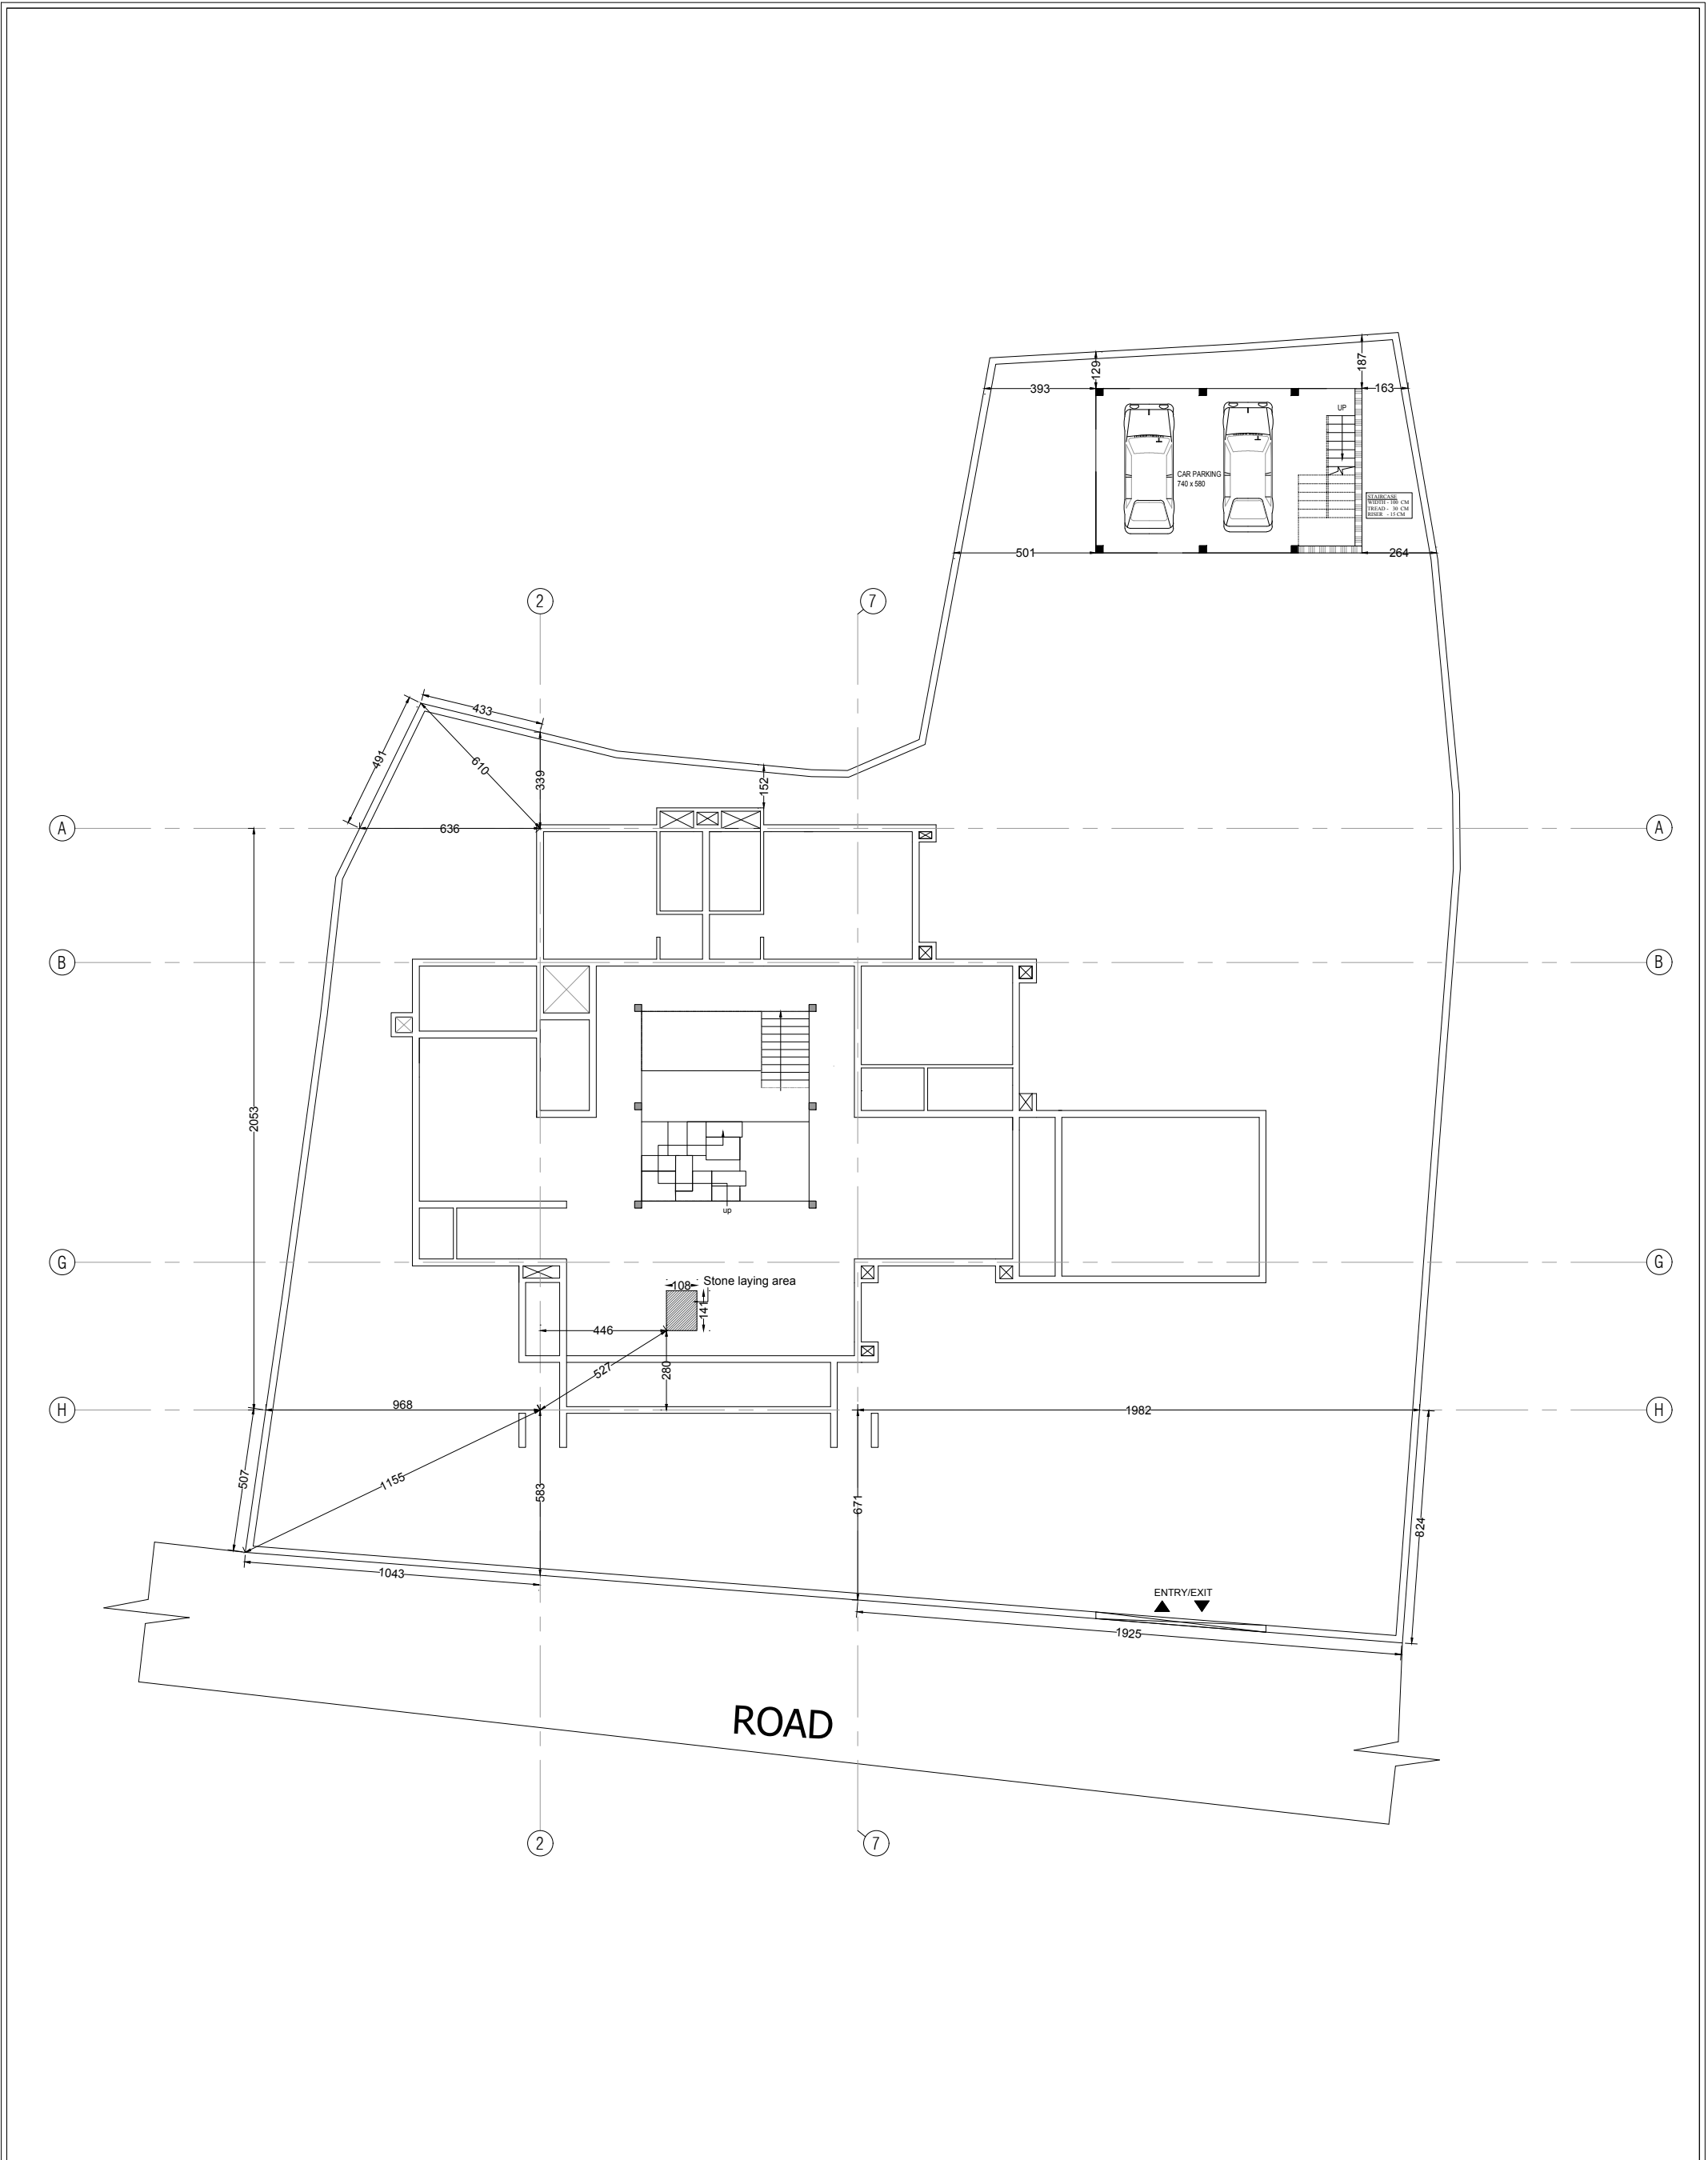

|                                                                        |                  |                                            |           |  |                                          |   |
|------------------------------------------------------------------------|------------------|--------------------------------------------|-----------|--|------------------------------------------|---|
| <div><div></div><div>E</div><div>N</div><div>W</div><div>S</div></div> | DATE: 06/03/2021 | CLIENT:<br>MR. MIJULAL AND<br>MRS. RADHIKA | REVISION: |  | <div><div></div></div> <div>AHANAS</div> | ALL DIMENSIONS ARE IN CMS<br><br>NO DIMENSIONS TO BE SCALED OFF FROM<br>DRAWINGS ONLY WRITTEN DIMENSIONS TO BE<br><br>IN THE EVENT OF ANY DISCREPANCY OR<br>DIFFERENCE BETWEEN ANY INTERIOR DRAWINGS<br>OR SITE CONDITIONS OR OTHERWISE IMMEDIATE<br>REFERENCE IS TO BE MADE TO THE DESIGNER<br>FOR CLARIFICATION PRIOR TO EXECUTION OF<br>WORK AT SITE |
|                                                                        | SCALE :NTS       |                                            |           |  |                                          |   |
|                                                                        | DRAWN: AYESHA    | PROJECT:<br>RESIDENCE AT THOPUMPADY        |           |  |                                          |   |
|                                                                        | CHECKED:AP       |                                            |           |  |                                          |   |
|                                                                        | PROJECT NO: 496  | DRAWING TITLE:<br>SET OUT DRAWING          |           |  |                                          |   |
|                                                                        |                  |                                            |           |  |                                          |   |