



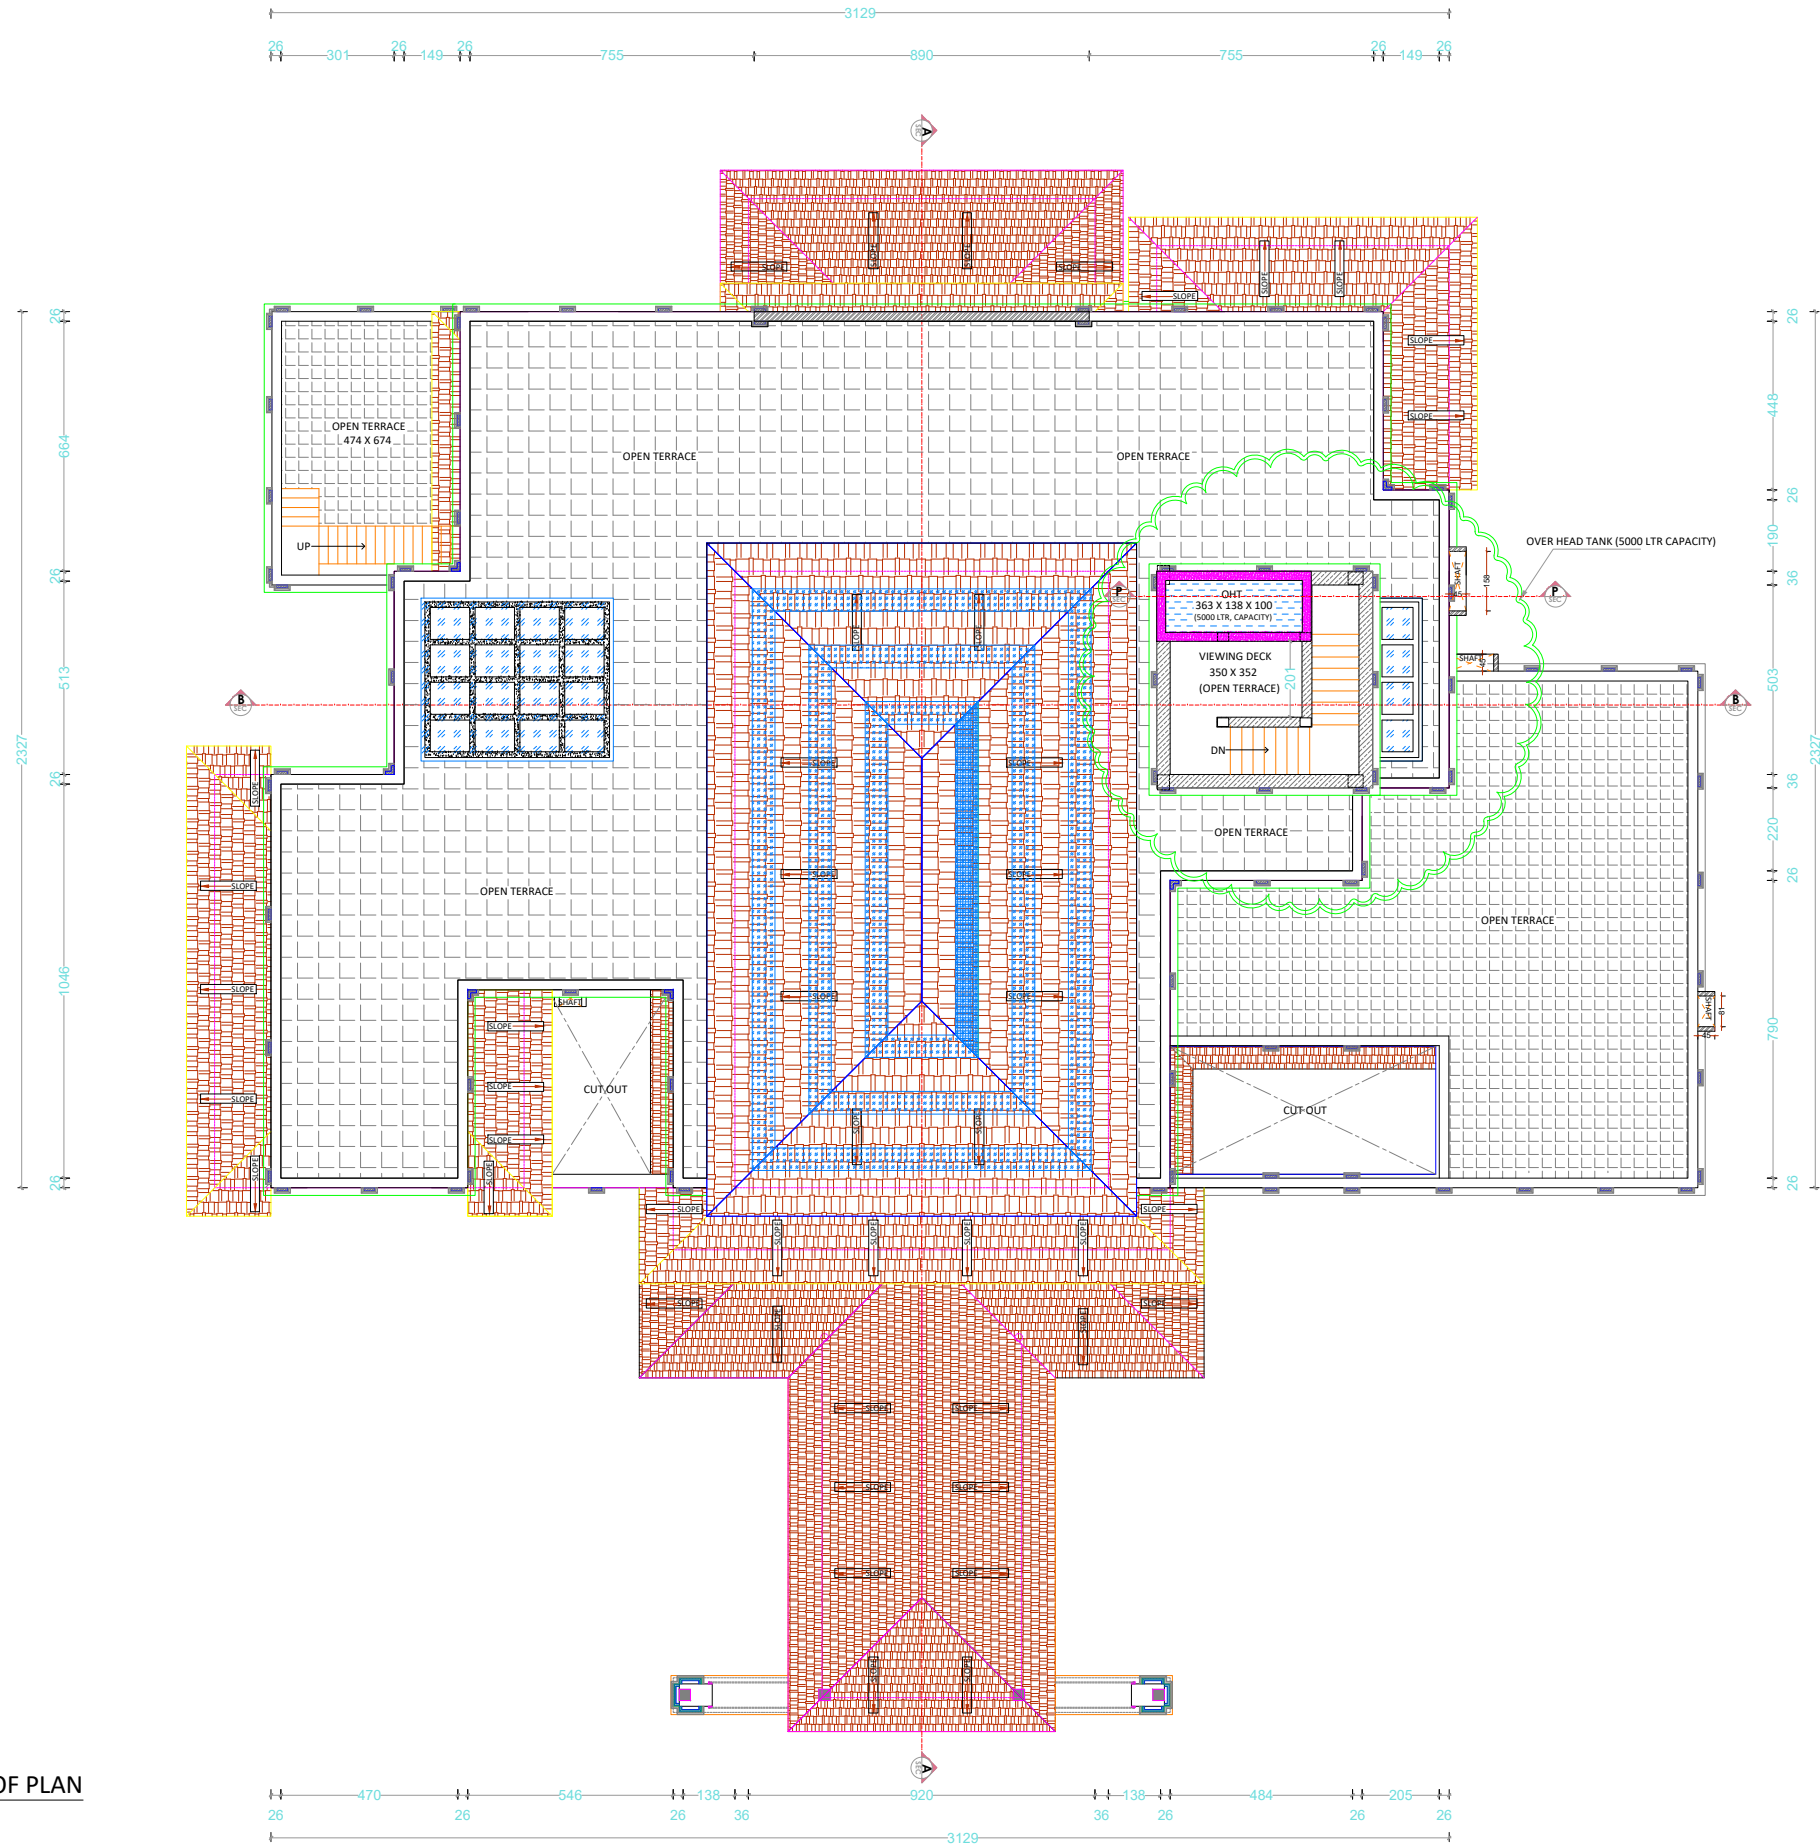

ROOF PLAN

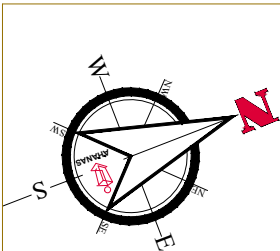

DATE: 16.03.2023

SCALE : NA

DRAWN: AP

CHECKED: ANEENA

PROJECT NO:563

DRAWING NO:
ADFS/AR/ 563/FH-06

PROJECT: RESIDENTIAL PROJECT AT
TIRUNELVELI

CLIENT: SHABREESH

DRAWING TITLE:

ROOF PLAN

REVISION:

1

13-05-24- WALL EXTENSION OF TOILET FOR PROVIDING TV
CHANGES IN SHAFT LOCATION/ SIZE AS PER HVAC
CONSULTANT REQUIREMENT



NOTES:

- ALL DIMENSIONS ARE IN CMS, UNLESS OTHERWISE SPECIFIED
- DIMENSIONS SHALL NOT BE MEASURED DIRECTLY FROM THIS DRAWINGS.
FOLLOW ONLY WRITTEN DIMENSIONS
- IN THE EVENT OF ANY DISCREPANCY OR DIFFERENCE BETWEEN ANY
DRAWINGS OR SITE CONDITIONS OR OTHERWISE IMMEDIATE REFERENCE
IS TO BE MADE TO THE DESIGNER FOR CLARIFICATION PRIOR TO EXECUTION
OF WORK AT SITE
- ALL THE CIVIL WORKS SHOULD BE IN LINE LEVEL AND PLUMB.
- PLASTERING TO BE CUT AT SKIRTING LEVEL.