
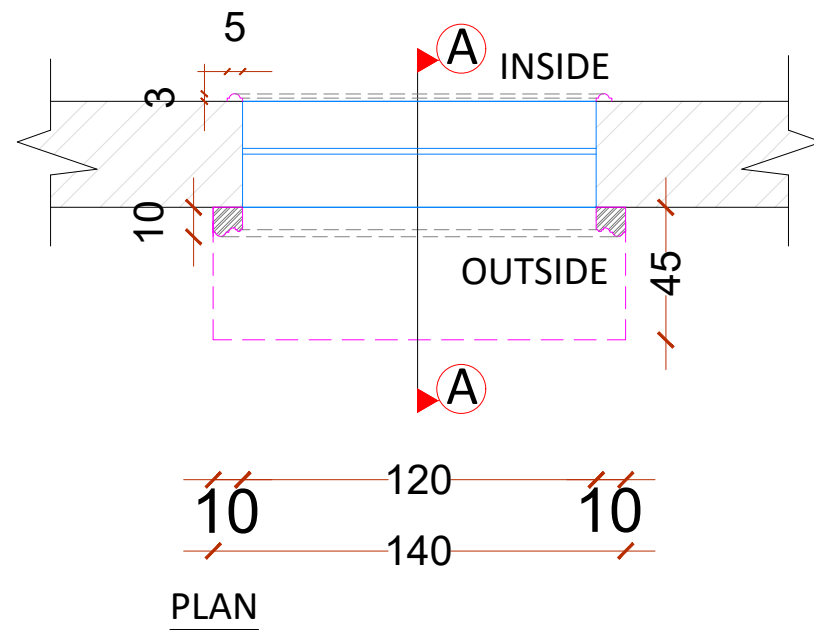


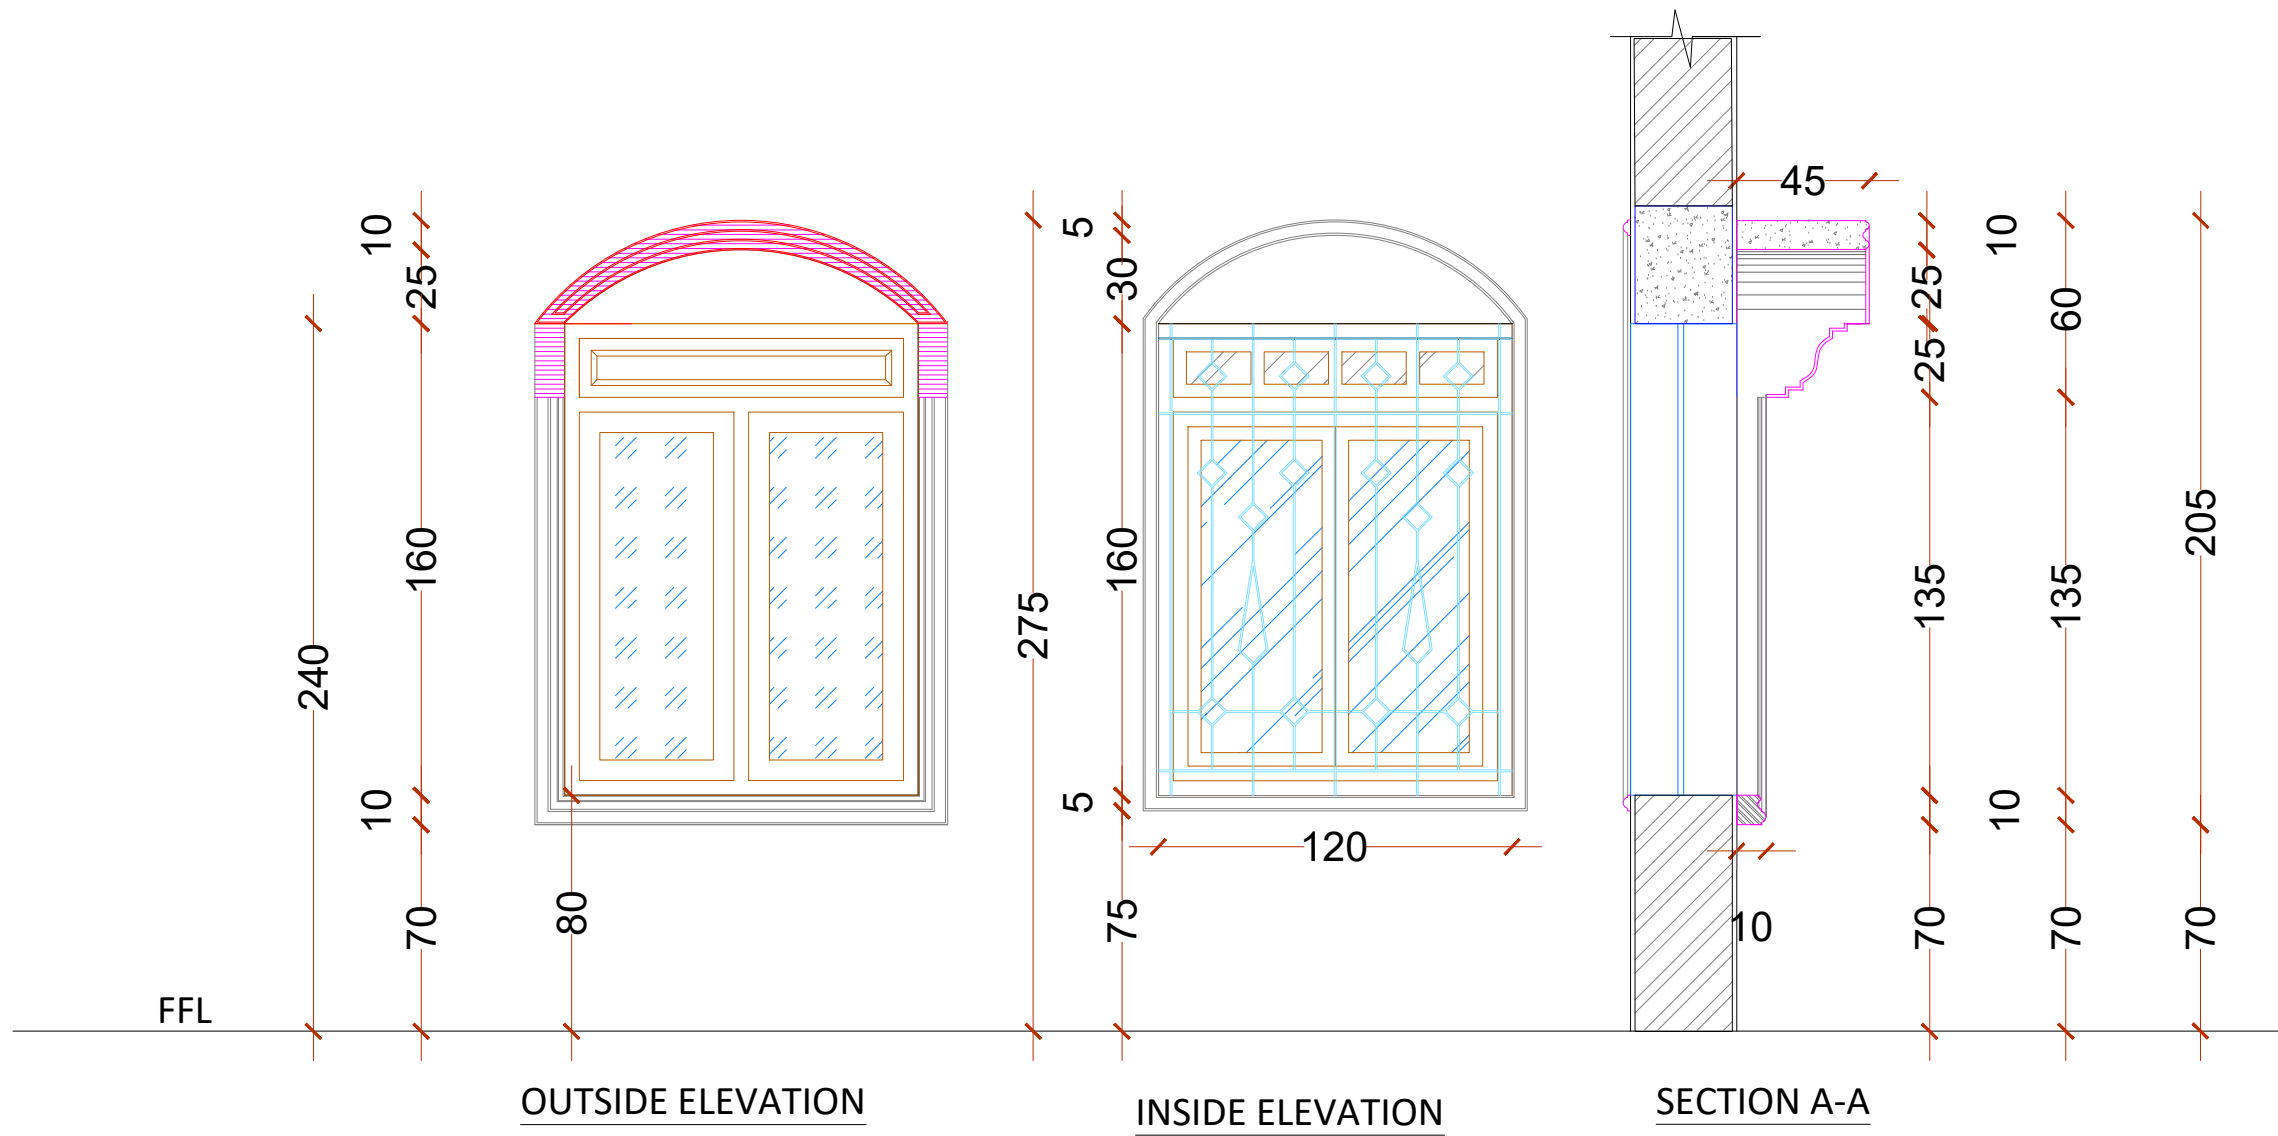

	DATE: 24.06.2023		PROJECT: RESIDENTIAL PROJECT AT TIRUNELVELI		REVISION:			NOTES:	
	SCALE : NA							o ALL DIMENSIONS ARE IN CMS, UNLESS OTHERWISE SPECIFIED	
	DRAWN: PJ		CLIENT: SHABREESH					o DIMENSIONS SHALL NOT BE MEASURED DIRECTLY FROM THIS DRAWINGS. FOLLOW ONLY WRITTEN DIMENSIONS	
	CHECKED: JAMESLEE		DRAWING TITLE: WINDOW SHADE AND MOLDING DETAILING					o IN THE EVENT OF ANY DISCREPANCY OR DIFFERENCE BETWEEN ANY DRAWINGS OR SITE CONDITIONS OR OTHERWISE IMMEDIATE REFERENCE IS TO BE MADE TO THE DESIGNER FOR CLARIFICATION PRIOR TO EXECUTION OF WORK AT SITE	
	PROJECT NO:563	DRAWING NO: ADFS/AR/ 563/FH-12a						o ALL THE CIVIL WORKS SHOULD BE IN LINE LEVEL AND PLUMB.	
	o PLASTERING TO BE CUT AT SKIRTING LEVEL.								