


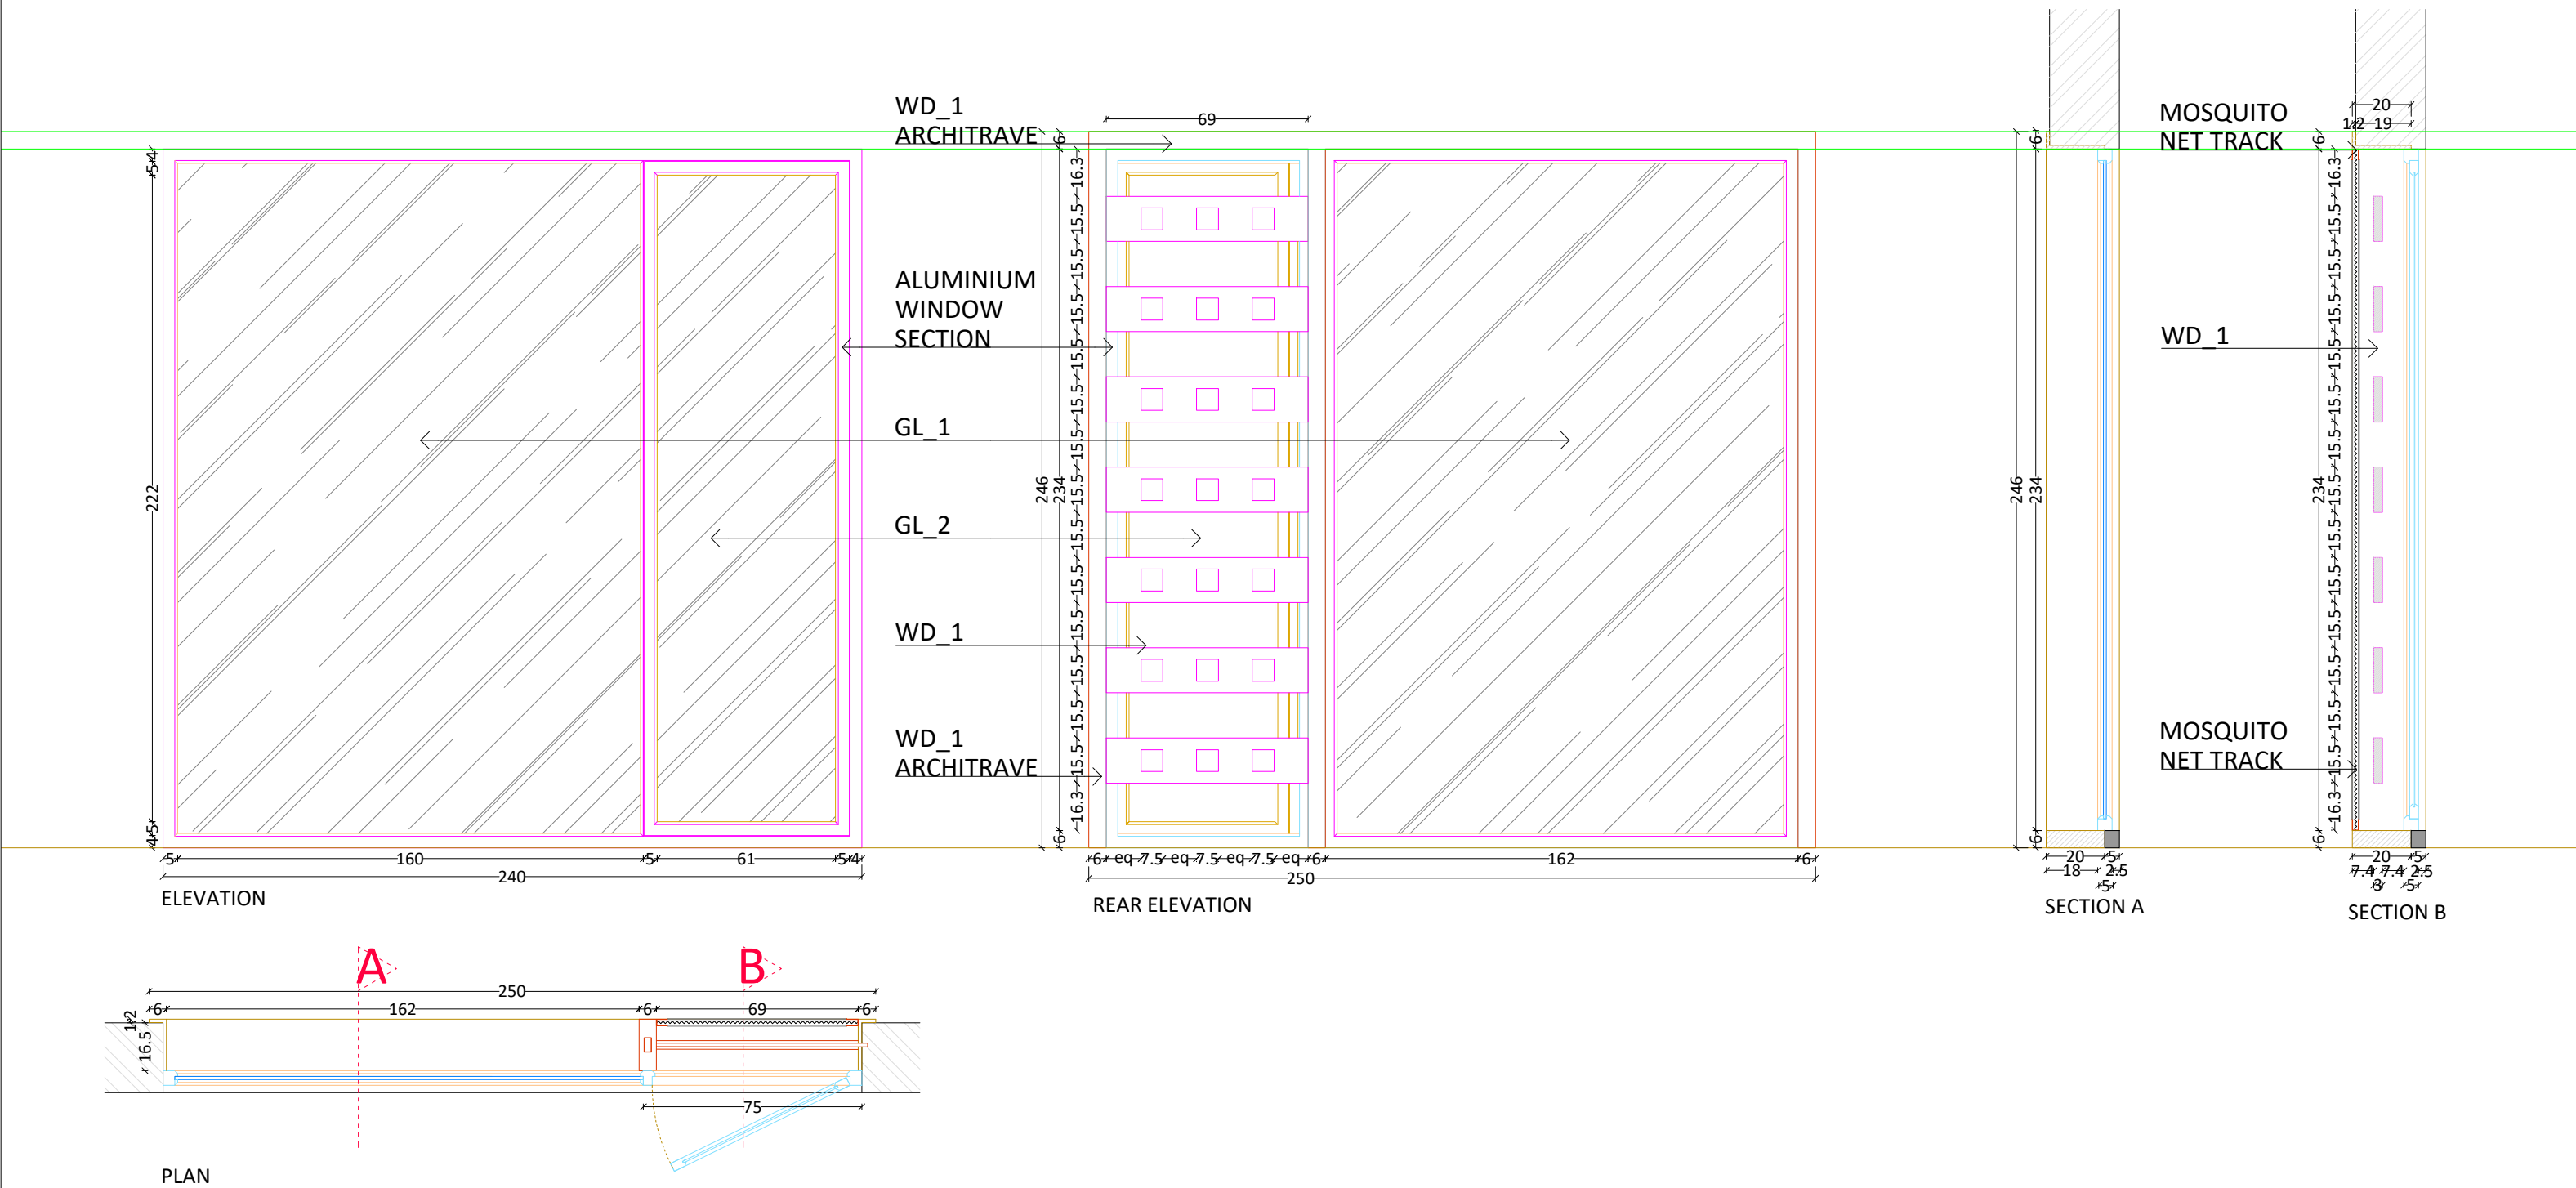

NO. OF QUANTITY REQUIRED : 1

NOTE

GL_1 - LAMINATED GLASS - ALL FIXED WINDOWS
GL_2 - TOUGHENED GLASS - ALL SHUTTER OPENINGS

PROJECT: RESI @ MIJULAL AND RADHIKA	DWG TITLE: FW4b WINDOW & DOOR DETAILS	DRAWN: NA	REVISED DATE: 15-03-2024	ALL DIMENSIONS ARE IN CMS No dimensions to be scaled off from the drawings only written dimensions to be. In the event of any discrepancy or difference between any interior drawings or site conditions or other wise immediate reference is to be made to the designer for clarification prior to execution of work at site
DWG NO:	DATE: 17-08-2022	CHECKED:	REVISION NO: R03	
REVISION:			SCALE: 1:25	

